

ΥΠΗΡΕΣΙΑ: ΕΓΝΑΤΙΑ ΟΔΟΣ
ΕΡΓΟ: ΕΓΚ. ΕΠΕΞΕΡΓΑΣΙΑ & ΕΡΓΑ ΔΙΑΘΕΣΗΣ ΛΥΜΑΤΩΝ ΔΟΜΟΥΣΑΣ (N2200)

ΜΕΛΕΤΗ: ΜΕΛΕΤΗ ΕΦΑΡΜΟΓΗΣ

ΑΝΑΔΟΧΟΣ:

Κωδικός Έργου: ΤΥΠΙΚΑ ΣΧΕΔΙΑ ΑΥΤΟΜΑΤΙΣΜΟΥ V01
Είδος Έργου: ΗΛΕΚΤΡΙΚΟΙ ΠΙΝΑΚΕΣ

Θέση εγκατάστασης: Ν. ΔΟΝΟΥΣΑ

Υπεύθυνος Έργου:

Αποθήκευση: Χ:\Data\404 Μ.ΕΦ.ΔΟΝΟΥΣΑ\ΠΡΟΧ\ΗΛΕΚ\EPLAN

Δημιουργία MAP 2014

Αναθεώρηση MAP 2014

Από (αρχ.) ΜΓΣ

Σύνολο σελ. 55

ΠΙΝΑΚΑΣ

ΒΑΣΙΚΑ ΣΤΟΙΧΕΙΑ

TNS, 3ph, N, PE, 400V, 50Hz
ΣΥΝΟΛΙΚΗ ΙΣΧΥΣ ΠΙΝΑΚΑ 191KW
IP 54 ΚΑΤΑΣΚΕΥΗ: IEC 144
ΤΥΠΟΥ ΠΕΔΙΟΥ - ??? X ??? X ??? mm

ΚΩΔΙΚΟΠΟΙΗΣΗ ΚΛΕΜΜΟΣΕΙΡΩΝ

-X0	ΙΣΧΥΟΣ-ΔΙΑΝΟΜΗ	400V AC
-X10	ΙΣΧΥΟΣ-ΑΠΟ UPS	230V AC
-X20	ΕΞΩΤΕΡΙΚΟΣ ΦΩΤΙΣΜΟΣ	230V AC
-X30	ΑΥΤΟΜΑΤΙΣΜΟΣ Η/Ζ	230V AC
-X1	ΨΗΦΙΑΚΑ ΣΗΜΑΤΑ	24V DC
-X11	ΨΗΦΙΑΚΑ ΜΕΤΑ ΑΠΟ ΜΑΝΙΤΑΡΙ	230V AC
-X21	ΕΛΕΓΧΟΣ ΥΠΟΒΡΥΧ. ΑΝΤΛΙΩΝ	24V DC
-X31	LAMP TEST	24V DC
-X2	ΨΗΦΙΑΚΑ ΣΗΜΑΤΑ	230V AC
-X3	ΣΗΜΑΤΑ PLC	24V DC
-X4	ΑΝΑΛΟΓΙΚΑ ΣΗΜΑΤΑ	24V DC

ΚΩΔΙΚΟΠΟΙΗΣΗ ΚΑΛΩΔΙΩΝ

-WP...	ΙΣΧΥΟΣ	400V AC
-WS...	ΚΑΛΩΔΙΟ ΠΡΟΜΗΘΕΥΤΗ	400V AC
-WD...	ΨΗΦΙΑΚΑ ΣΗΜΑΤΑ	24V DC
-WL...	ΔΙΑΚΟΠΤΕΣ ΣΤΑΘΜΗΣ	24V DC
-WA...	ΑΝΑΛΟΓΙΚΑ ΣΗΜΑΤΑ	24V DC

ΔΥΝΑΜΙΚΑ-ΙΣΧΥΟΣ


L1	ΦΑΣΗ ΔΙΚΤΥΟΥ -1 [R]	400V AC
L2	ΦΑΣΗ ΔΙΚΤΥΟΥ -1 [S]	400V AC
L3	ΦΑΣΗ ΔΙΚΤΥΟΥ -1 [T]	400V DC
N	ΟΥΔΕΤΕΡΟΣ	
PE	ΣΥΣΤΗΜΑ ΓΕΙΩΣΗΣ	
DL1	ΦΑΣΗ ΔΙΚΤΥΟΥ -1 [R] ΜΕΤΑ ΤΟ ΡΕΛΛΕ	400V AC
DL2	ΦΑΣΗ ΔΙΚΤΥΟΥ -1 [S] ΜΕΤΑ ΤΟ ΡΕΛΛΕ	400V AC
DL3	ΦΑΣΗ ΔΙΚΤΥΟΥ -1 [T] ΜΕΤΑ ΤΟ ΡΕΛΛΕ	400V DC
DN	ΟΥΔΕΤΕΡΟΣ ΜΕΤΑ ΤΟ ΡΕΛΛΕ	
LY	ΦΑΣΗ ΤΡΟΦΟΔΟΣΙΑΣ ΑΝΙΧΝ. ΥΓΡΑΣΙΑΣ	230V AC
NY	ΟΥΔΕΤΕΡΟΣ ΤΡΟΦΟΔΟΣΙΑΣ ΑΝΙΧΝ. ΥΓΡΑΣΙΑΣ	
LHZ	ΦΑΣΗ ΑΠΟ ΗΖ	230V AC
NHZ	ΟΥΔΕΤΑΙΡΟΣ ΑΠΟ ΗΖ	


ΔΥΝΑΜΙΚΑ-ΑΥΤΟΜΑΤΙΣΜΟΥ


FL1	230V AC - ΠΡΙΝ ΤΟΝ ΚΕΝΤΡΙΚΟ ΔΙΑΚΟΠΤΗ ΑΝΑΓΚΗΣ
FL2	230V ΜΕΤΑ ΤΟΝ ΚΕΝΤΡΙΚΟ ΔΙΑΚΟΠΤΗ ΑΝΑΓΚΗΣ
FN	ΟΥΔΕΤΕΡΟΣ
L+	24V DC ΜΕΤΑ ΤΟ ΤΡΟΦΟΔΟΤΙΚΟ
L-	+/- 0V DC
LP+	24V DC ΜΕΤΑ ΤΟ ΤΡΟΦΟΔΟΤΙΚΟ PLC
LP-	+/- 0V DC PLC
LT	24V DC ΓΙΑ ΕΛΕΓΧΟ ΛΥΧΝΙΩΝ


+GENERAL/1


V1.0	MAP 2014	Version 1.0	ΜΓΣ	ΜΖΣ	ΜΖΣ	ΜΕΛΕΤΗ ΕΦΑΡΜΟΓΗΣ	ΑΡΧΙΚΗ ΣΕΛΙΔΑ ΠΙΝΑΚΑ ΧΑΜΗΛΗΣ ΤΑΣΗΣ	ΕΓΚΑΤΑΣΤΑΣΗ ΕΠΕΞΕΡΓΑΣΙΑΣ ΛΥΜΑΤΩΝ ΔΟΝΟΥΣΑΣ		= EEL
						ΠΟΛΥΓΡΑΜΜΙΚΑ ΔΙΑΓΡΑΜΜΑΤΑ ΤΩΝ ΗΛΕΚΤΡΙΚΩΝ ΠΙΝΑΚΩΝ		+ POWER		
ΑΝΑΘΕΩΡΗΣΗ	ΗΜΕΡΟΜΗΝΙΑ	ΟΝΟΜΑΣΙΑ	ΣΧΕΔ.	ΕΛΕΓΧ.	ΘΕΩΡ.			ΣΥΝ. ΣΕΛ. ΕΡΓΟΥ	ΤΜΗΜΑ ΔΙΑΝΟΜΗΣ ΙΣΧΥΟΣ	ΣΕΛ. από
								55		2 από 15

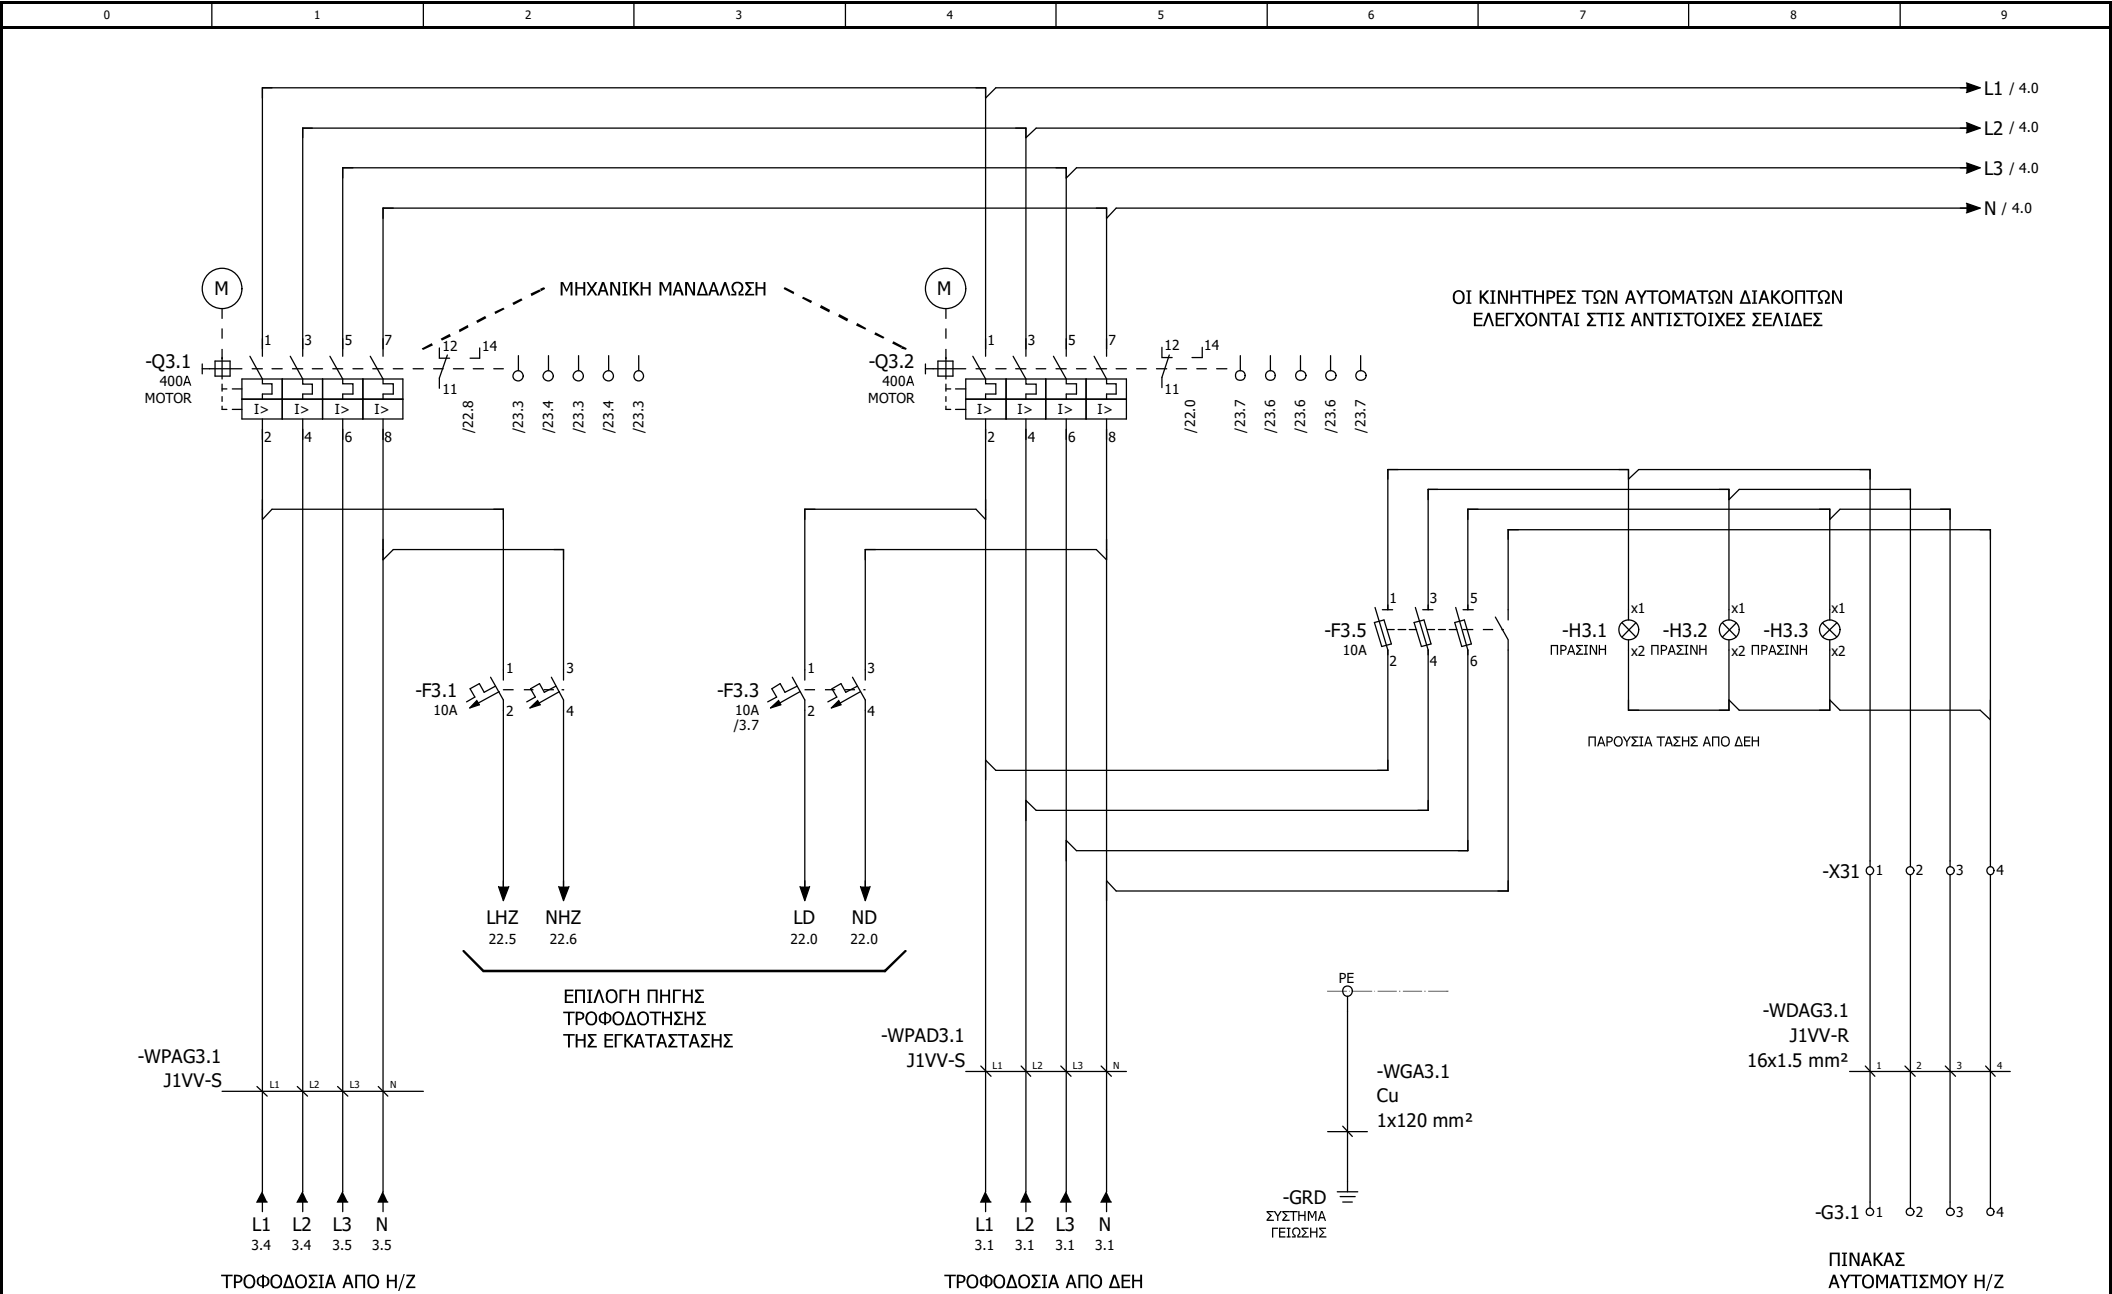


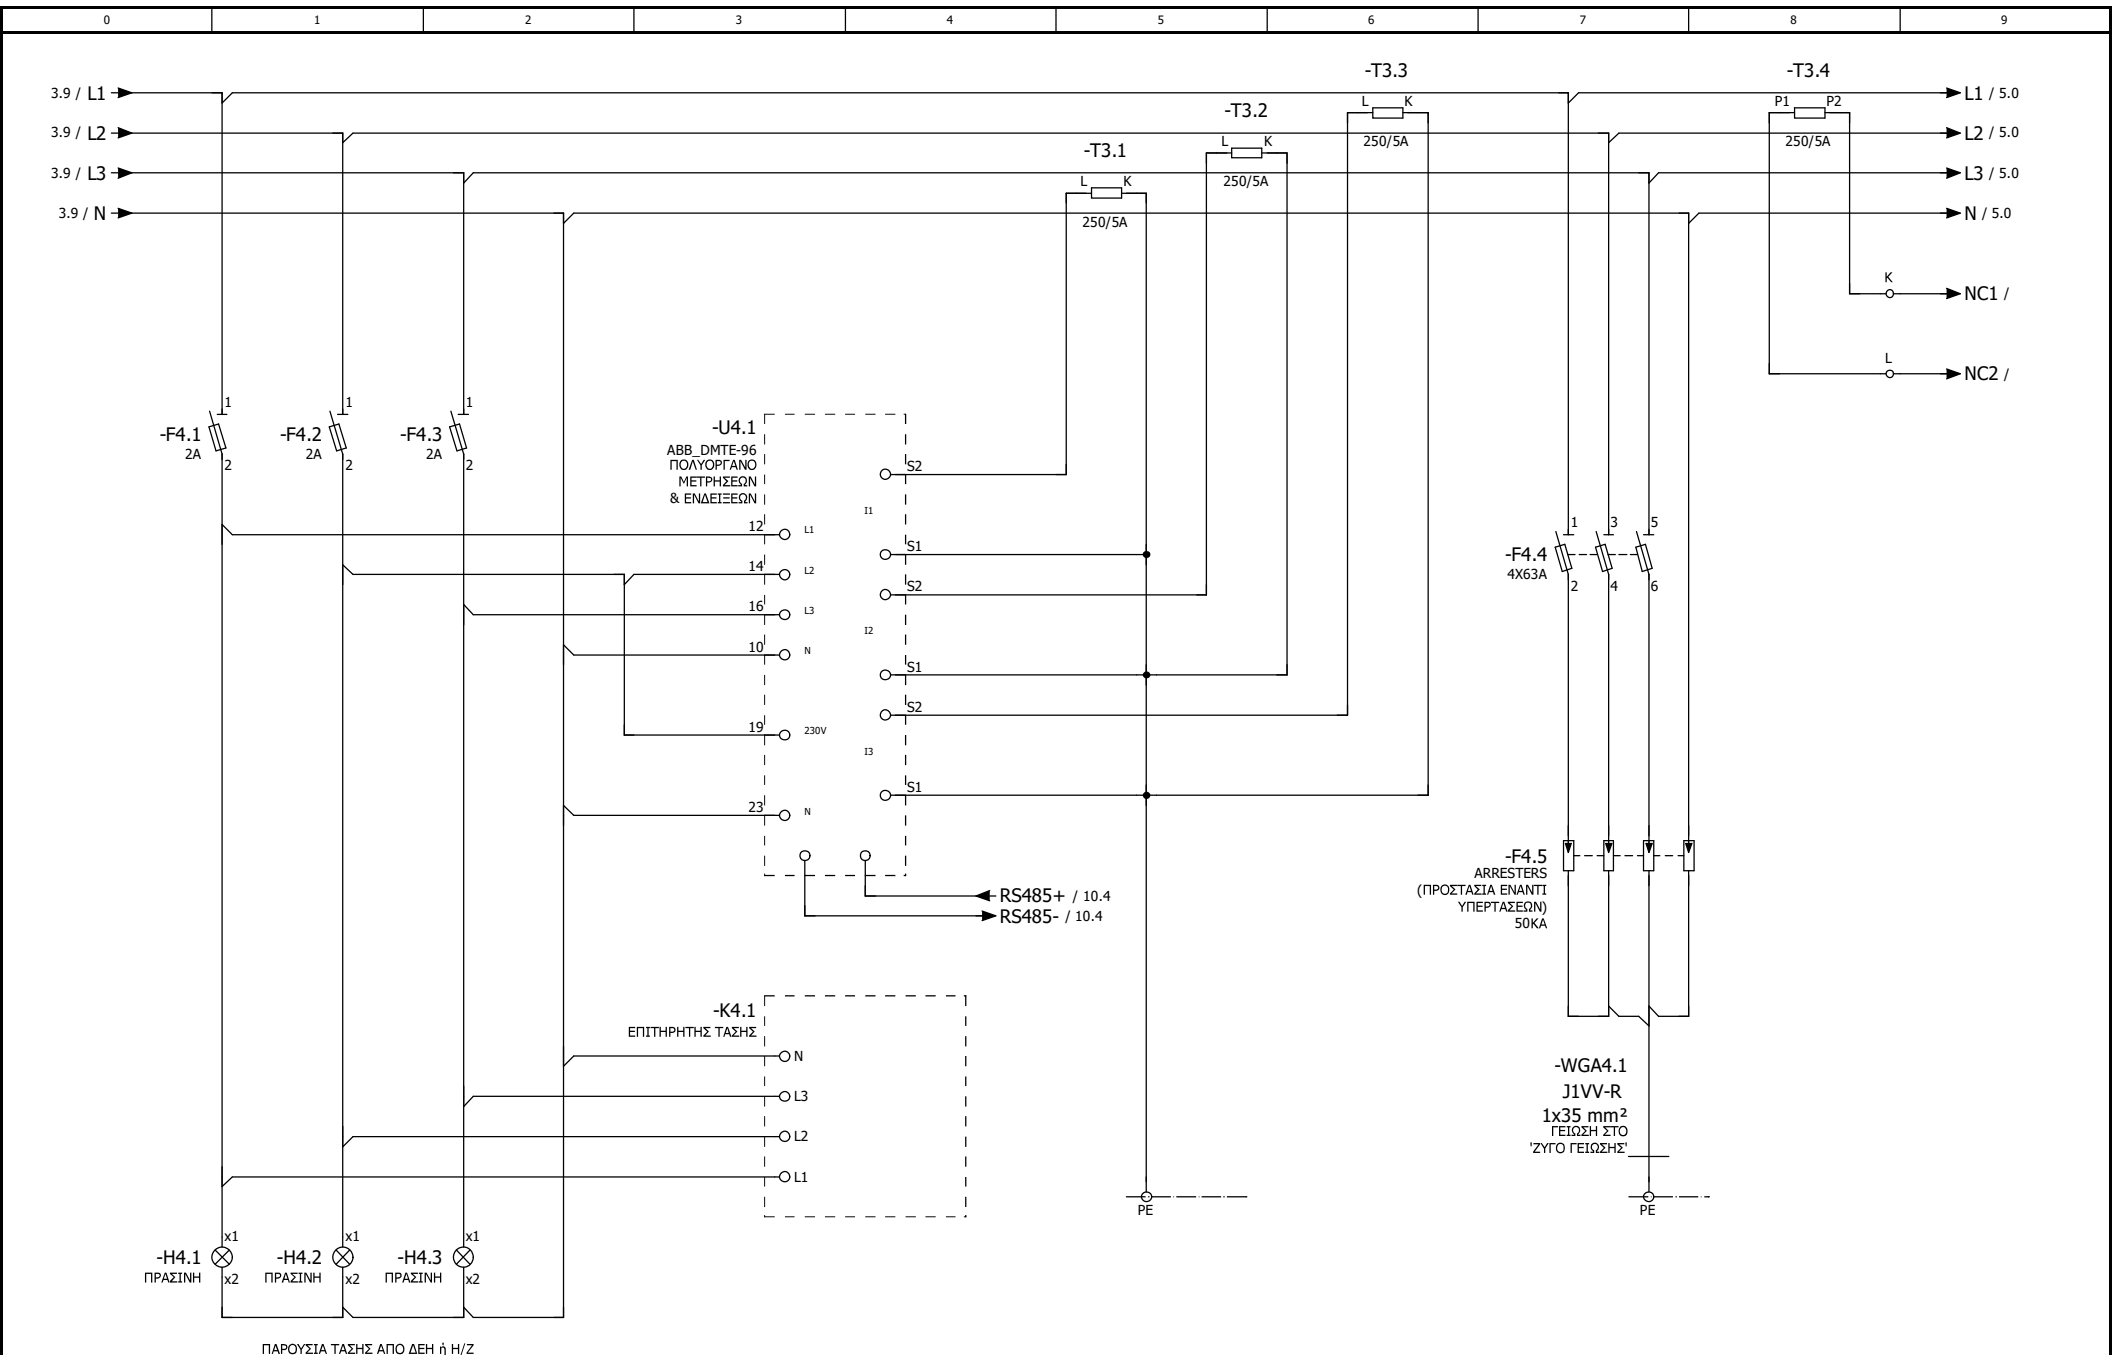

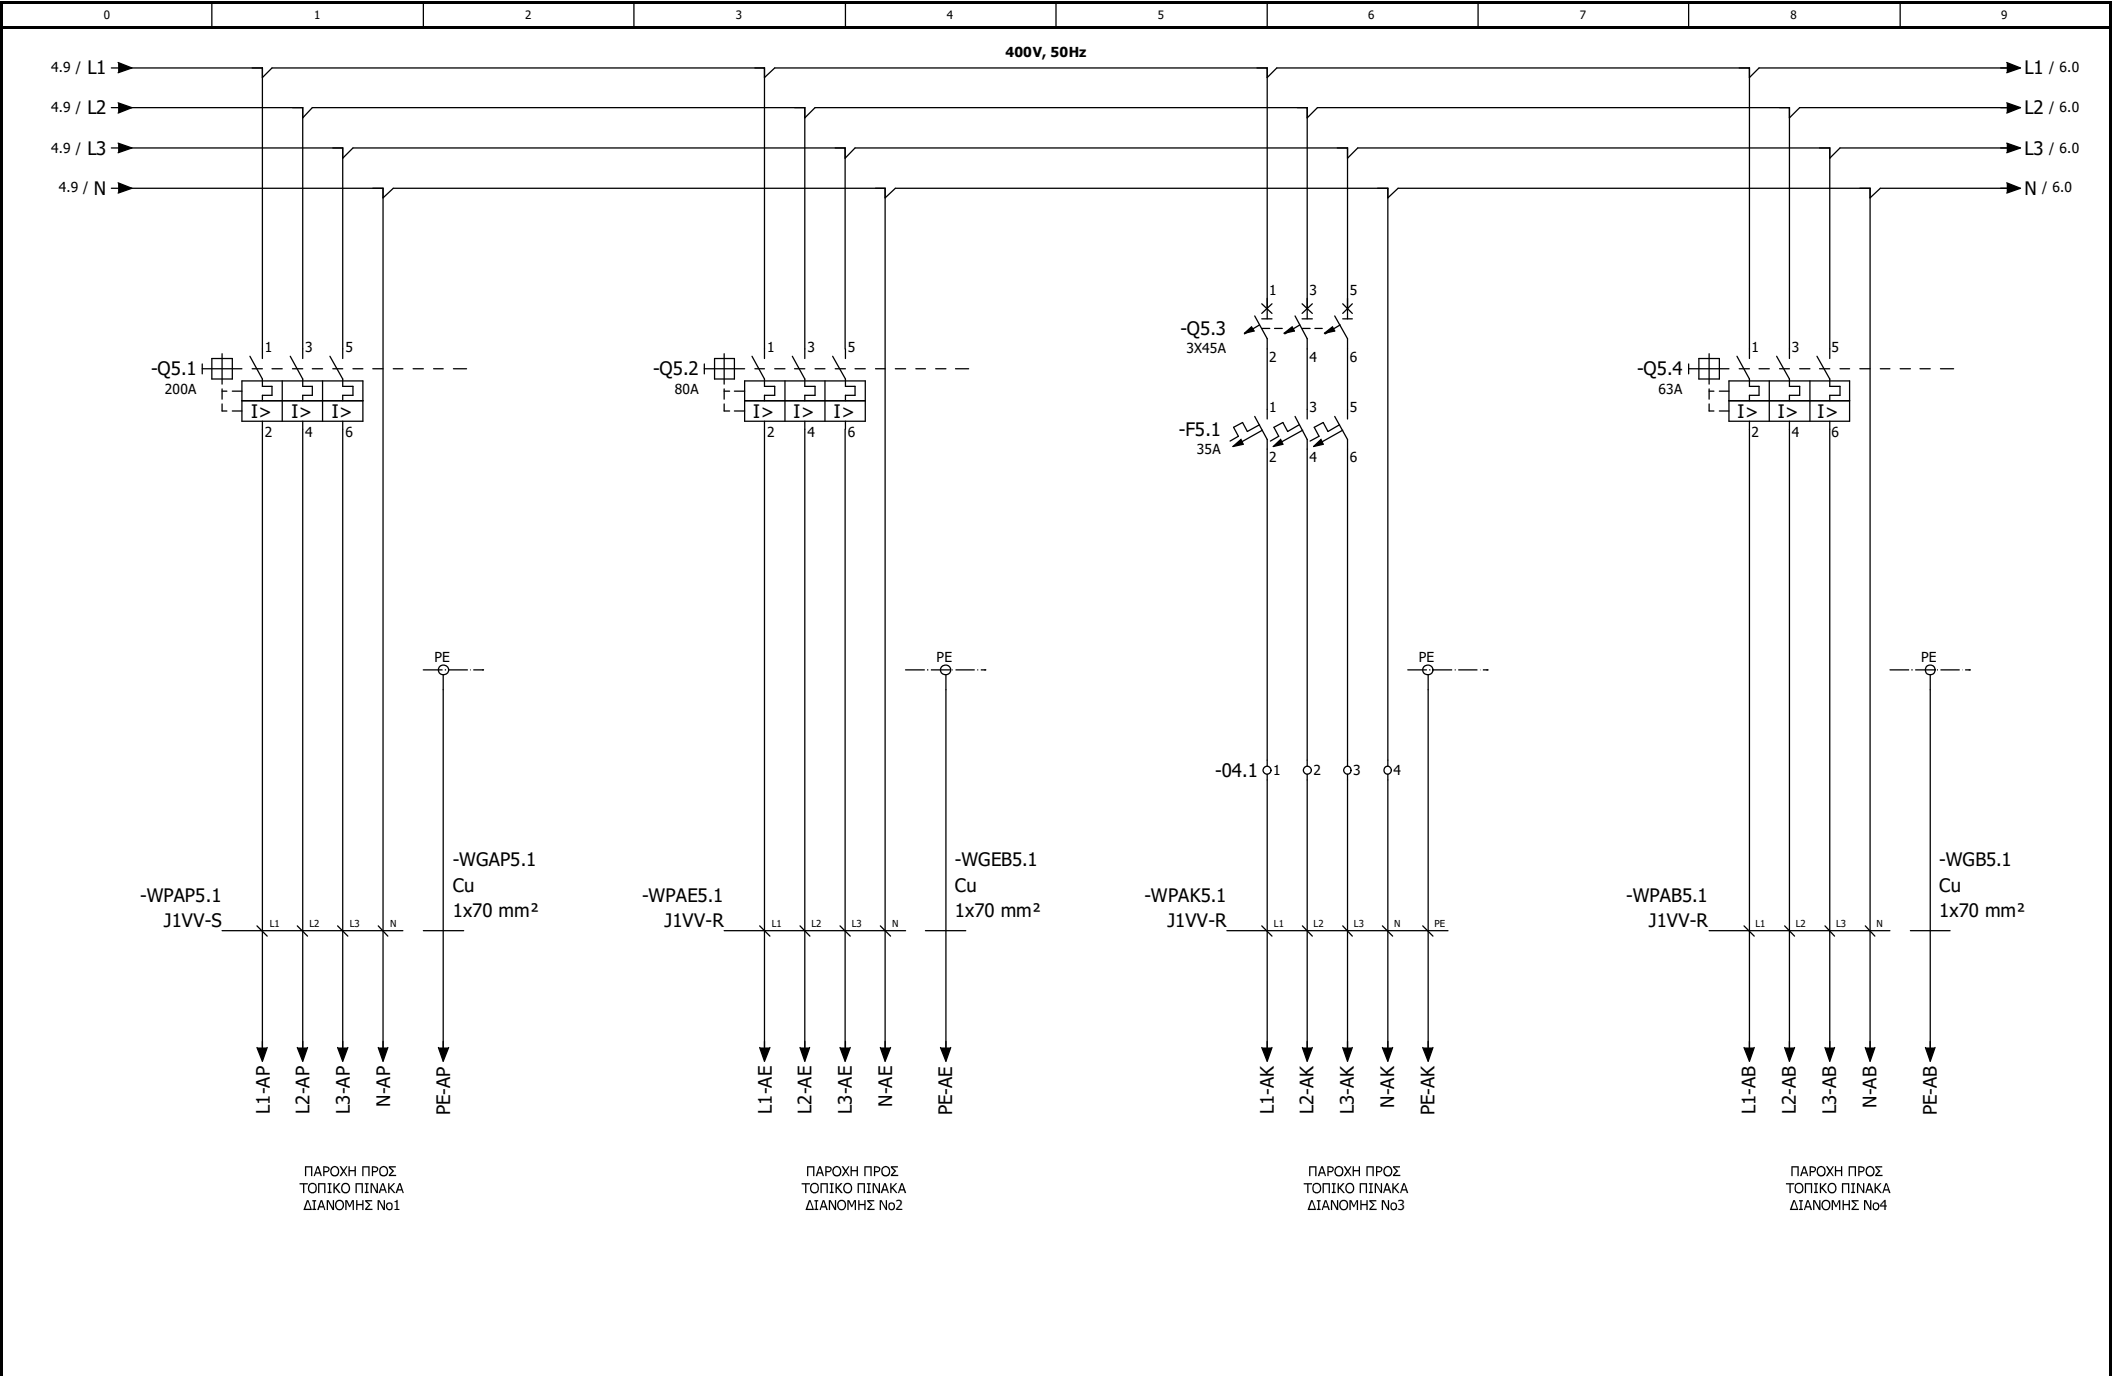


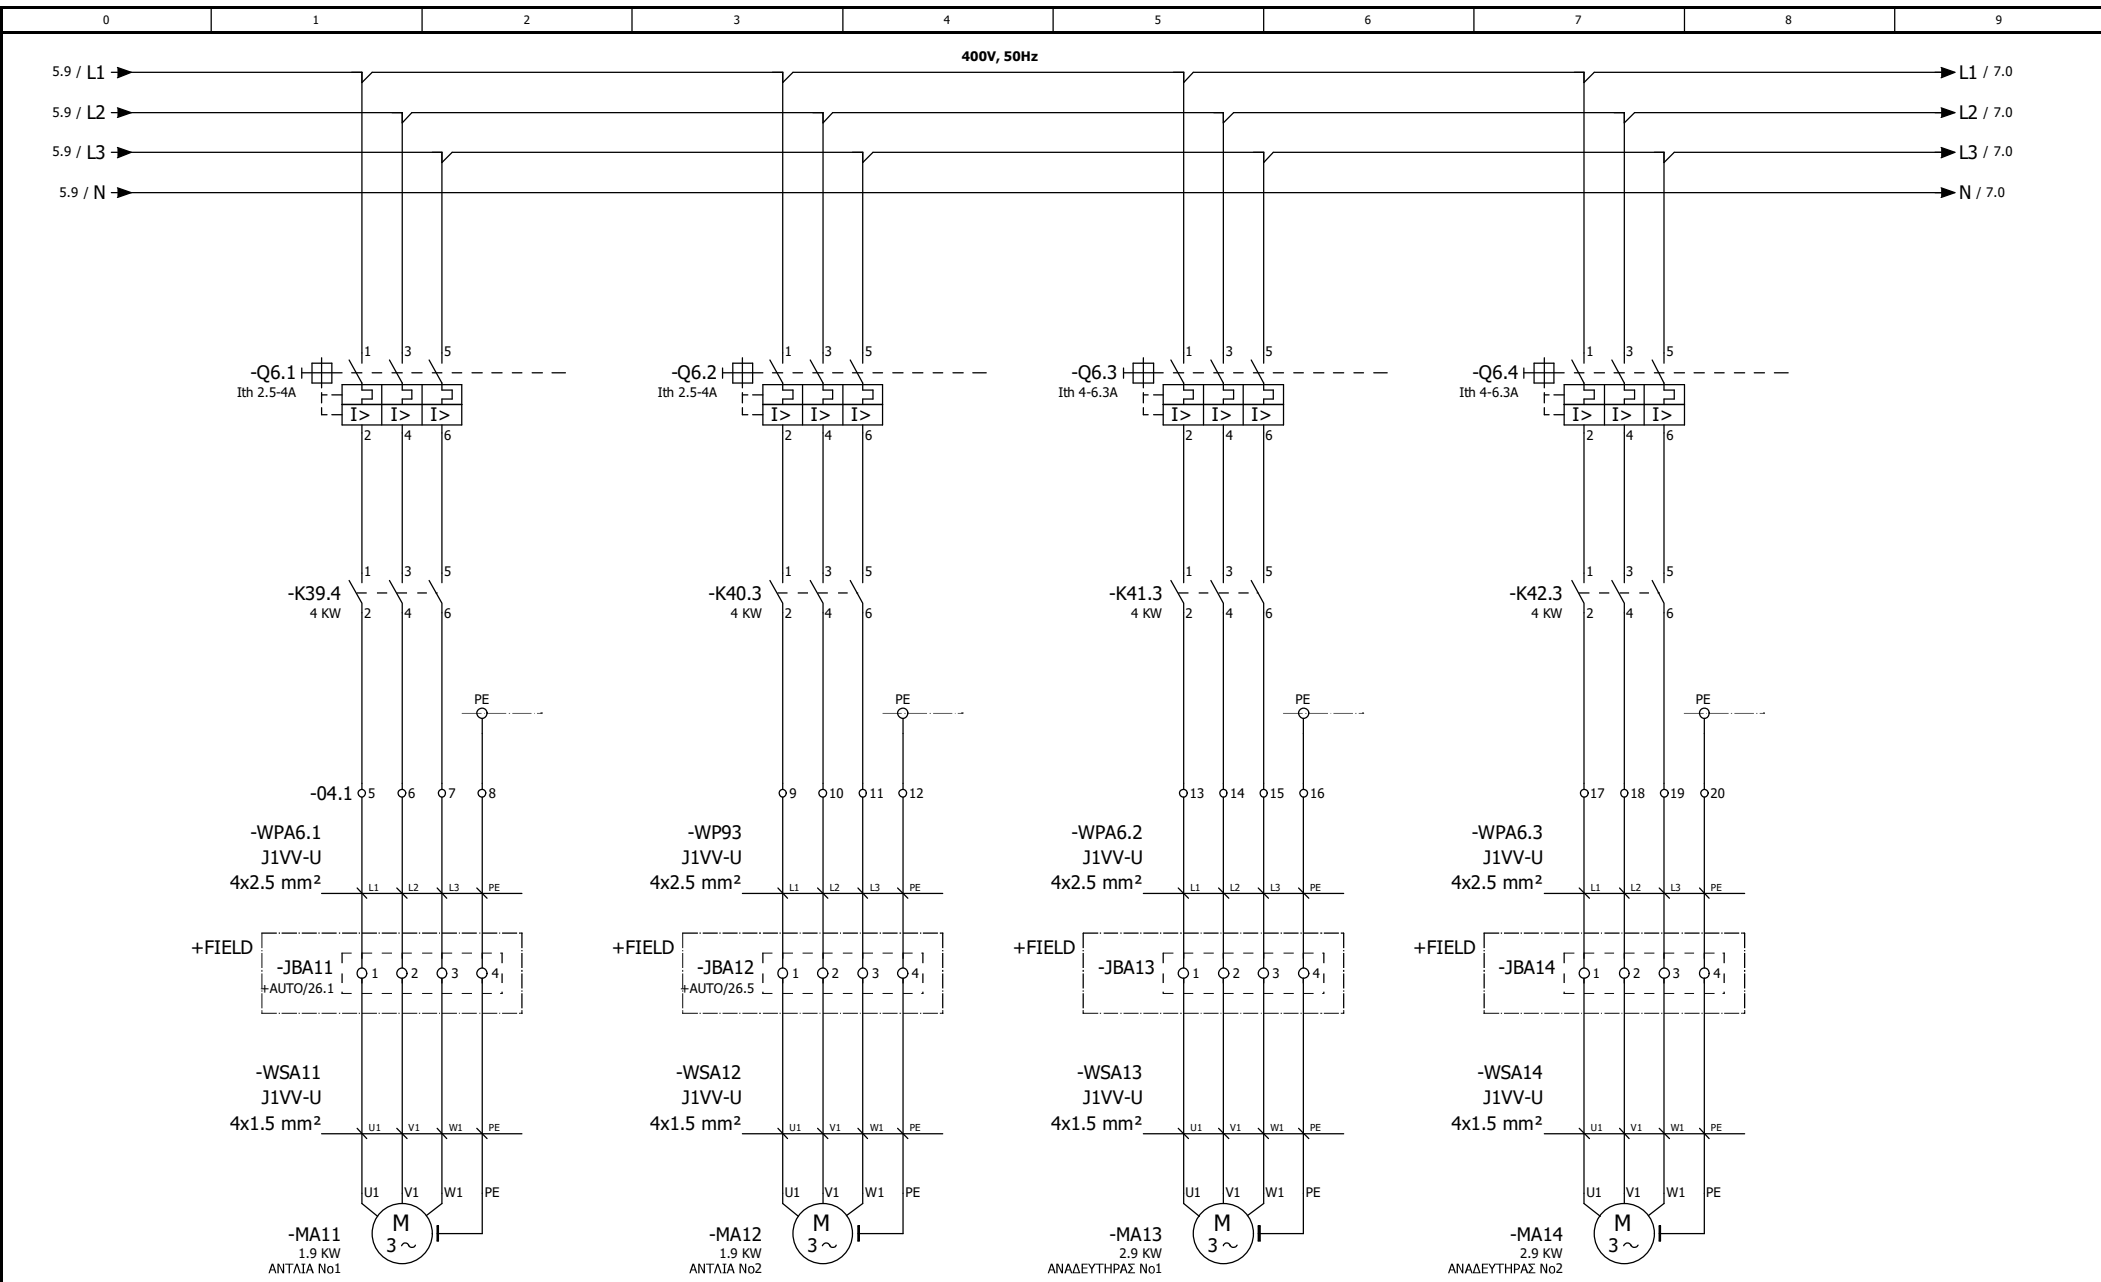


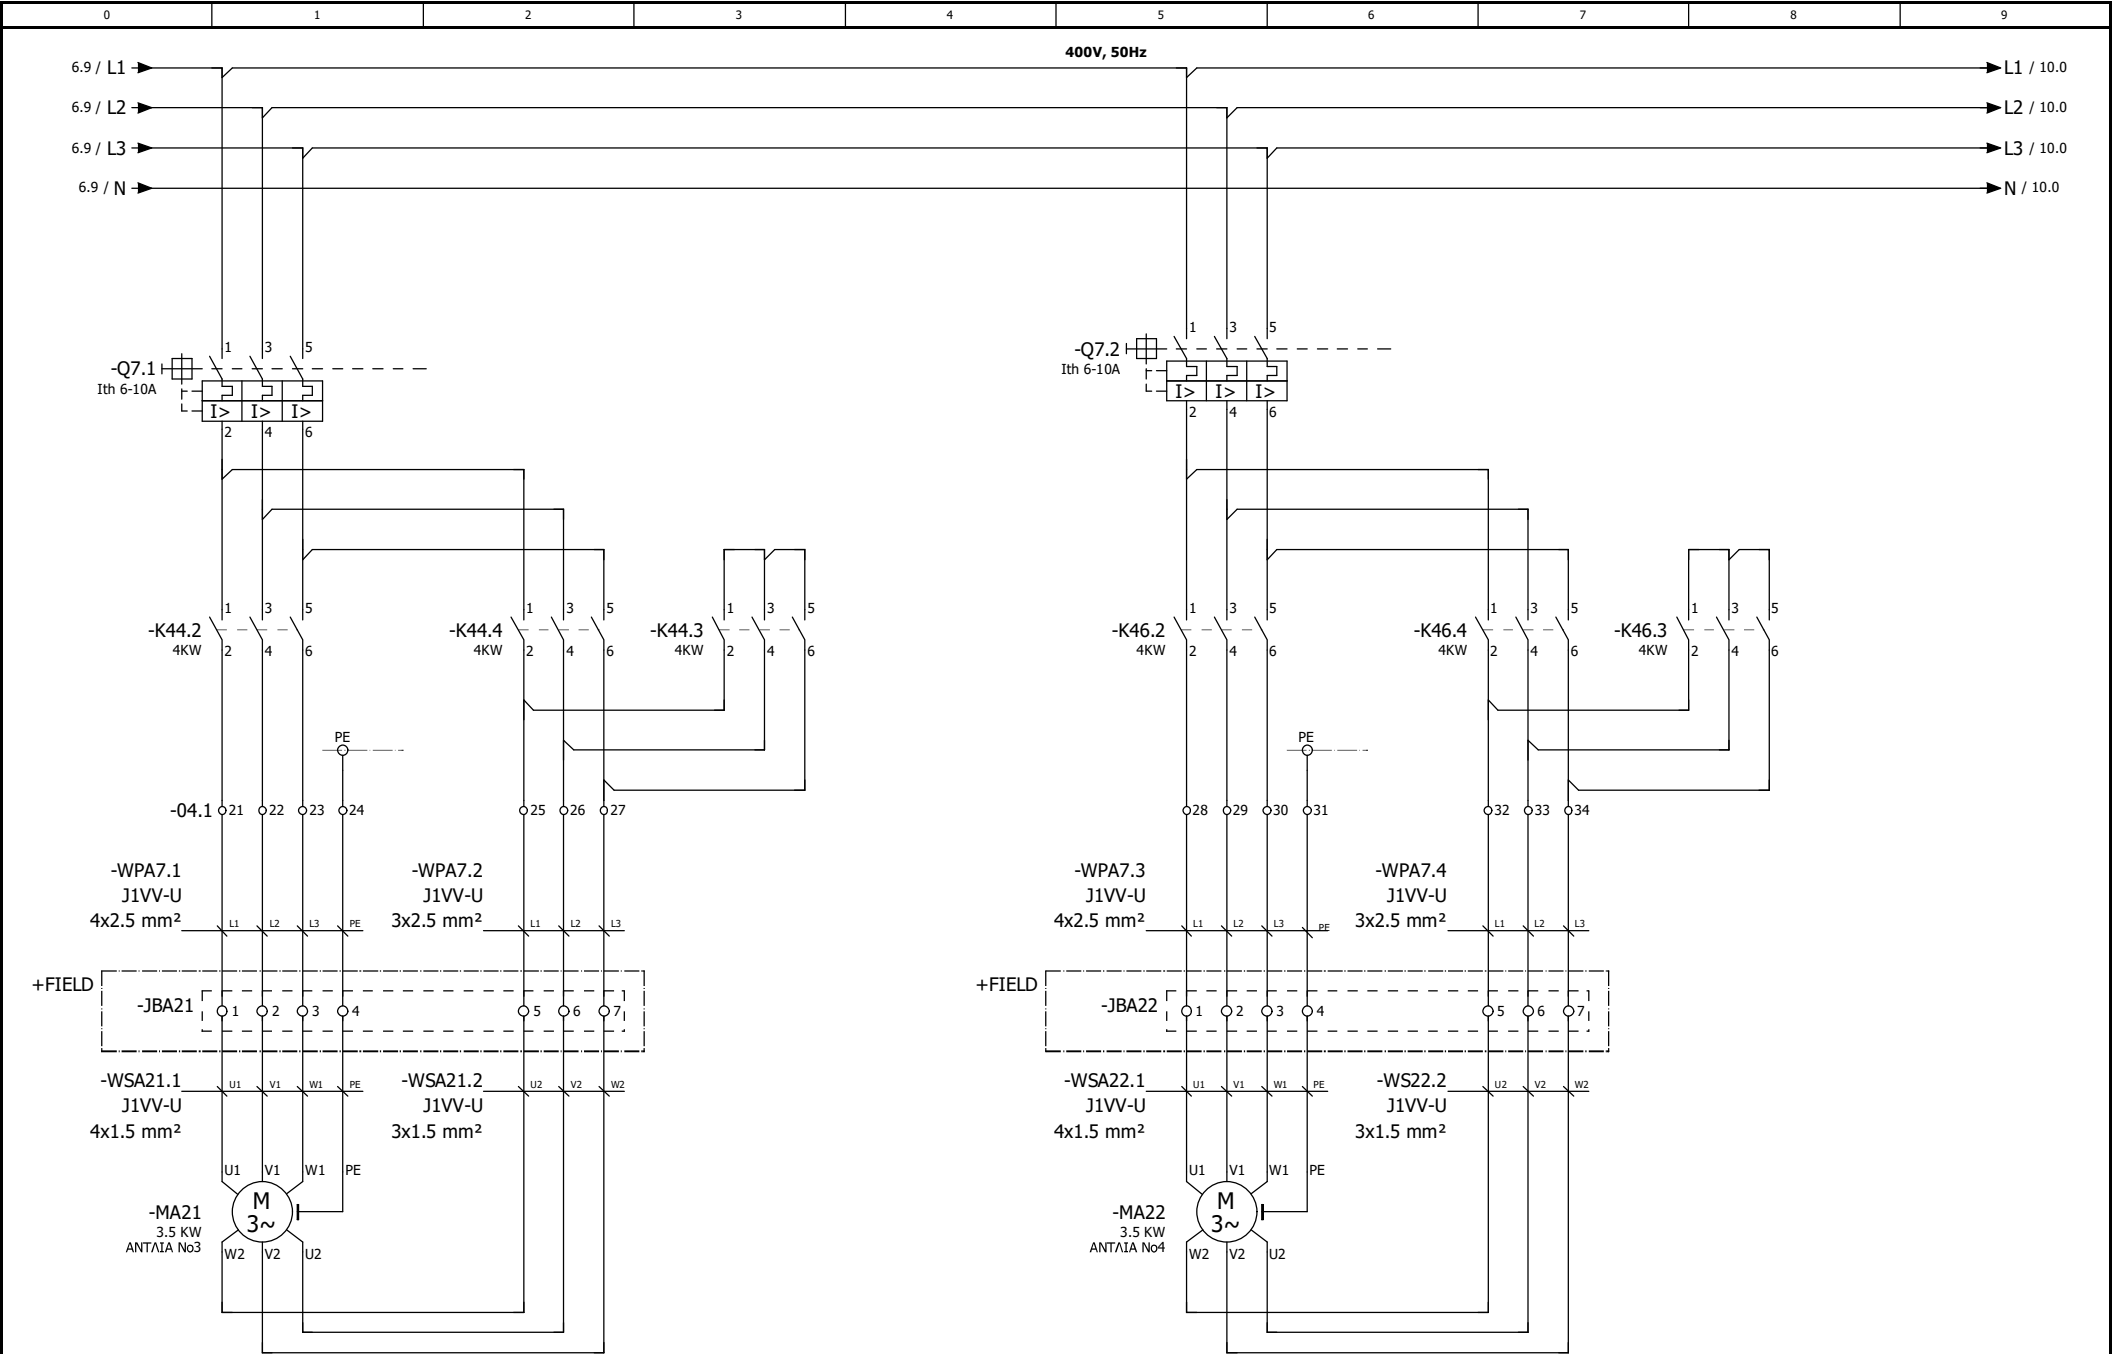


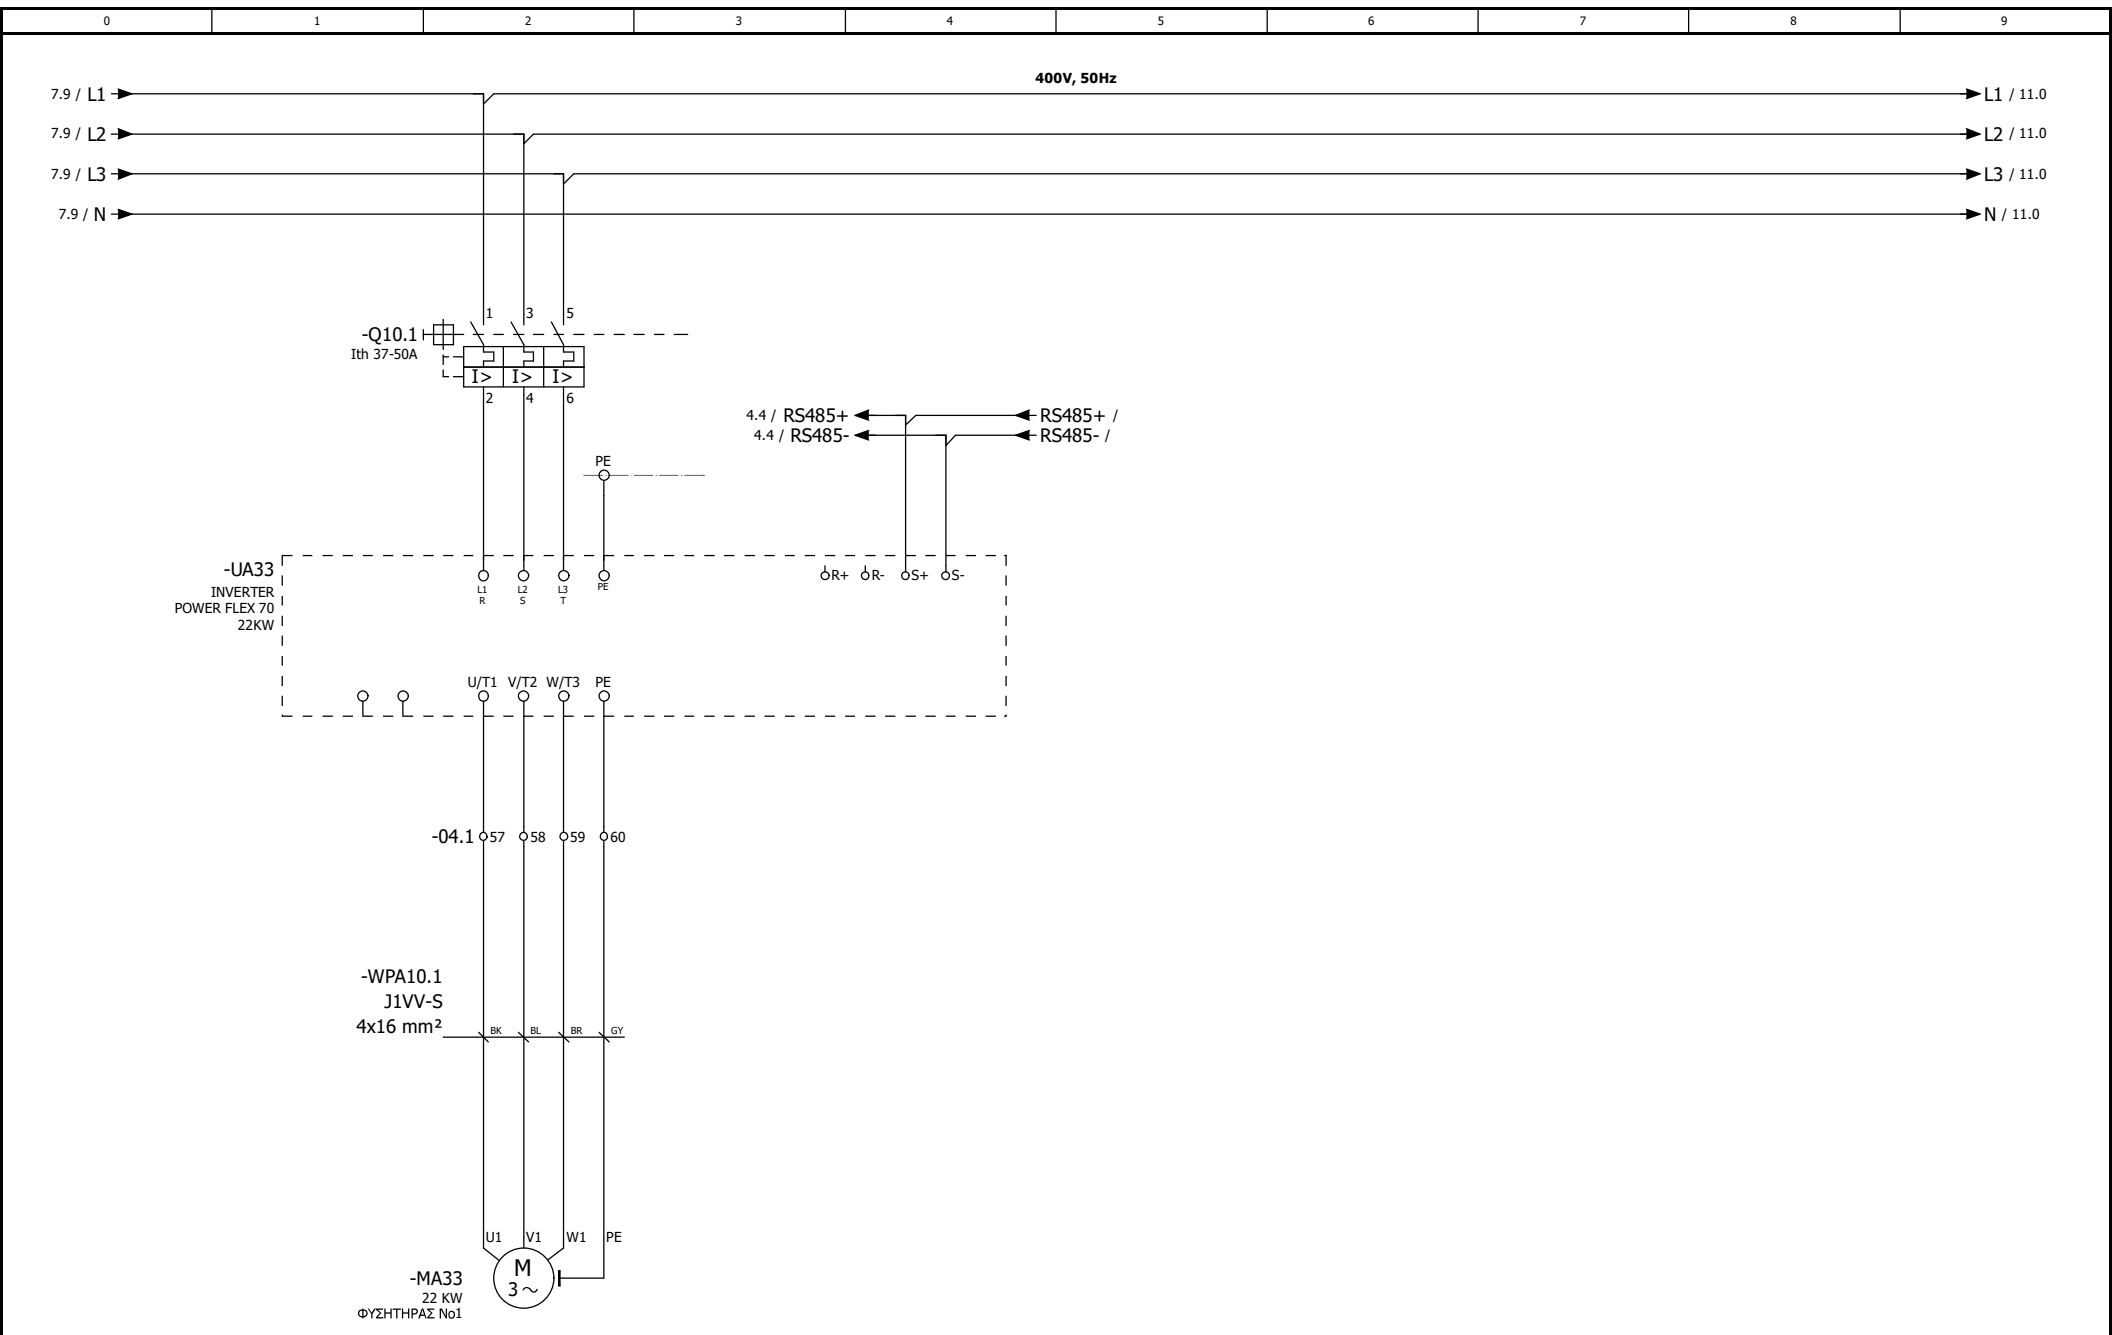


7											11		
V1.0	MAP 2014	Version 1.0	ΜΓΣ	ΜΖΣ	ΜΖΣ	ΜΕΛΕΤΗ ΕΦΑΡΜΟΓΗΣ ΠΟΛΥΓΡΑΜΜΙΚΑ ΔΙΑΓΡΑΜΜΑΤΑ ΤΩΝ ΗΛΕΚΤΡΙΚΩΝ ΠΙΝΑΚΩΝ	ΤΡΟΦΟΔΟΣΙΑ ΚΙΝΗΤΗΡΩΝ ΜΕ INVERTER	ΕΓΚΑΤΑΣΤΑΣΗ ΕΠΕΞΕΡΓΑΣΙΑΣ ΛΥΜΑΤΩΝ ΔΟΝΟΥΣΑΣ		= EEL			
									+ POWER				
ΑΝΑΘΕΩΡΗΣΗ	ΗΜΕΡΟΜΗΝΙΑ	ΟΝΟΜΑΣΙΑ	ΣΧΕΔ.	ΕΛΕΓΧ.	ΘΕΩΡ.			ΣΥΝ. ΣΕΛ. ΕΡΓΟΥ 55	ΤΜΗΜΑ ΔΙΑΝΟΜΗΣ ΙΣΧΥΟΣ	σελ. από	10 15		

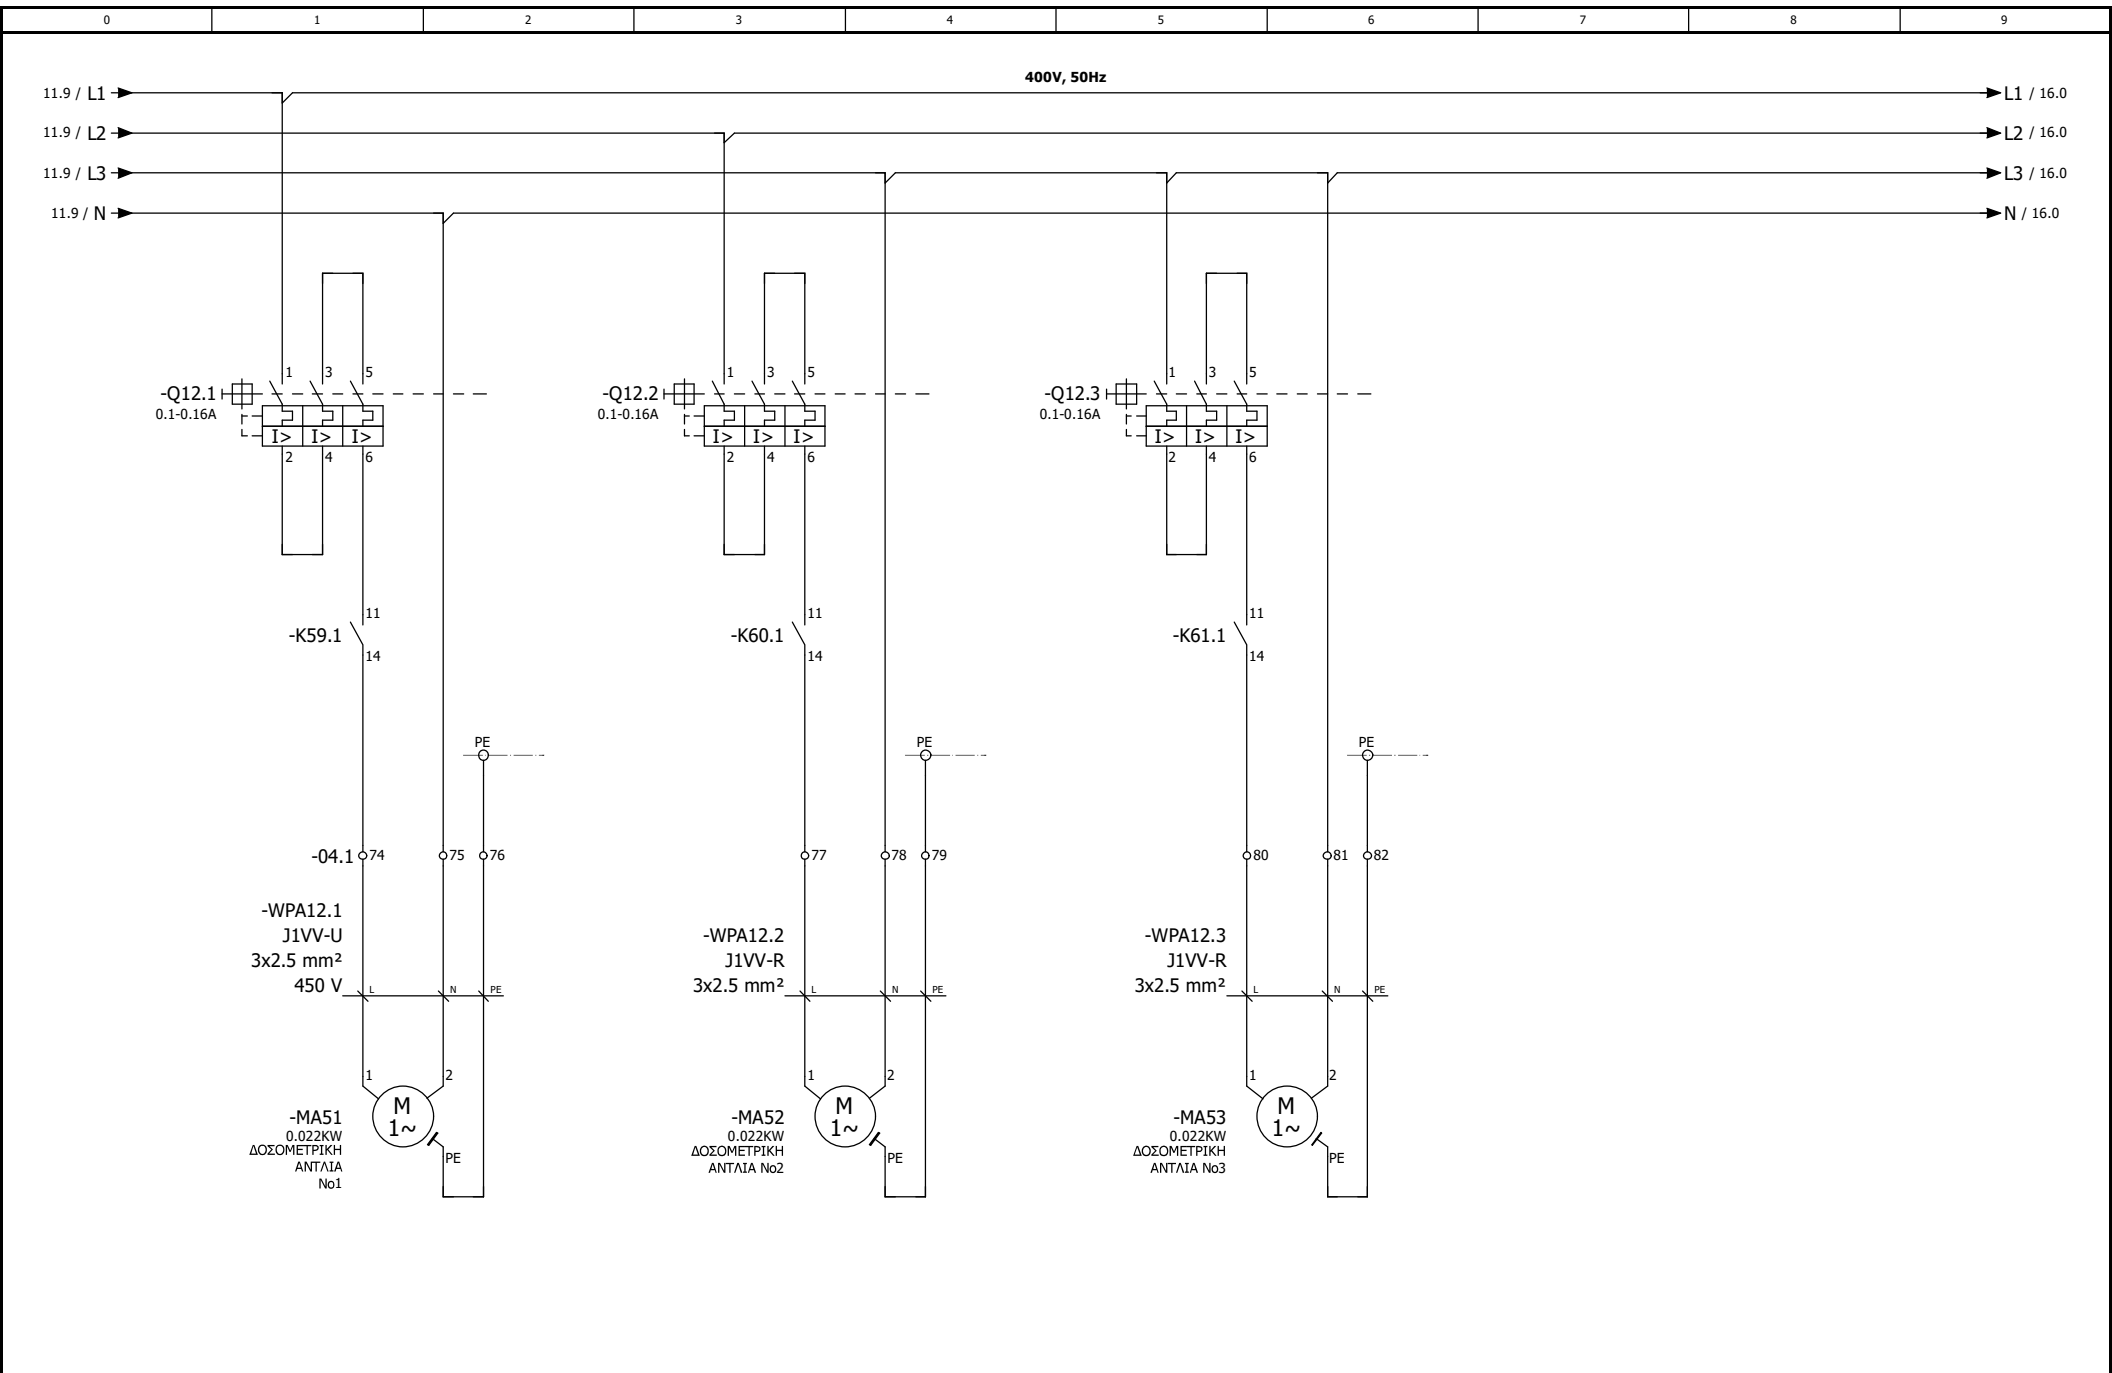


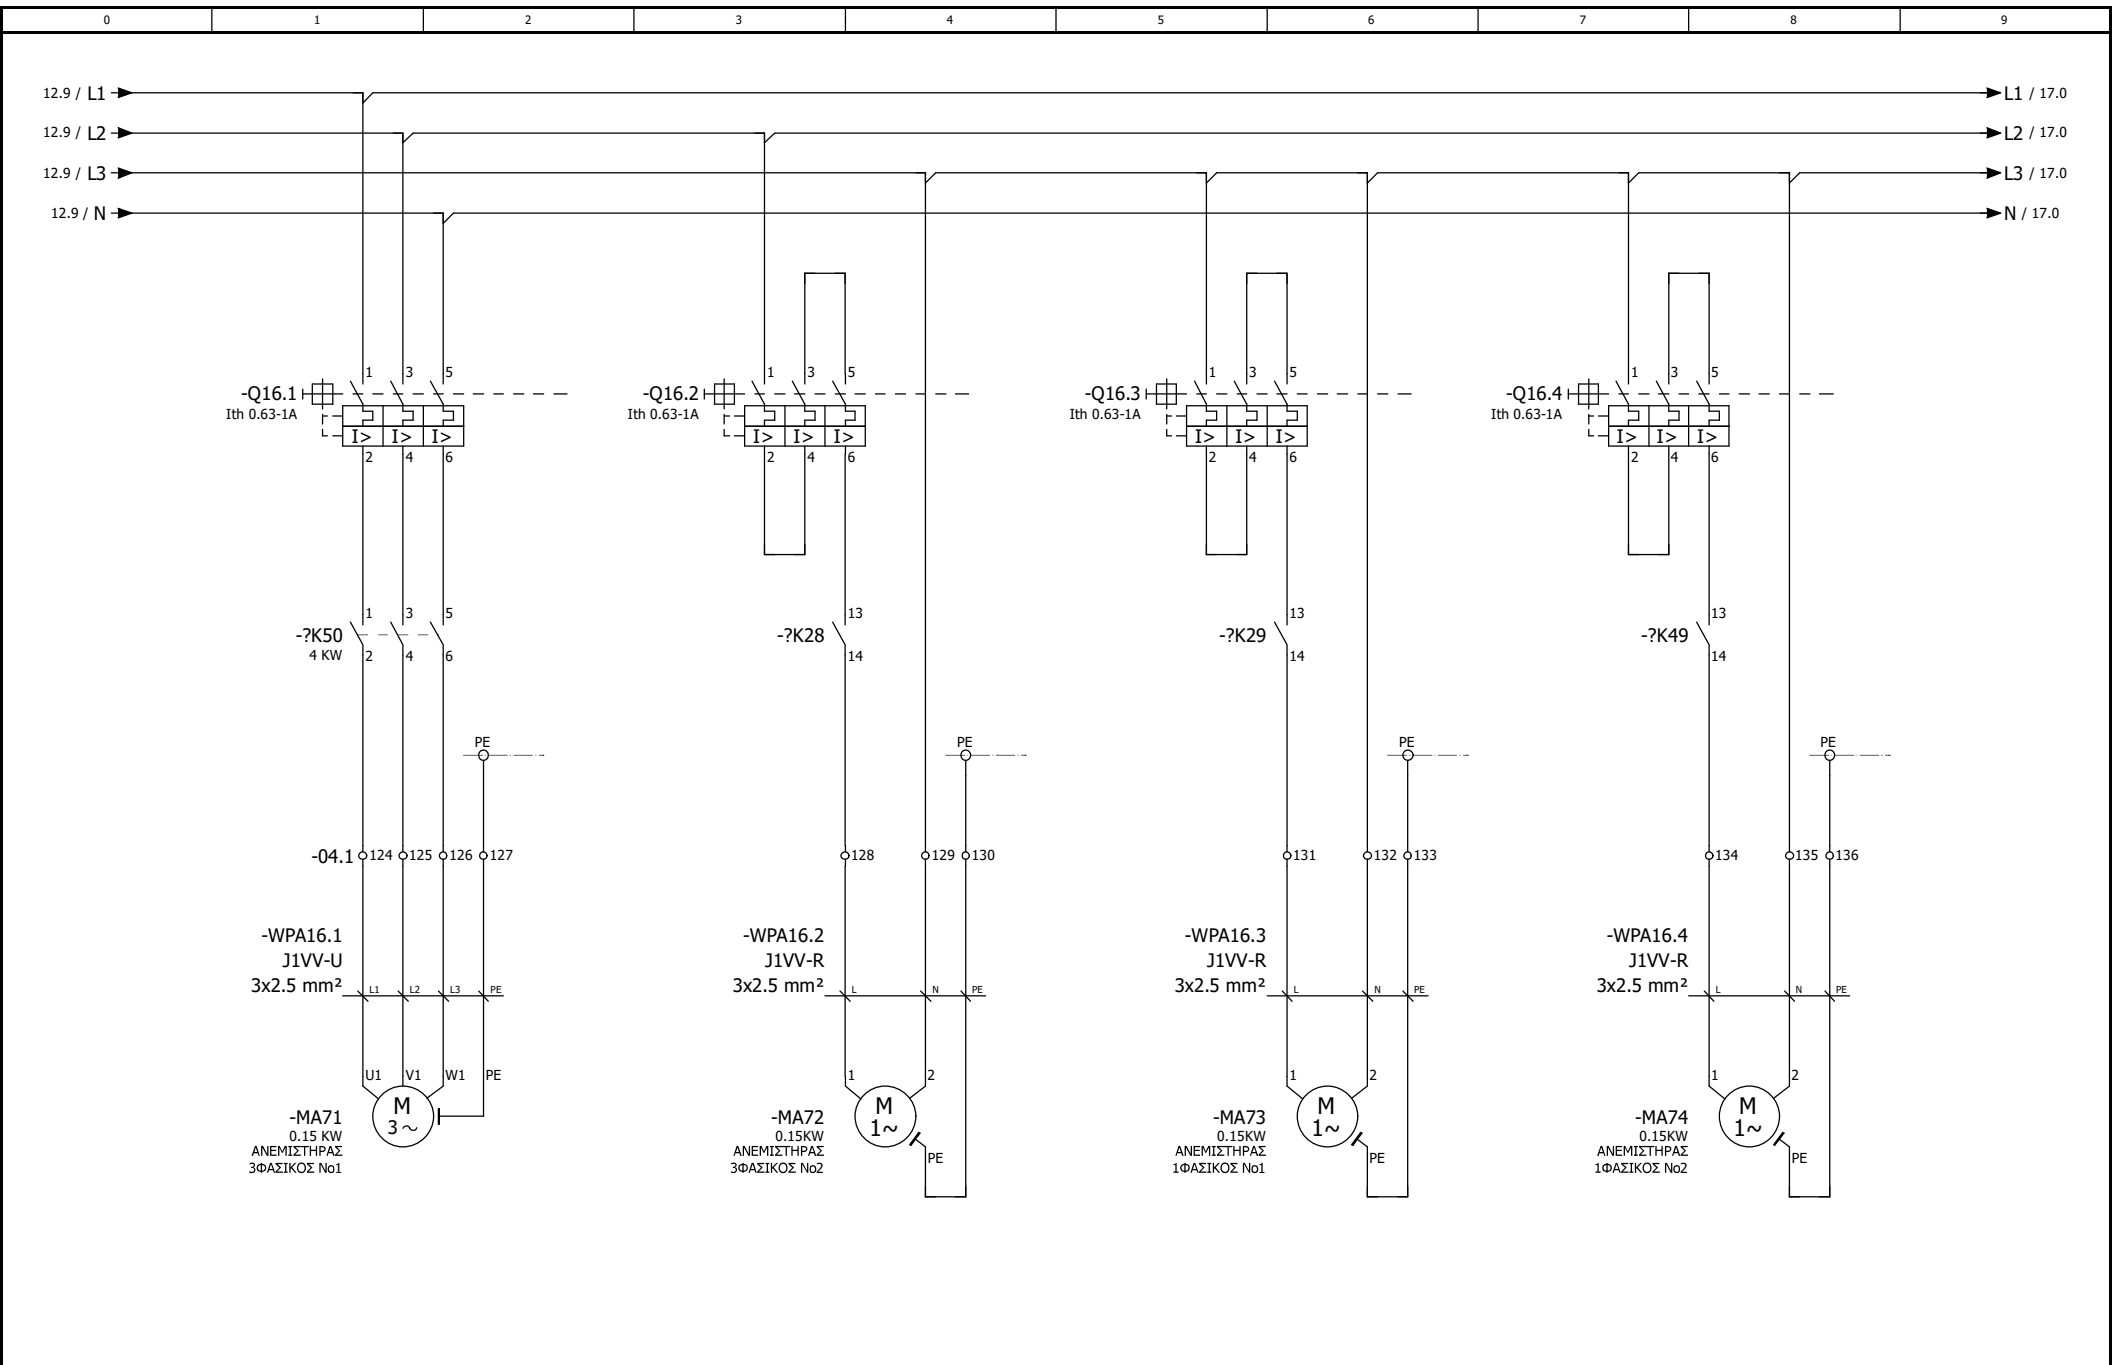

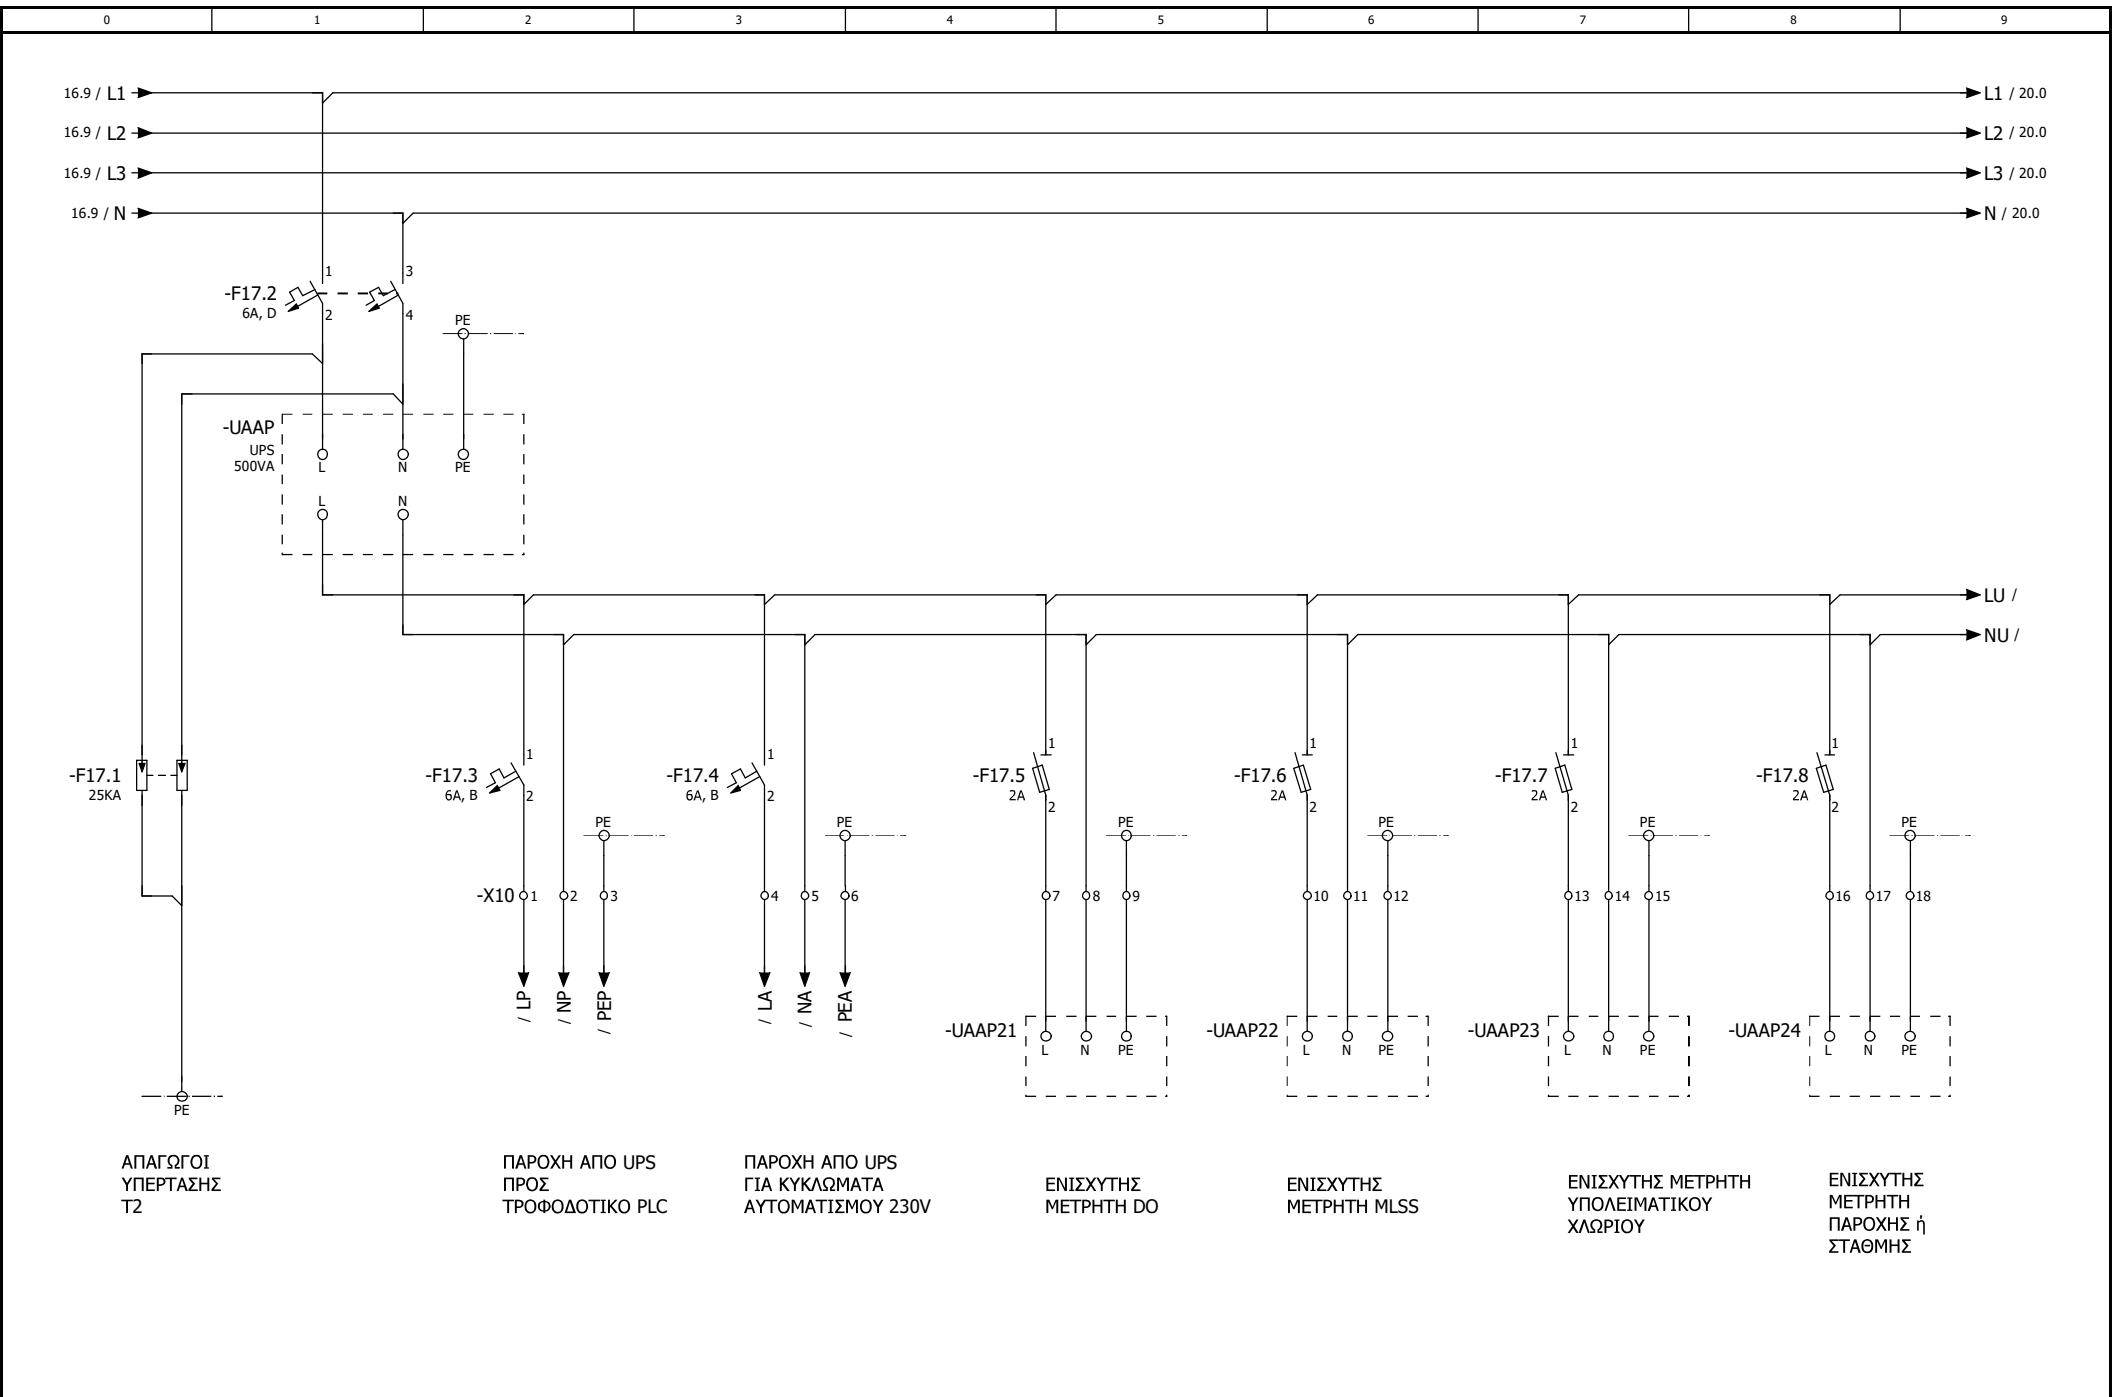


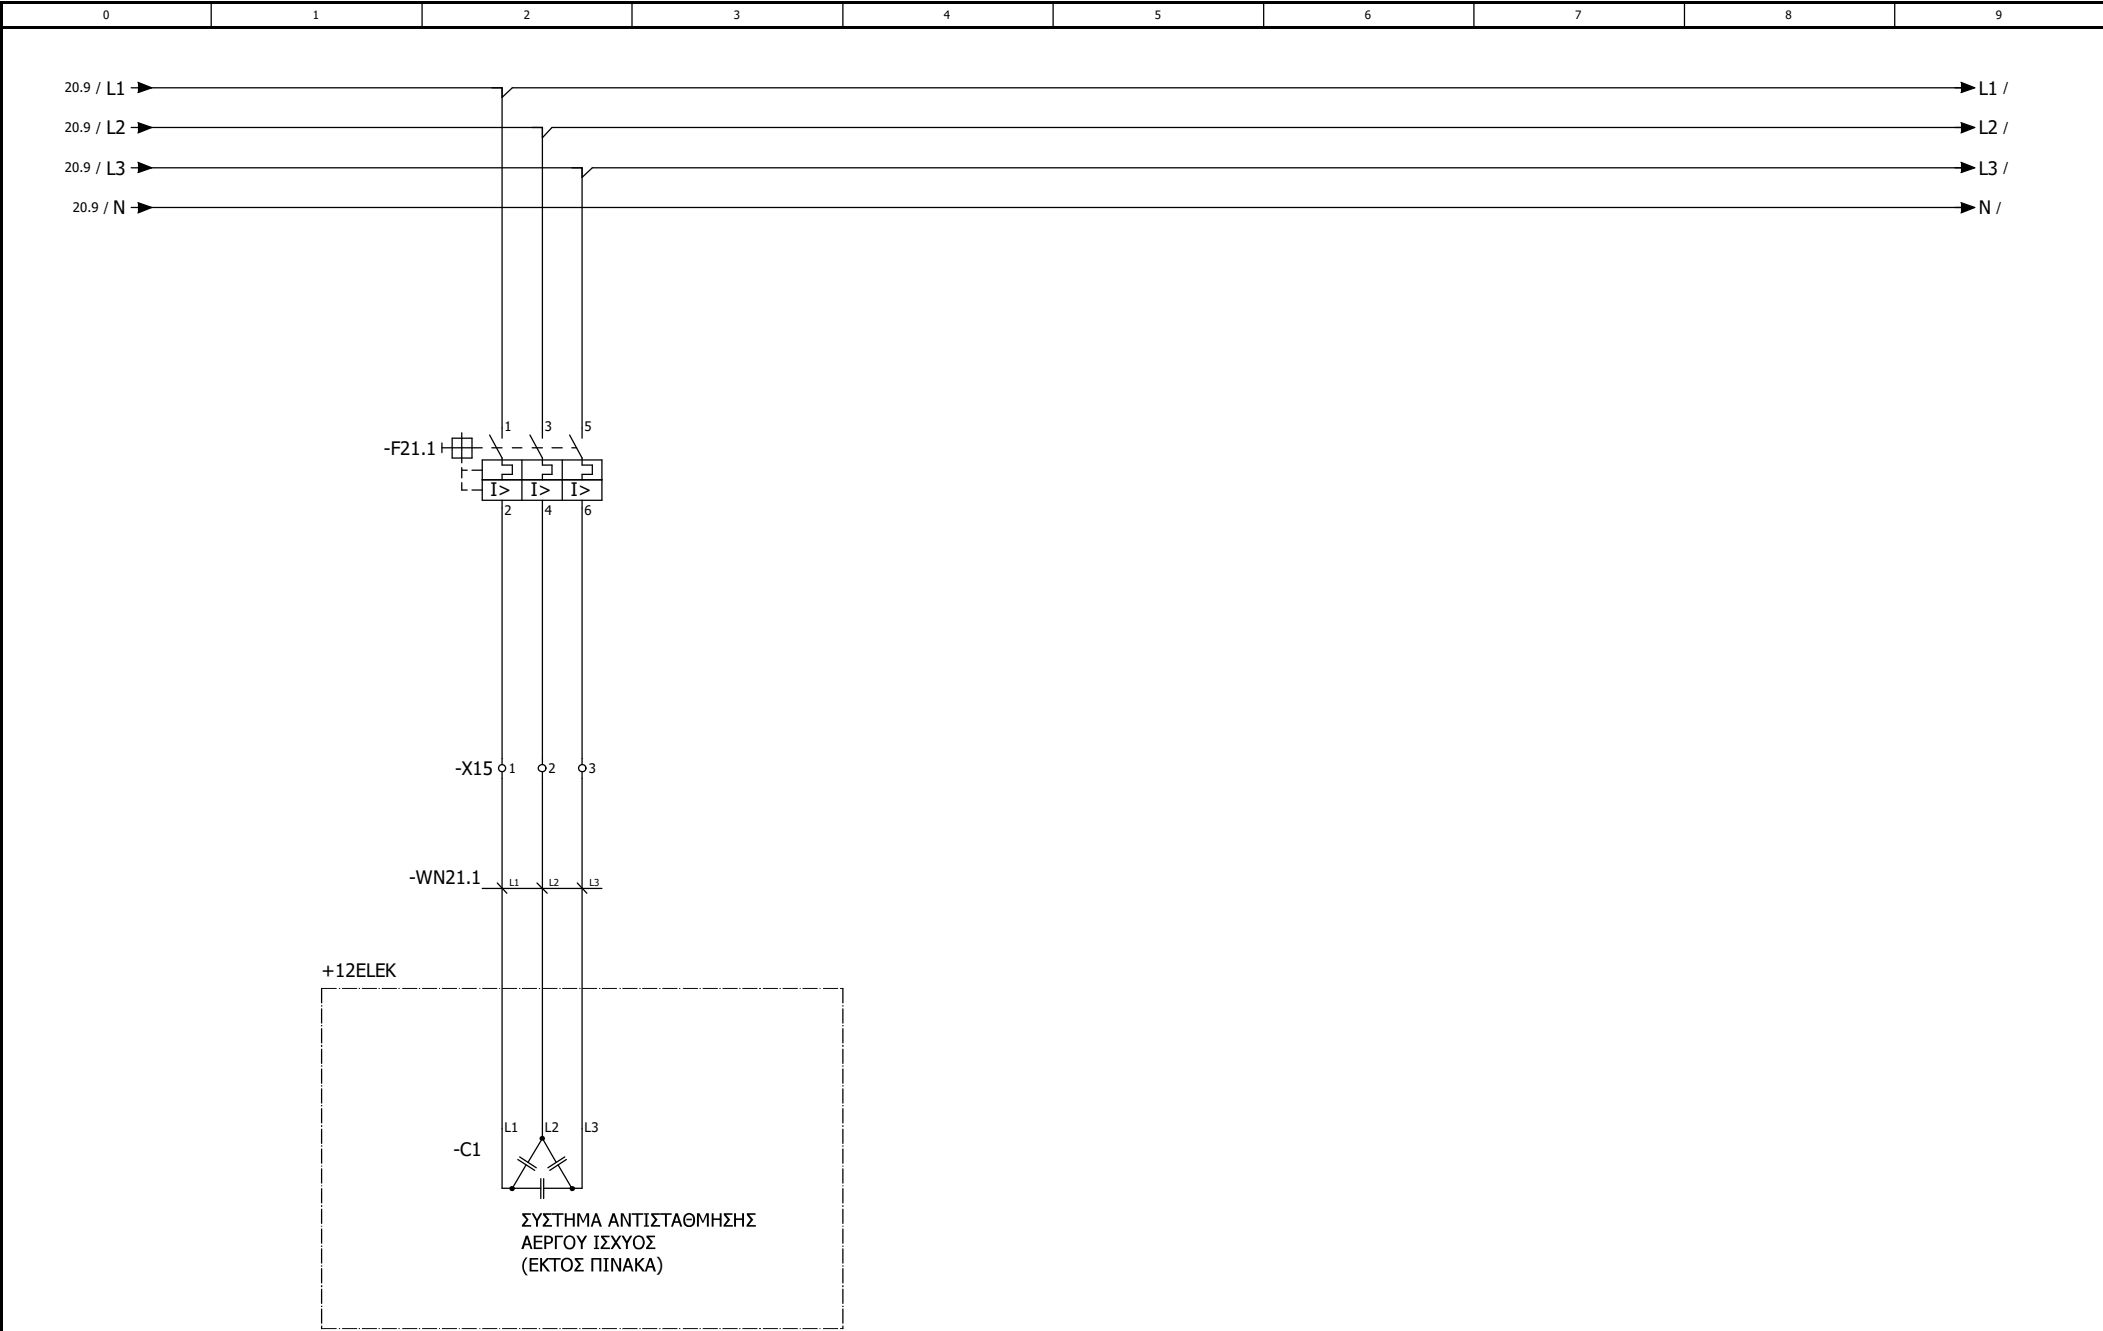





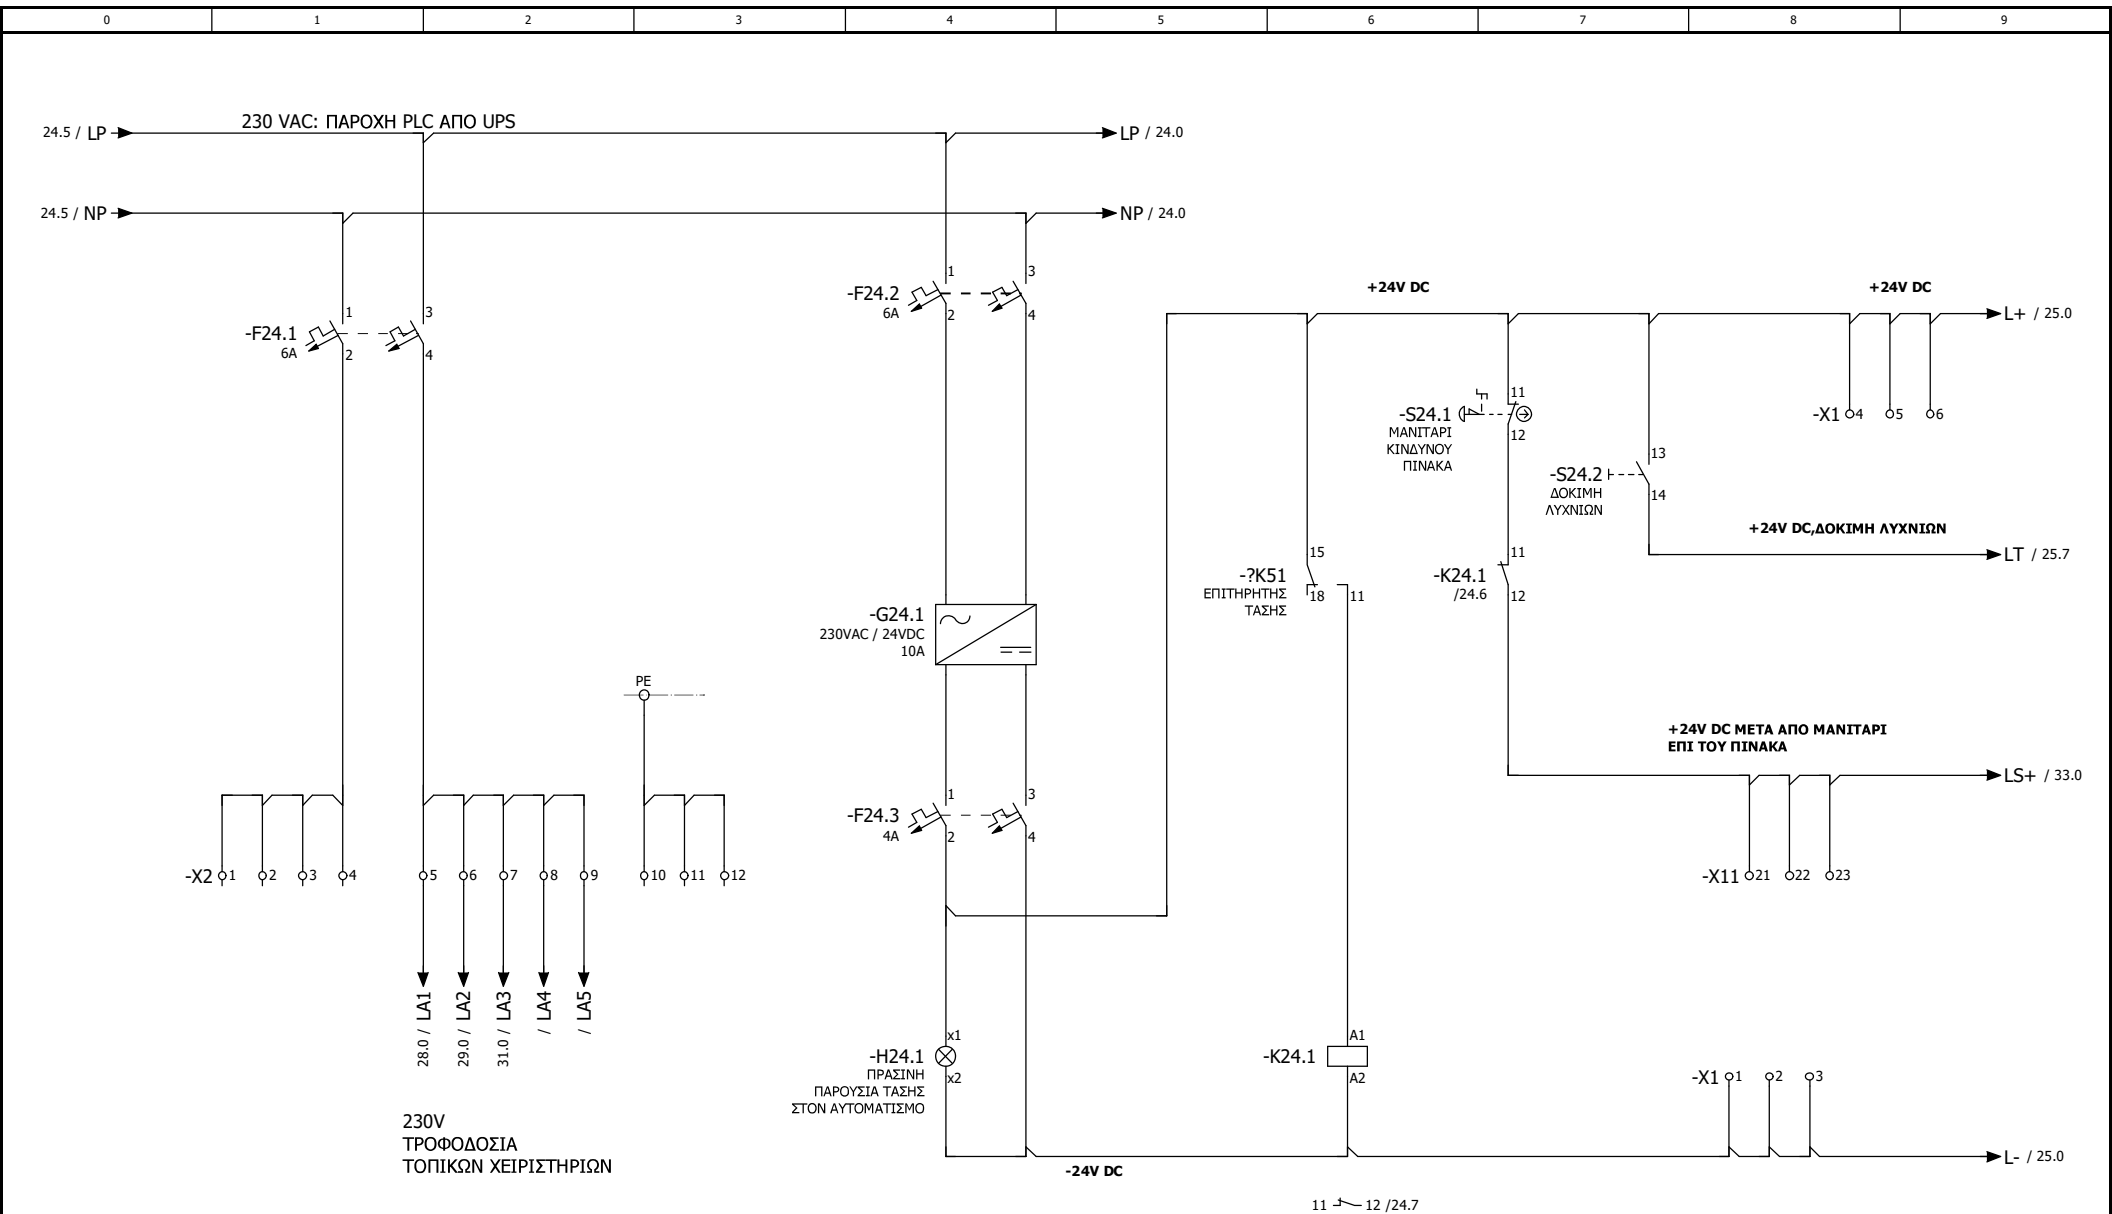



+POWER/23							25		
V1.0	MAP 2014	Version 1.0	ΜΓΣ	ΜΖΣ	ΜΖΣ	ΜΕΛΕΤΗ ΕΦΑΡΜΟΓΗΣ	ΕΓΚΑΤΑΣΤΑΣΗ ΕΠΕΞΕΡΓΑΣΙΑΣ ΛΥΜΑΤΩΝ ΔΟΝΟΥΣΑΣ		
						ΠΟΛΥΓΡΑΜΜΙΚΑ ΔΙΑΓΡΑΜΜΑΤΑ	= EEL		
						ΤΩΝ ΗΛΕΚΤΡΙΚΩΝ ΠΙΝΑΚΩΝ	+ AUTO		
ΤΑΣΕΙΣ ΕΛΕΓΧΟΥ ΑΥΤΟΜΑΤΙΣΜΟΥ							ΣΥΝ. ΣΕΛ. ΕΡΓΟΥ		
AC/DC ΤΡΟΦΟΔΟΤΙΚΟ 24VDC							55		
ΤΜΗΜΑ ΑΥΤΟΜΑΤΙΣΜΟΥ							σελ. 24		
							από 27		

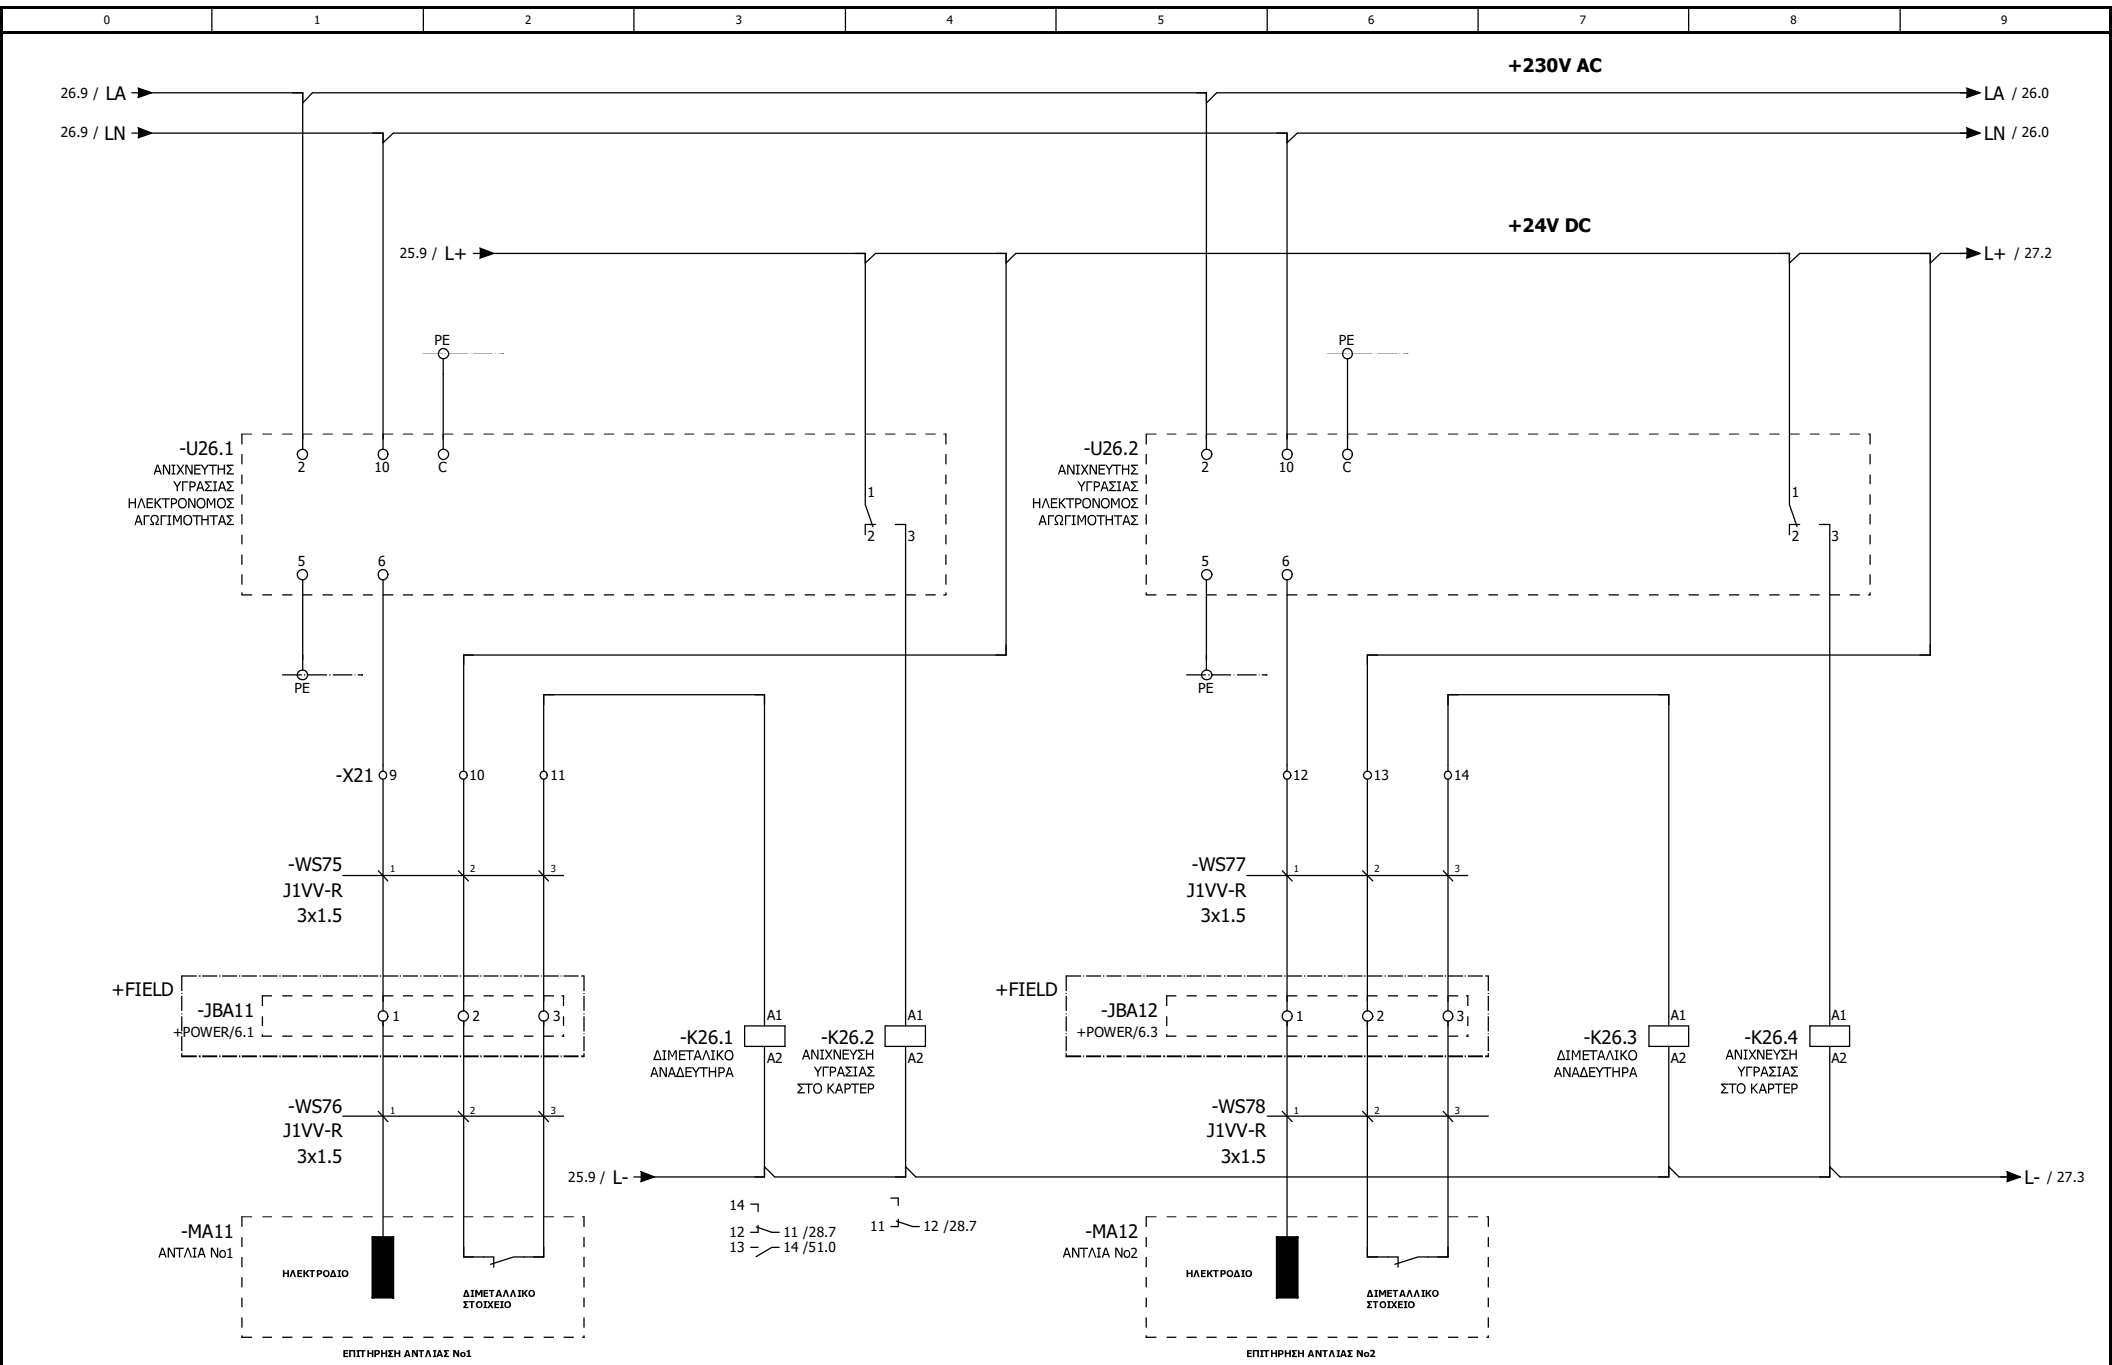


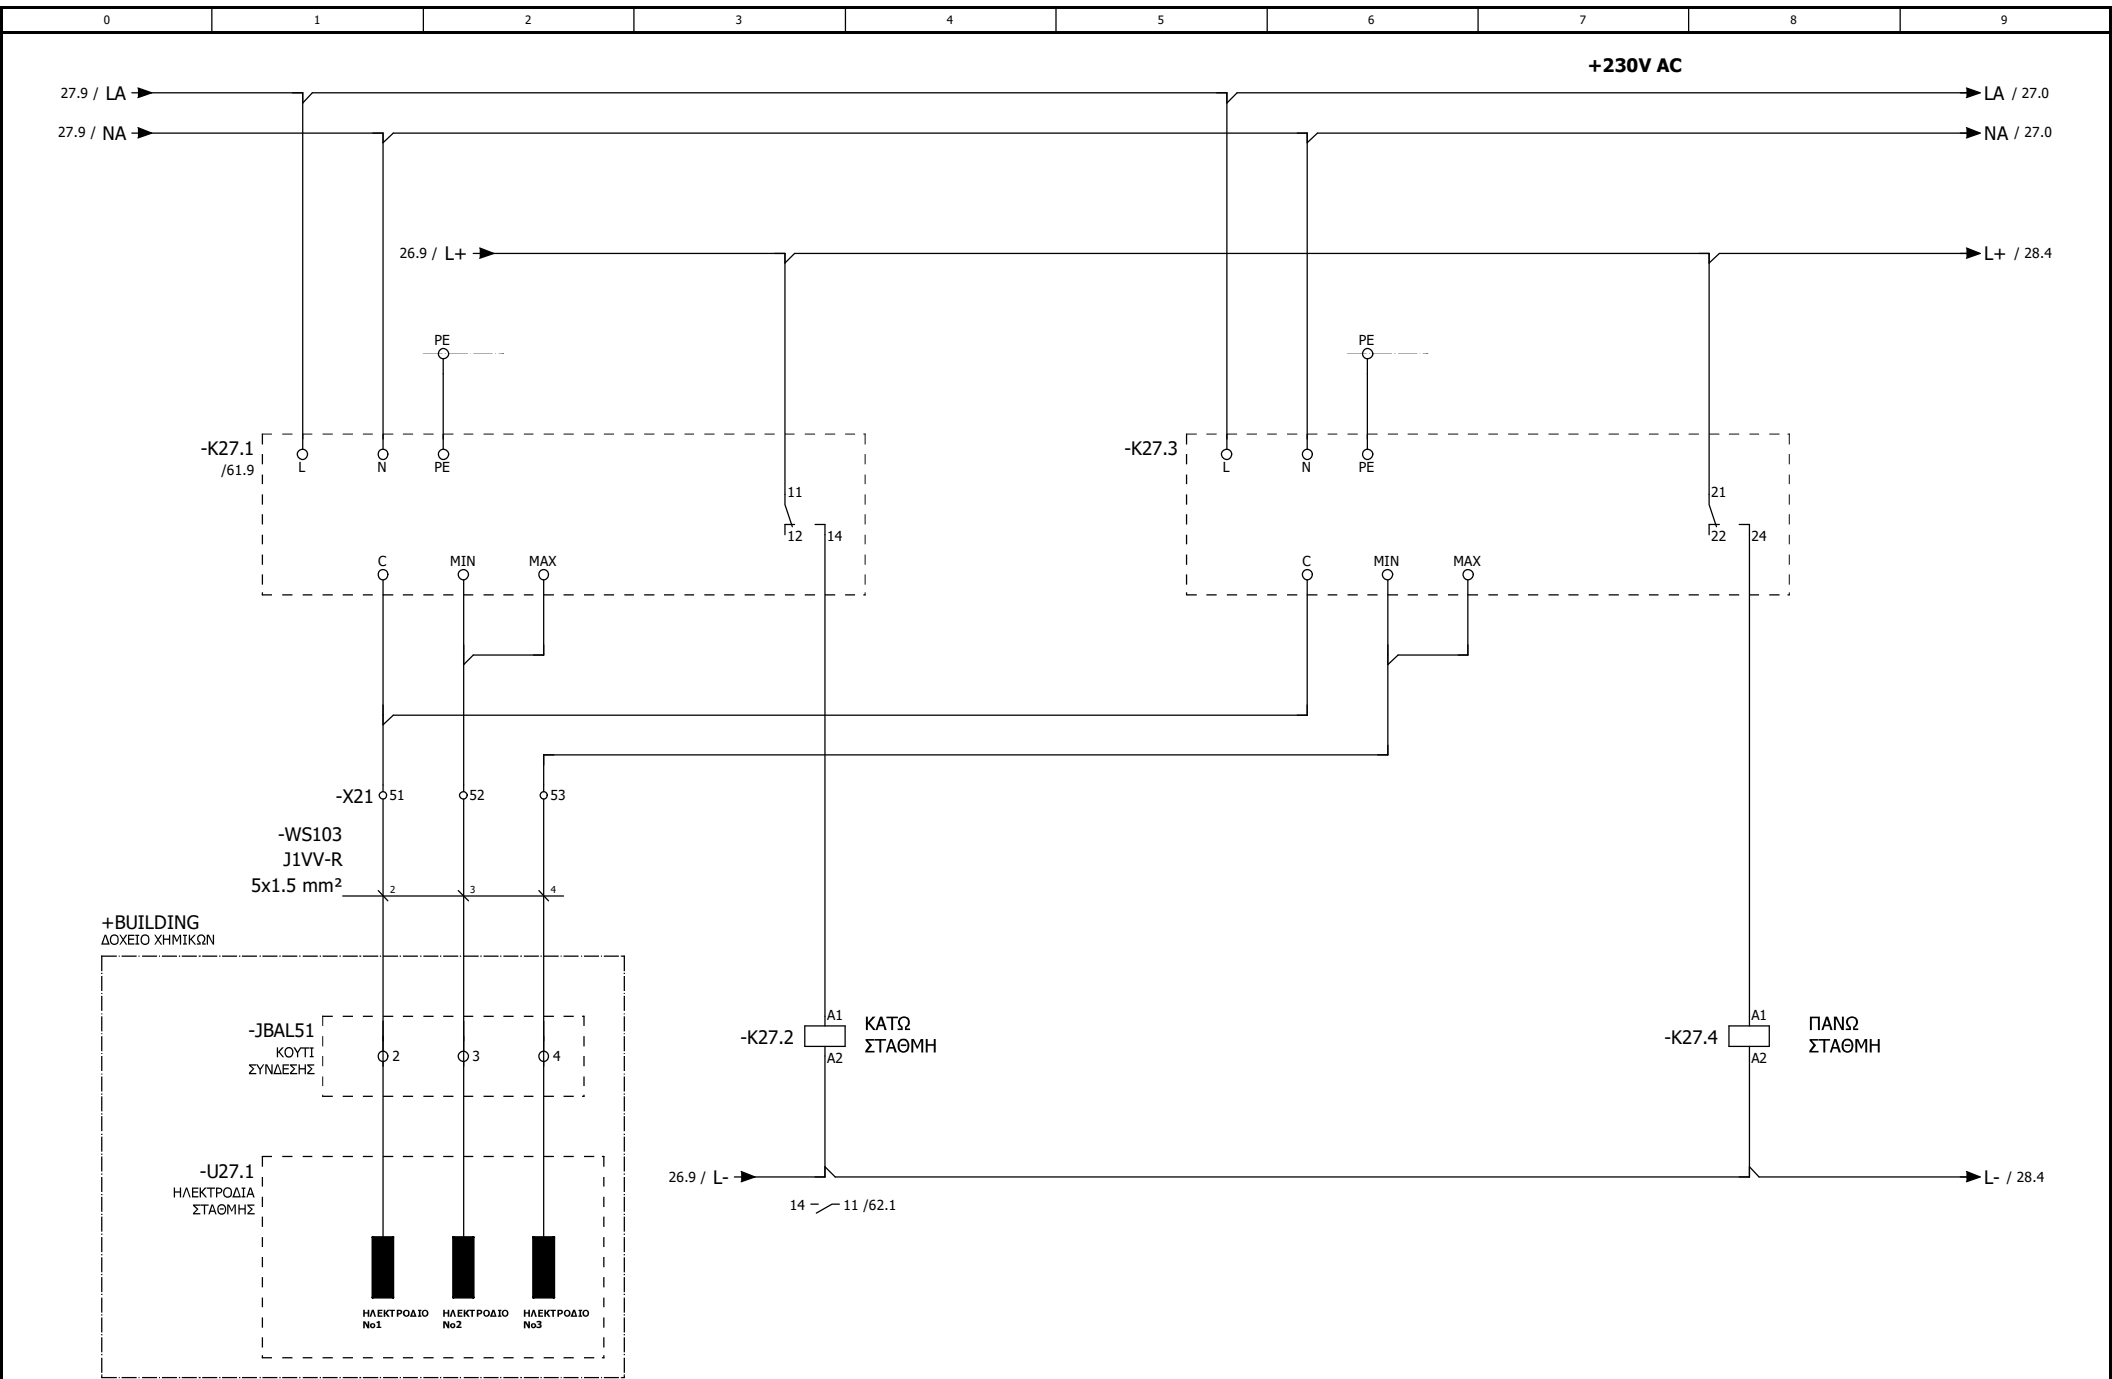



26						28		
V1.0	MAP 2014	Version 1.0	ΜΓΣ	ΜΖΣ	ΜΖΣ	ΜΕΛΕΤΗ ΕΦΑΡΜΟΓΗΣ		
						ΗΛΕΚΤΡΟΔΙΑ ΣΤΑΘΜΗΣ ΔΟΧΕΙΩΝ ΧΗΜΙΚΩΝ		
ΑΝΑΘΕΩΡΗΣΗ			ΗΜΕΡΟΜΗΝΙΑ			ΕΓΚΑΤΑΣΤΑΣΗ ΕΠΕΞΕΡΓΑΣΙΑΣ ΛΥΜΑΤΩΝ ΔΟΝΟΥΣΑΣ		
ΟΝΟΜΑΣΙΑ			ΣΧΕΔ.			= EEL		
ΕΛΕΓΧ.			ΘΕΩΡ.			+ AUTO		
ΤΩΝ ΗΛΕΚΤΡΙΚΩΝ ΠΙΝΑΚΩΝ			ΣΥΝ. ΣΕΛ. ΕΡΓΟΥ			ΤΜΗΜΑ ΑΥΤΟΜΑΤΙΣΜΟΥ		
			55			σελ. 27		
						από 27		

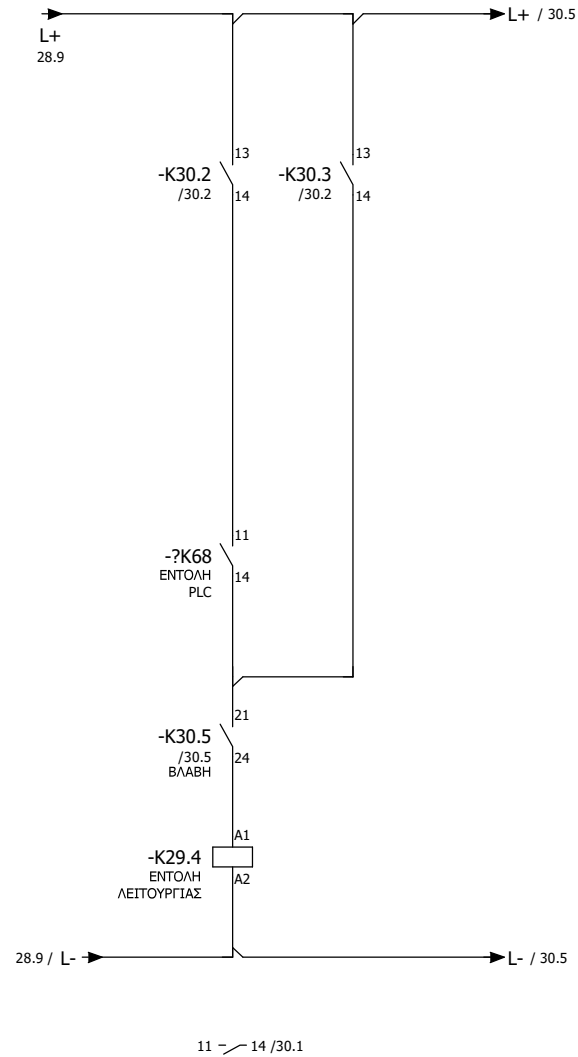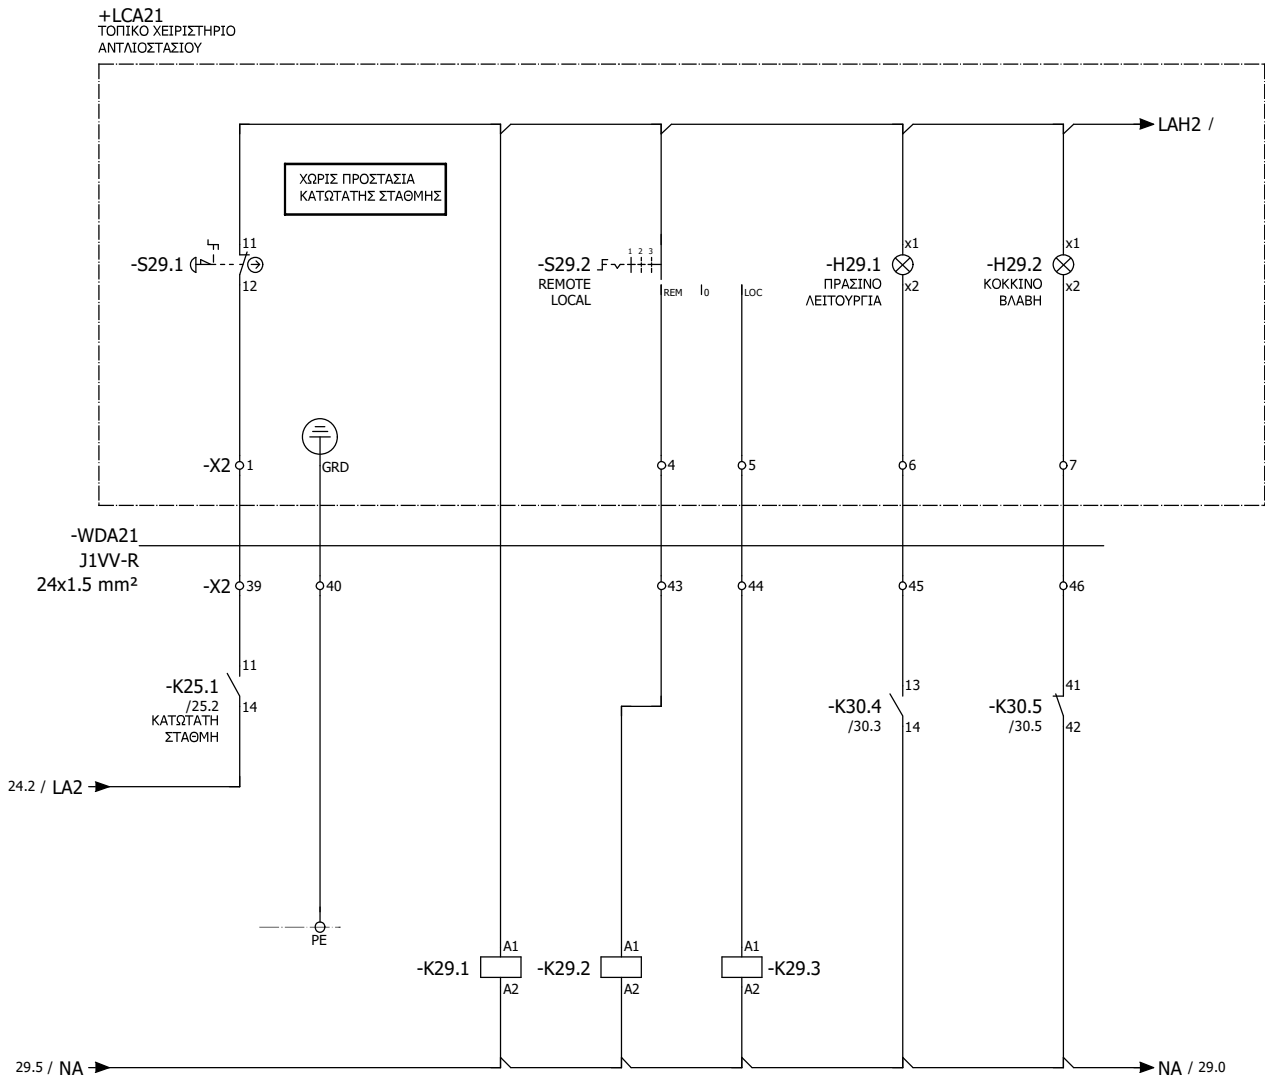


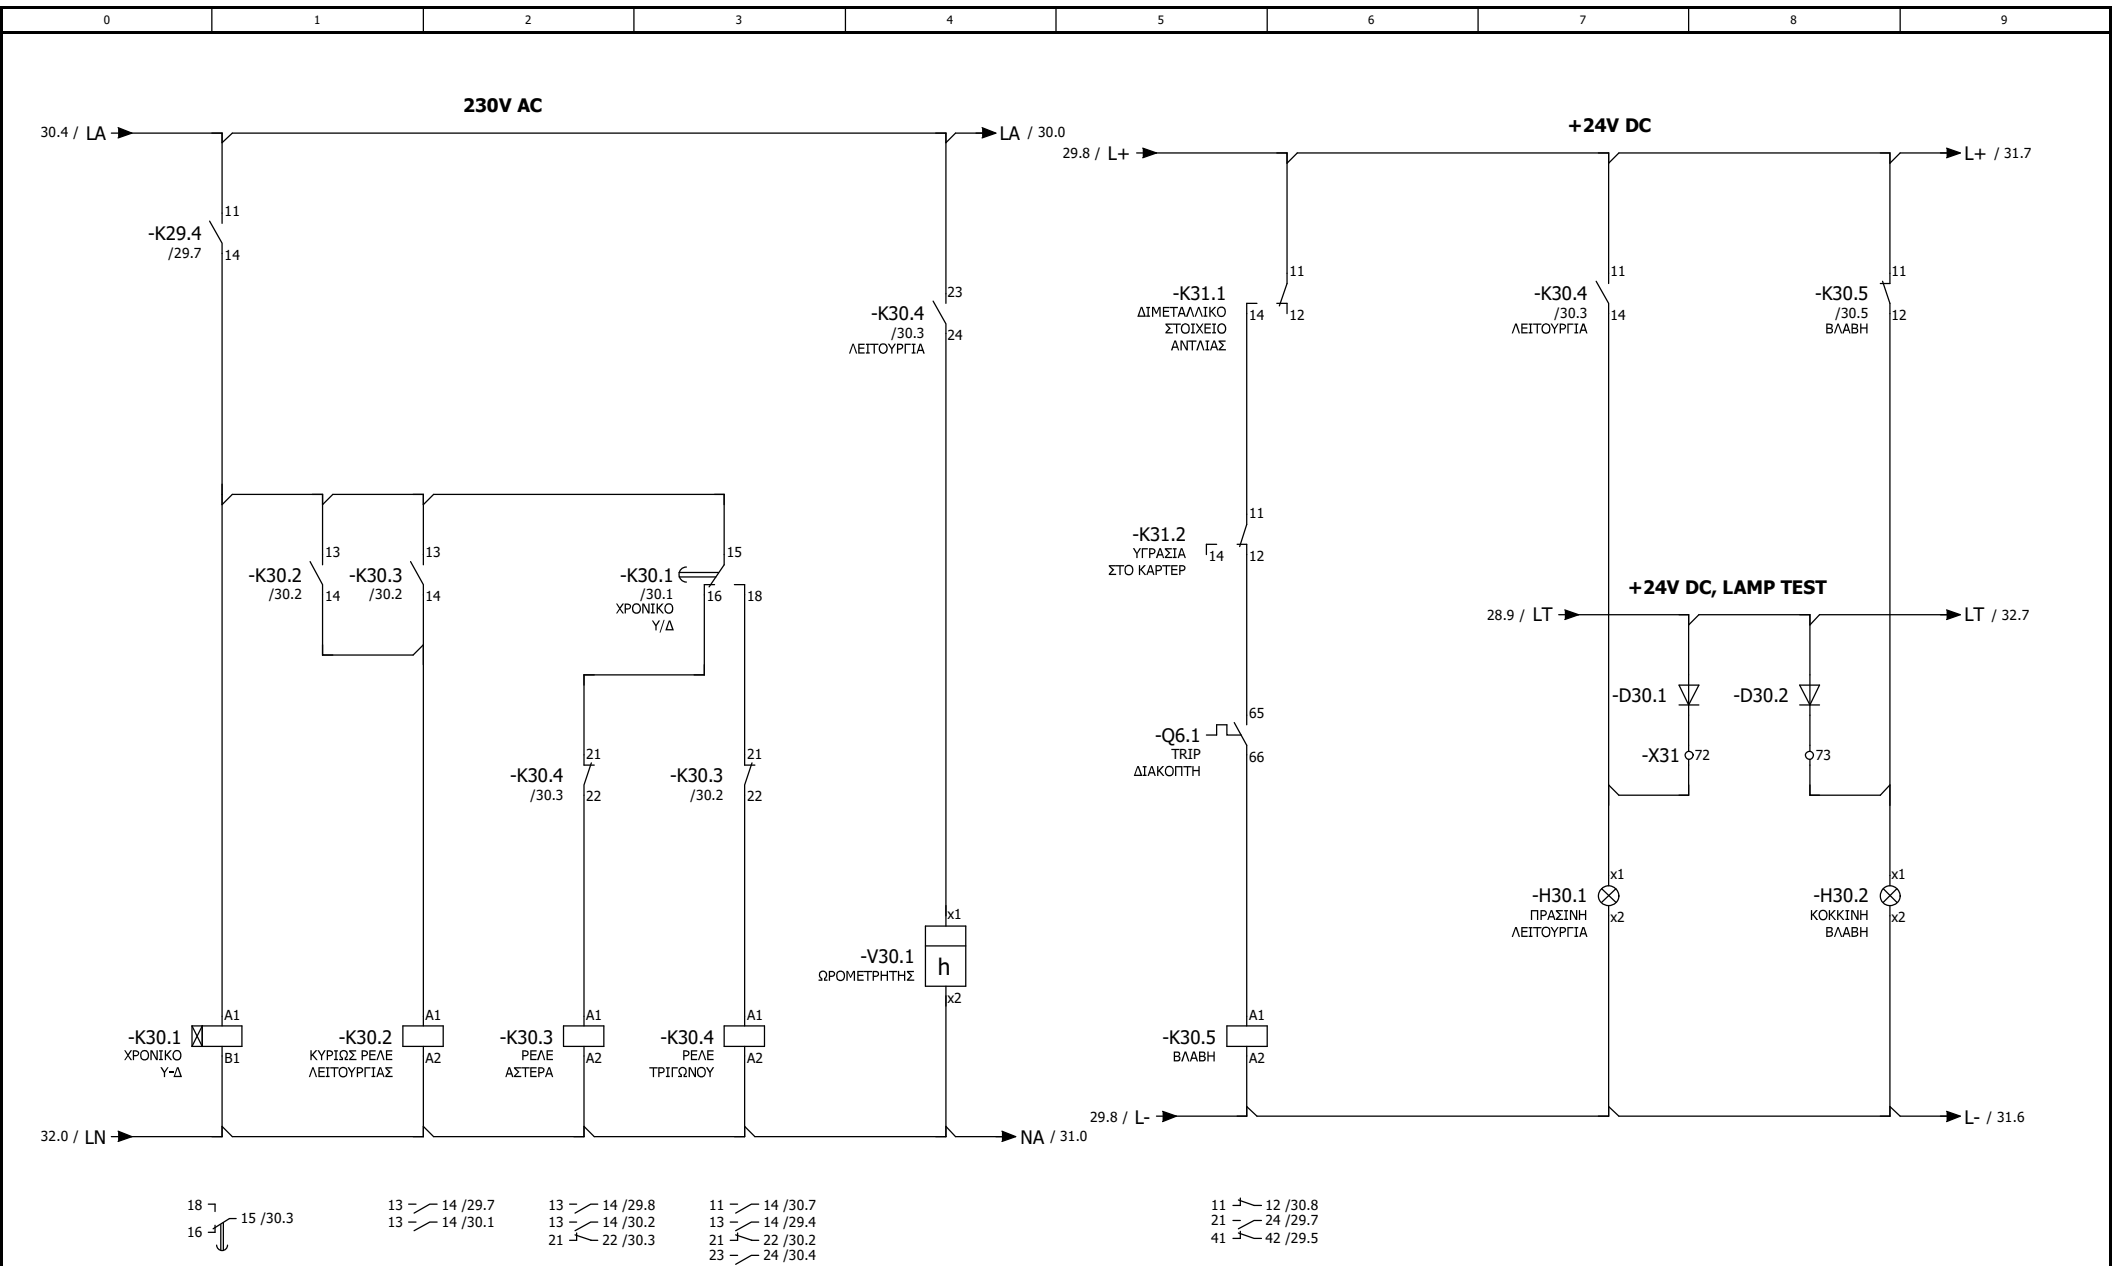


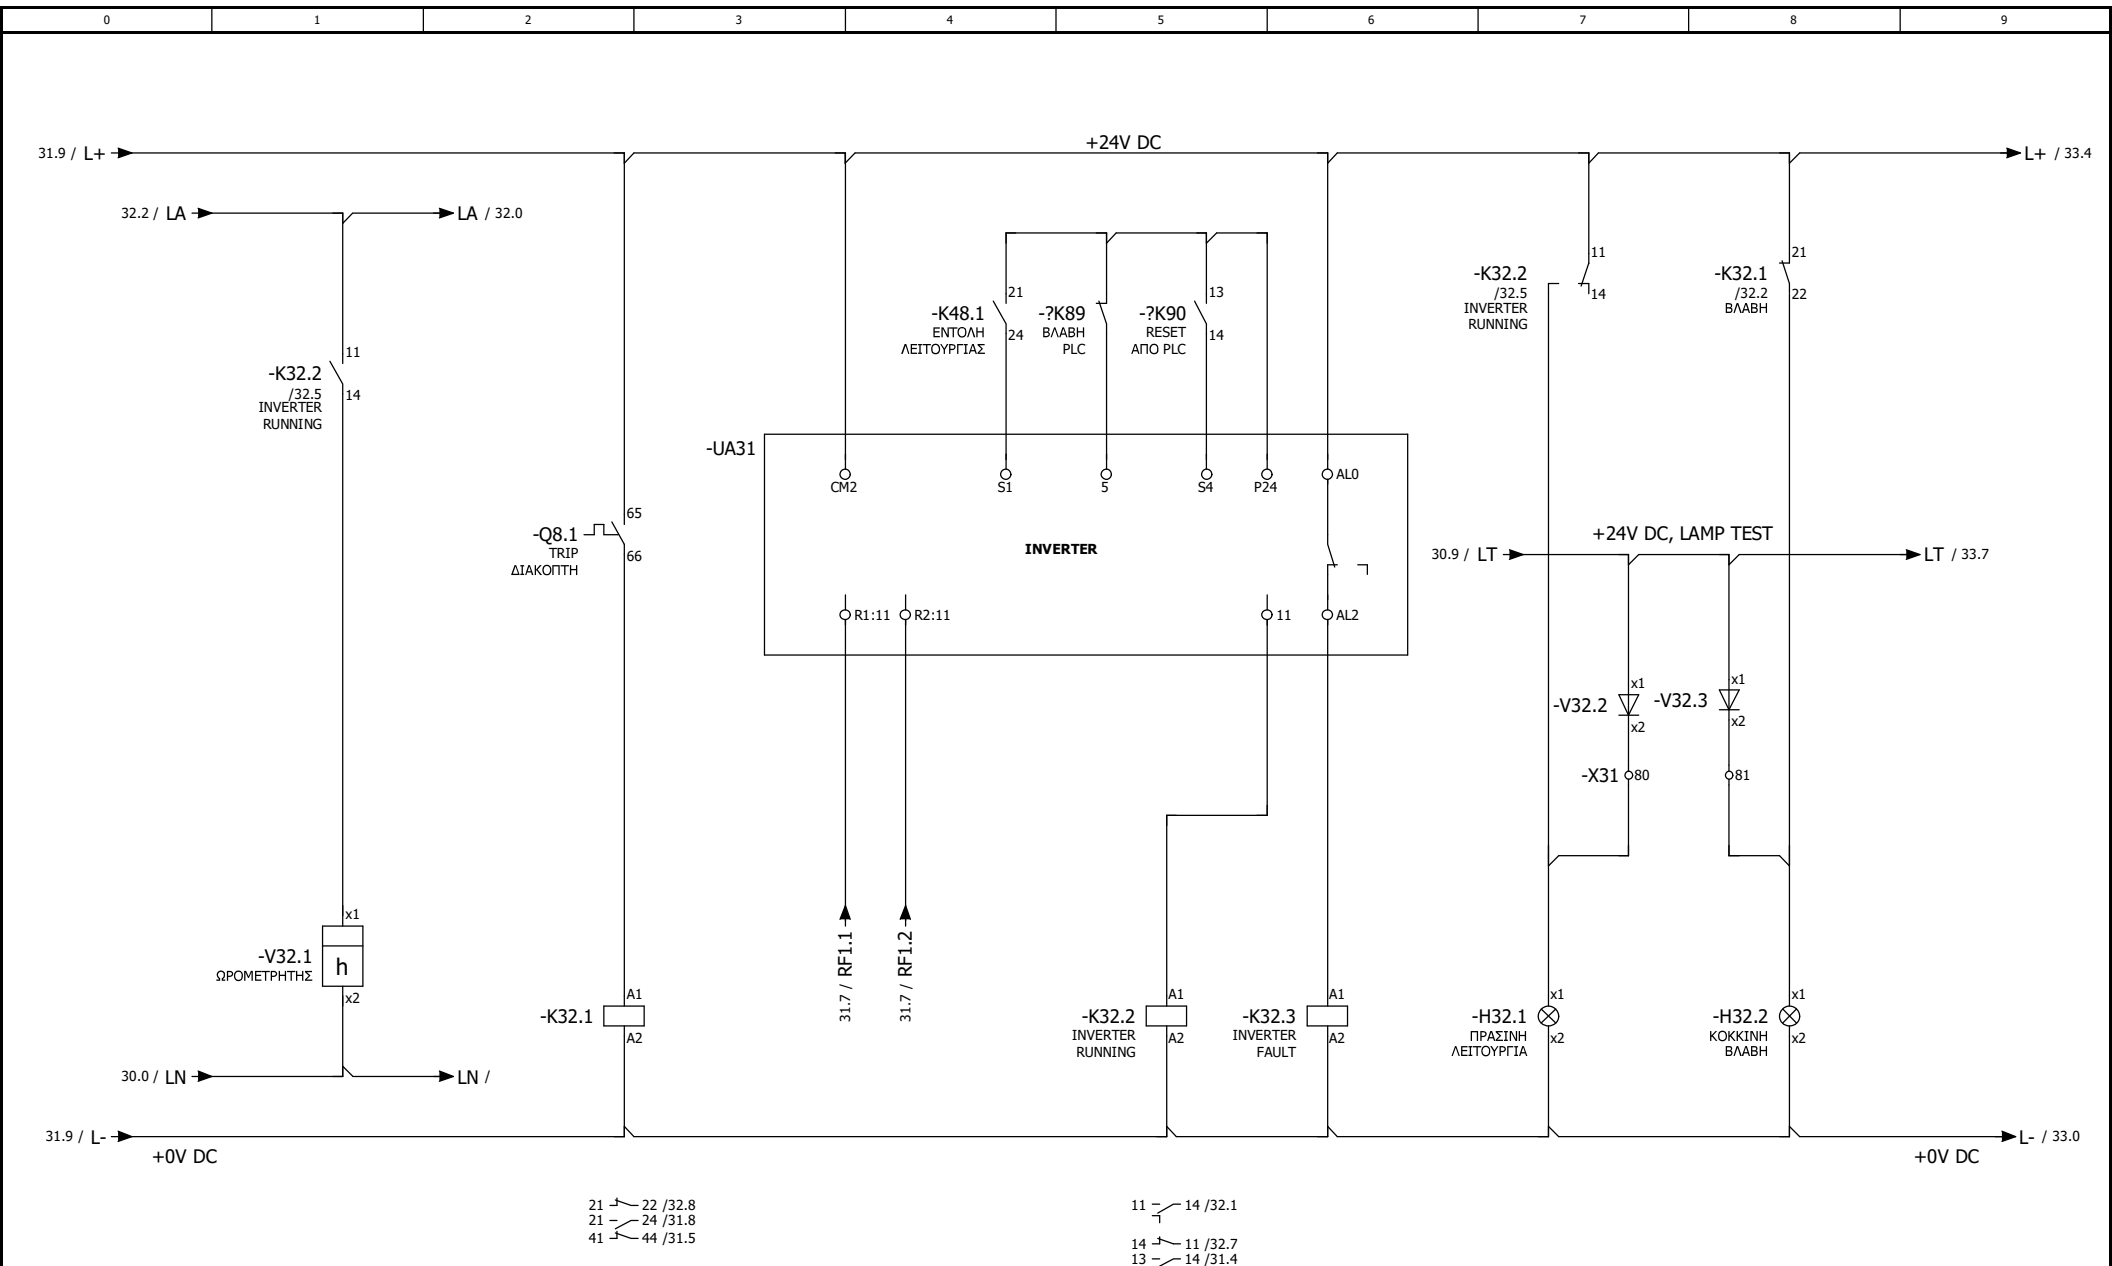


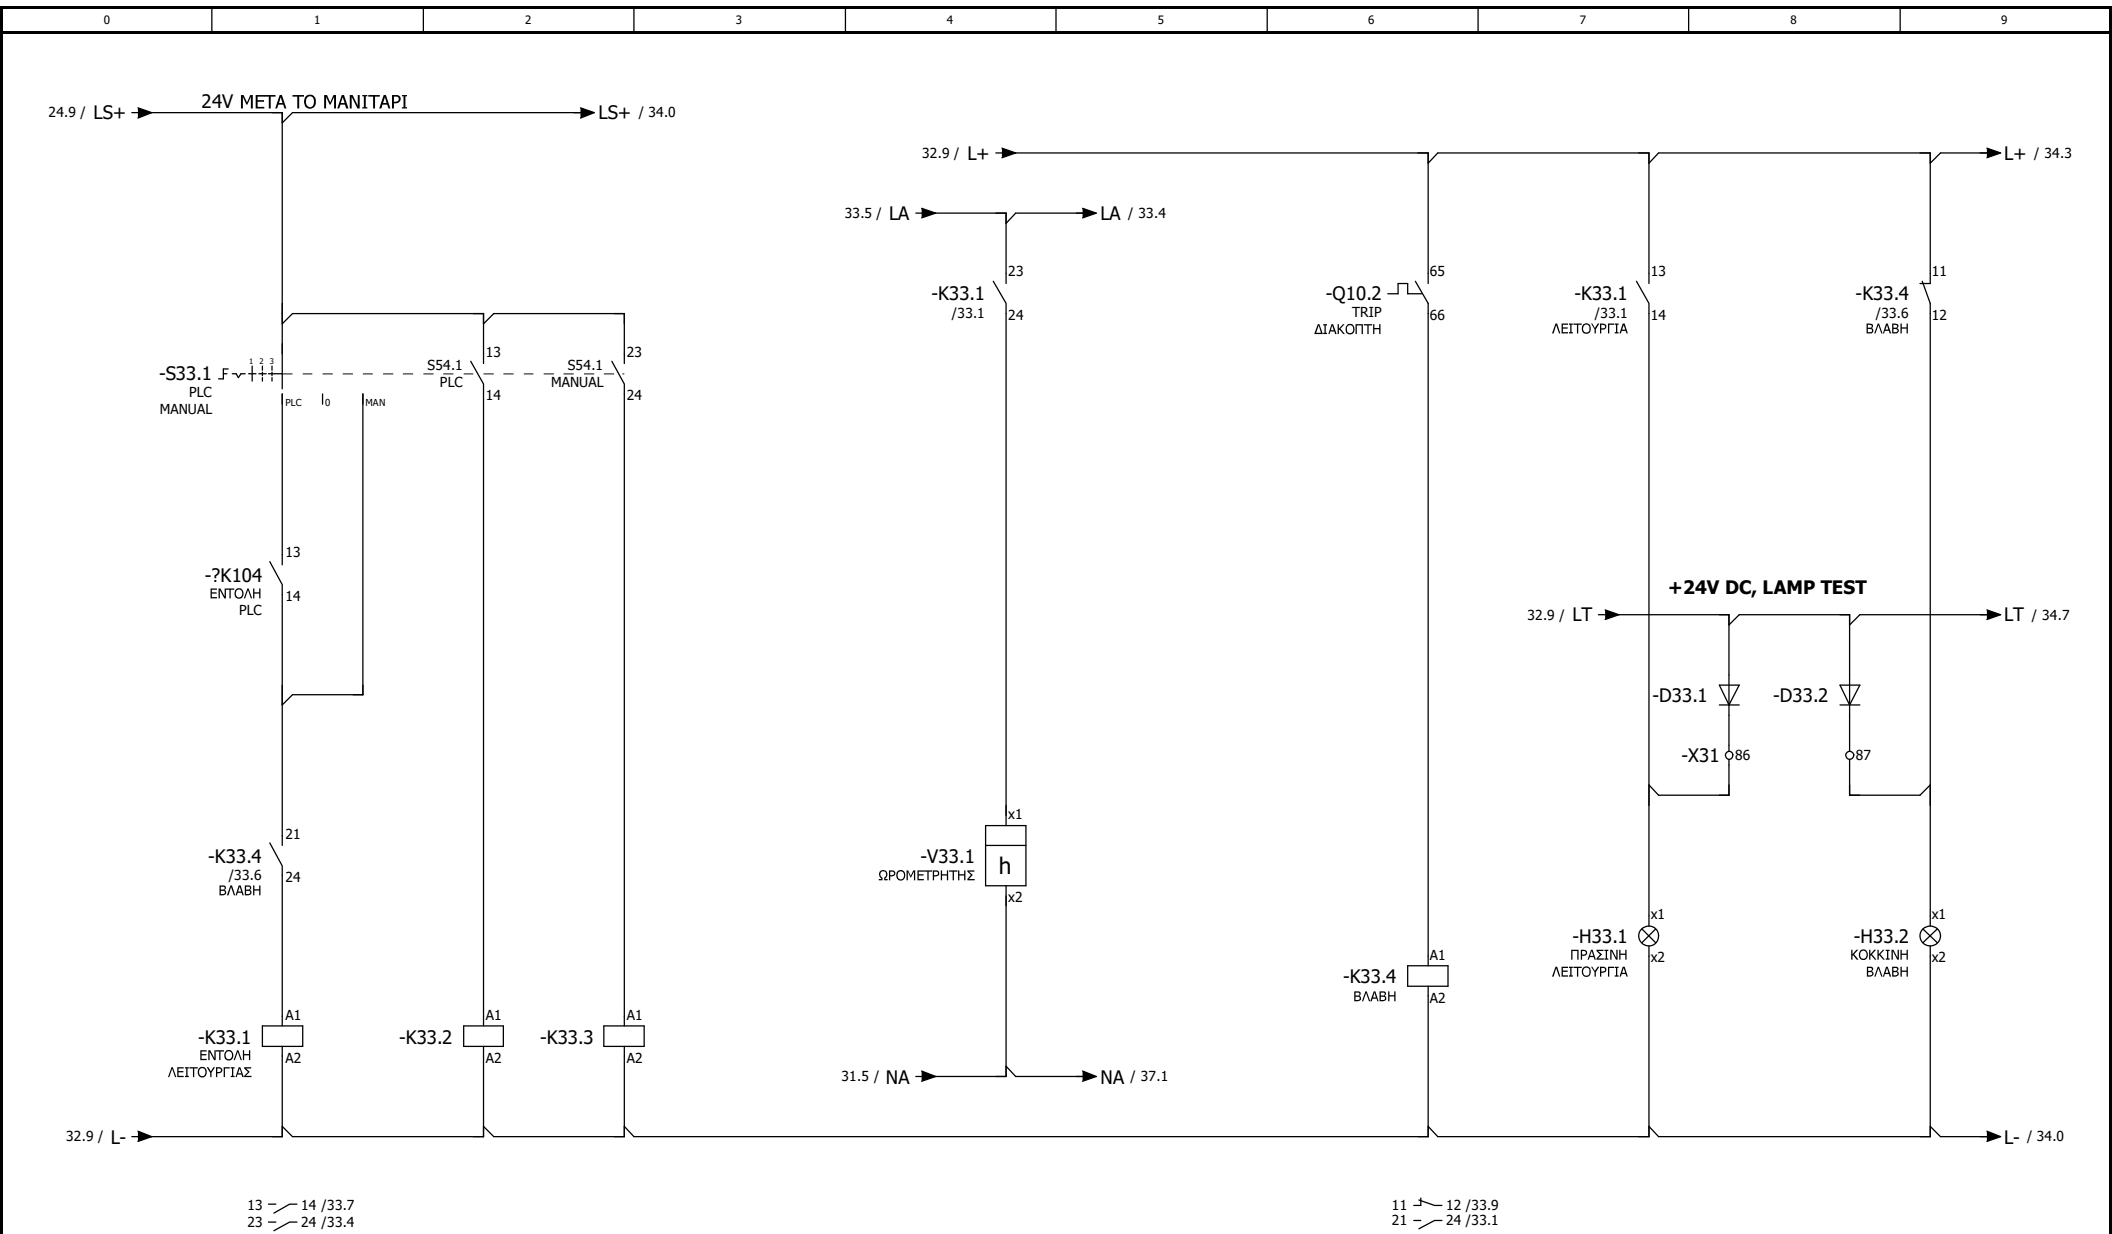


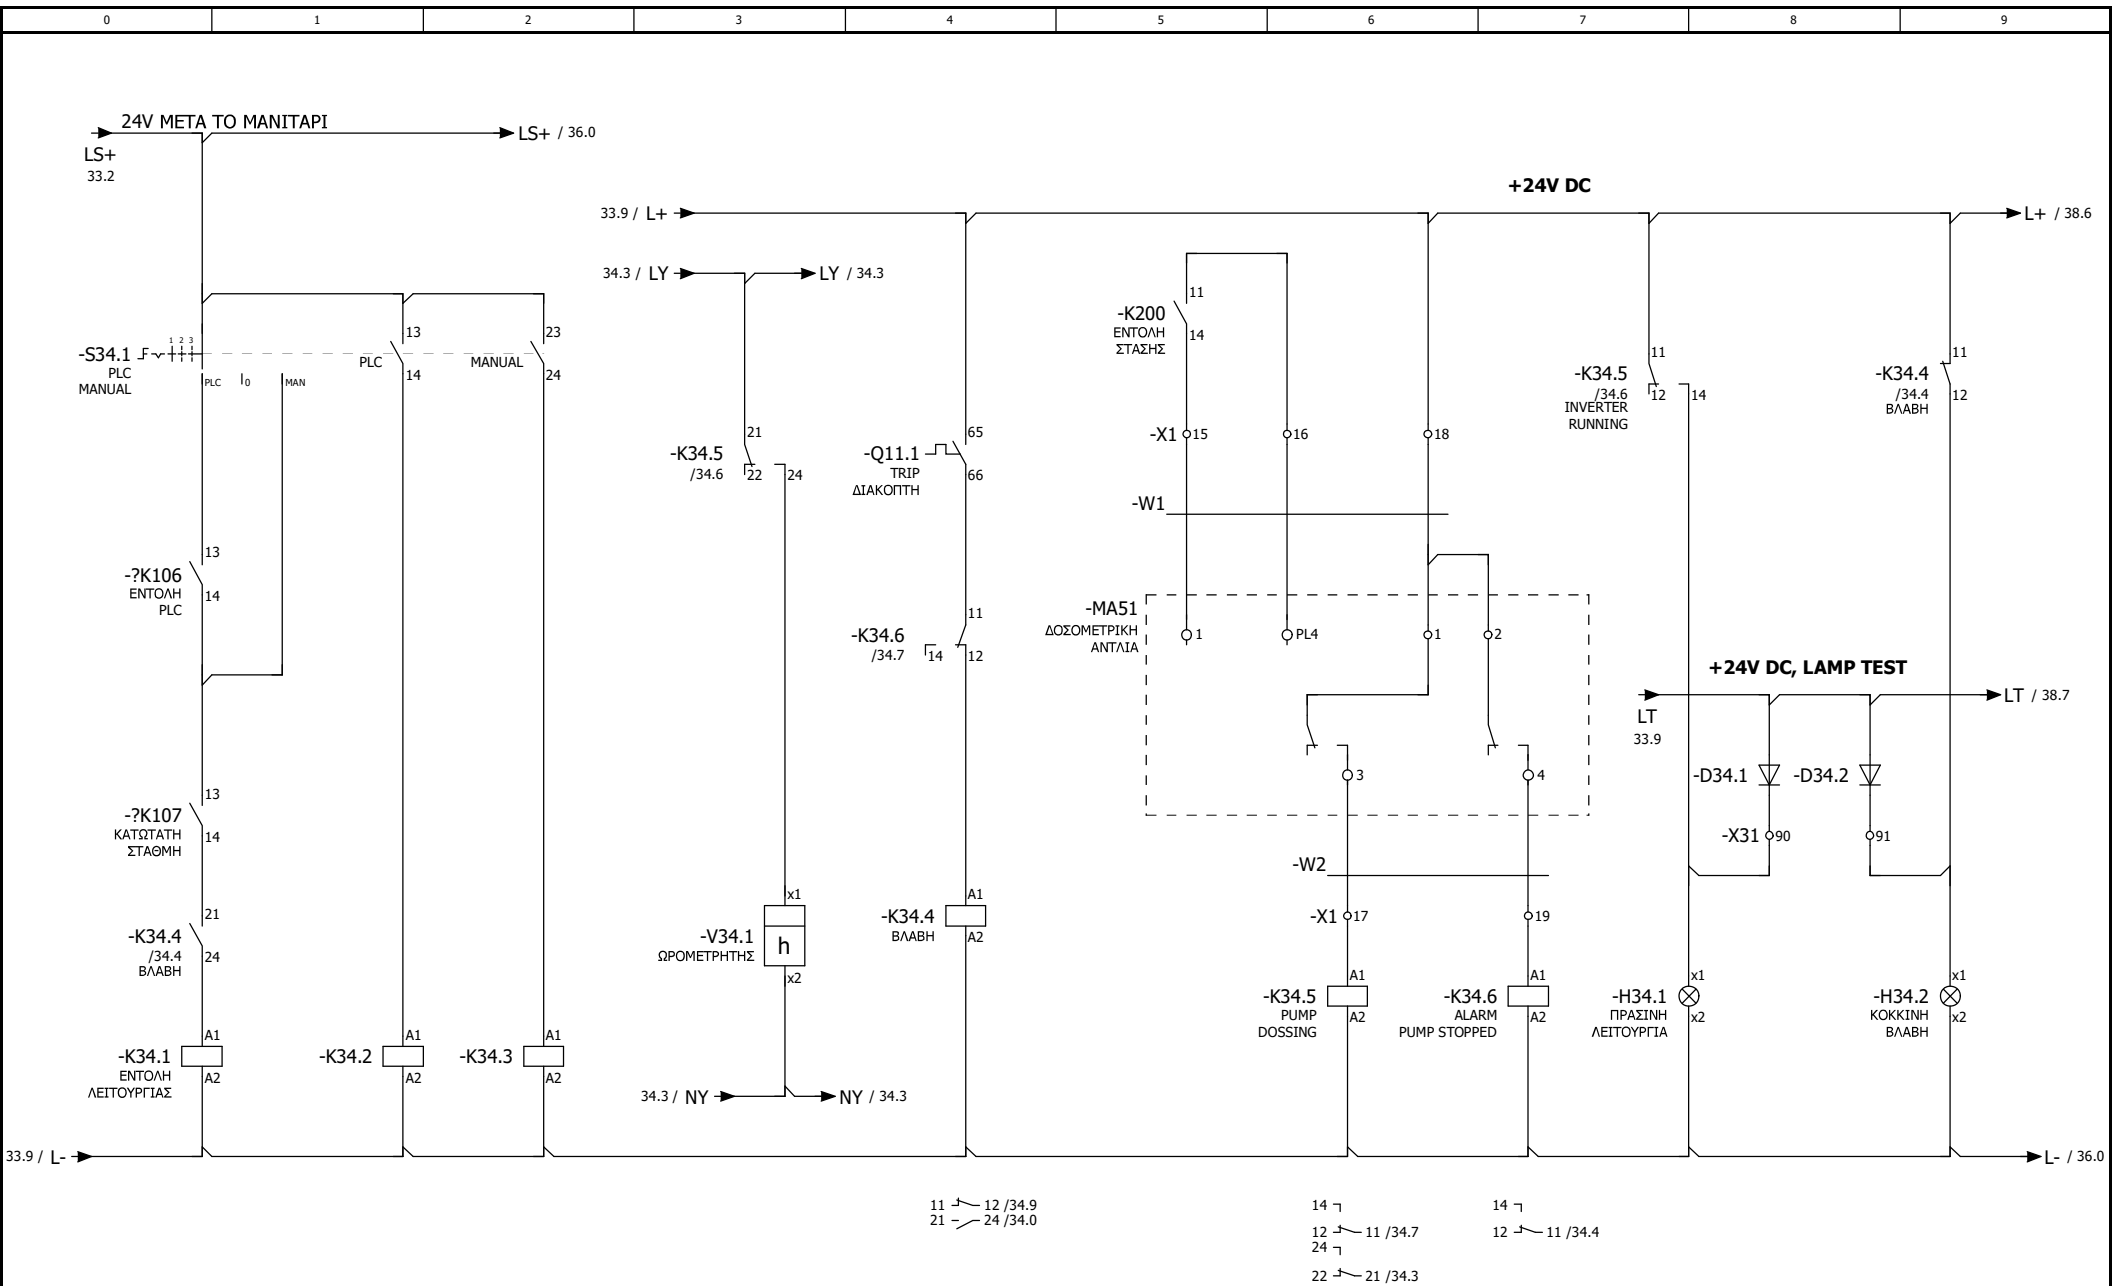


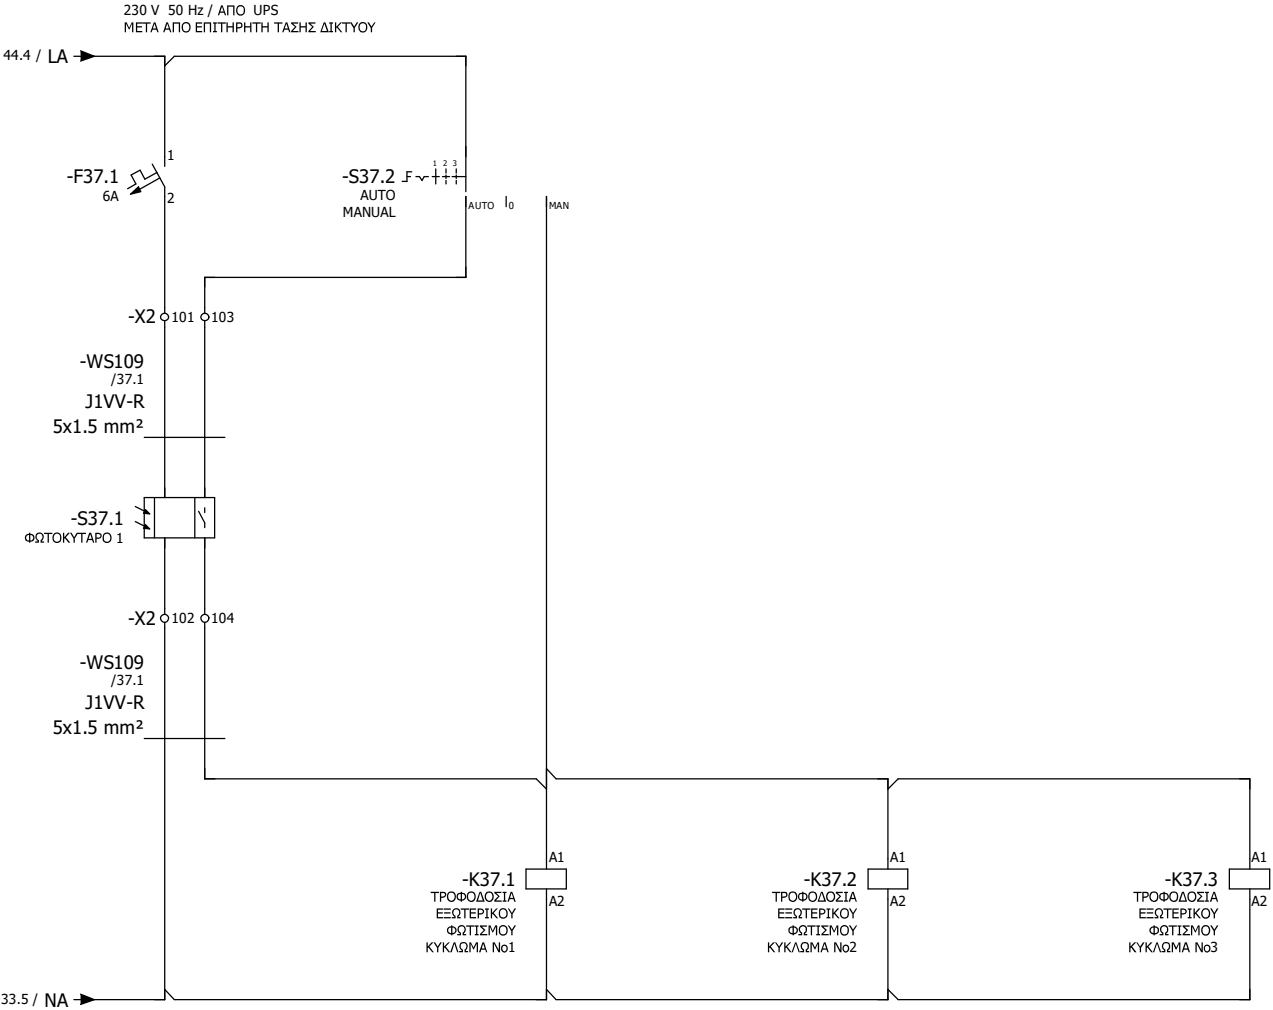


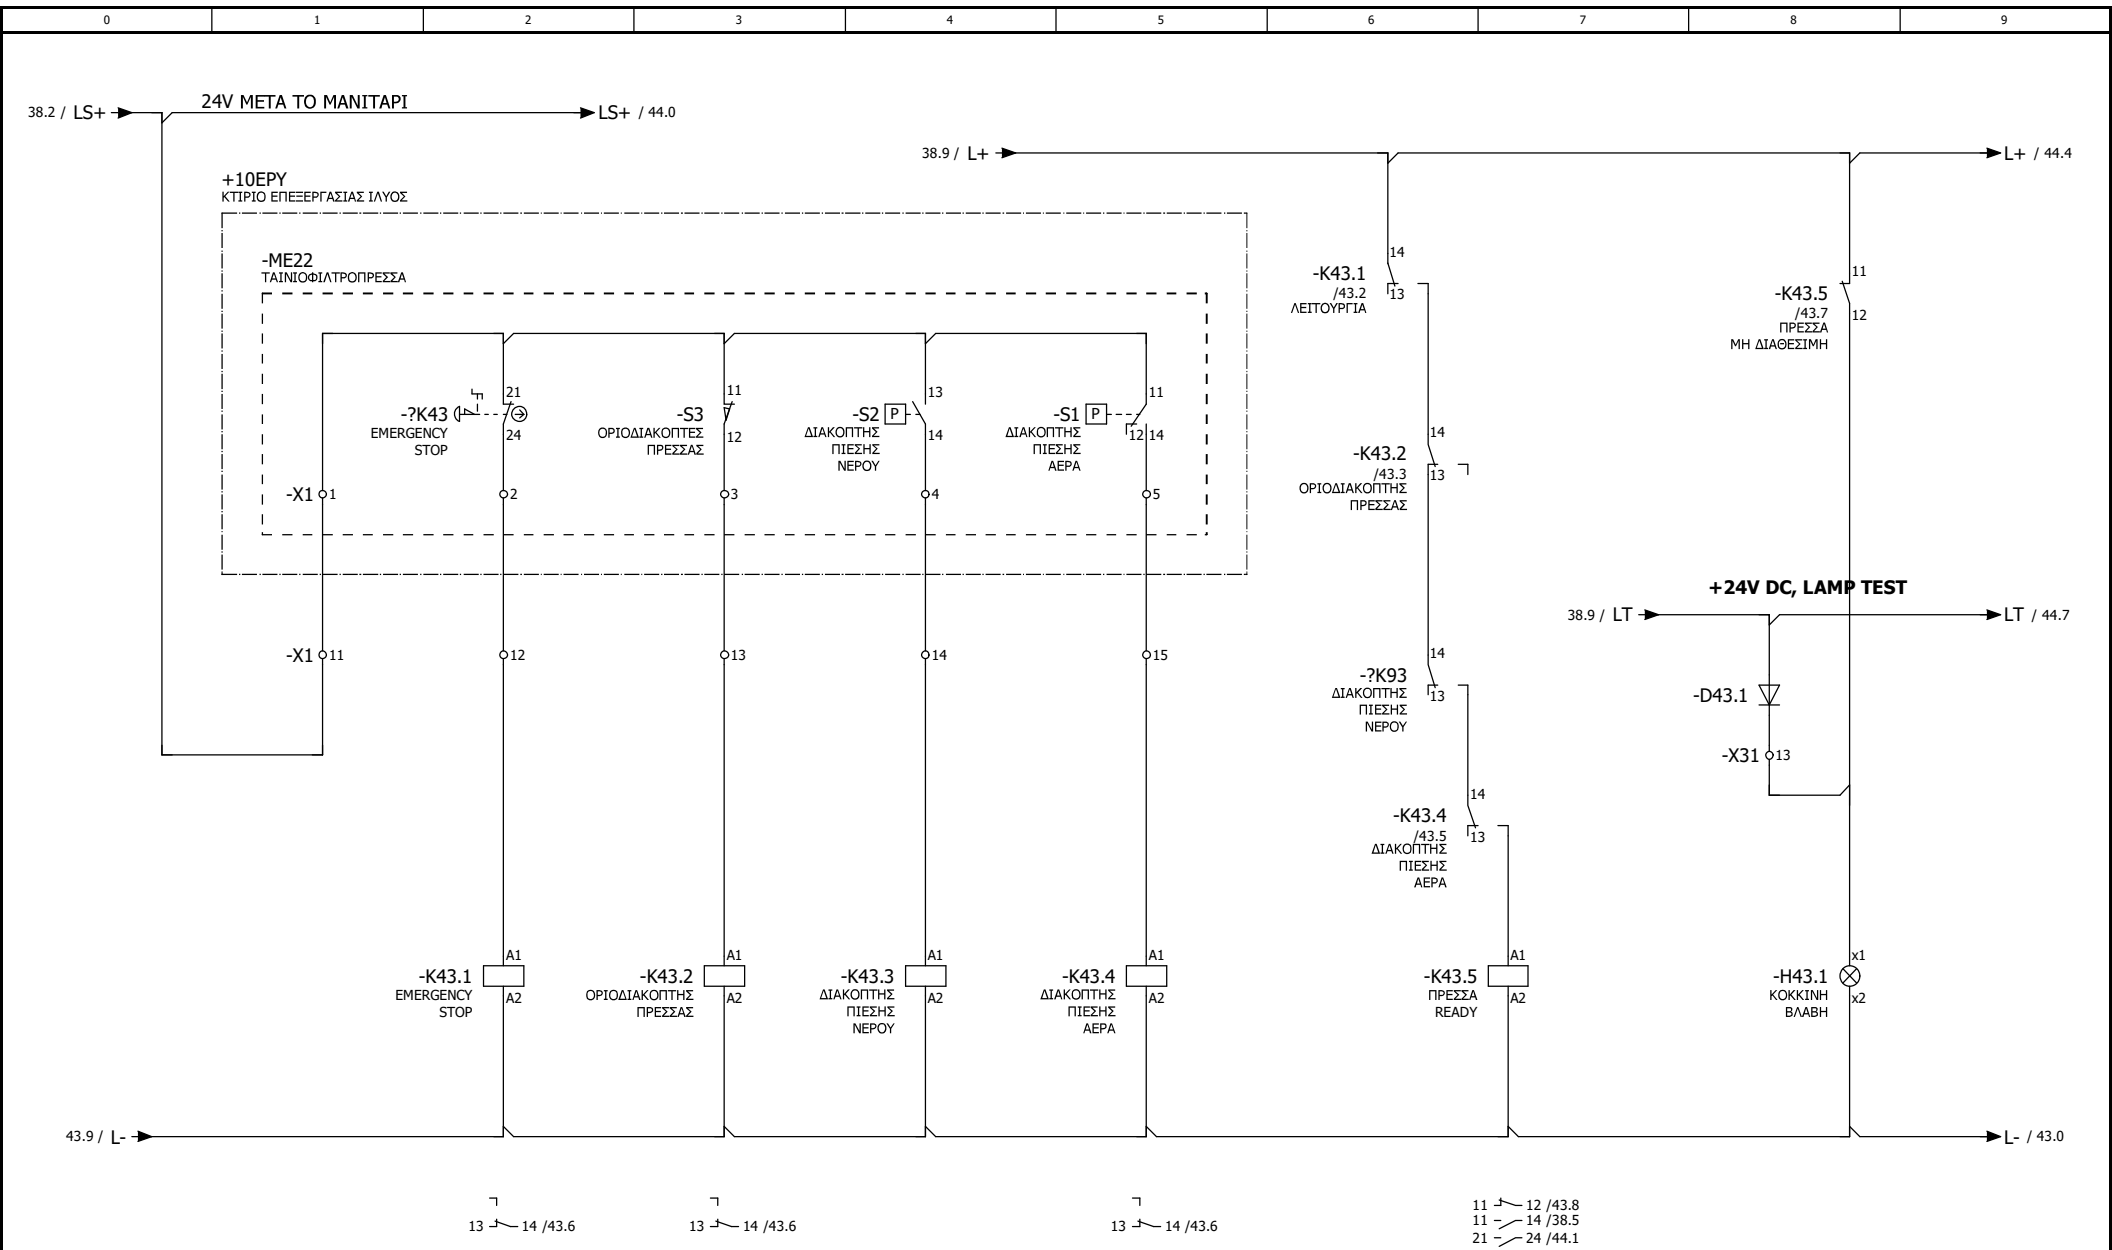


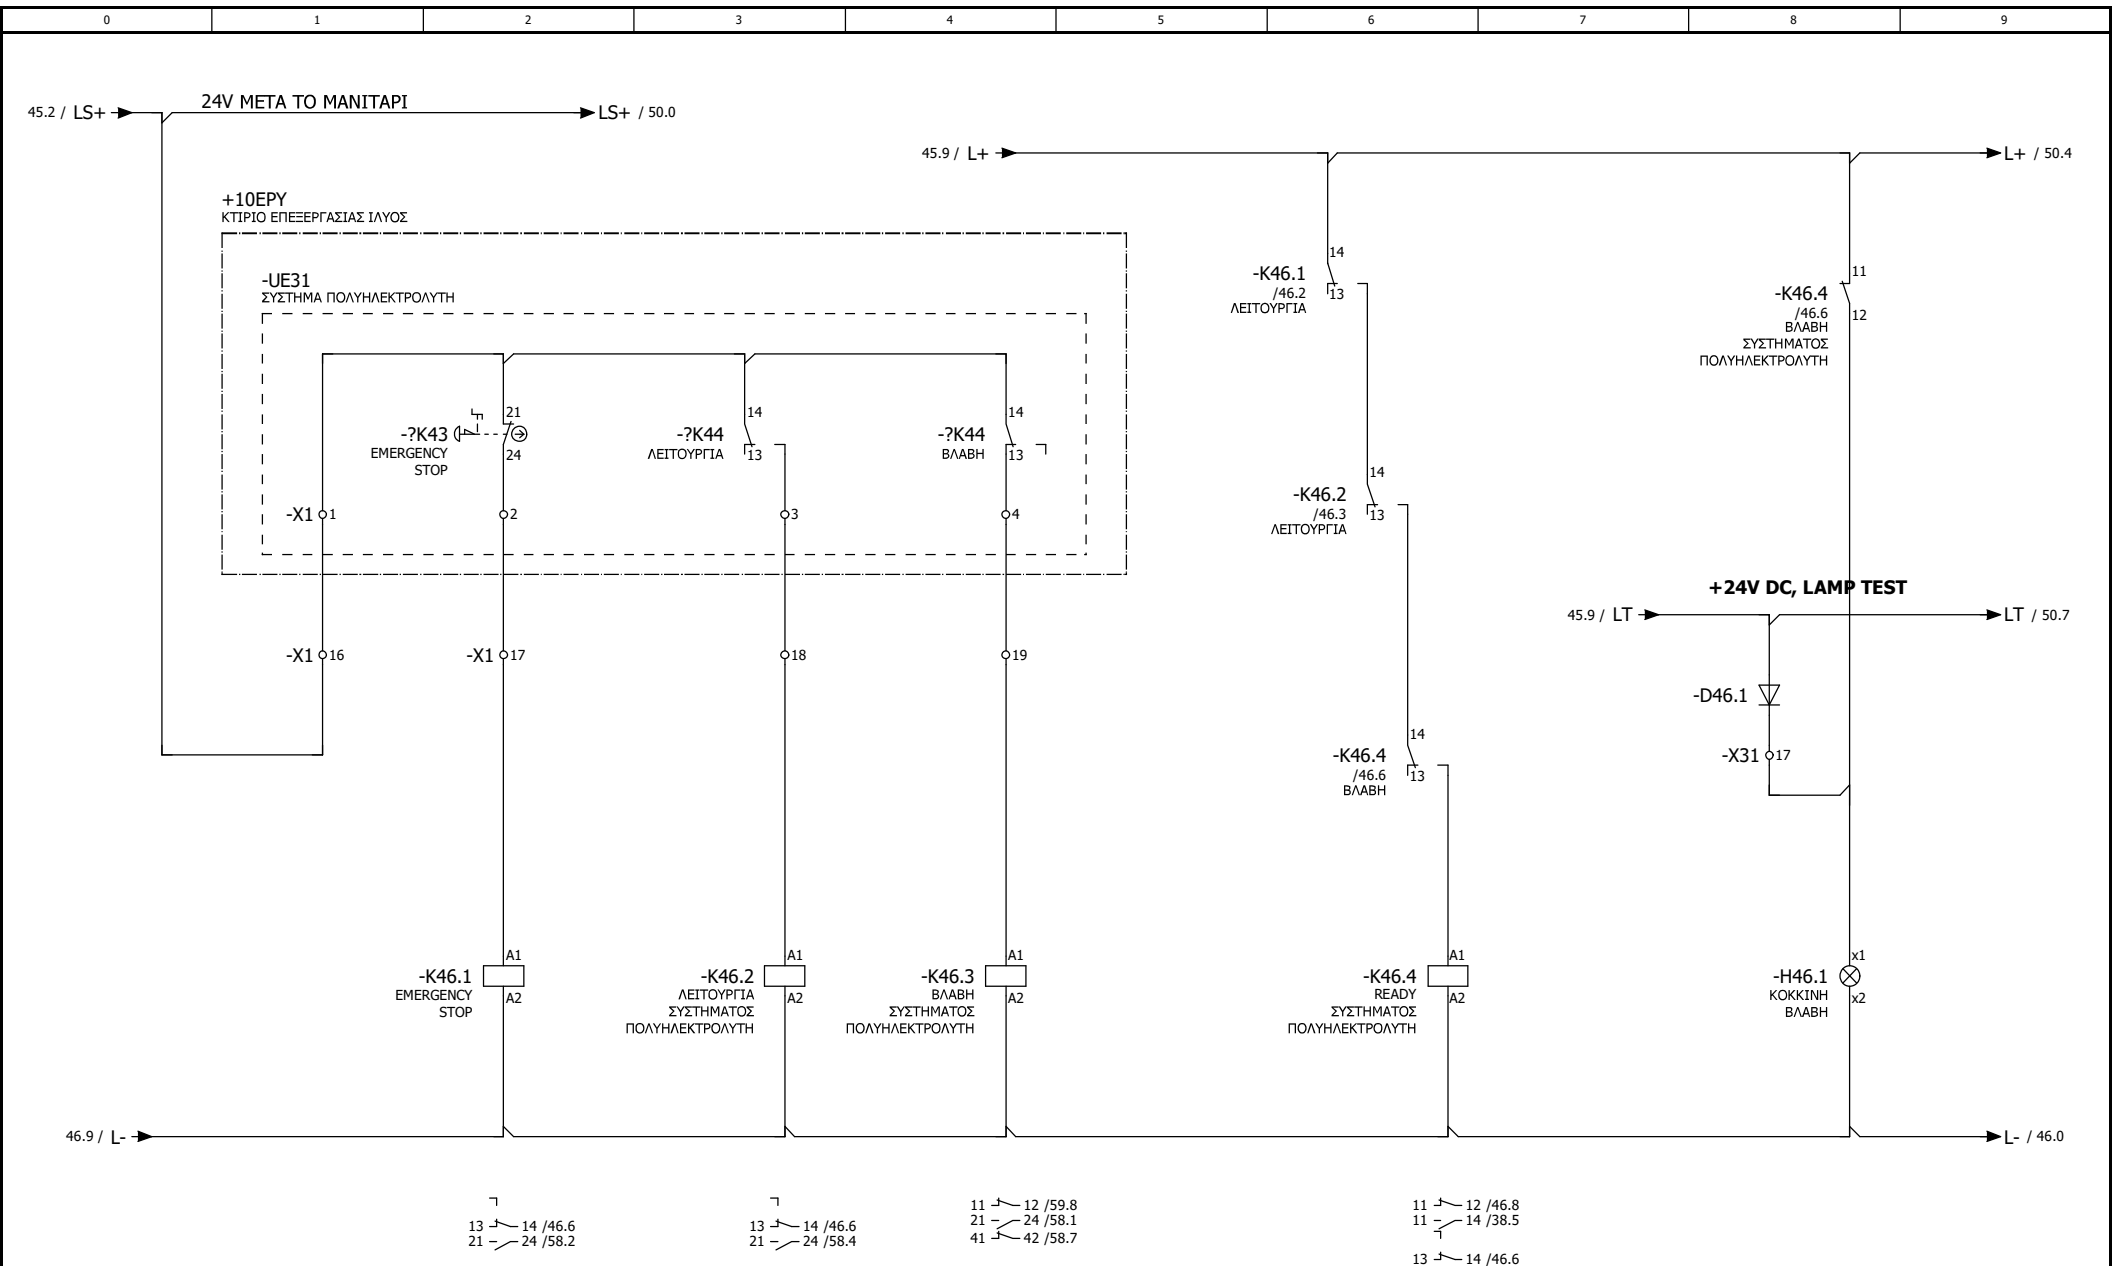


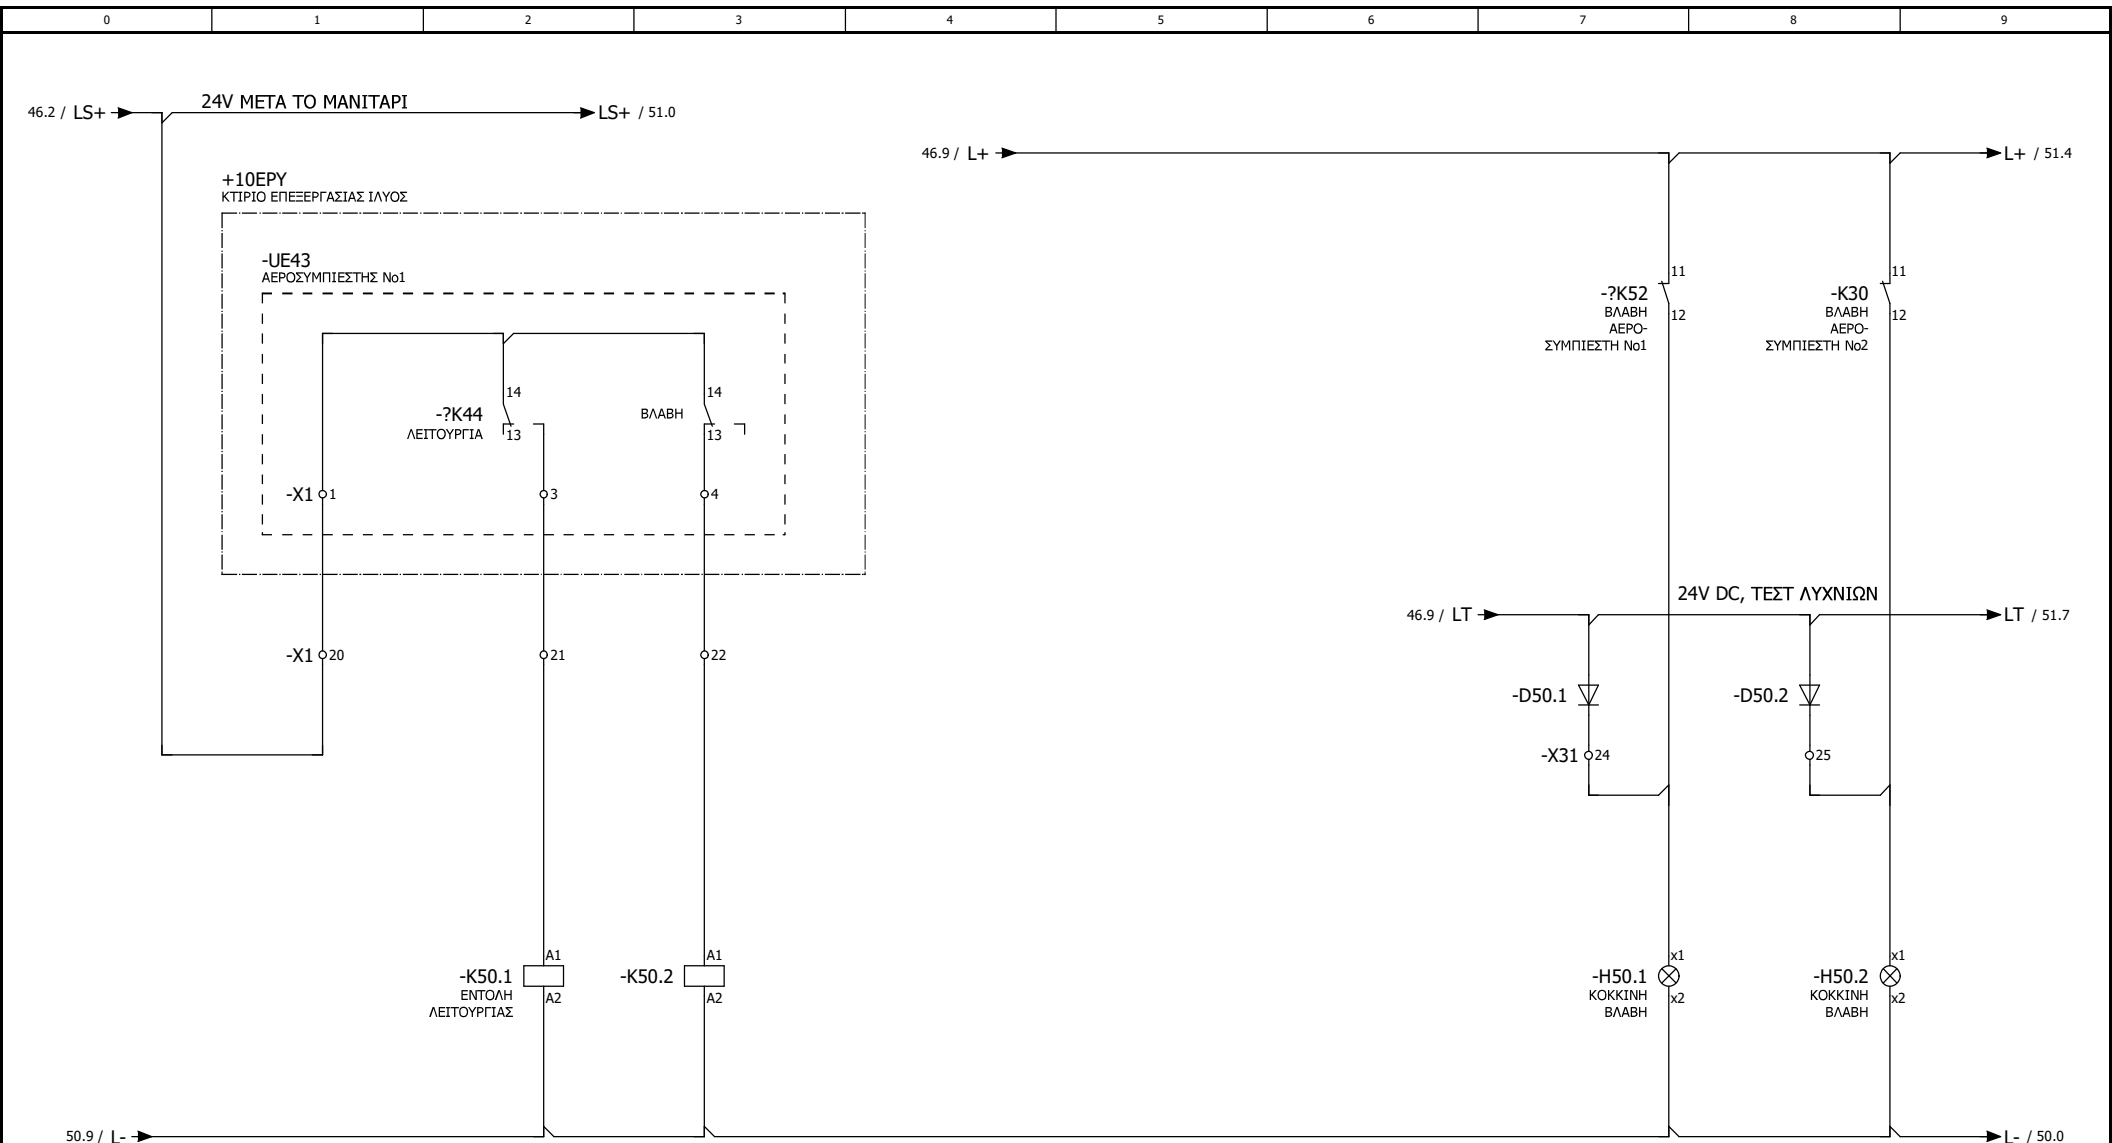


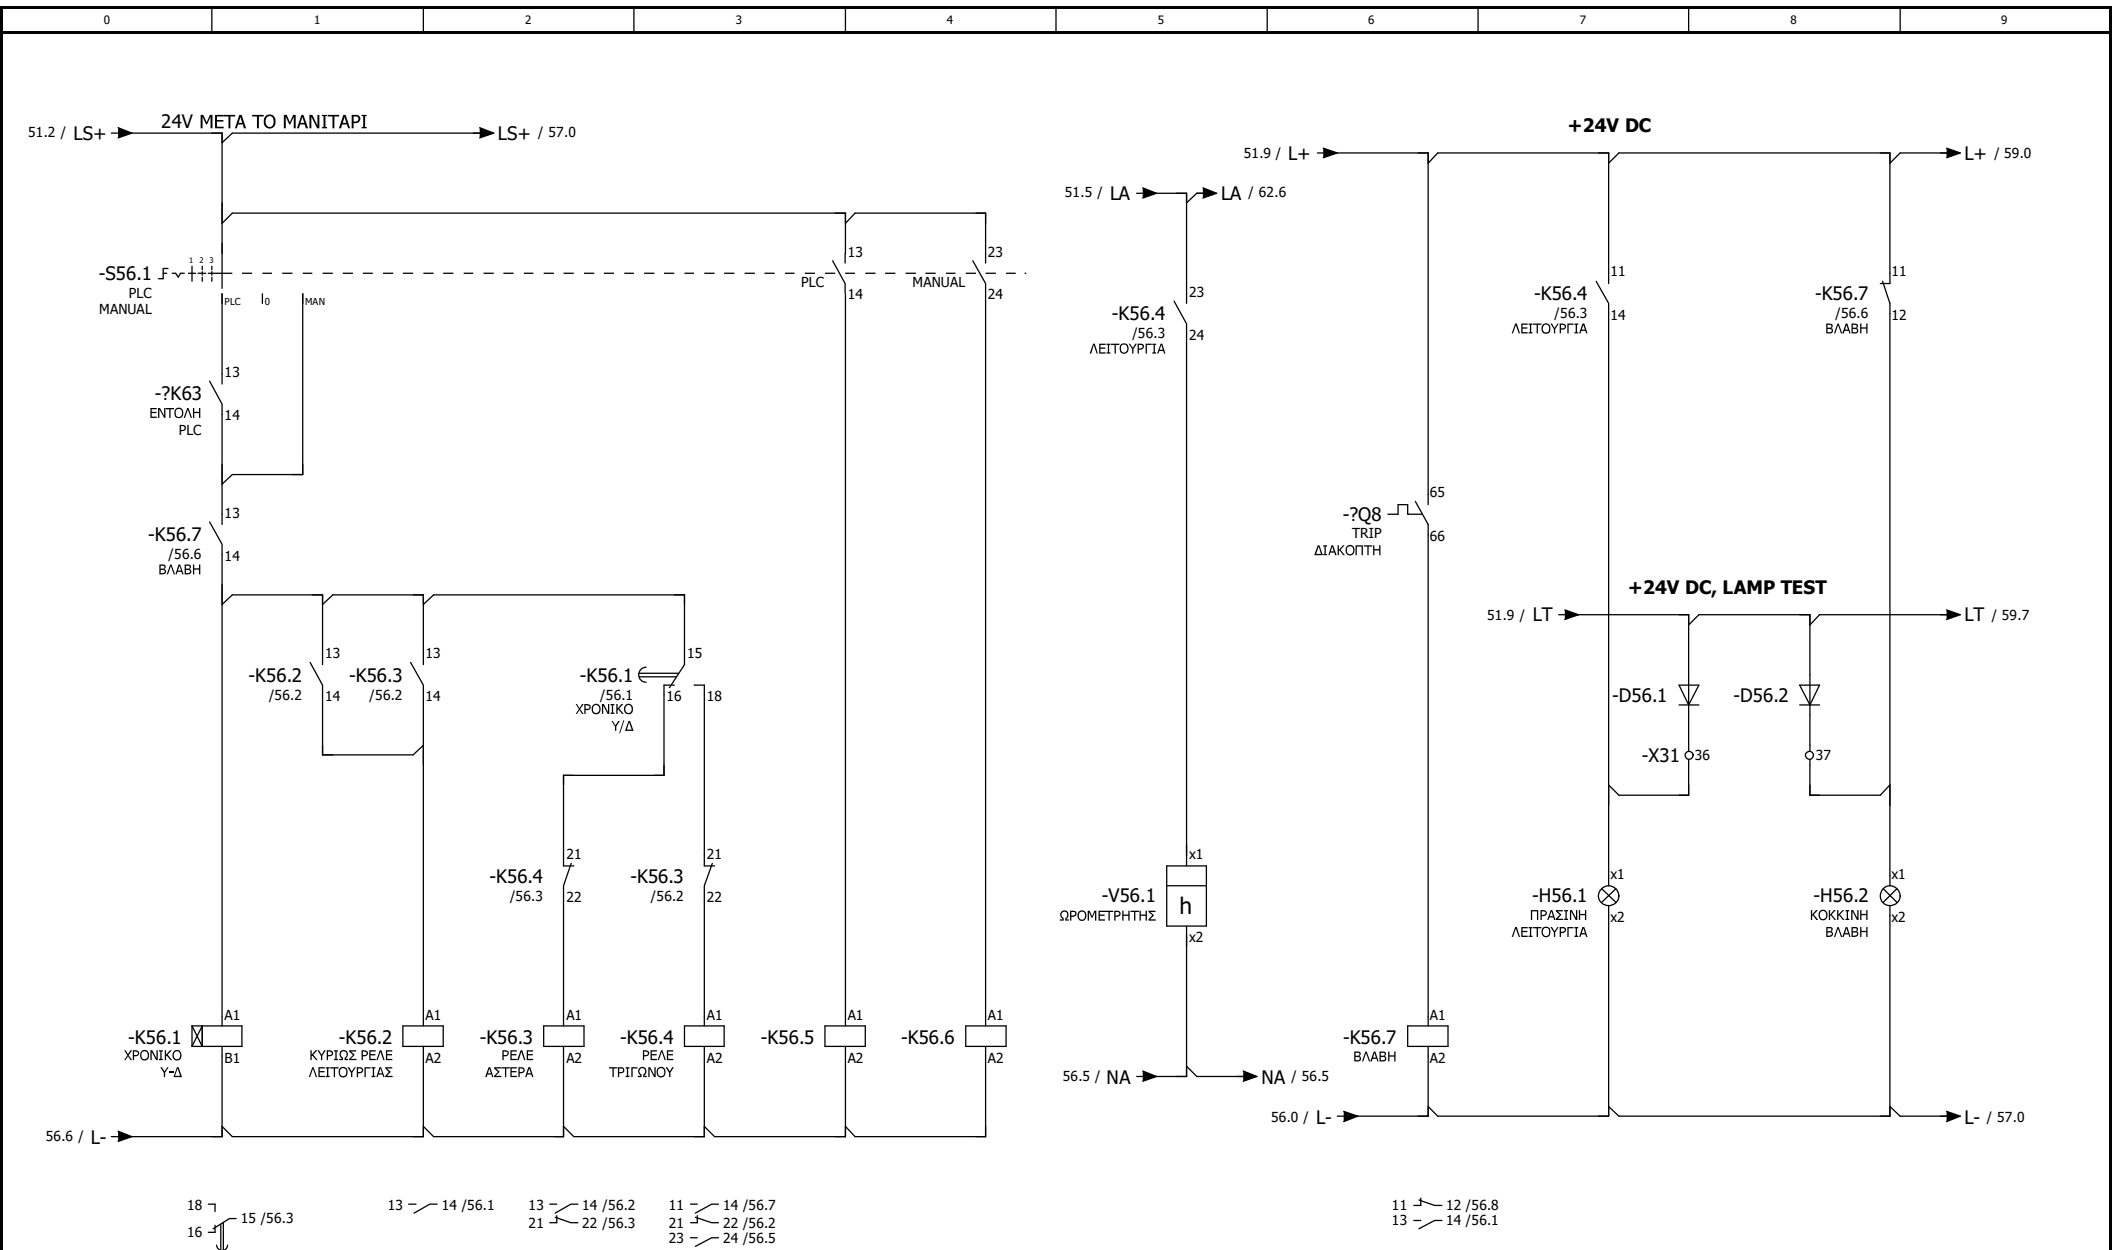


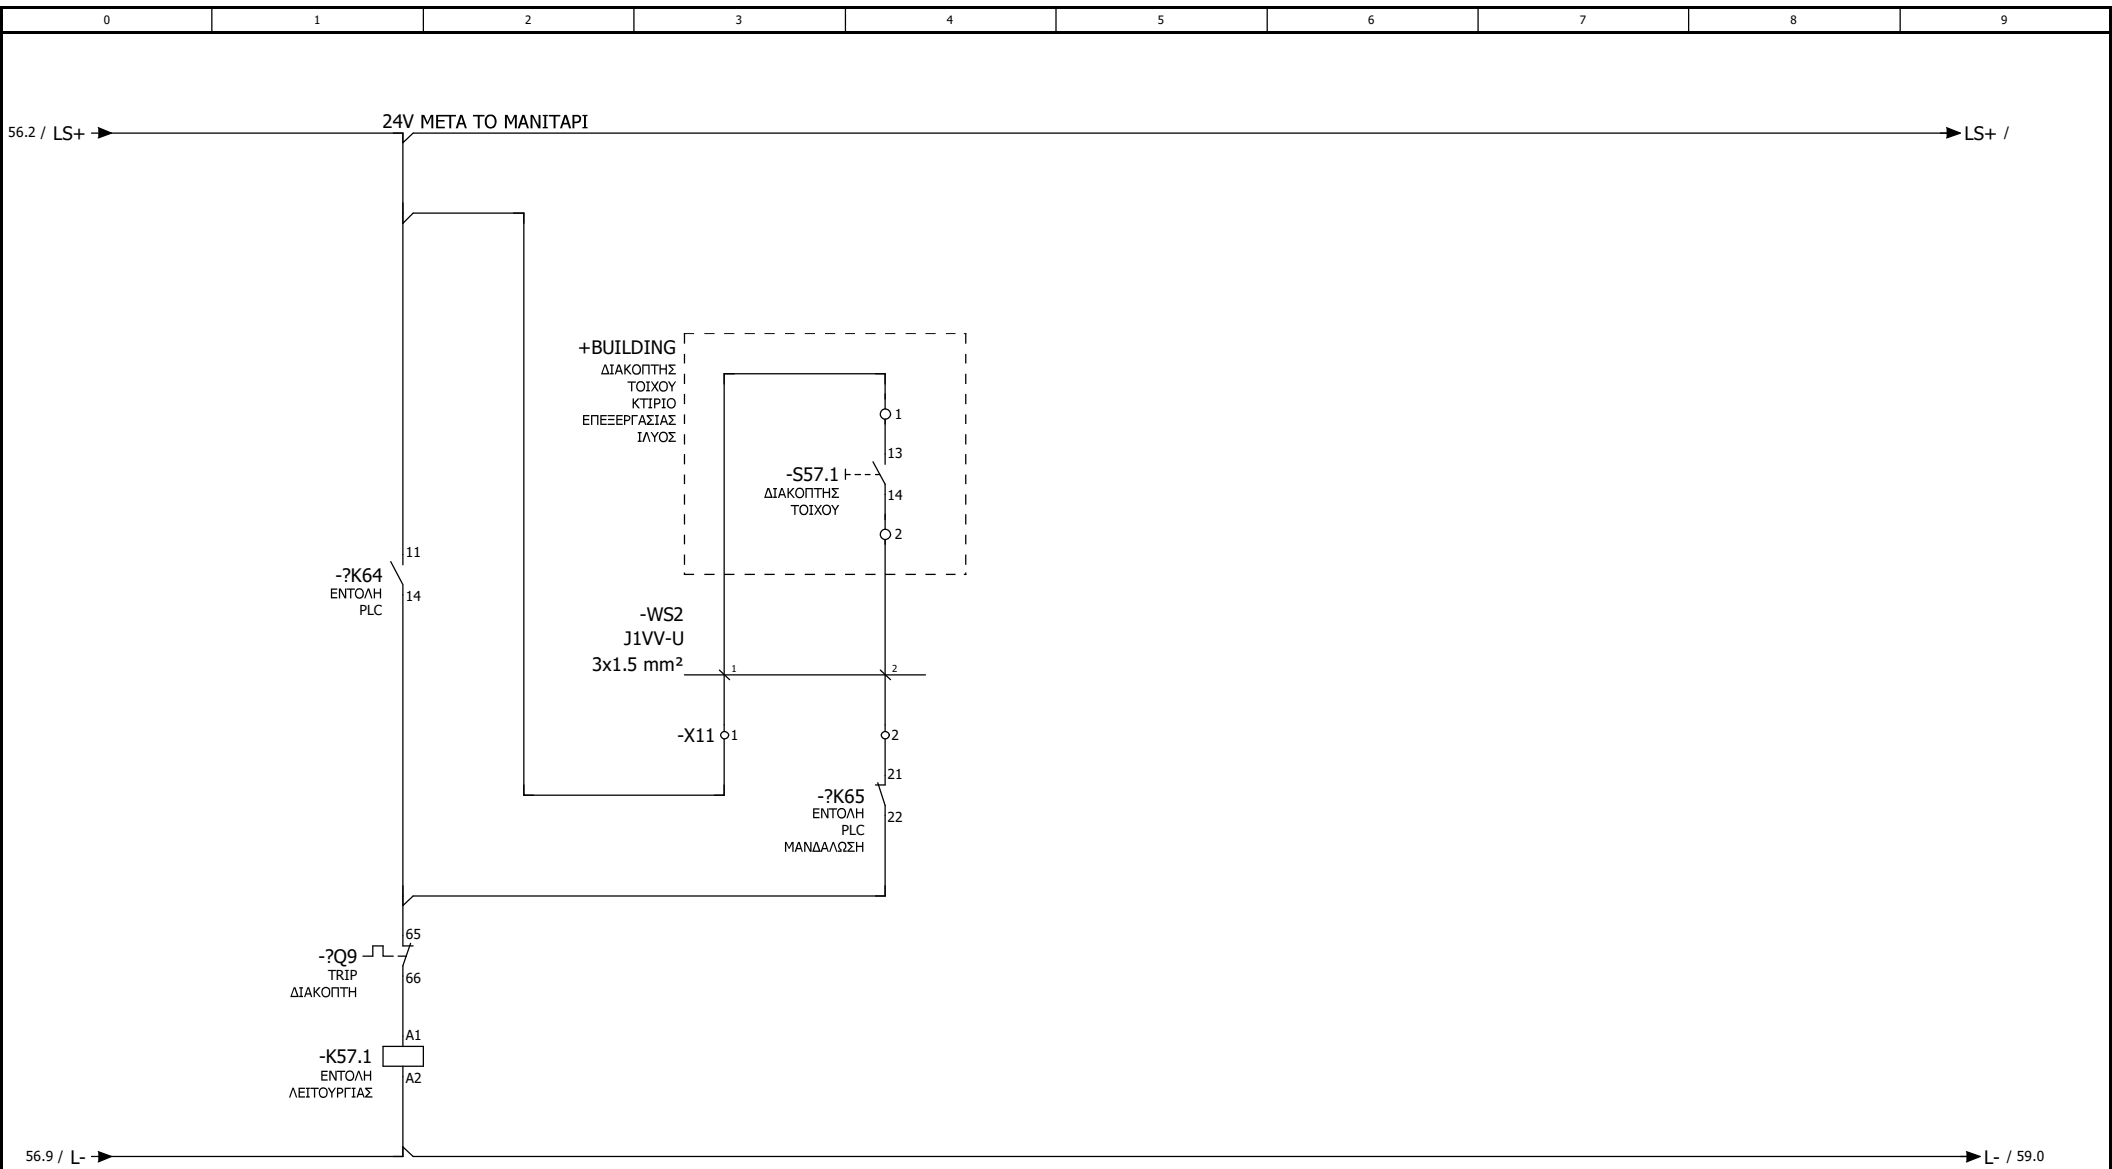


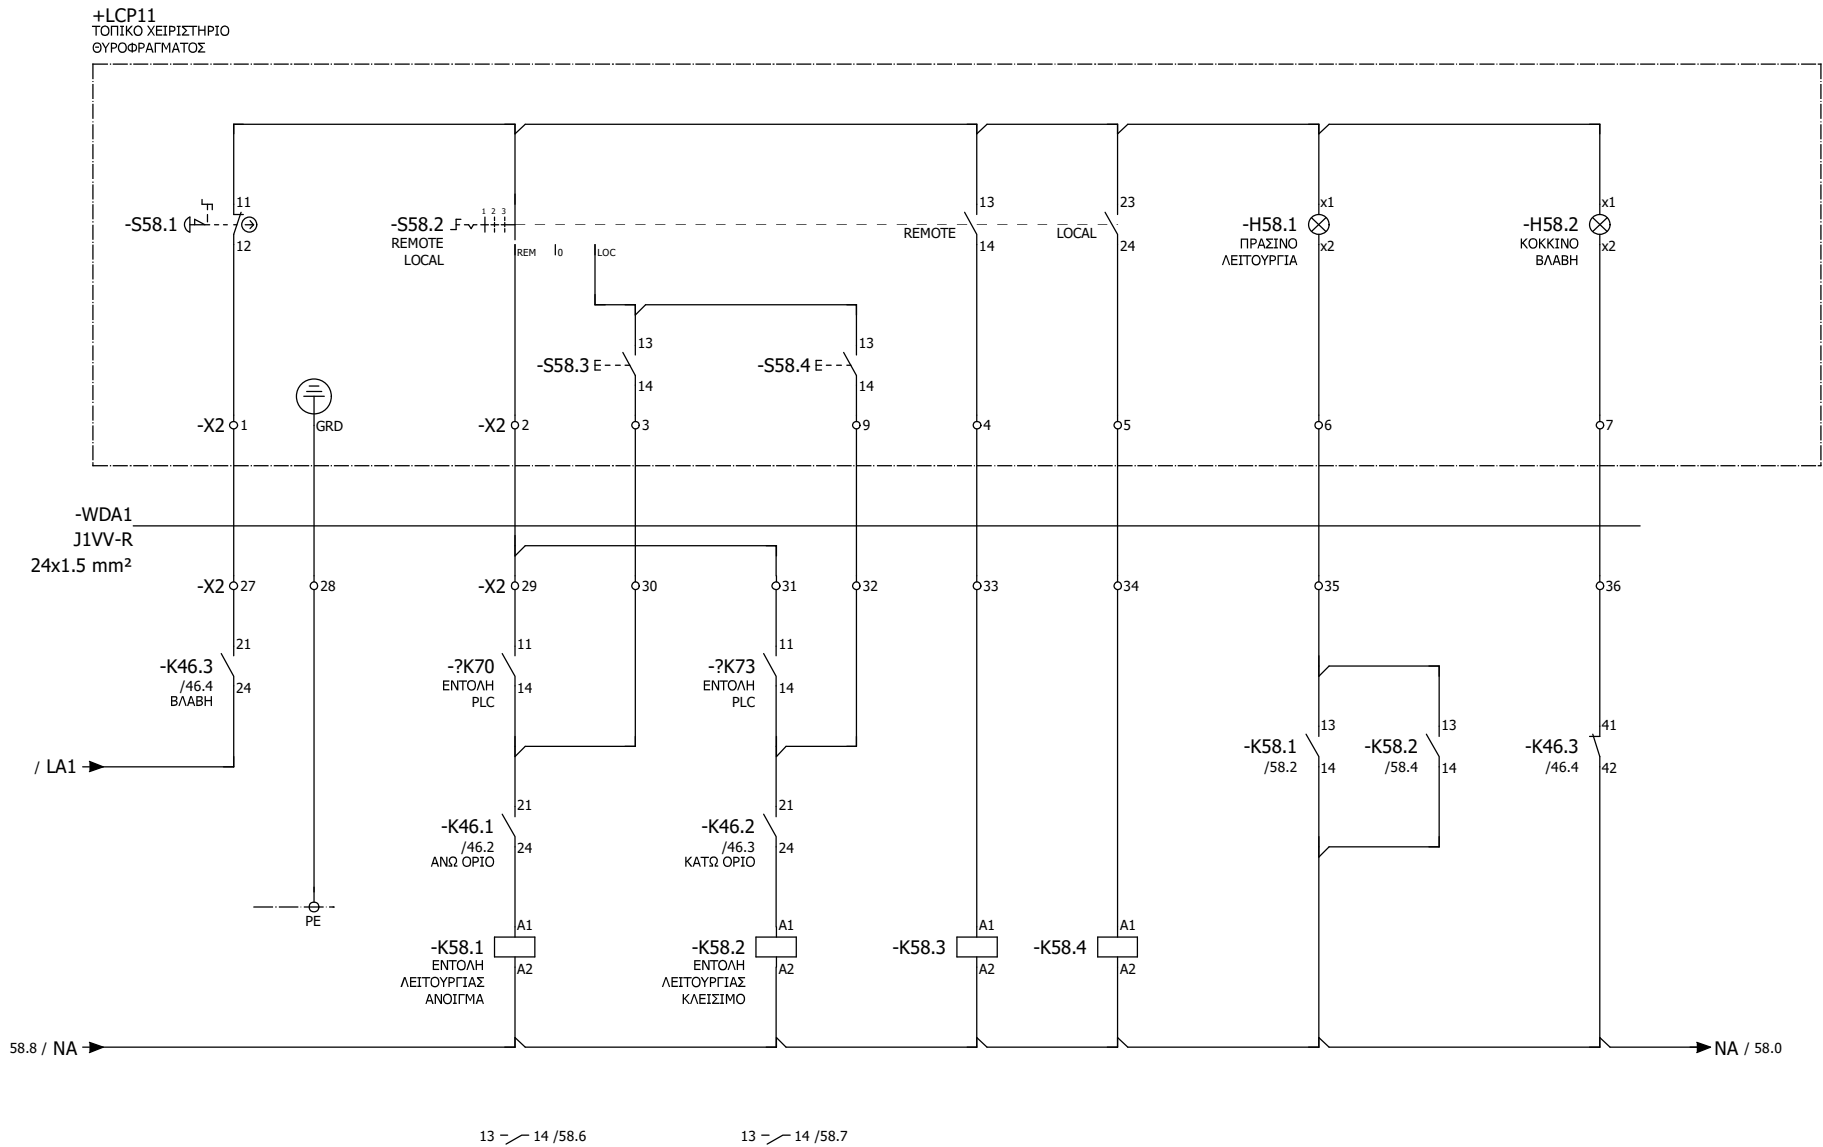


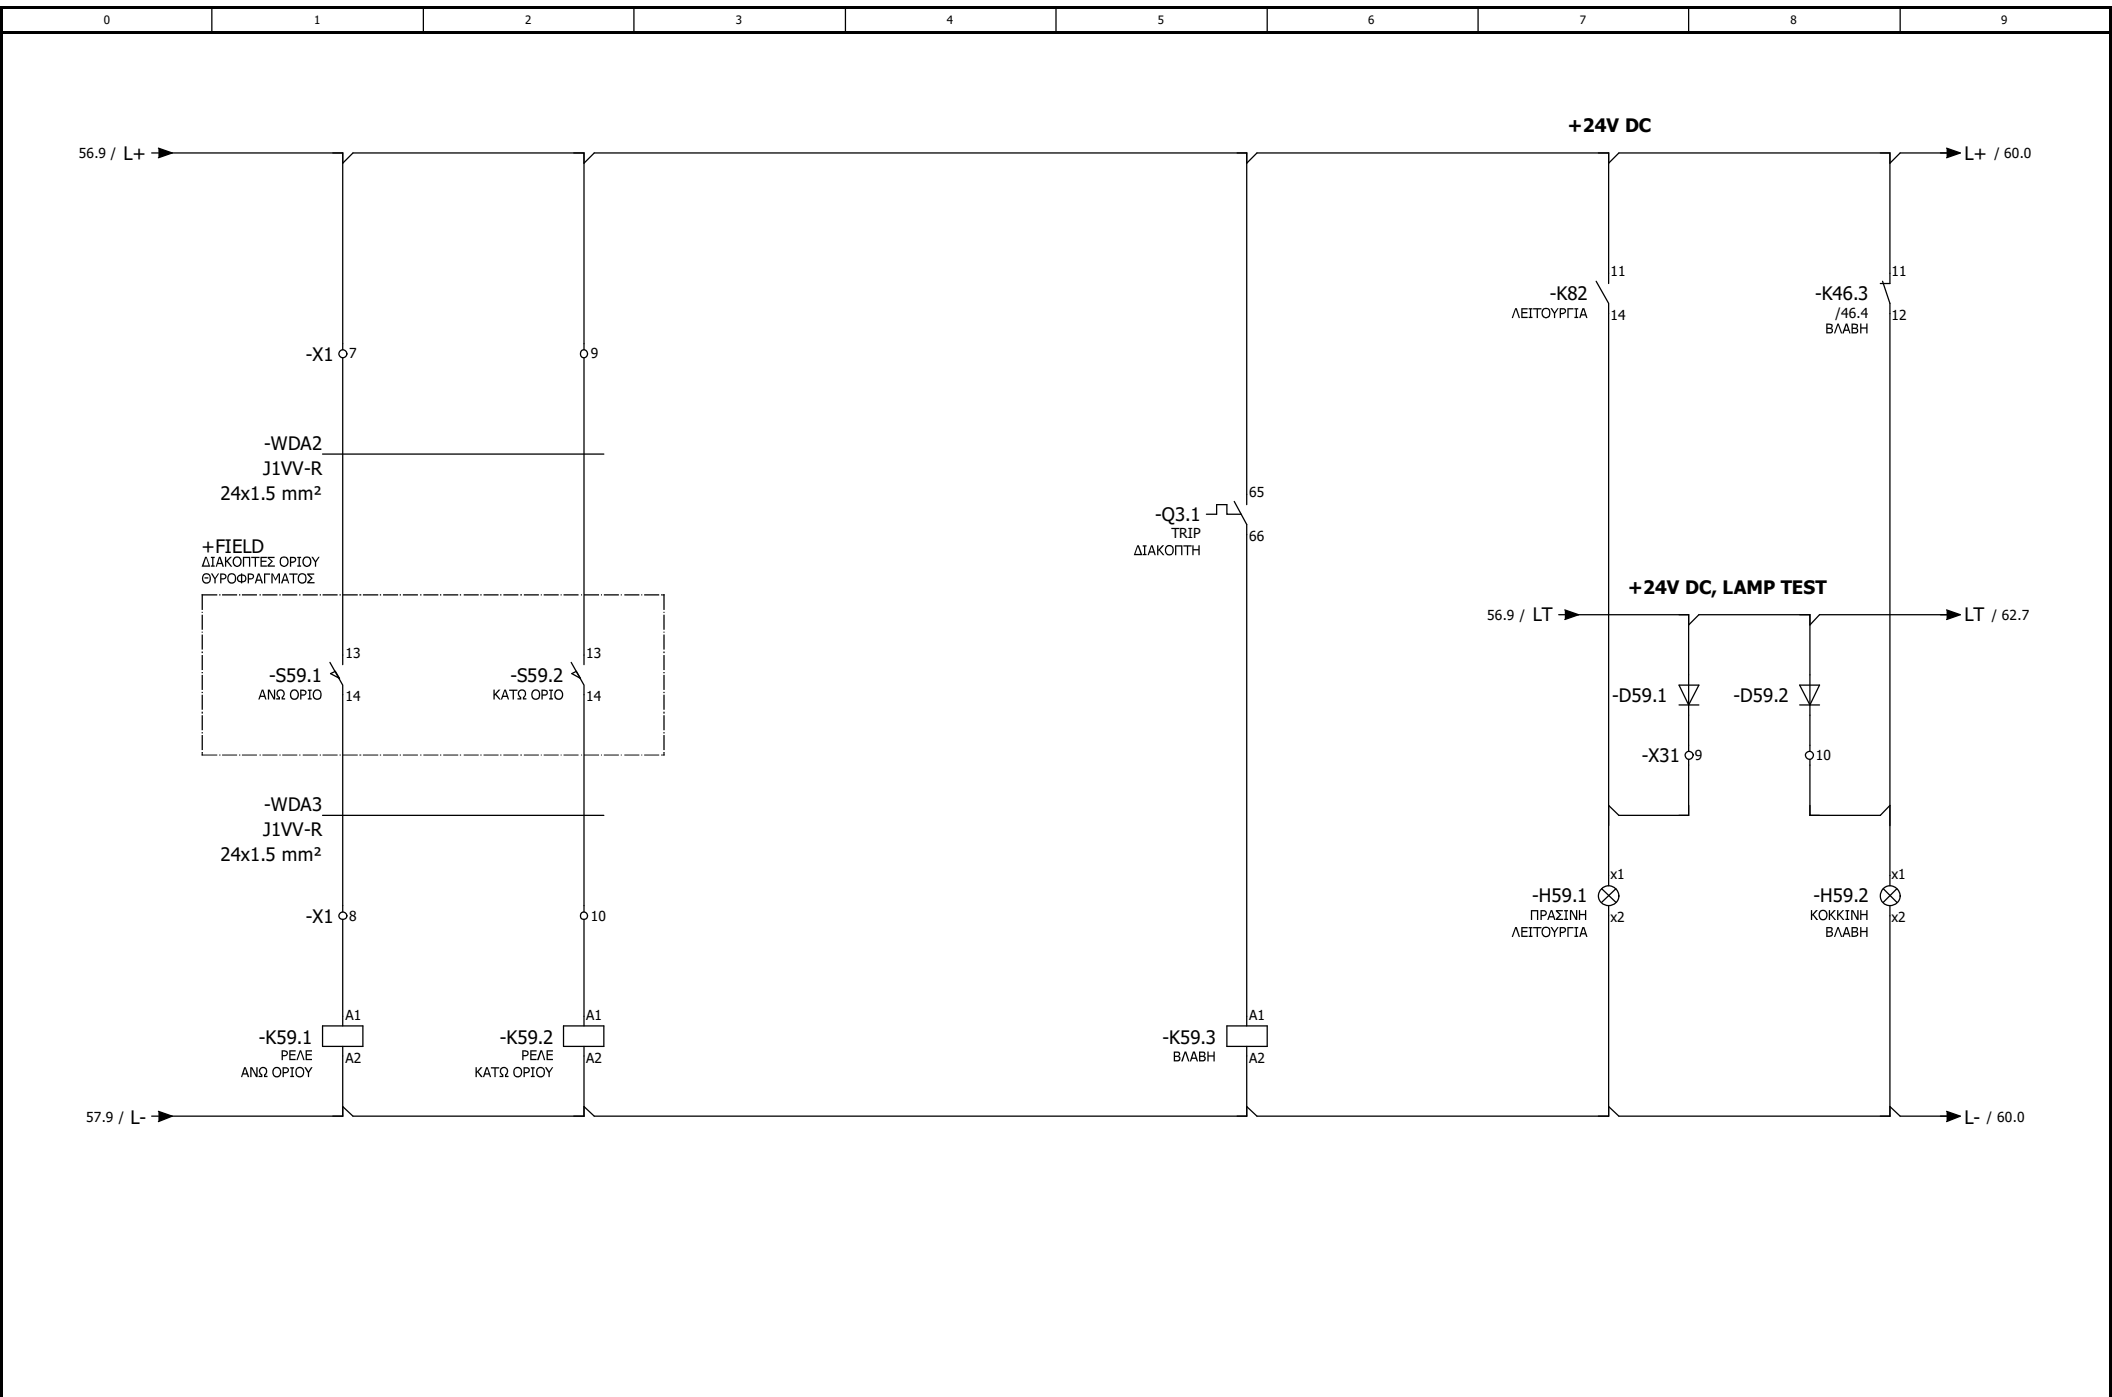

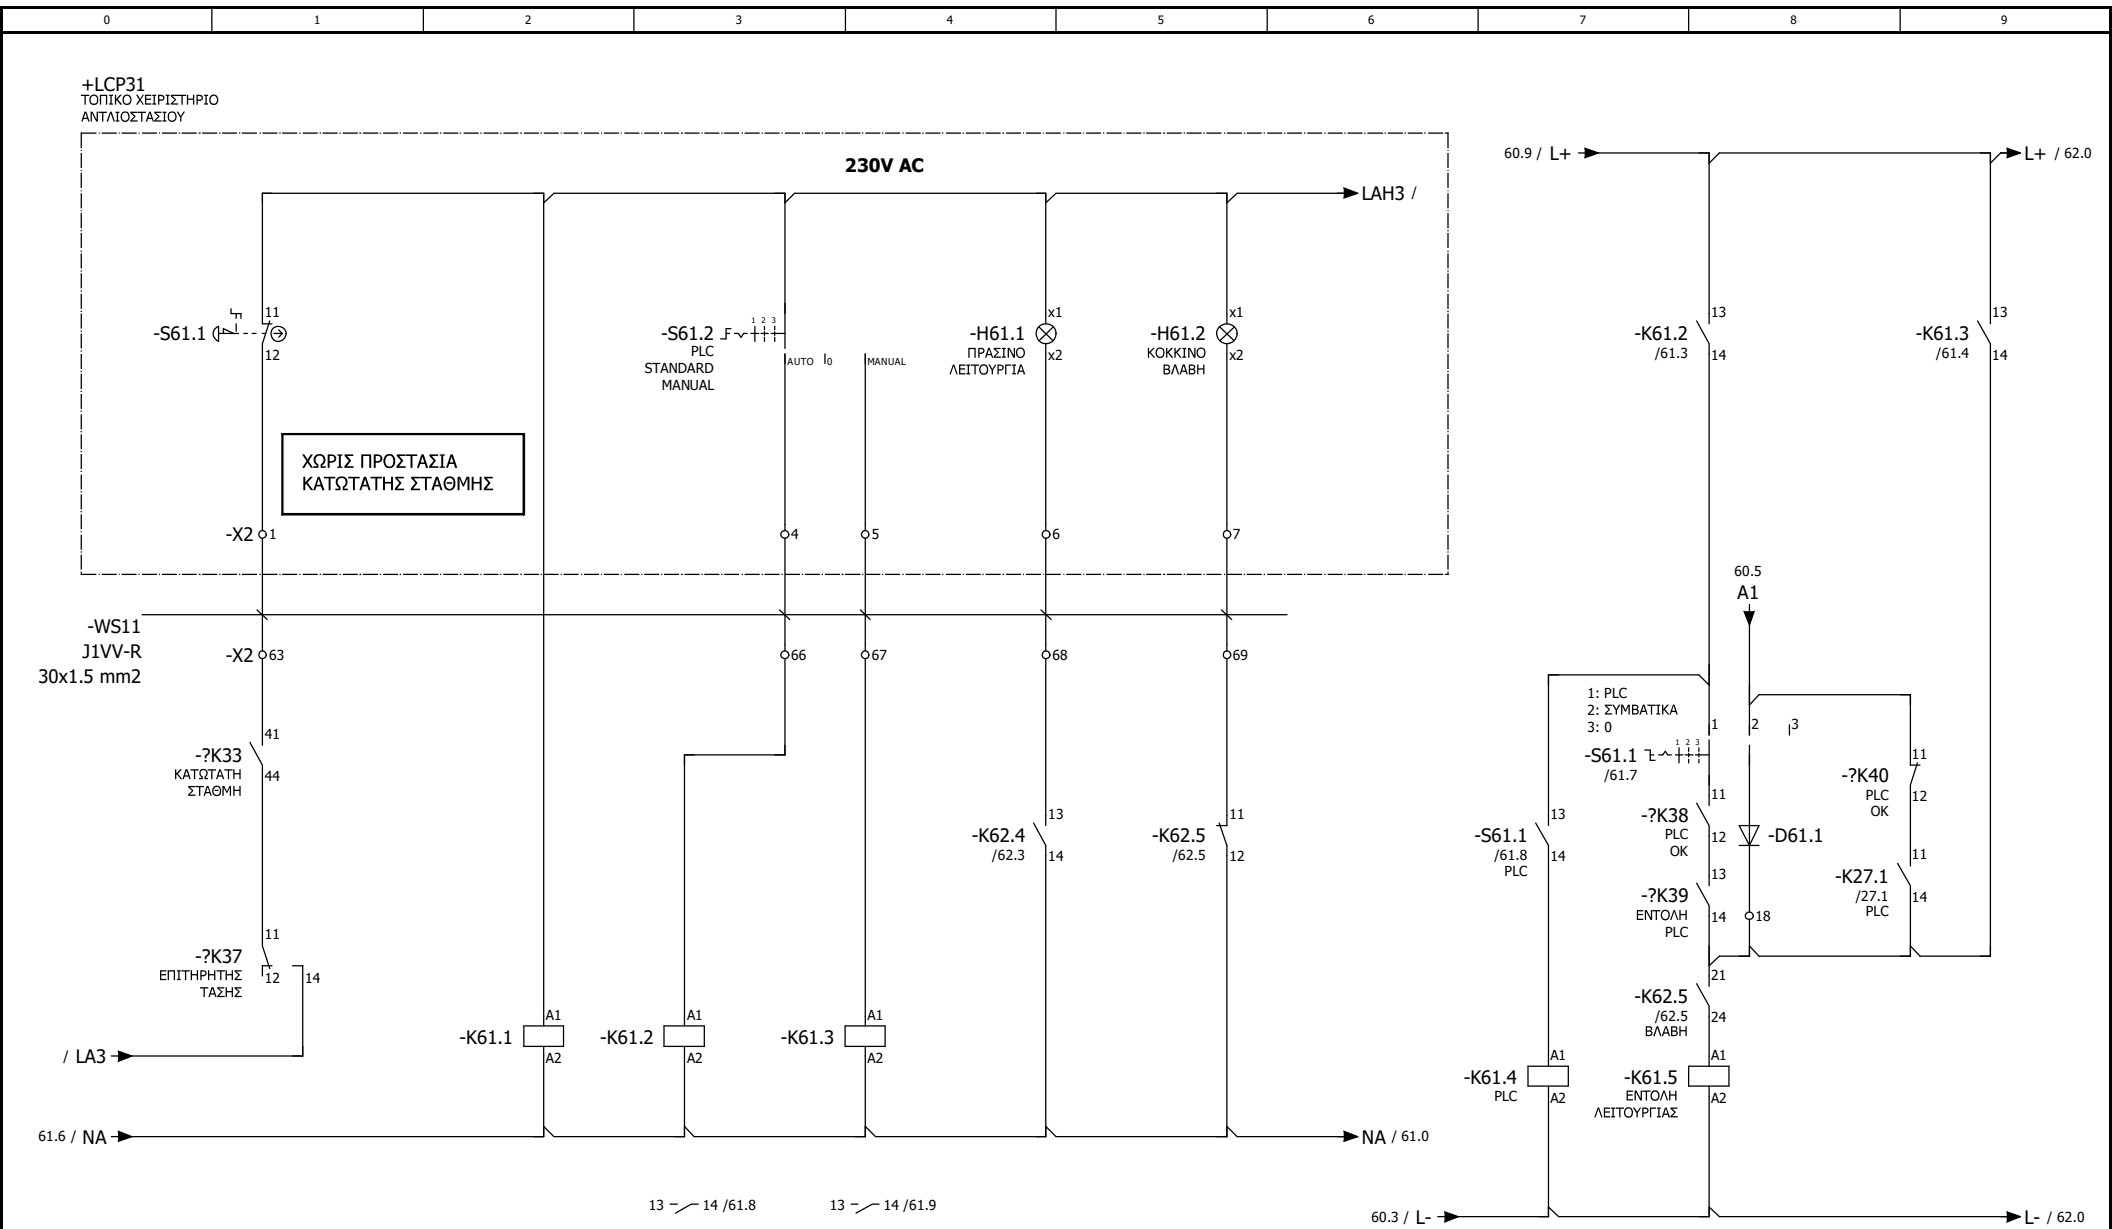

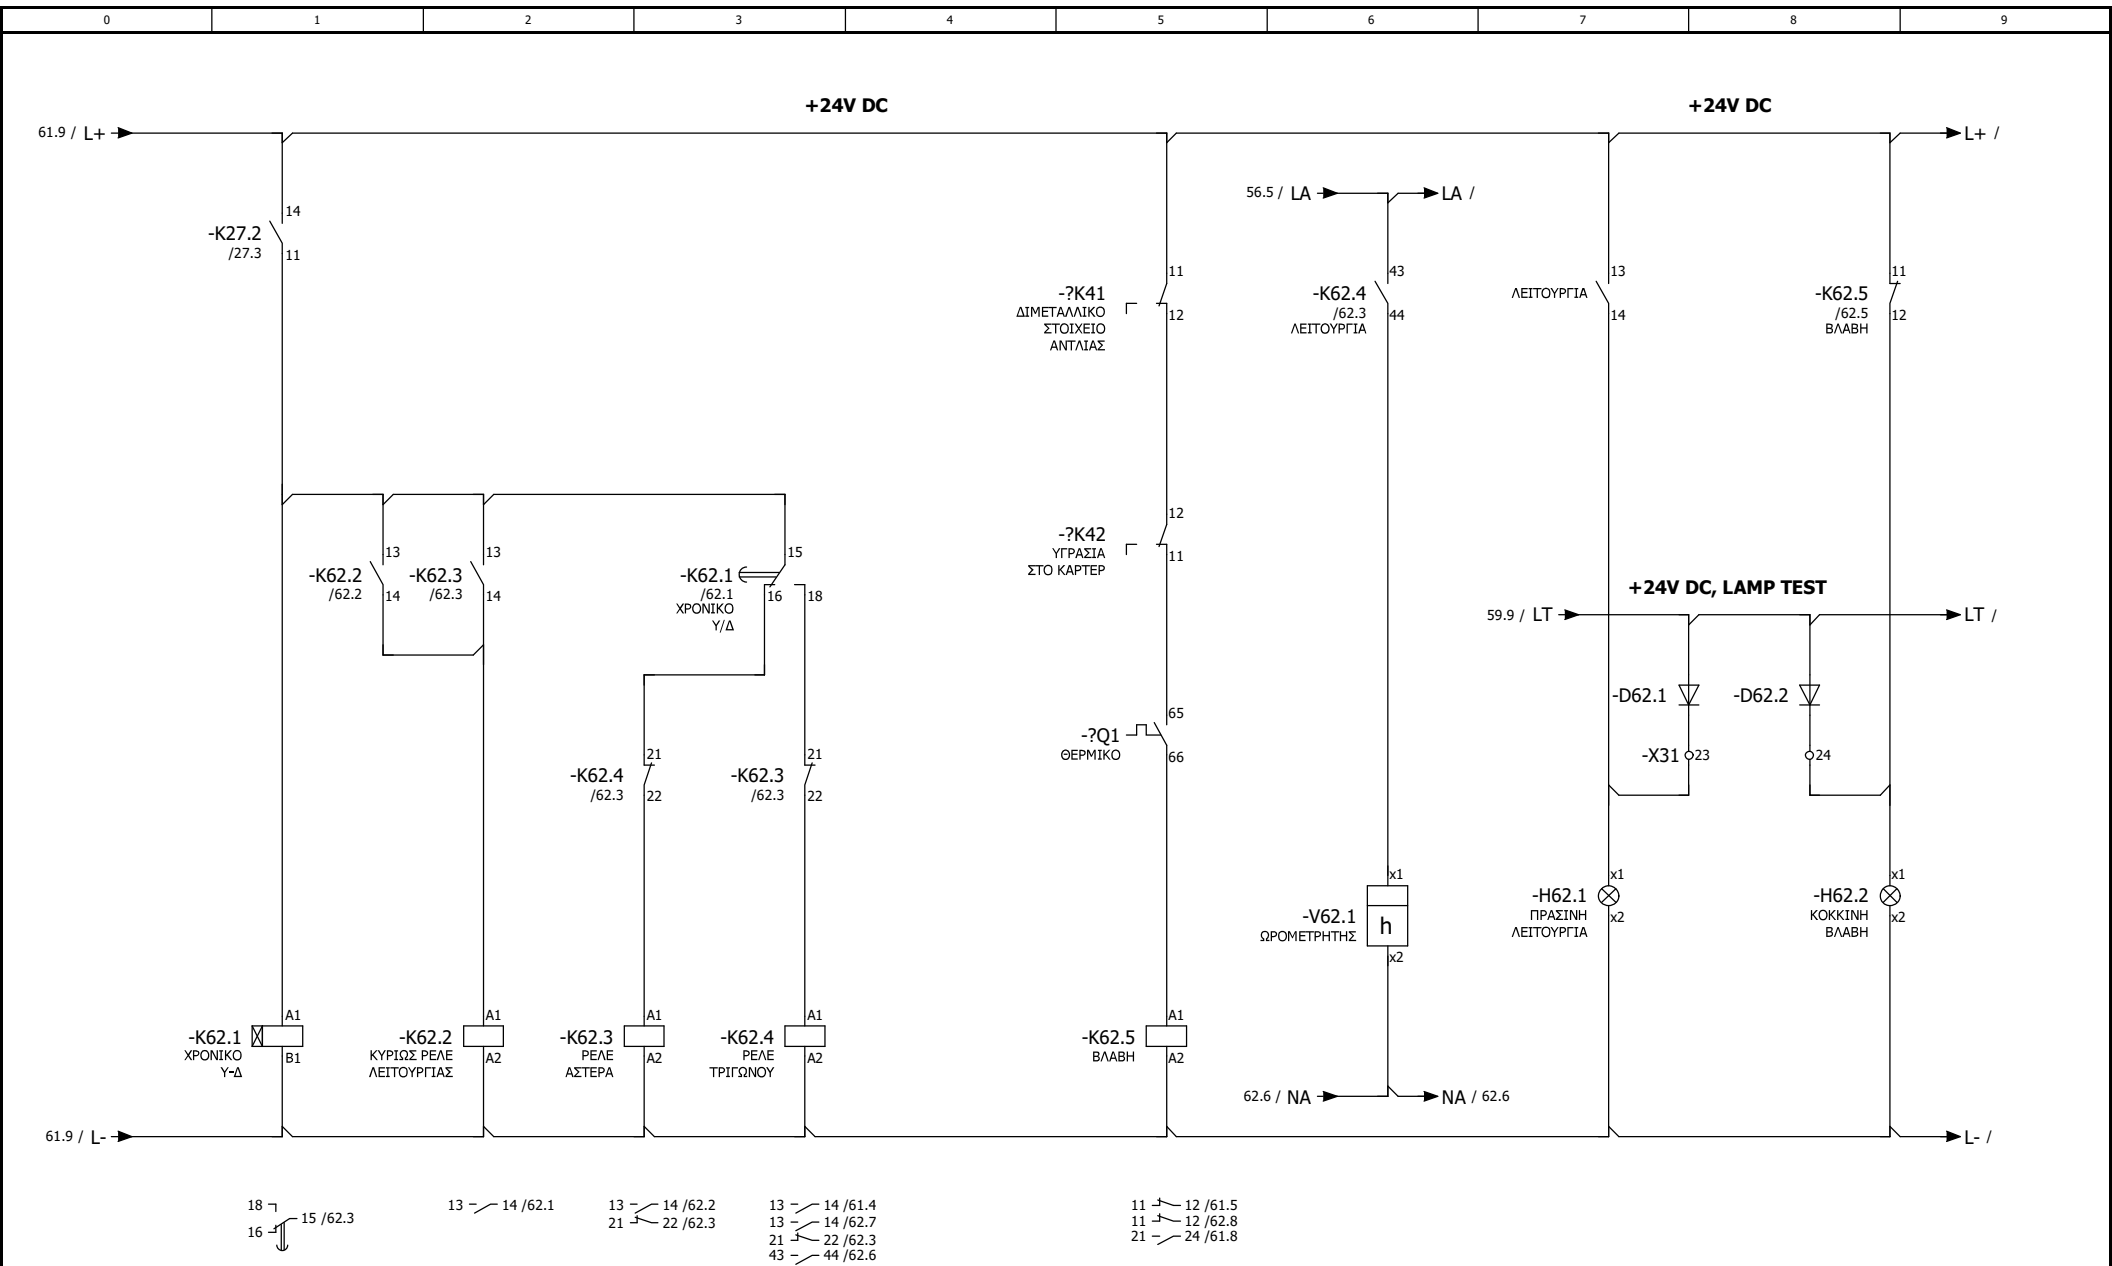


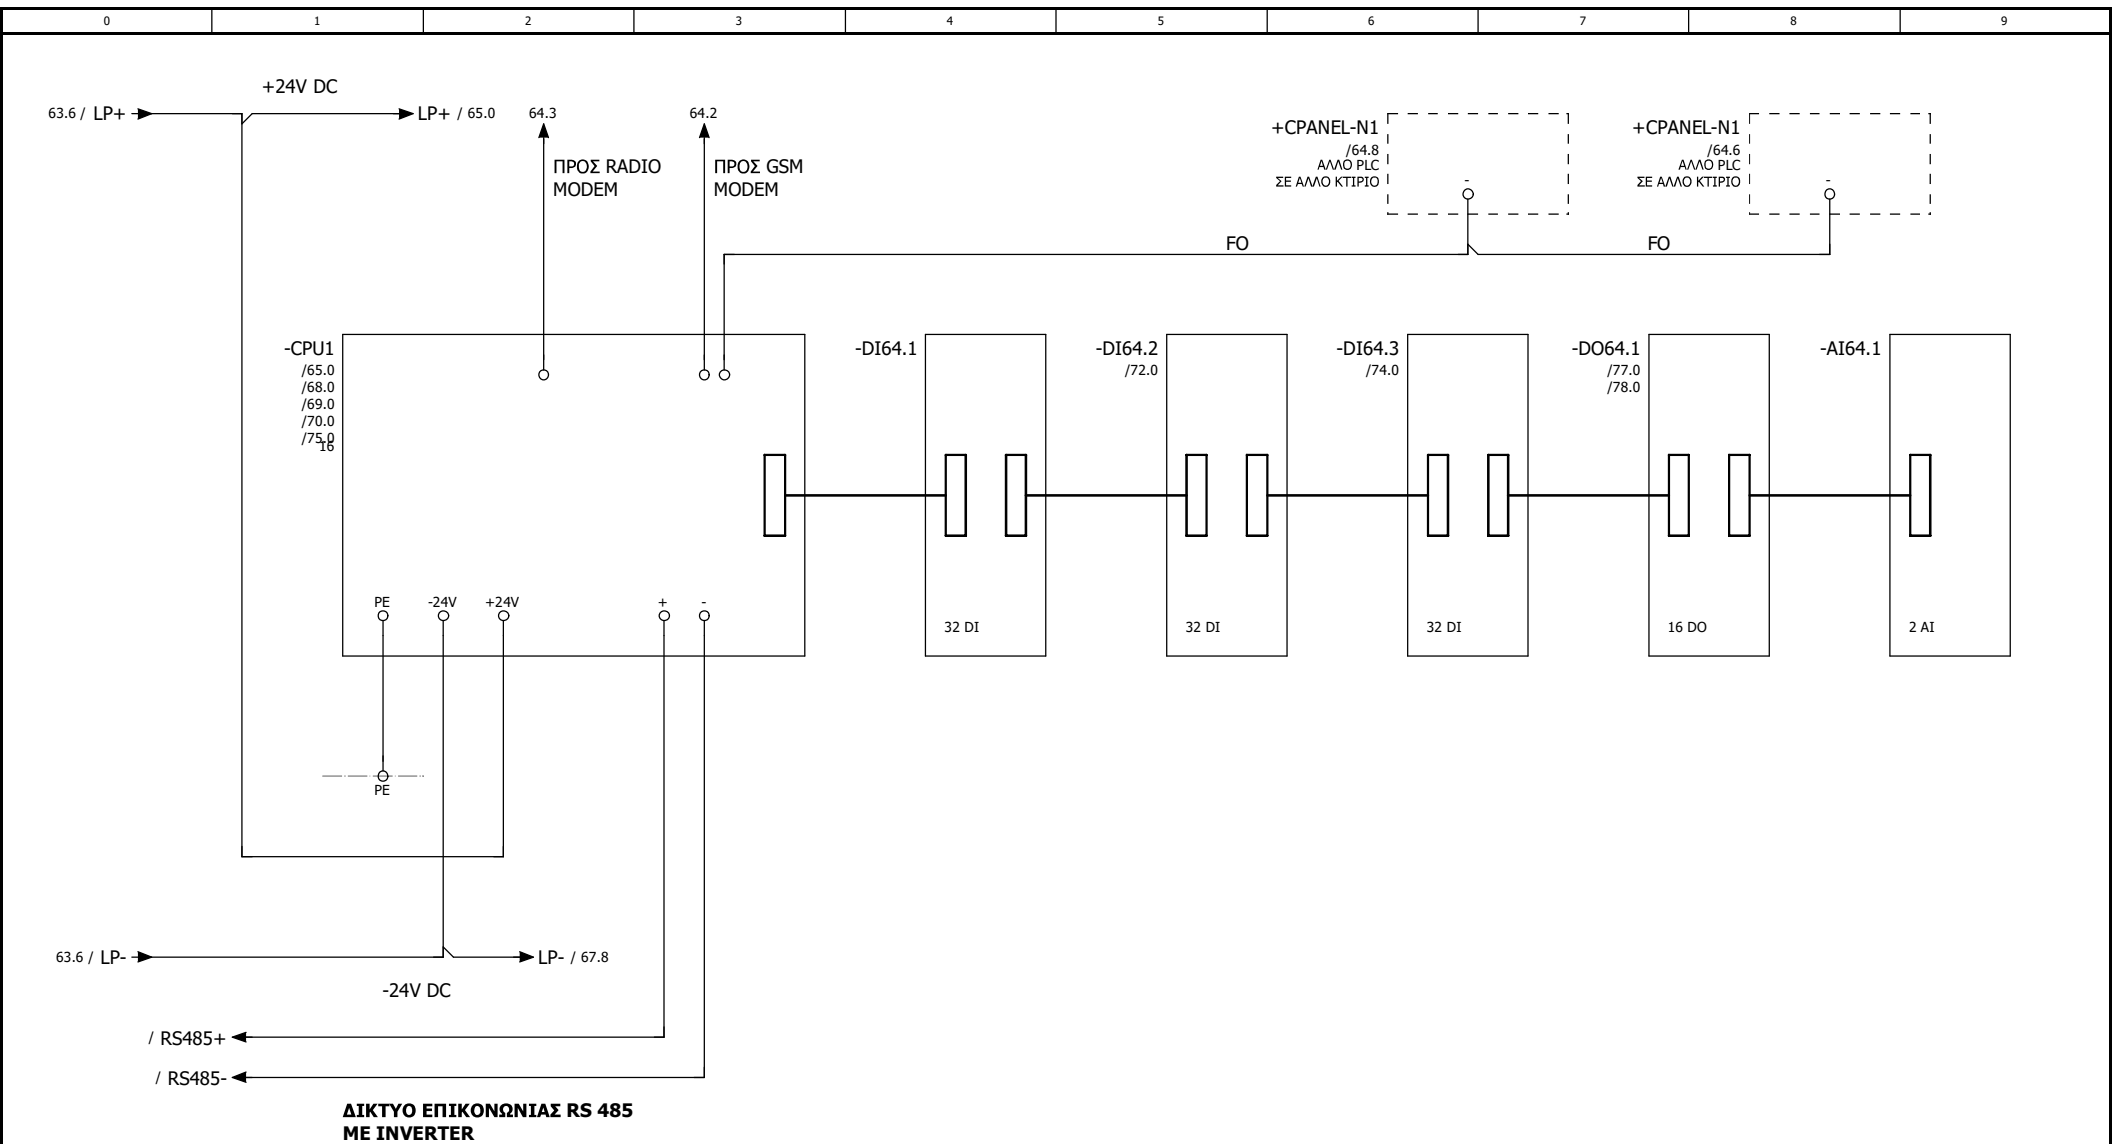

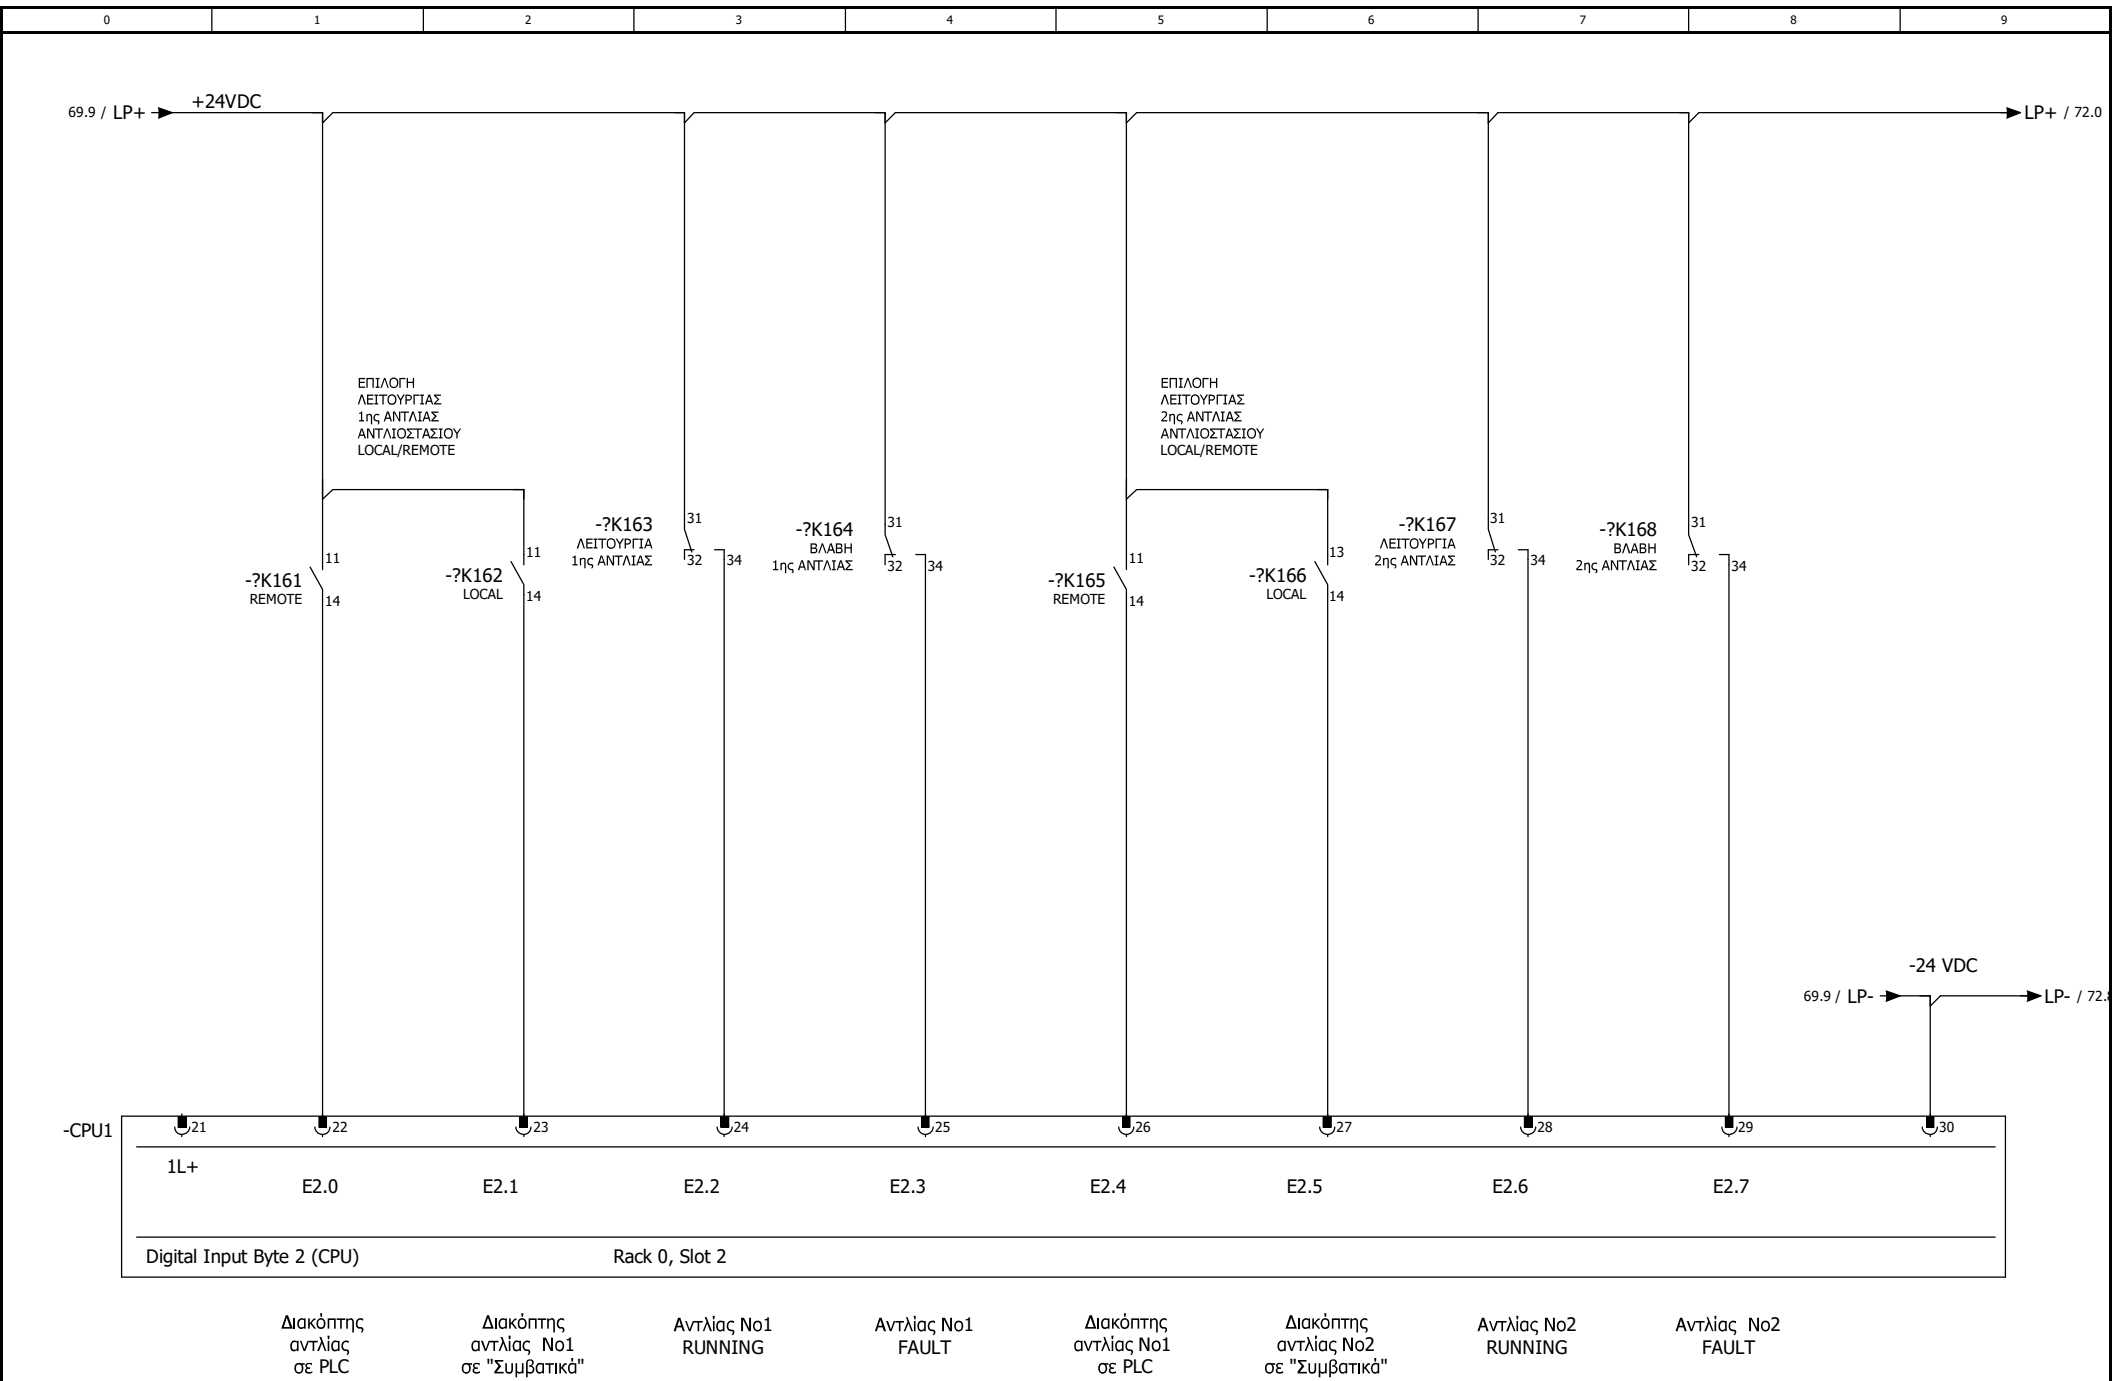


70.9 / LP+ → P#4/974.0

+LCA61
ΠΙΝΑΚΑΣ ΣΥΣΤΗΜΑΤΟΣ COMPACT

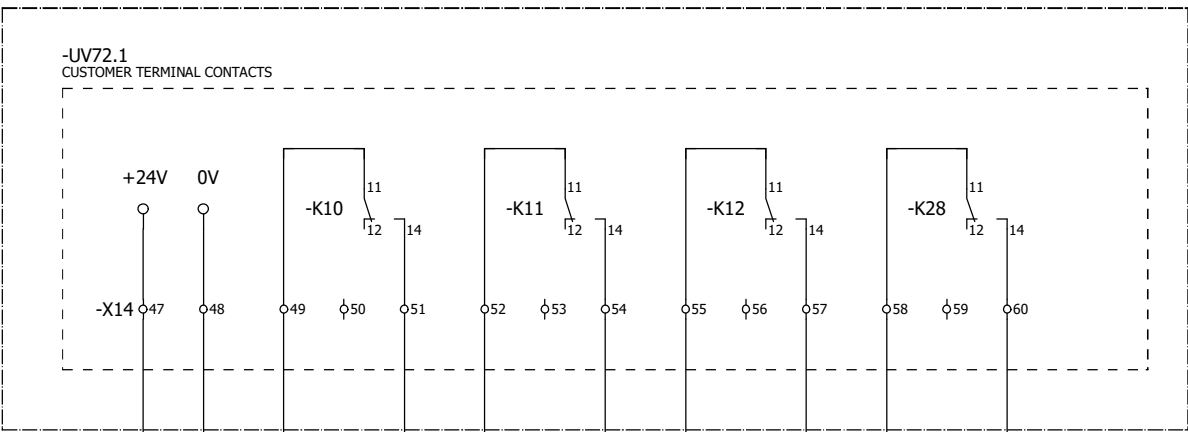

-WS114
/78.6
/78.6
J1VV-R
16x1.5 mm²

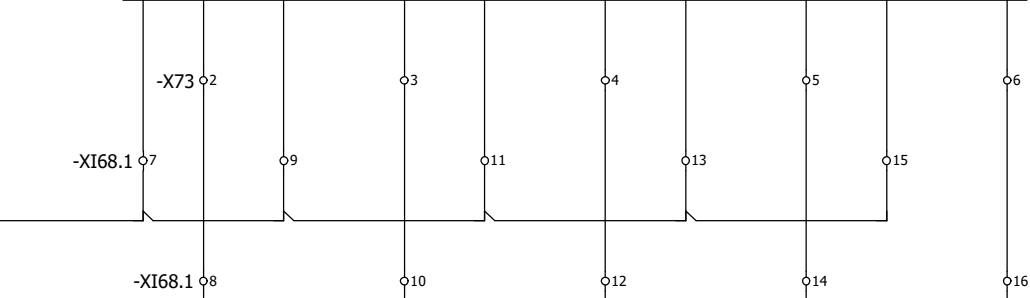

70.9 / LP- → -24 VDC → LP- / 74.8

-DI72.1



Συνθήκη
Λειτουργίας
1ης αντλίας

Συνθήκη
Λειτουργίας
2ης αντλίας

Ελεύθερη


Σήμα Νο1
από CP


Σήμα Νο2
από CP

Σήμα Νο3
από CP


Σήμα Νο4
από CP

Σήμα Νο5
από CP

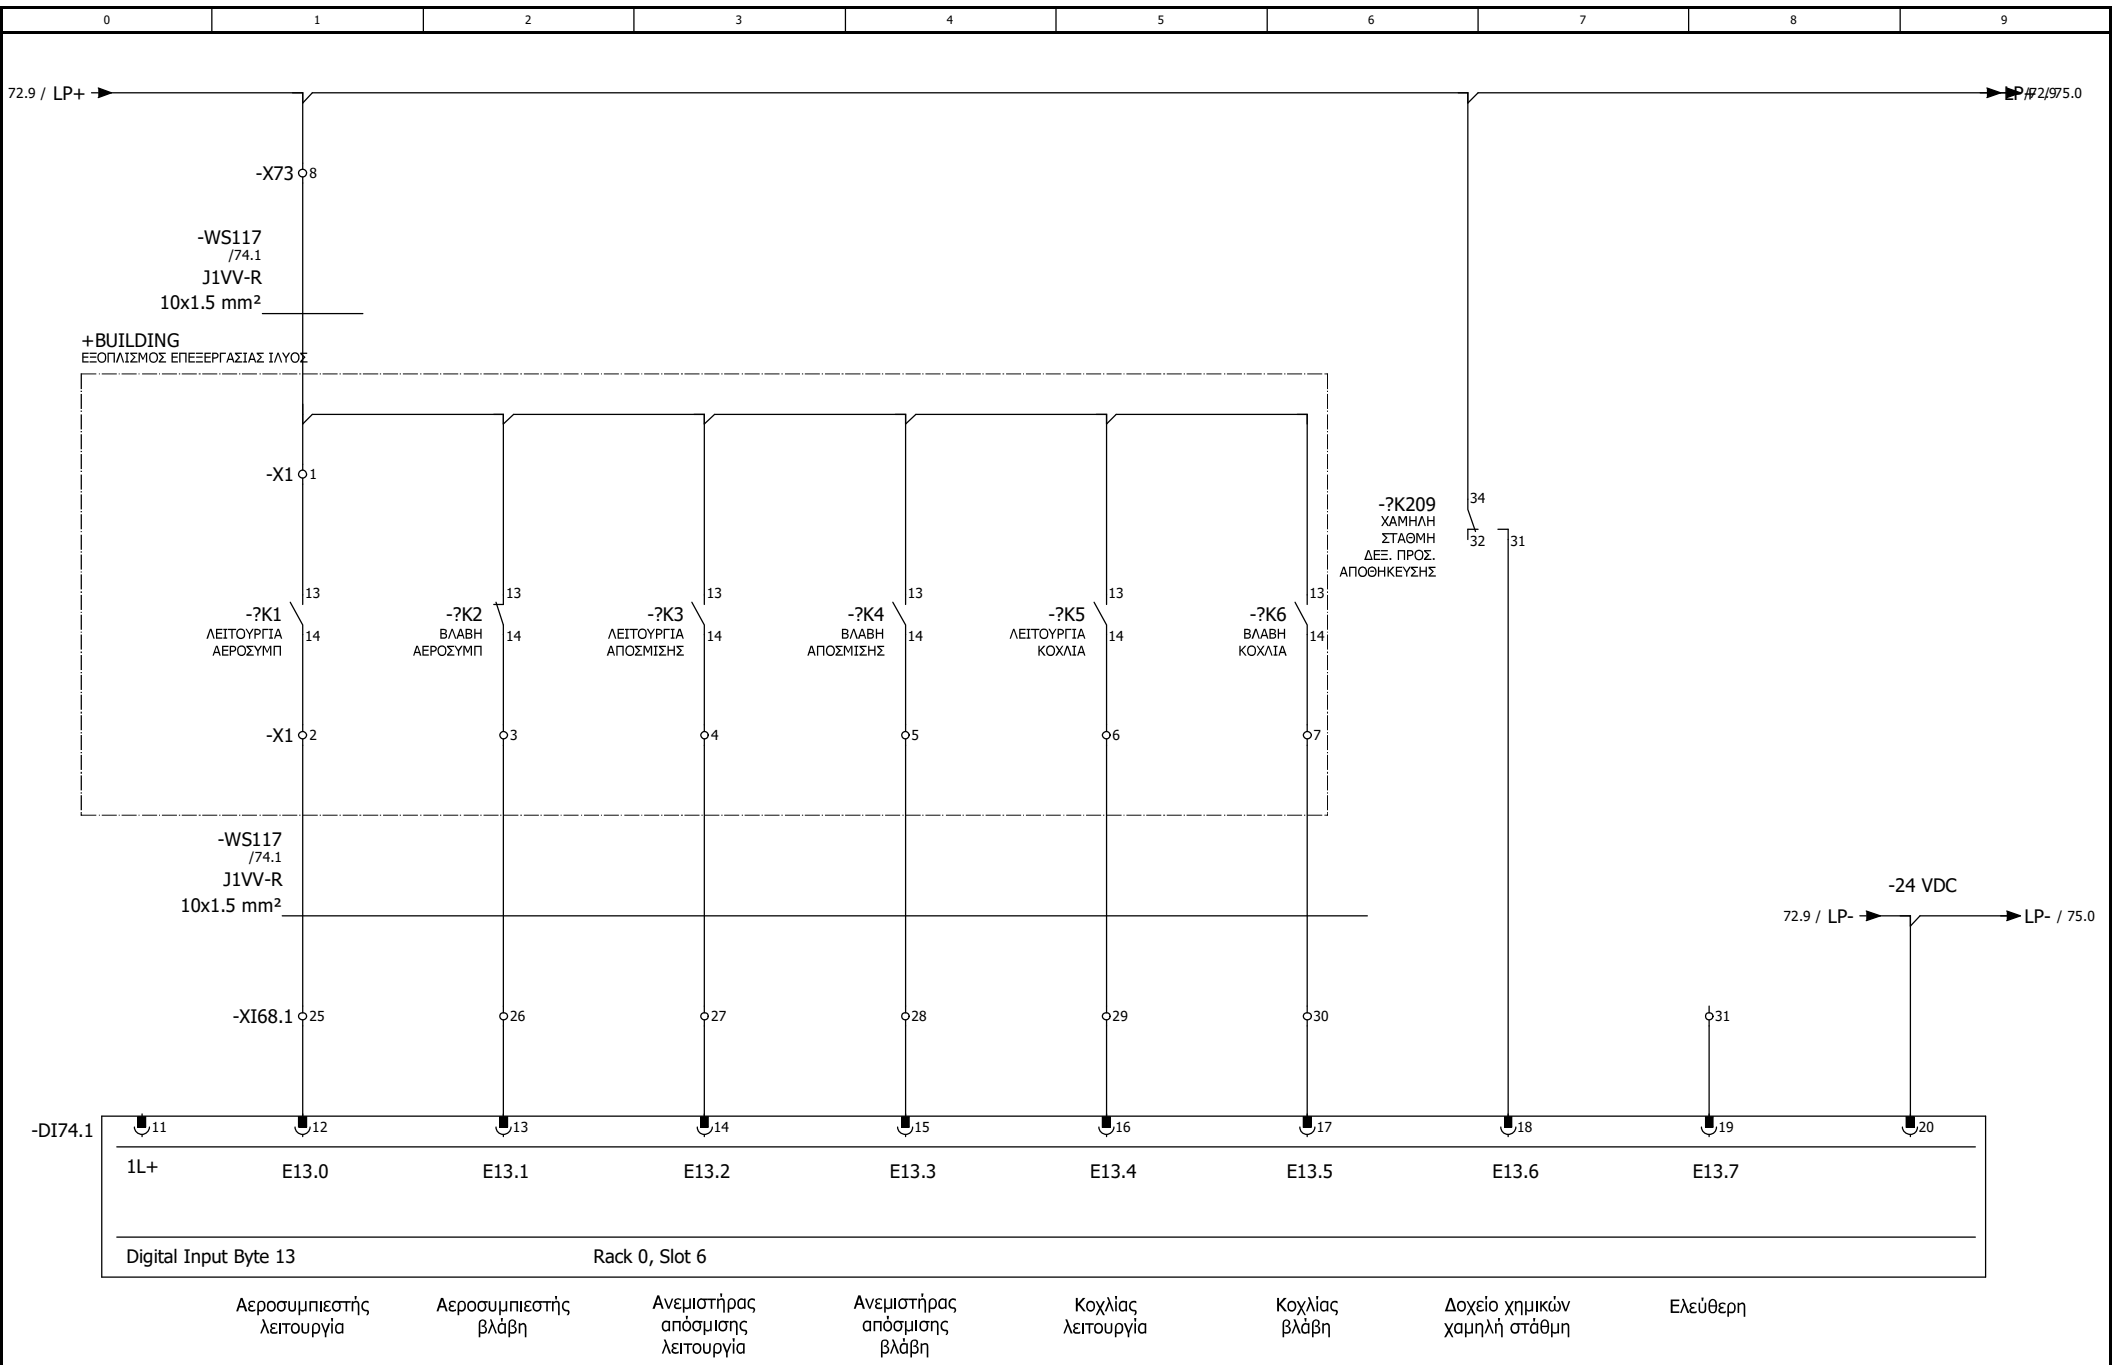

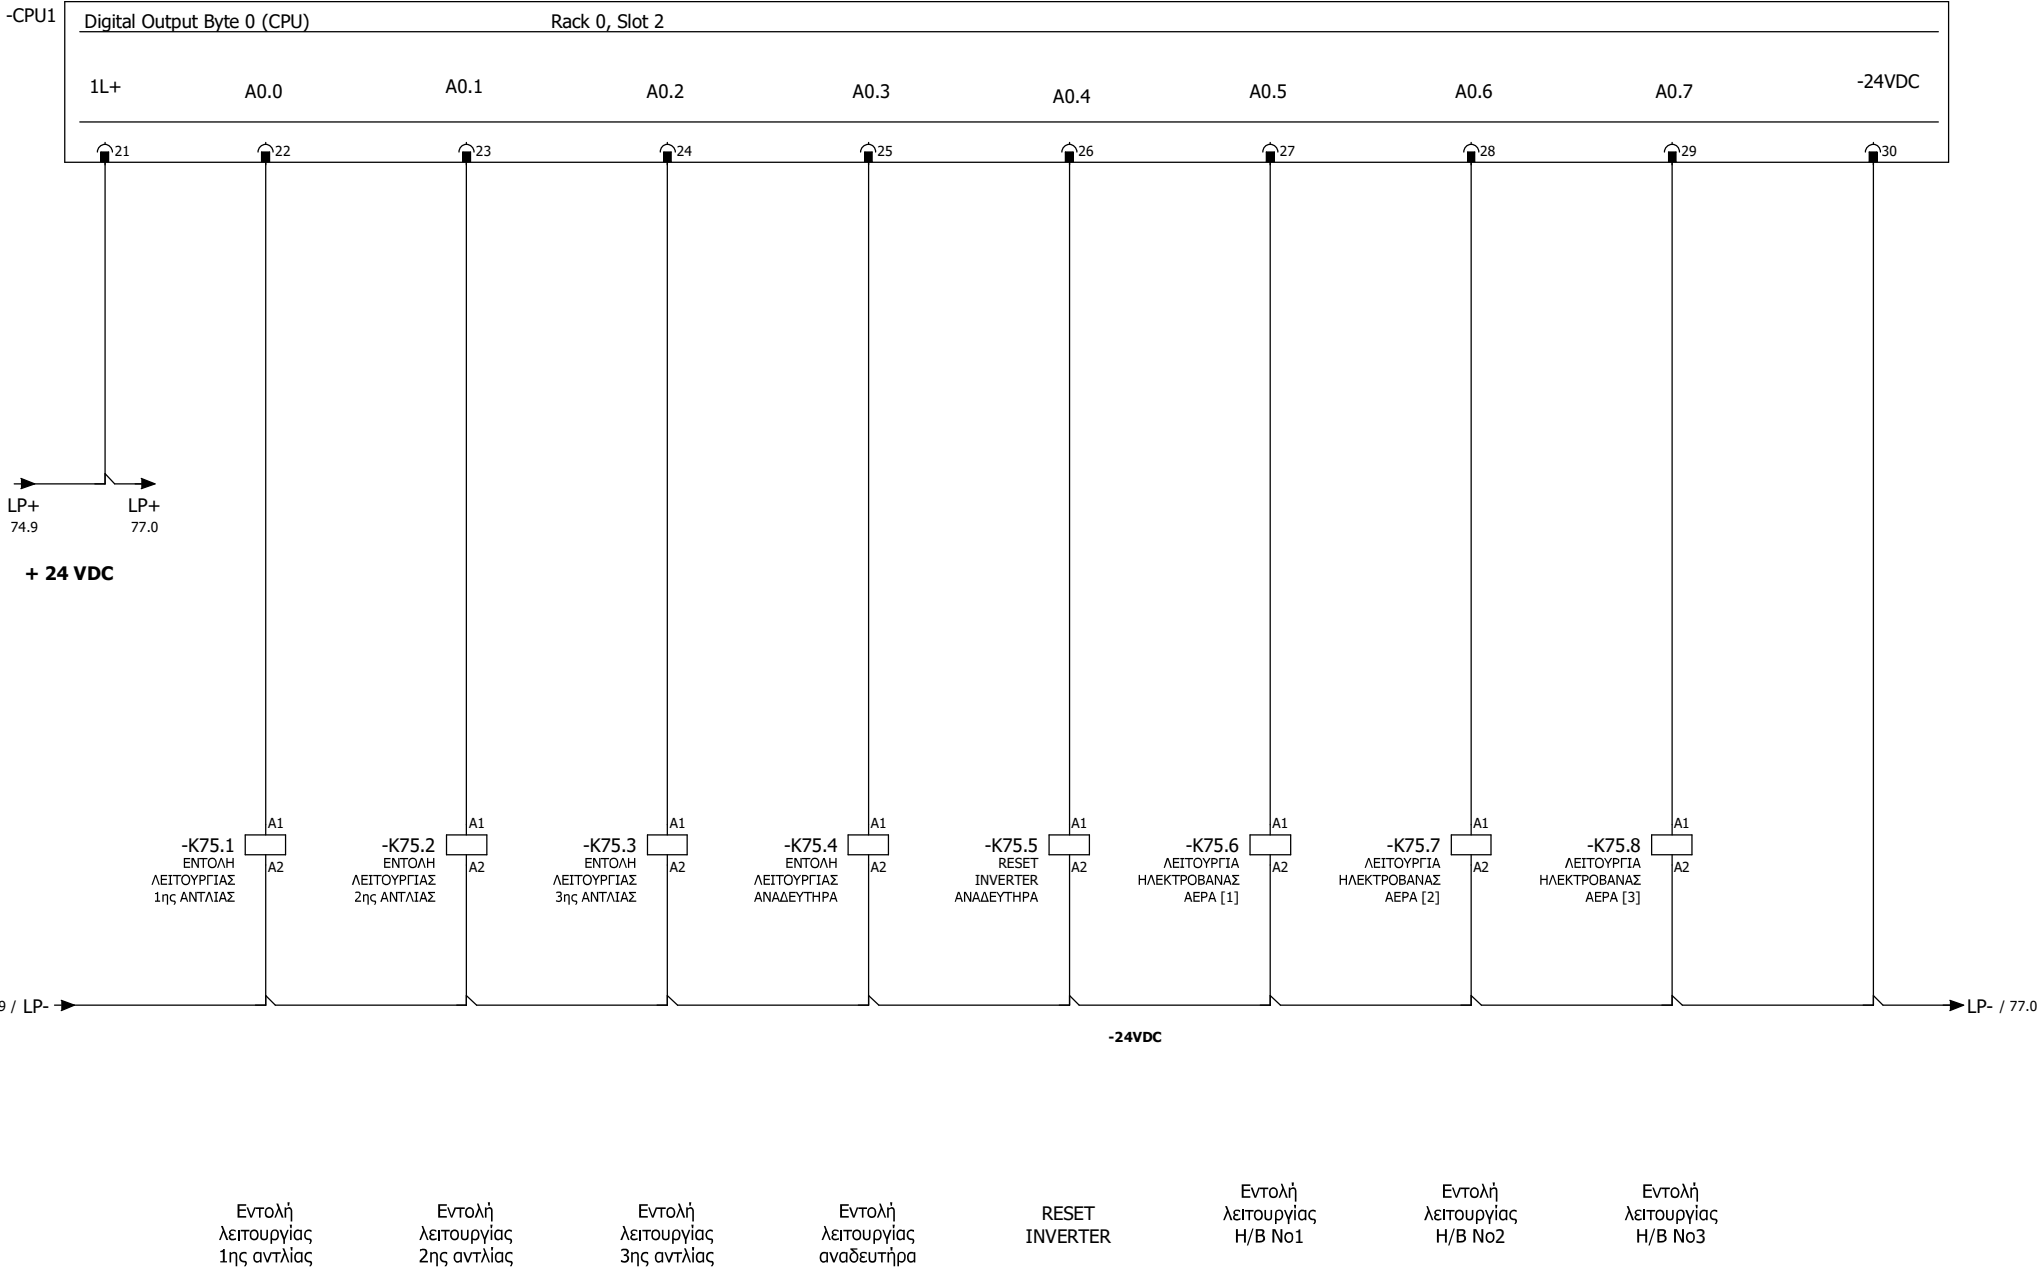

0	1	2	3	4	5	6	7	8	9
---	---	---	---	---	---	---	---	---	---

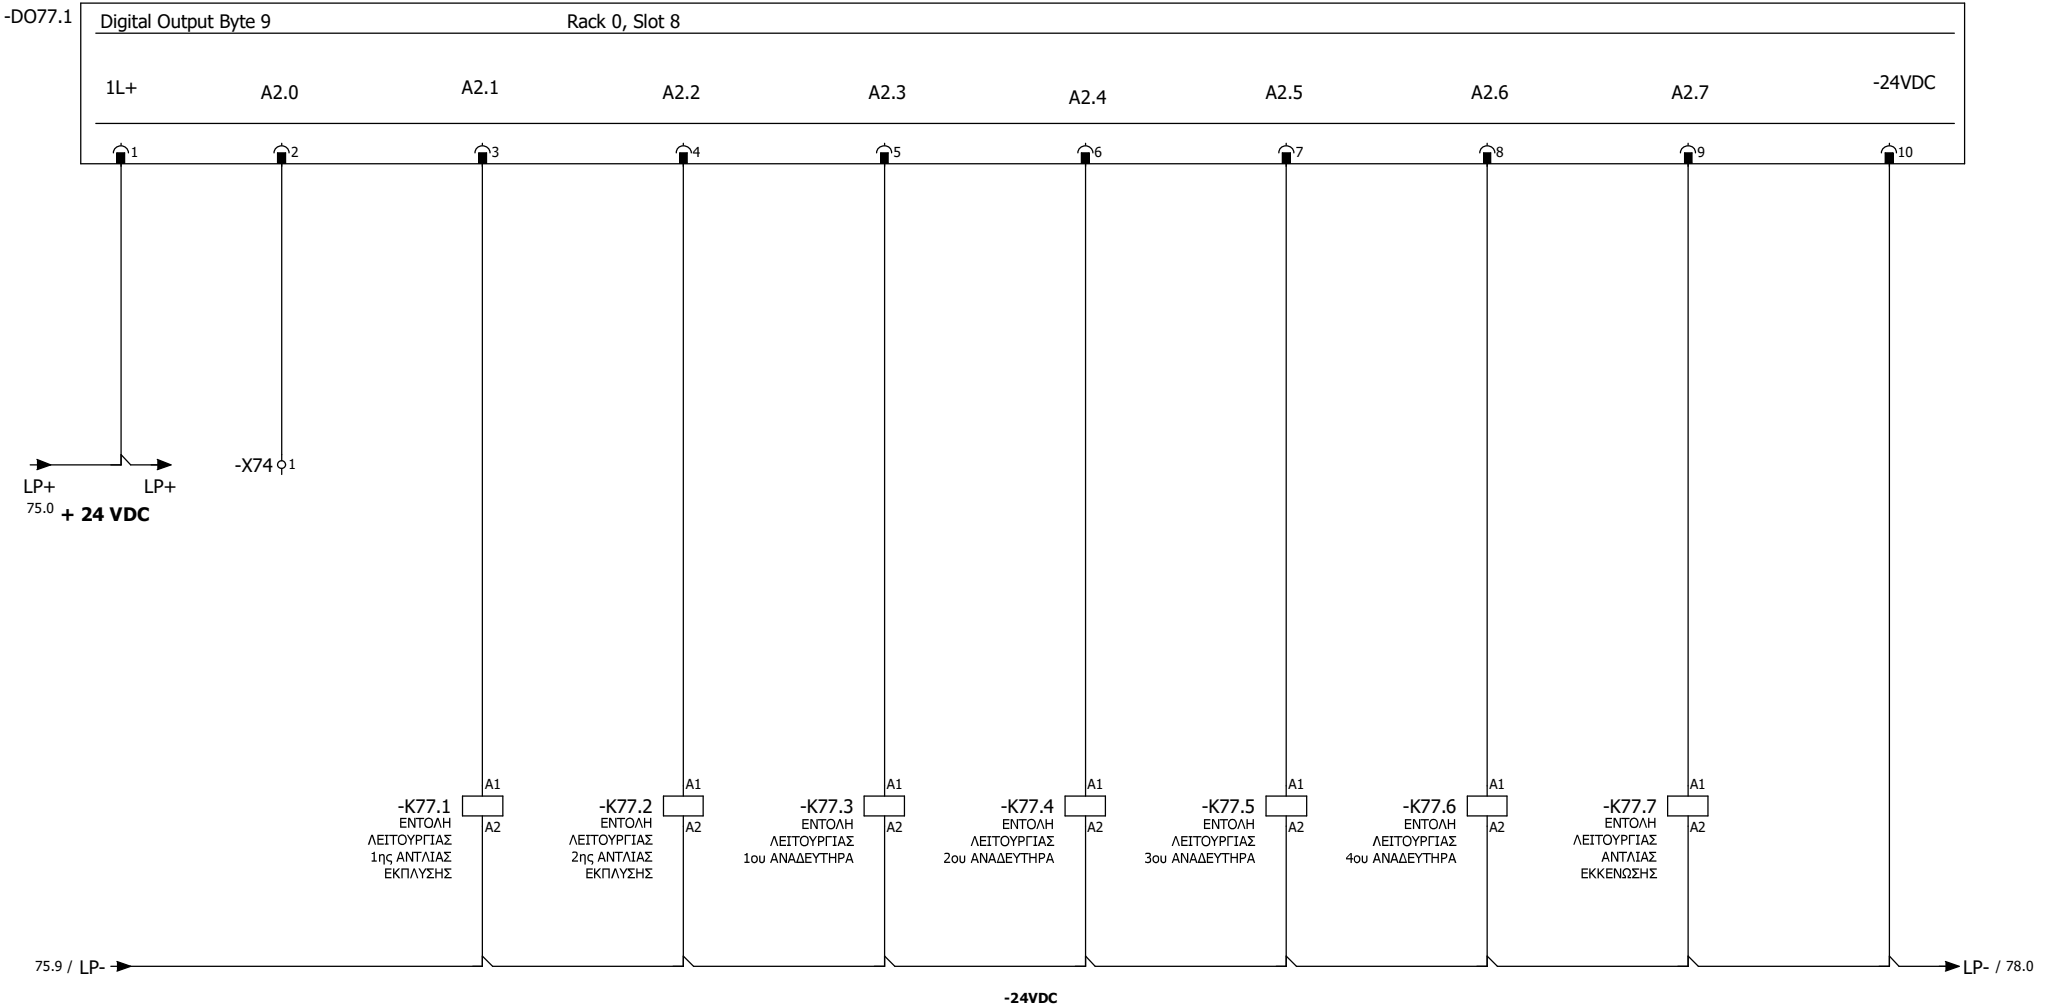

Ελεύθερη

Εντολή λειτουργίας 1ης αντλίας έκπλυσης

Εντολή λειτουργίας 2ης αντλίας έκπλυσης

Εντολή λειτουργίας 1ου αναδευτήρα

Εντολή λειτουργίας 2ου αναδευτήρα

Εντολή λειτουργίας 3ου αναδευτήρα

Εντολή λειτουργίας 4ου αναδευτήρα

Εντολή λειτουργίας αντλίας εκκένωσης

