

0	1	2	3	4	5	6	7	8	9										
ΠΕΛΑΤΗΣ : ΕΡΓΟ ΑΝΑΒΑΘΜΙΣΗΣ ΚΑΙ ΕΠΕΚΤΑΣΗΣ ΤΗΣ ΕΓΚΑΤΑΣΤΑΣΗΣ ΕΡΓΟ : ΕΠΕΞΕΡΓΑΣΙΑΣ ΛΥΜΑΤΩΝ (ΕΕΛ) ΑΓΙΟΥ ΝΙΚΟΛΑΟΥ ΑΡΙΘΜΟΣ ΣΧΕΔΙΟΥ : <tr><td colspan="10"> ΠΕΡΙΓΡΑΦΗ ΠΙΝΑΚΑ : ΠΙΝΑΚΑΣ ΕΡΓΩΝ ΕΙΣΟΔΟΥ ΚΩΔΙΚΟΣ ΠΙΝΑΚΑ : MCC-01 ΚΑΤΑΣΚΕΥΑΣΤΗΣ : ΥΠΕΥΘΥΝΟΣ ΕΡΓΟΥ : ΣΧΕΔΙΑΣΤΗΣ : ΤΥΠΟΣ : ΤΟΠΟΘΕΤΗΣΗ : ΗΜ/ΝΙΑ ΔΗΜΙΟΥΡΓΙΑΣ : 19.09.2019 ΑΡΙΘΜΟΣ ΣΕΛΙΔΩΝ: 1070 </td></tr>										ΠΕΡΙΓΡΑΦΗ ΠΙΝΑΚΑ : ΠΙΝΑΚΑΣ ΕΡΓΩΝ ΕΙΣΟΔΟΥ ΚΩΔΙΚΟΣ ΠΙΝΑΚΑ : MCC-01 ΚΑΤΑΣΚΕΥΑΣΤΗΣ : ΥΠΕΥΘΥΝΟΣ ΕΡΓΟΥ : ΣΧΕΔΙΑΣΤΗΣ : ΤΥΠΟΣ : ΤΟΠΟΘΕΤΗΣΗ : ΗΜ/ΝΙΑ ΔΗΜΙΟΥΡΓΙΑΣ : 19.09.2019 ΑΡΙΘΜΟΣ ΣΕΛΙΔΩΝ: 1070									
ΠΕΡΙΓΡΑΦΗ ΠΙΝΑΚΑ : ΠΙΝΑΚΑΣ ΕΡΓΩΝ ΕΙΣΟΔΟΥ ΚΩΔΙΚΟΣ ΠΙΝΑΚΑ : MCC-01 ΚΑΤΑΣΚΕΥΑΣΤΗΣ : ΥΠΕΥΘΥΝΟΣ ΕΡΓΟΥ : ΣΧΕΔΙΑΣΤΗΣ : ΤΥΠΟΣ : ΤΟΠΟΘΕΤΗΣΗ : ΗΜ/ΝΙΑ ΔΗΜΙΟΥΡΓΙΑΣ : 19.09.2019 ΑΡΙΘΜΟΣ ΣΕΛΙΔΩΝ: 1070																			

0	1	2	3	4	5	6	7	8	9
---	---	---	---	---	---	---	---	---	---

ΠΕΡΙΕΧΟΜΕΝΑ

ΠΙΝΑΚΑΣ	ΚΩΔΙΚΟΣ ΣΧΕΔΙΟΥ	ΣΕΛΙΔΑ	ΠΕΡΙΓΡΑΦΗ ΣΕΛΙΔΑΣ	ΤΟΠΟΘΕΣΙΑ	ΗΜΕΡΟΜΗΝΙΑ
MCC-01		1	ΕΞΩΦΥΛΛΟ	=MCC-01/1	19.09.2019
MCC-01		2	ΠΕΡΙΕΧΟΜΕΝΑ	=MCC-01/2	19.09.2019
MCC-01		2.a	ΠΕΡΙΕΧΟΜΕΝΑ	=MCC-01/2.a	19.09.2019
MCC-01	MAIN	1	ΤΡΟΦΟΔΟΣΙΑ ΠΙΝΑΚΑ	=MCC-01+MAIN/1	19.09.2019
MCC-01	MAIN	2	ΑΝΑΧΩΡΗΣΕΙΣ	=MCC-01+MAIN/2	18.09.2019
MCC-01	MAIN	3	ΑΝΑΧΩΡΗΣΕΙΣ	=MCC-01+MAIN/3	19.09.2019
MCC-01	MAIN	4	ΑΝΑΧΩΡΗΣΕΙΣ	=MCC-01+MAIN/4	19.09.2019
MCC-01	MAIN	5	ΚΕΝΗ ΣΕΛΙΔΑ	=MCC-01+MAIN/5	18.09.2019
MCC-01	MAIN	6	ΑΝΑΧΩΡΗΣΕΙΣ ΠΙΝΑΚΩΝ & ΑΥΤΟΜΑΤΙΣΜΟΥ	=MCC-01+MAIN/6	19.09.2019
MCC-01	MAIN	7	ΑΝΑΧΩΡΗΣΕΙΣ ΠΙΝΑΚΩΝ	=MCC-01+MAIN/7	19.09.2019
MCC-01	MAIN	8	ΑΝΑΧΩΡΗΣΕΙΣ ΠΙΝΑΚΩΝ (ΜΟΝΑΔΑ ΠΑΡΑΓΩΓΗΣ ΠΡΟΟΖΟΝΩΣΗΣ)	=MCC-01+MAIN/8	19.09.2019
MCC-01	MAIN	12	UPS	=MCC-01+MAIN/12	19.09.2019
MCC-01	MAIN	13	ΤΑΣΕΙΣ ΕΛΕΓΧΟΥ 230VAC	=MCC-01+MAIN/13	19.09.2019
MCC-01	MAIN	14	ΤΑΣΕΙΣ ΕΛΕΓΧΟΥ 230VAC	=MCC-01+MAIN/14	19.09.2019
MCC-01	MAIN	15	ΤΑΣΕΙΣ ΕΛΕΓΧΟΥ 24VDC	=MCC-01+MAIN/15	19.09.2019
MCC-01	MAIN	16	ΚΕΝΗ ΣΕΛΙΔΑ	=MCC-01+MAIN/16	18.09.2019
MCC-01	CONTROL	1	ΡΥΘΜΙΣΤΙΚΗ ΔΙΚΛΕΙΔΑ ΚΥΡΙΟΥ ΑΓΩΓΟΥ ΕΙΣΟΔΟΥ M01-01-05	=MCC-01+CONTROL/1	19.09.2019
MCC-01	CONTROL	1.a	ΡΥΘΜΙΣΤΙΚΗ ΔΙΚΛΕΙΔΑ ΚΥΡΙΟΥ ΑΓΩΓΟΥ ΕΙΣΟΔΟΥ M01-01-05	=MCC-01+CONTROL/1.a	19.09.2019
MCC-01	CONTROL	2	ΡΥΘΜΙΣΤΙΚΗ ΔΙΚΛΕΙΔΑ ΕΦΕΔΡΙΚΟΥ ΑΓΩΓΟΥ ΕΙΣΟΔΟΥ M01-01-06	=MCC-01+CONTROL/2	19.09.2019
MCC-01	CONTROL	2.a	ΡΥΘΜΙΣΤΙΚΗ ΔΙΚΛΕΙΔΑ ΕΦΕΔΡΙΚΟΥ ΑΓΩΓΟΥ ΕΙΣΟΔΟΥ M01-01-06	=MCC-01+CONTROL/2.a	19.09.2019
MCC-01	CONTROL	3	ΑΥΤΟΚΑΘΑΡΙΖΟΜΕΝΗ ΕΣΧΑΡΑ M01-01-09	=MCC-01+CONTROL/3	19.09.2019
MCC-01	CONTROL	3.a	ΑΥΤΟΚΑΘΑΡΙΖΟΜΕΝΗ ΕΣΧΑΡΑ M01-01-09	=MCC-01+CONTROL/3.a	19.09.2019
MCC-01	CONTROL	4	ΚΟΧΛΙΑΣ ΜΕΤΑΦΟΡΑΣ - ΣΥΜΠΙΕΣΗΣ M01.02	=MCC-01+CONTROL/4	19.09.2019
MCC-01	CONTROL	5	ΑΞΟΝΙΚΟΣ ΑΝΕΜΙΣΤΗΡΑΣ ΕΞΑΕΡΙΣΜΟΥ ΚΤΗΡΙΟΥ ΕΣΧΑΡΩΣΗΣ M01-01-16-1	=MCC-01+CONTROL/5	19.09.2019
MCC-01	CONTROL	6	ΑΞΟΝΙΚΟΣ ΑΝΕΜΙΣΤΗΡΑΣ ΕΞΑΕΡΙΣΜΟΥ ΚΤΗΡΙΟΥ ΕΣΧΑΡΩΣΗΣ M01-01-16-2	=MCC-01+CONTROL/6	19.09.2019
MCC-01	CONTROL	7	ΣΥΣΤΗΜΑ ΚΑΘ. ΑΕΡΑ ΠΙΝΑΚΑ MCC-01	=MCC-01+CONTROL/7	19.09.2019
MCC-01	CONTROL	8	ΚΑΤΑΚΟΡΥΦΟΣ ΑΝΑΔΕΥΤΗΡΑΣ ΦΡΕΑΤΙΟΥ ΠΡΟΣΘΗΚΗΣ ΘΕΠΙΚΟΥ ΟΞΕΟΣ M02-01-01	=MCC-01+CONTROL/8	19.09.2019
MCC-01	CONTROL	9	ΑΝΕΜΙΣΤΗΡΑΣ ΧΩΡΟΥ ΠΑΡΑΓΩΓΗΣ ΠΡΟΟΖΟΝΩΣΗΣ M02-01-18	=MCC-01+CONTROL/9	19.09.2019
MCC-01	CONTROL	10	ΑΝΕΜΙΣΤΗΡΑΣ ΧΩΡΟΥ ΟΖΟΝΙΣΤΗΡΑ ΠΡΟΟΖΟΝΩΣΗΣ M02-01-19	=MCC-01+CONTROL/10	19.09.2019
MCC-01	CONTROL	11	ΑΝΕΜΙΣΤΗΡΑΣ EMERGENCY ΠΡΟΟΖΟΝΩΣΗΣ M02-01-20	=MCC-01+CONTROL/11	19.09.2019
MCC-01	CONTROL	12	ΑΝΤΛΙΑ ΤΡΟΦΟΔΟΣΙΑΣ ΟΡΓΑΝΟΥ ΜΕΤΡΗΣΗΣ ΔΙΑΛΥΜΕΝΟΥ ΟΖΟΝΤΟΣ ΣΤΟ ΝΕΡΟ M02-01-28	=MCC-01+CONTROL/12	19.09.2019
MCC-01	CONTROL	13	ΣΗΜΑΤΑ ΑΠΟ ΠΙΝΑΚΑ ΕΡΓΩΝ ΚΕΦΑΛΗΣ LP-02	=MCC-01+CONTROL/13	18.09.2019
MCC-01	CONTROL	13.a	ΕΝΤΟΛΕΣ ΠΙΝΑΚΑΣ ΕΡΓΩΝ ΚΕΦΑΛΗΣ LP-02	=MCC-01+CONTROL/13.a	19.09.2019


			ΗΜ/ΝΙΑ	19.09.2019	ΑΡ. ΣΧΕΔΙΟΥ : ΕΡΓΟ ΑΝΑΒΑΘΜΙΣΗΣ ΚΑΙ ΕΠΕΚΤΑΣΗΣ ΤΗΣ ΕΡΓΟ : ΕΓΚΑΤΑΣΤΑΣΗΣ ΕΠΕΞΕΡΓΑΣΙΑΣ ΛΥΜΑΤΩΝ (ΕΕΛ) ΠΕΛΑΤΗΣ : ΑΓΙΟΥ ΝΙΚΟΛΑΟΥ ΠΕΡΙΓΡΑΦΗ ΠΙΝΑΚΑ : ΠΙΝΑΚΑΣ ΕΡΓΩΝ ΕΙΣΟΔΟΥ	ΠΕΡΙΕΧΟΜΕΝΑ	= MCC-01
			ΜΕΛΕΤΗ				+
	09.04.2019		ΣΧΕΔΙΟ				ΦΥΛΛΟ: 2
ΑΛΛΑΓΗ	ΗΜ/ΝΙΑ	ΟΝΟΜΑ	ΘΕΩΡ.				ΤΕΛ. ΦΥΛΛΟ: 2.a

0	1	2	3	4	5	6	7	8	9
---	---	---	---	---	---	---	---	---	---


ΠΕΡΙΕΧΟΜΕΝΑ

[illegible]


			ΗΜ/ΝΙΑ	19.09.2019	ΑΡ, ΣΧΕΔΙΟΥ : ΕΡΓΟ ΑΝΑΒΑΘΜΙΣΗΣ ΚΑΙ ΕΠΕΚΤΑΣΗΣ ΤΗΣ ΕΡΓΟ : ΕΠΚΑΤΑΣΤΑΣΗΣ ΠΕΠΕΡΓΑΣΙΑΣ ΛΥΜΑΤΩΝ (ΕΕΛ) ΠΕΛΑΤΗΣ : ΑΓΓΟΥ ΝΙΚΟΛΑΟΥ ΠΕΡΙΓΡΑΦΗ ΠΙΝΑΚΑ : ΠΙΝΑΚΑΣ ΕΡΓΩΝ ΕΙΣΟΔΟΥ	ΠΕΡΙΕΧΟΜΕΝΑ	=	MCC-01
			ΜΕΛΕΤΗ				+	
	09.04.2019		ΣΧΕΔΙΟ				ΦΥΛΛΟ:	2.a
ΑΛΛΑΓΗ	ΗΜ/ΝΙΑ	ΟΝΟΜΑ	ΘΕΩΡ.				ΤΕΛ. ΦΥΛΛΟ:	2.a

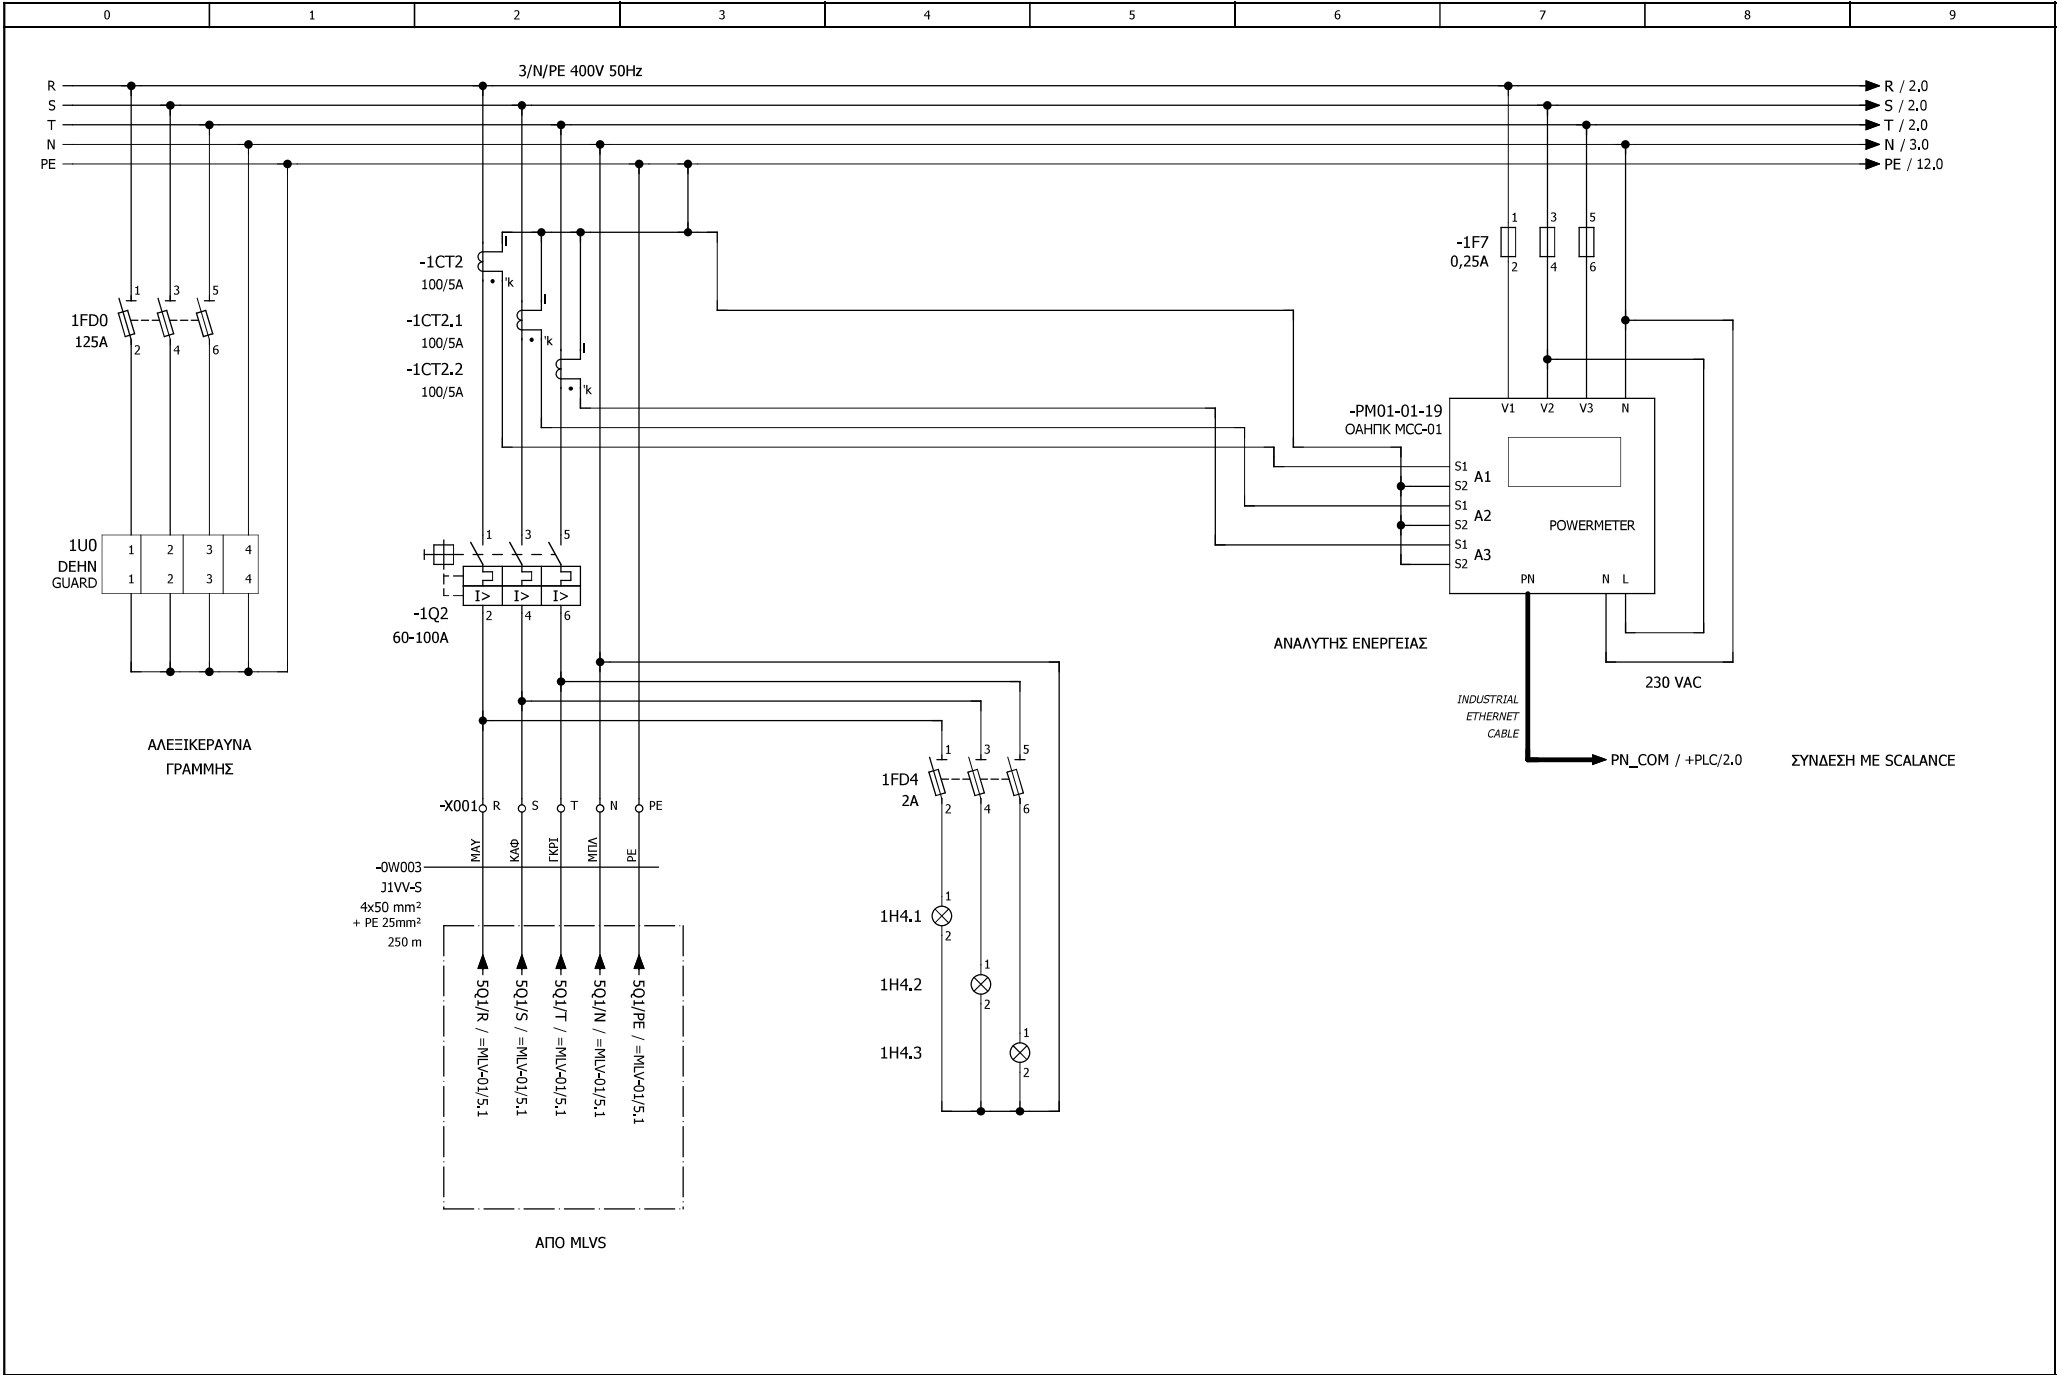


			ΗΜ/ΝΙΑ	19.09.2019	ΑΡ. ΣΧΕΔΙΟΥ	ΕΡΓΟ ΑΝΑΒΑΘΜΙΣΗΣ ΚΑΙ ΕΠΕΚΤΑΣΗΣ ΤΗΣ	ΤΡΟΦΟΔΟΣΙΑ ΠΙΝΑΚΑ	= MCC-01
			ΜΕΛΕΤΗ		ΕΡΓΟ	ΕΓΚΑΤΑΣΤΑΣΗΣ ΕΠΕΞΕΡΓΑΣΙΑΣ ΛΥΜΑΤΩΝ (ΕΕΛ)		+ MAIN
09.04.2019			ΣΧΕΔΙΟ		ΠΕΛΑΤΗΣ	ΑΓΙΟΥ ΝΙΚΟΛΑΟΥ		ΦΥΛΛΟ: 1
ΑΛΛΑΓΗ	ΗΜ/ΝΙΑ	ΟΝΟΜΑ	ΘΕΩΡ.		ΠΕΡΙΓΡΑΦΗ ΠΙΝΑΚΑ	ΠΙΝΑΚΑΣ ΕΡΓΩΝ ΕΙΣΟΔΟΥ		ΤΕΛ. ΦΥΛΛΟ: 16

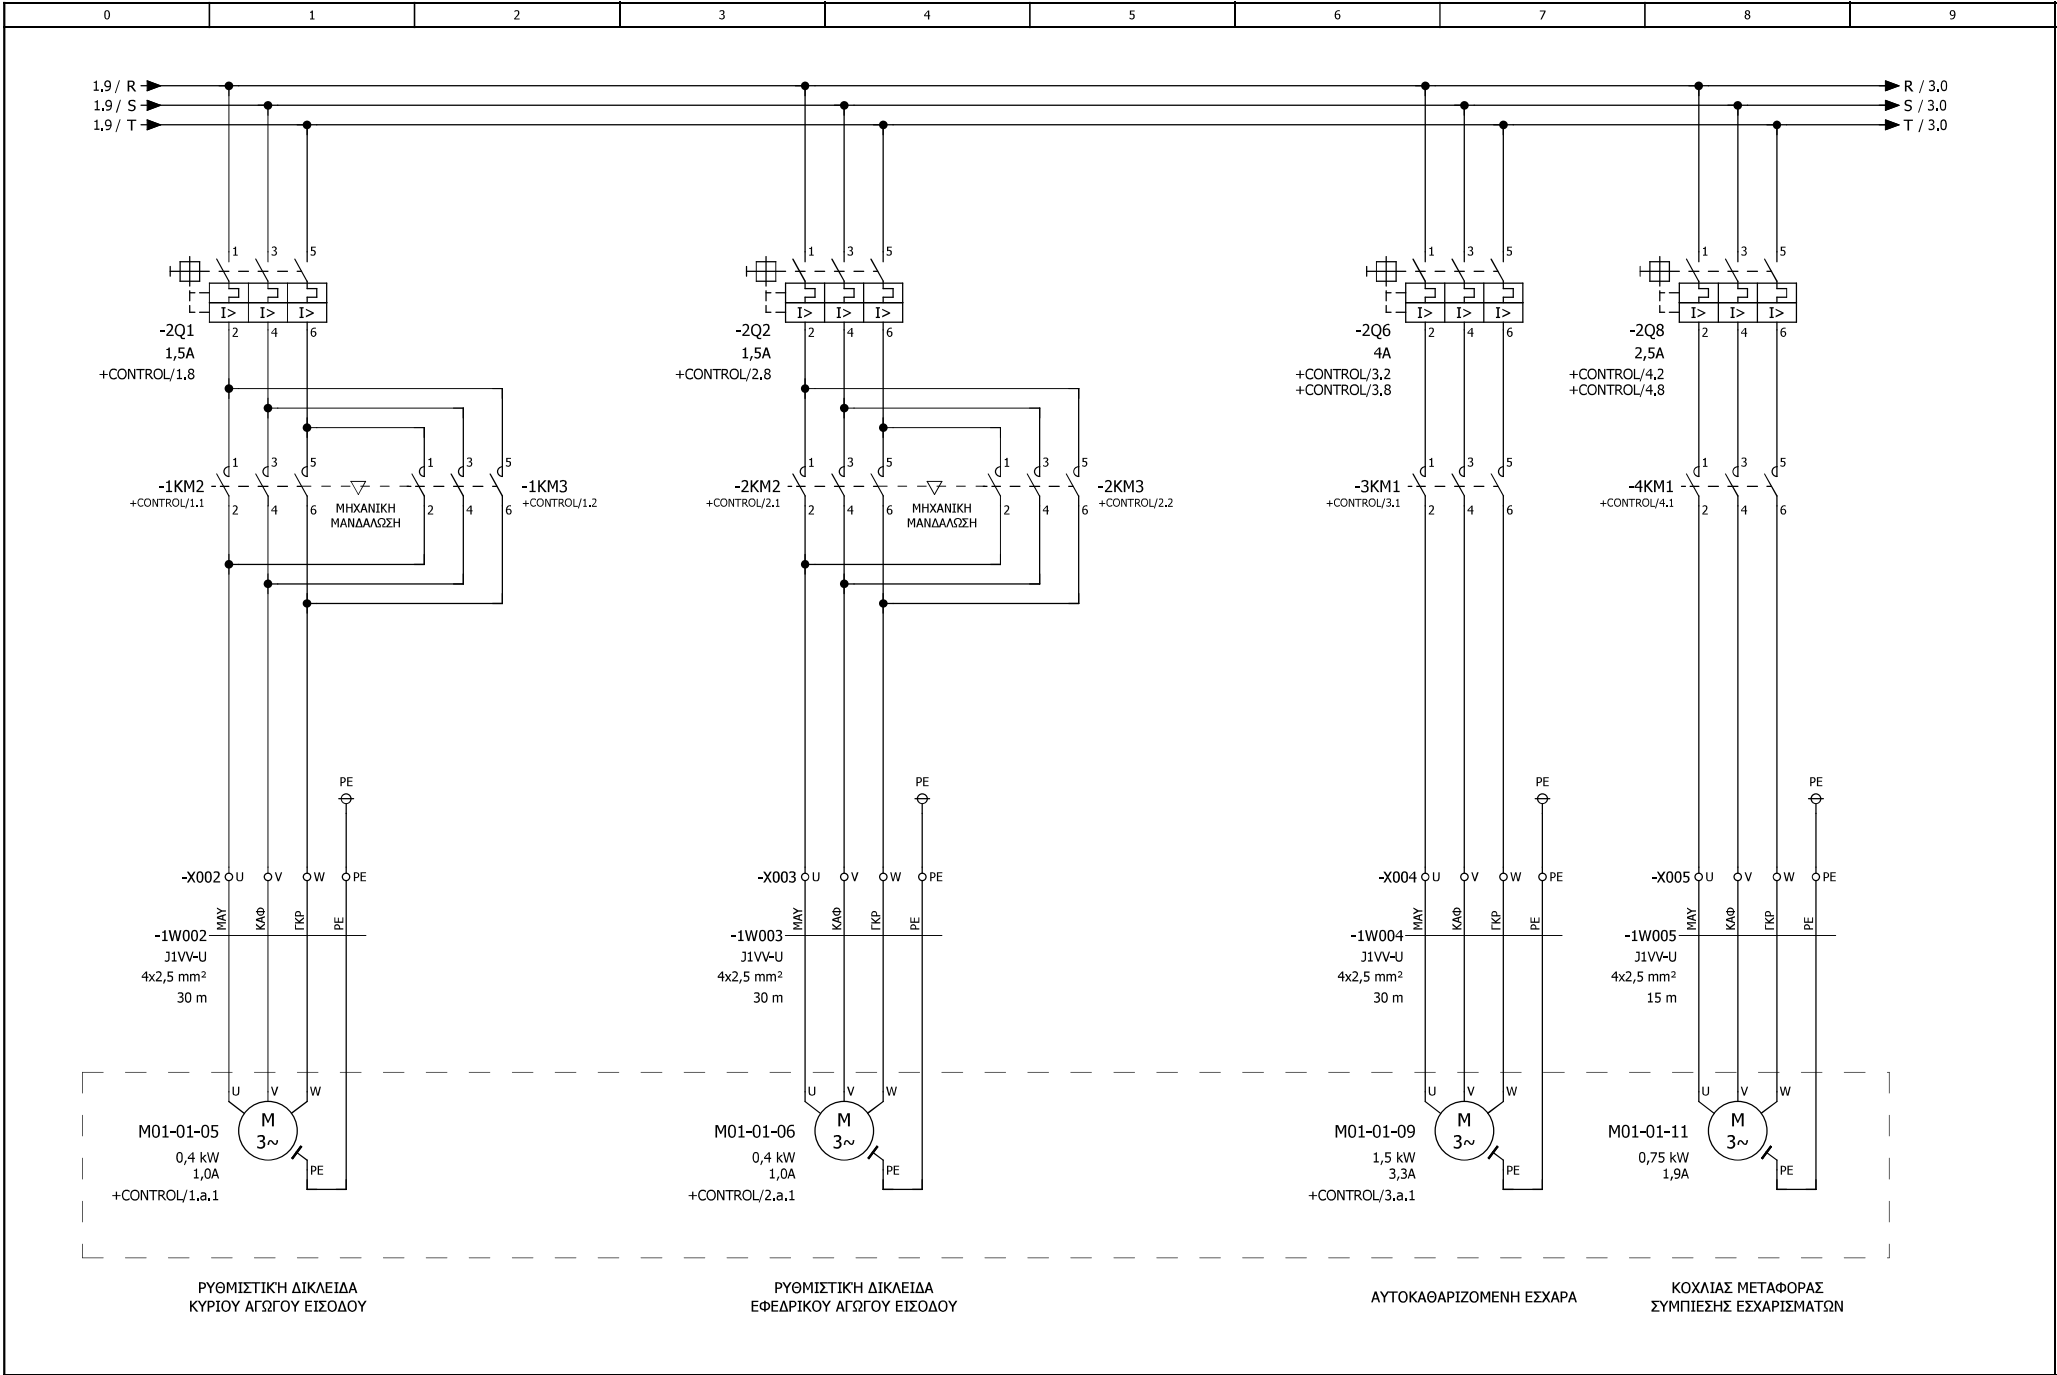

		ΗΜ/ΝΙΑ	19.09.2019	ΑΡ. ΣΧΕΔΙΟΥ	: ΕΡΓΟ ΑΝΑΒΑΘΜΙΣΗΣ ΚΑΙ ΕΠΕΚΤΑΣΗΣ ΤΗΣ	ΑΝΑΧΩΡΗΣΕΙΣ	= MCC-01
		ΜΕΛΕΤΗ		ΕΡΓΟ	: ΕΓΚΑΤΑΣΤΑΣΗΣ ΕΠΕΞΕΡΓΑΣΙΑΣ ΛΥΜΑΤΩΝ (ΕΕΛ)		+ MAIN
09.04.2019		ΣΧΕΔΙΟ		ΠΕΛΑΤΗΣ	: ΑΓΙΟΥ ΝΙΚΟΛΑΟΥ		ΦΥΛΛΟ: 2
ΑΛΛΑΓΗ	ΗΜ/ΝΙΑ	ΟΝΟΜΑ	ΘΕΩΡ.	ΠΕΡΙΓΡΑΦΗ ΠΙΝΑΚΑ	: ΠΙΝΑΚΑΣ ΕΡΓΩΝ ΕΙΣΟΔΟΥ		ΤΕΛ. ΦΥΛΛΟ: 16

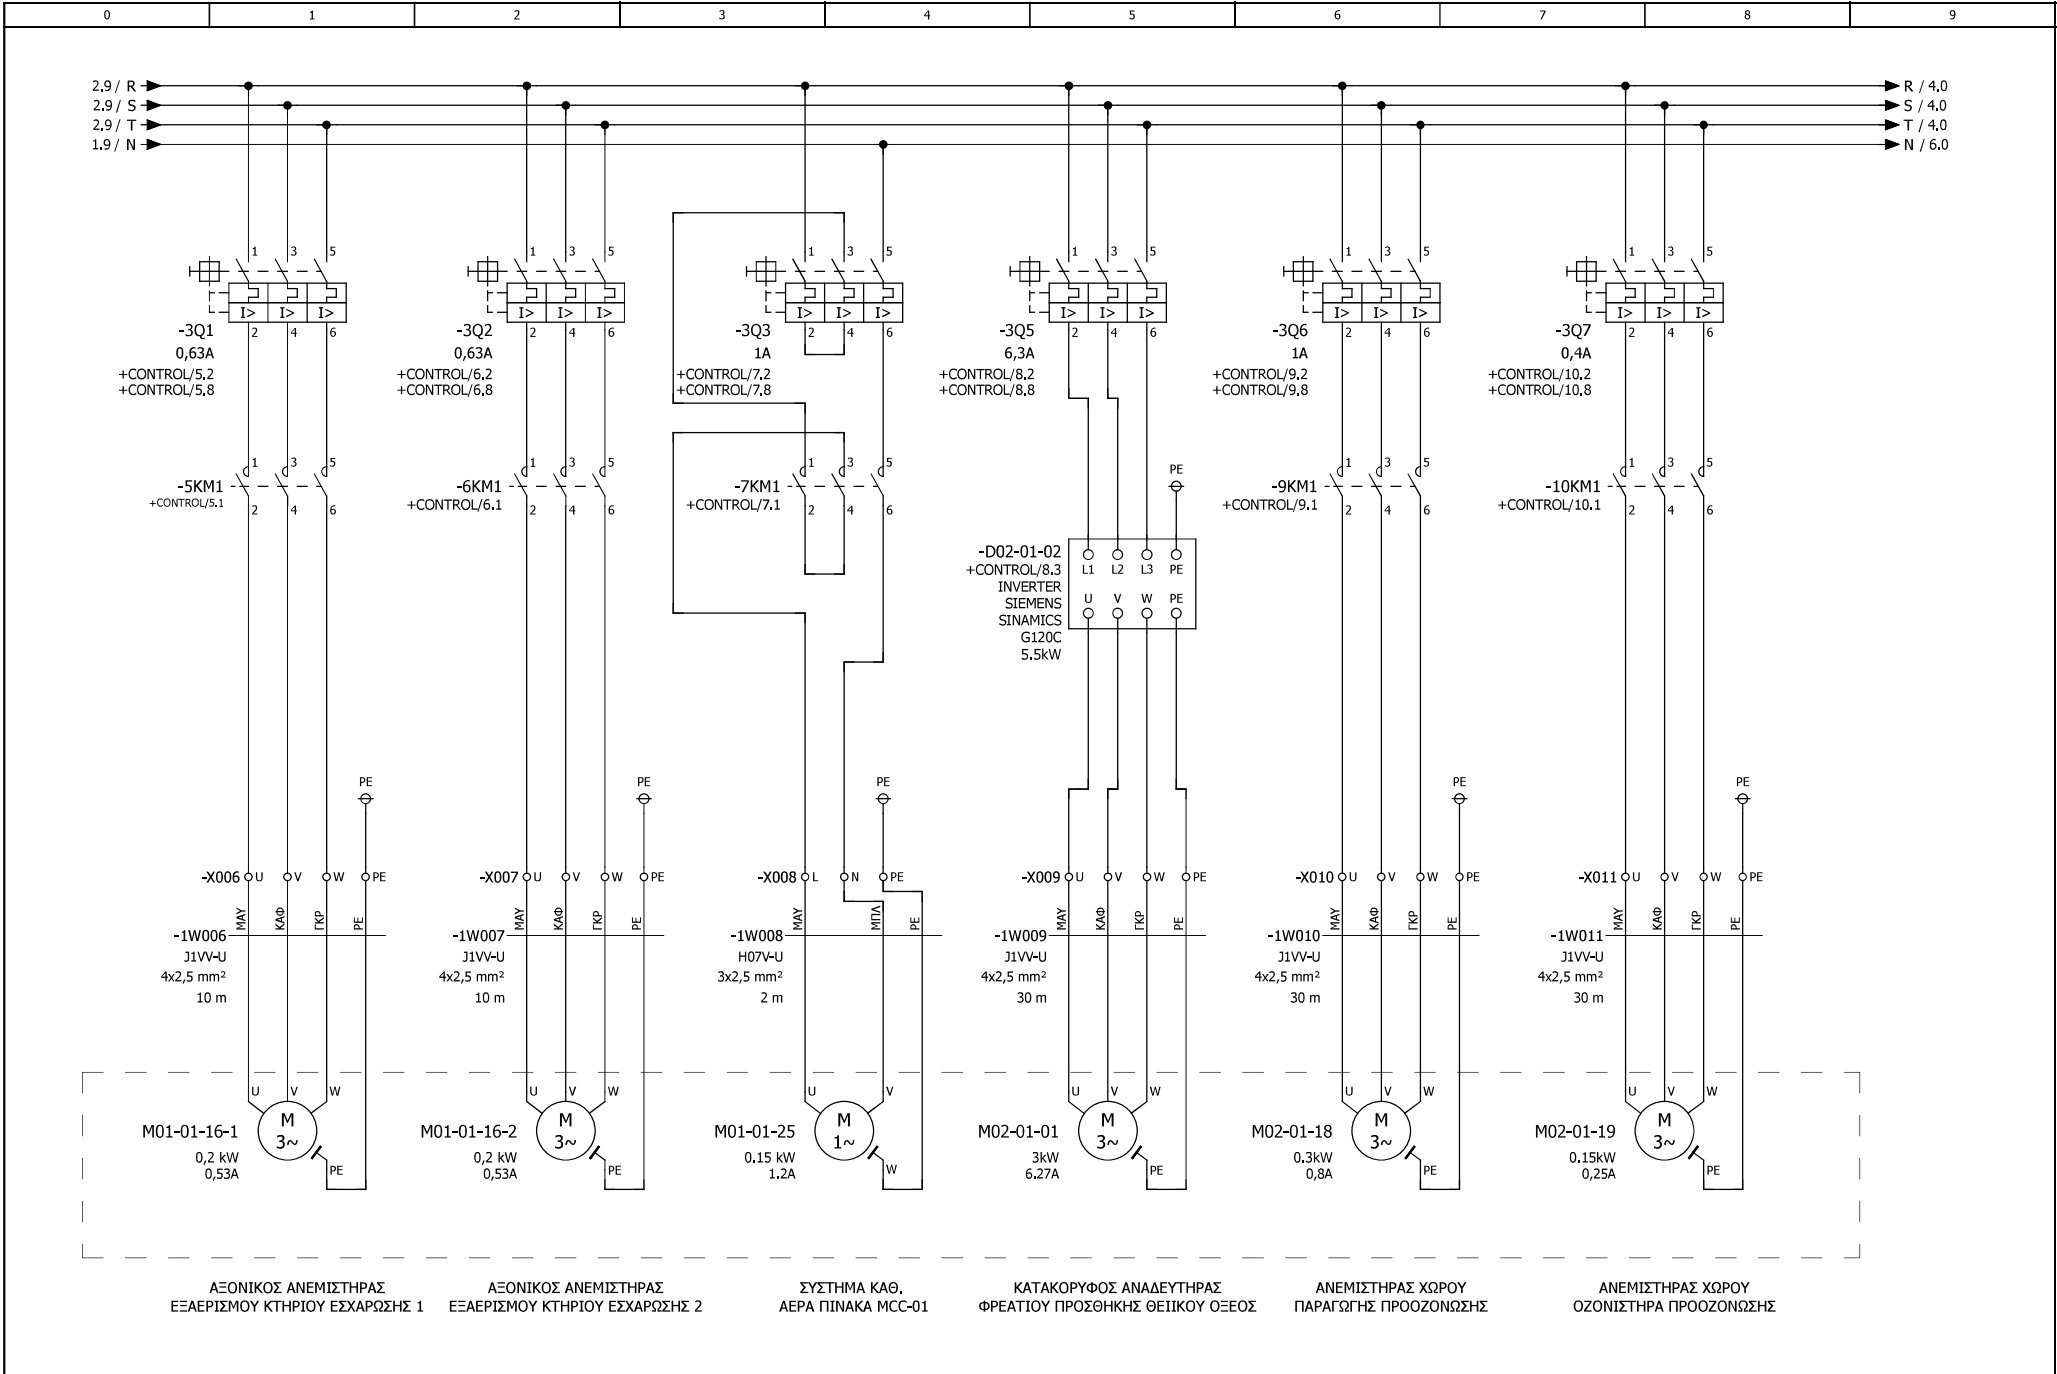


		ΗΜ/ΝΙΑ	19.09.2019	ΑΡ. ΣΧΕΔΙΟΥ	: ΕΡΓΟ ΑΝΑΒΑΘΜΙΣΗΣ ΚΑΙ ΕΠΕΚΤΑΣΗΣ ΤΗΣ	ΑΝΑΧΩΡΗΣΕΙΣ	= MCC-01
		ΜΕΛΕΤΗ		ΕΡΓΟ	: ΕΓΚΑΤΑΣΤΑΣΗΣ ΕΠΕΞΕΡΓΑΣΙΑΣ ΛΥΜΑΤΩΝ (ΕΕΛ)		+ MAIN
09.04.2019		ΣΧΕΔΙΟ		ΠΕΛΑΤΗΣ	: ΑΓΙΟΥ ΝΙΚΟΛΑΟΥ		ΦΥΛΛΟ: 3
ΑΛΛΑΓΗ	ΗΜ/ΝΙΑ	ΟΝΟΜΑ	ΘΕΩΡ.	ΠΕΡΙΓΡΑΦΗ ΠΙΝΑΚΑ	: ΠΙΝΑΚΑΣ ΕΡΓΩΝ ΕΙΣΟΔΟΥ		ΤΕΛ. ΦΥΛΛΟ: 16

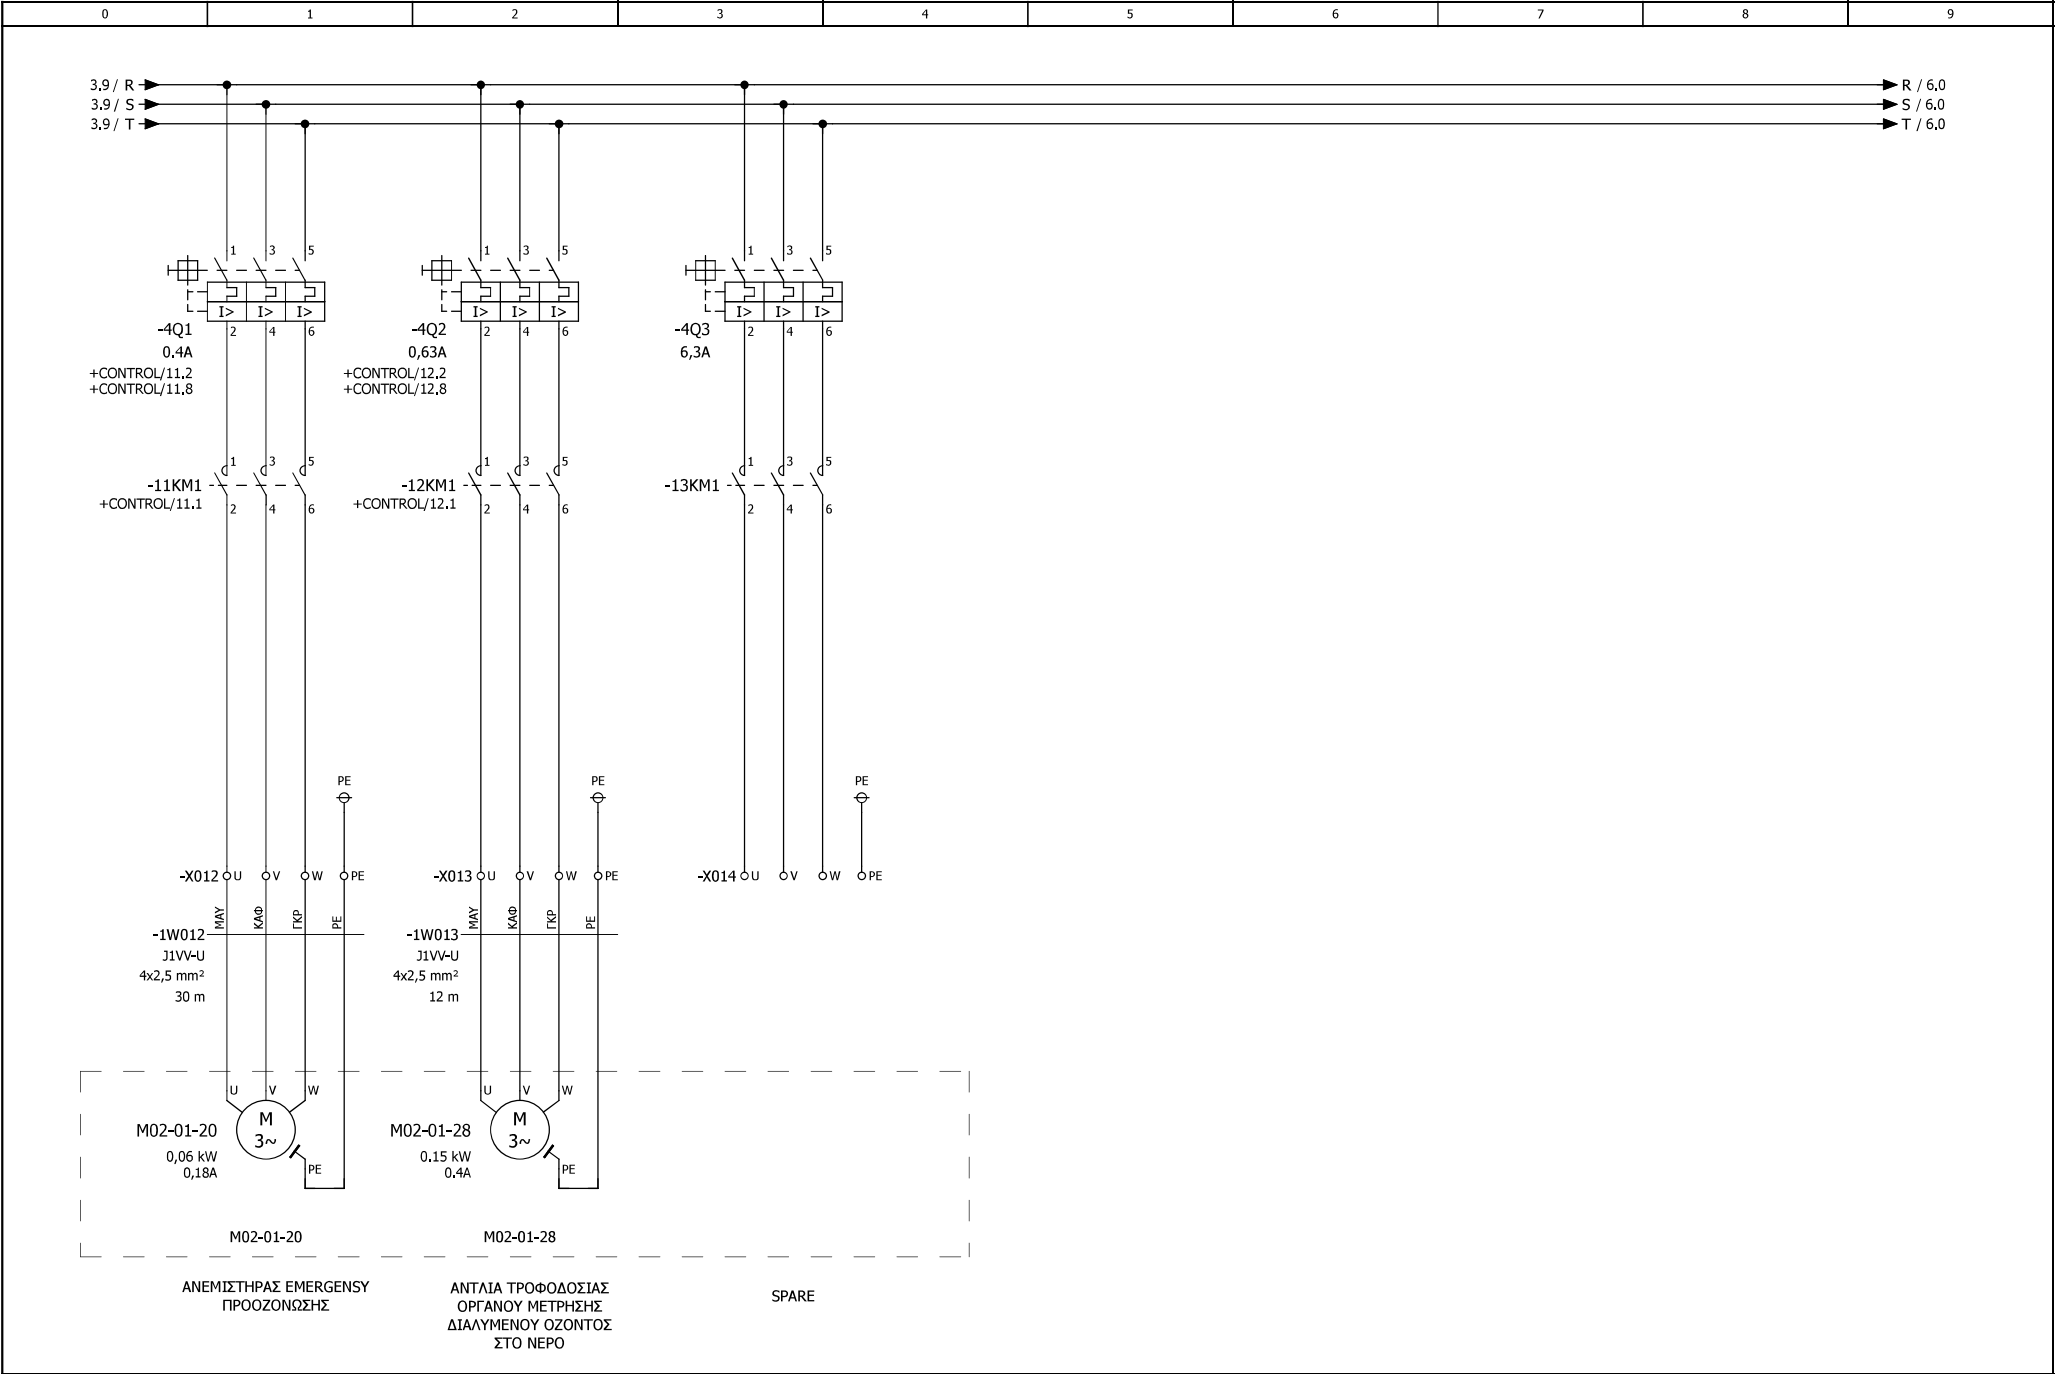


		ΗΜ/ΝΙΑ	19.09.2019	ΑΡ. ΣΧΕΔΙΟΥ	ΕΡΓΟ ΑΝΑΒΑΘΜΙΣΗΣ ΚΑΙ ΕΠΕΚΤΑΣΗΣ ΤΗΣ	ΑΝΑΧΩΡΗΣΕΙΣ	= MCC-01
		ΜΕΛΕΤΗ		ΕΡΓΟ	ΕΓΚΑΤΑΣΤΑΣΗΣ ΕΠΕΞΕΡΓΑΣΙΑΣ ΛΥΜΑΤΩΝ (ΕΕΛ)		+ MAIN
09.04.2019		ΣΧΕΔΙΟ		ΠΕΛΑΤΗΣ	ΑΓΙΟΥ ΝΙΚΟΛΑΟΥ		ΦΥΛΛΟ: 4
ΑΛΛΑΓΗ	ΗΜ/ΝΙΑ	ΟΝΟΜΑ	ΘΕΩΡ.	ΠΕΡΙΓΡΑΦΗ ΠΙΝΑΚΑ	ΠΙΝΑΚΑΣ ΕΡΓΩΝ ΕΙΣΟΔΟΥ		ΤΕΛ. ΦΥΛΛΟ: 16


0	1	2	3	4	5	6	7	8	9
			ΗΜ/ΝΙΑ	19.09.2019		ΑΡ. ΣΧΕΔΙΟΥ : ΕΡΓΟ ΑΝΑΒΑΘΜΙΣΗΣ ΚΑΙ ΕΠΕΚΤΑΣΗΣ ΤΗΣ ΕΡΓΟ : ΕΓΚΑΤΑΣΤΑΣΗΣ ΕΠΕΞΕΡΓΑΣΙΑΣ ΛΥΜΑΤΩΝ (ΕΕΛ) ΠΕΛΑΤΗΣ : ΑΓΙΟΥ ΝΙΚΟΛΑΟΥ ΠΕΡΙΓΡΑΦΗ ΠΙΝΑΚΑ : ΠΙΝΑΚΑΣ ΕΡΓΩΝ ΕΙΣΟΔΟΥ	ΚΕΝΗ ΣΕΛΙΔΑ	= MCC-01	
			ΜΕΛΕΤΗ					+ ΜΑΙΝ	
	09.04.2019		ΣΧΕΔΙΟ					ΦΥΛΛΟ:	5
ΑΛΛΑΓΗ	ΗΜ/ΝΙΑ	ΟΝΟΜΑ	ΘΕΩΡ.					ΤΕΛ. ΦΥΛΛΟ:	16

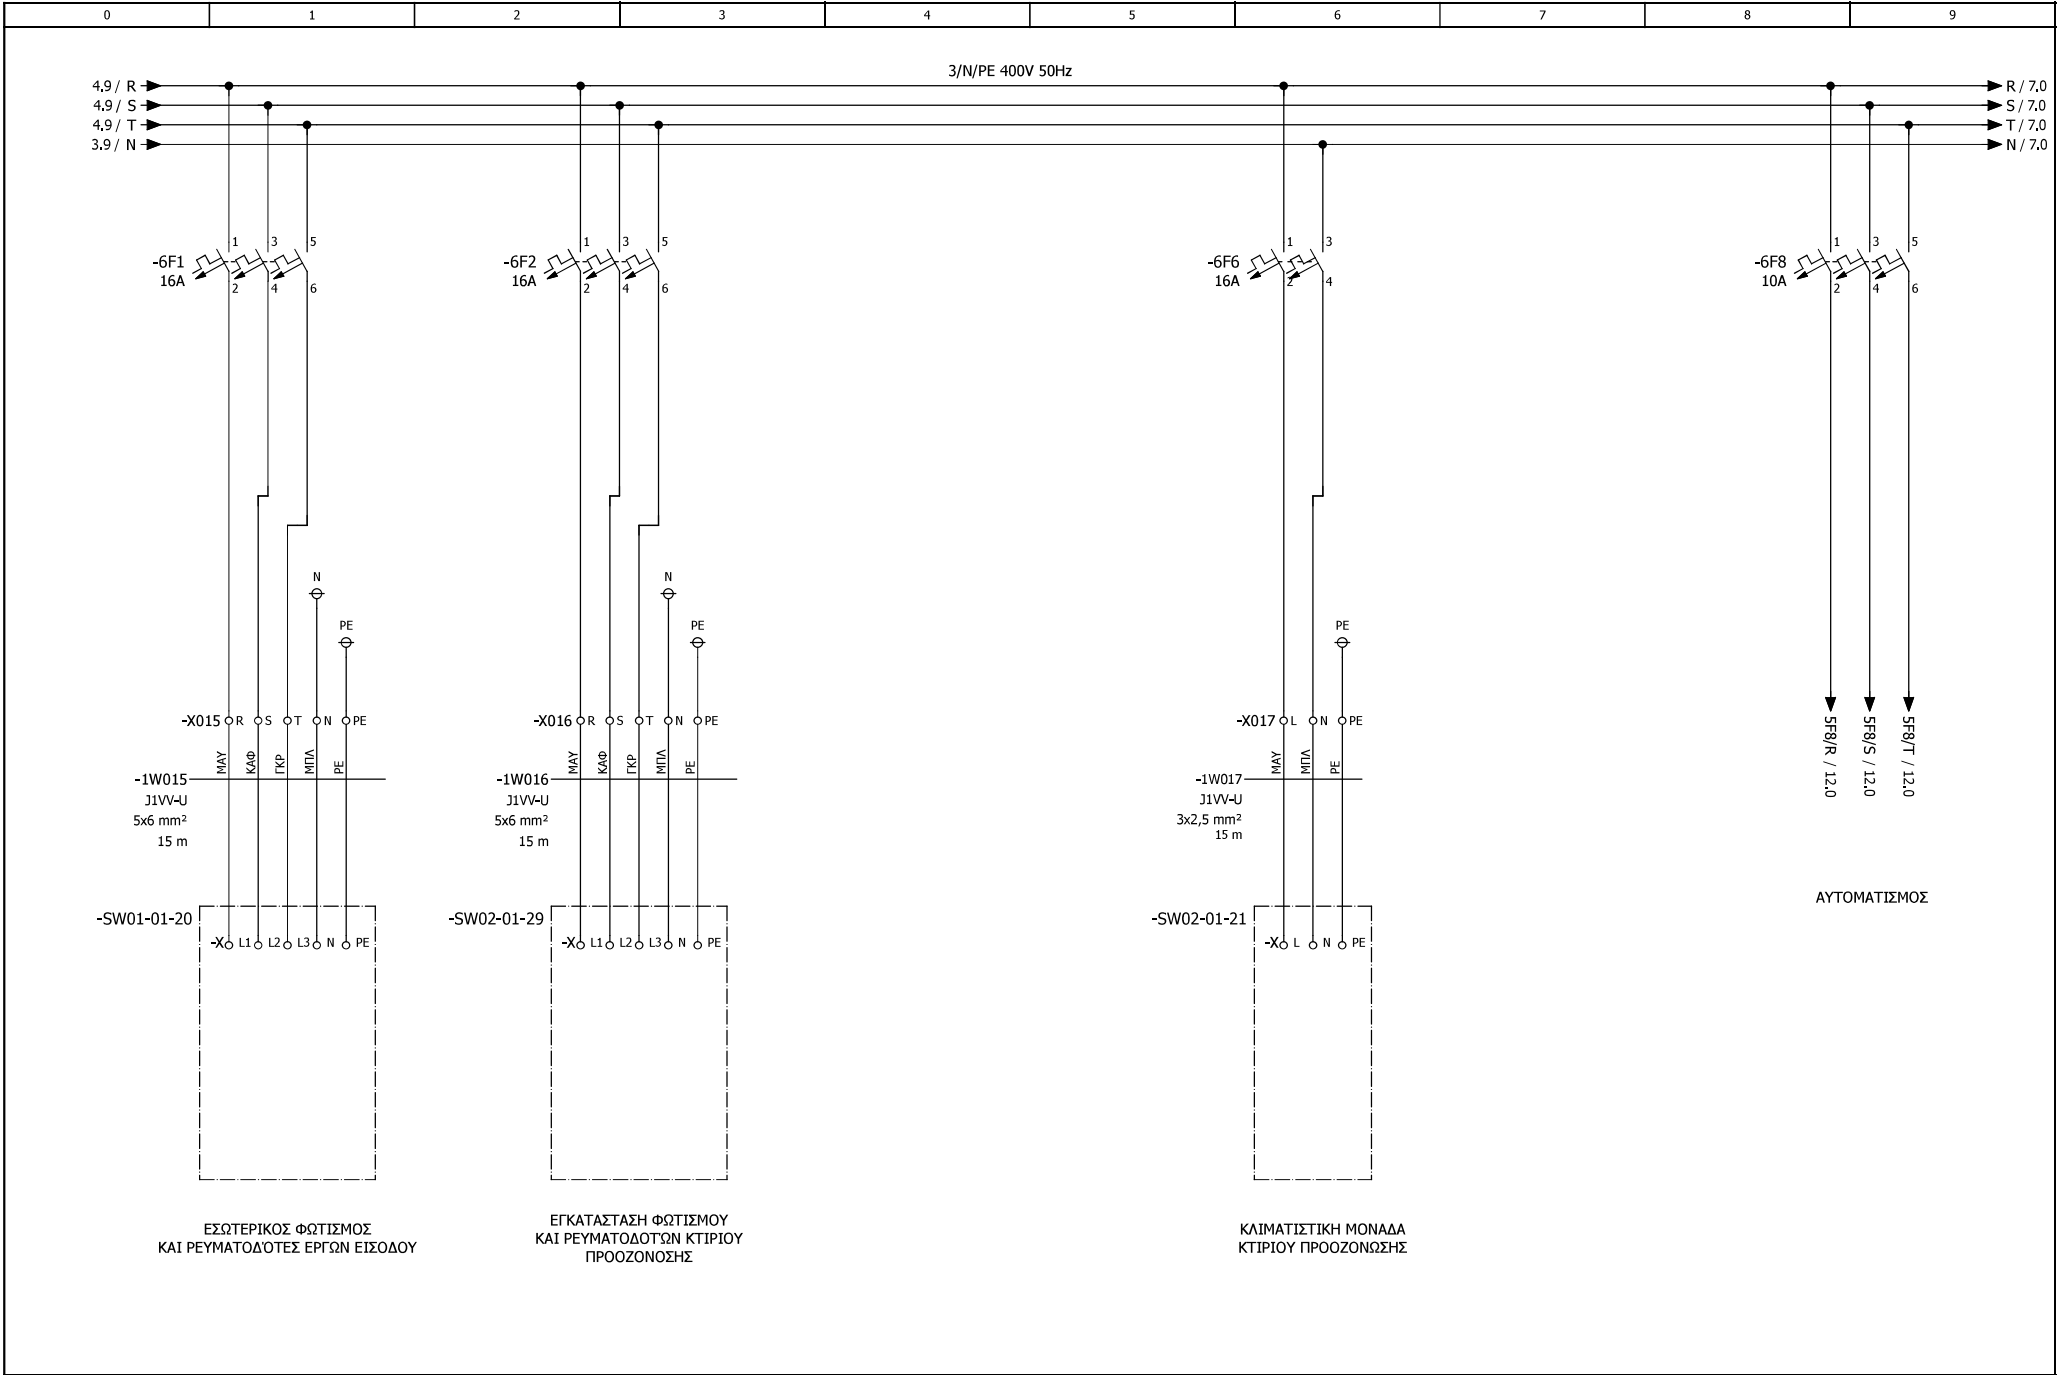


			ΗΜ/ΝΙΑ	19.09.2019		ΑΡ. ΣΧΕΔΙΟΥ	: ΕΡΓΟ ΑΝΑΒΑΘΜΙΣΗΣ ΚΑΙ ΕΠΕΚΤΑΣΗΣ ΤΗΣ	ΑΝΑΧΩΡΗΣΕΙΣ ΠΙΝΑΚΩΝ & ΑΥΤΟΜΑΤΙΣΜΟΥ	= MCC-01
			ΜΕΛΕΤΗ			ΕΡΓΟ	: ΕΓΚΑΤΑΣΤΑΣΗΣ ΕΠΕΞΕΡΓΑΣΙΑΣ ΛΥΜΑΤΩΝ (ΕΕΛ)		+ MAIN
	09.04.2019		ΣΧΕΔΙΟ			ΠΕΛΑΤΗΣ	: ΑΓΙΟΥ ΝΙΚΟΛΑΟΥ		ΦΥΛΛΟ: 6
ΑΛΛΑΓΗ	ΗΜ/ΝΙΑ	ΟΝΟΜΑ	ΘΕΩΡ.			ΠΕΡΙΓΡΑΦΗ ΠΙΝΑΚΑ	: ΠΙΝΑΚΑΣ ΕΡΓΩΝ ΕΙΣΟΔΟΥ		ΤΕΛ. ΦΥΛΛΟ: 16

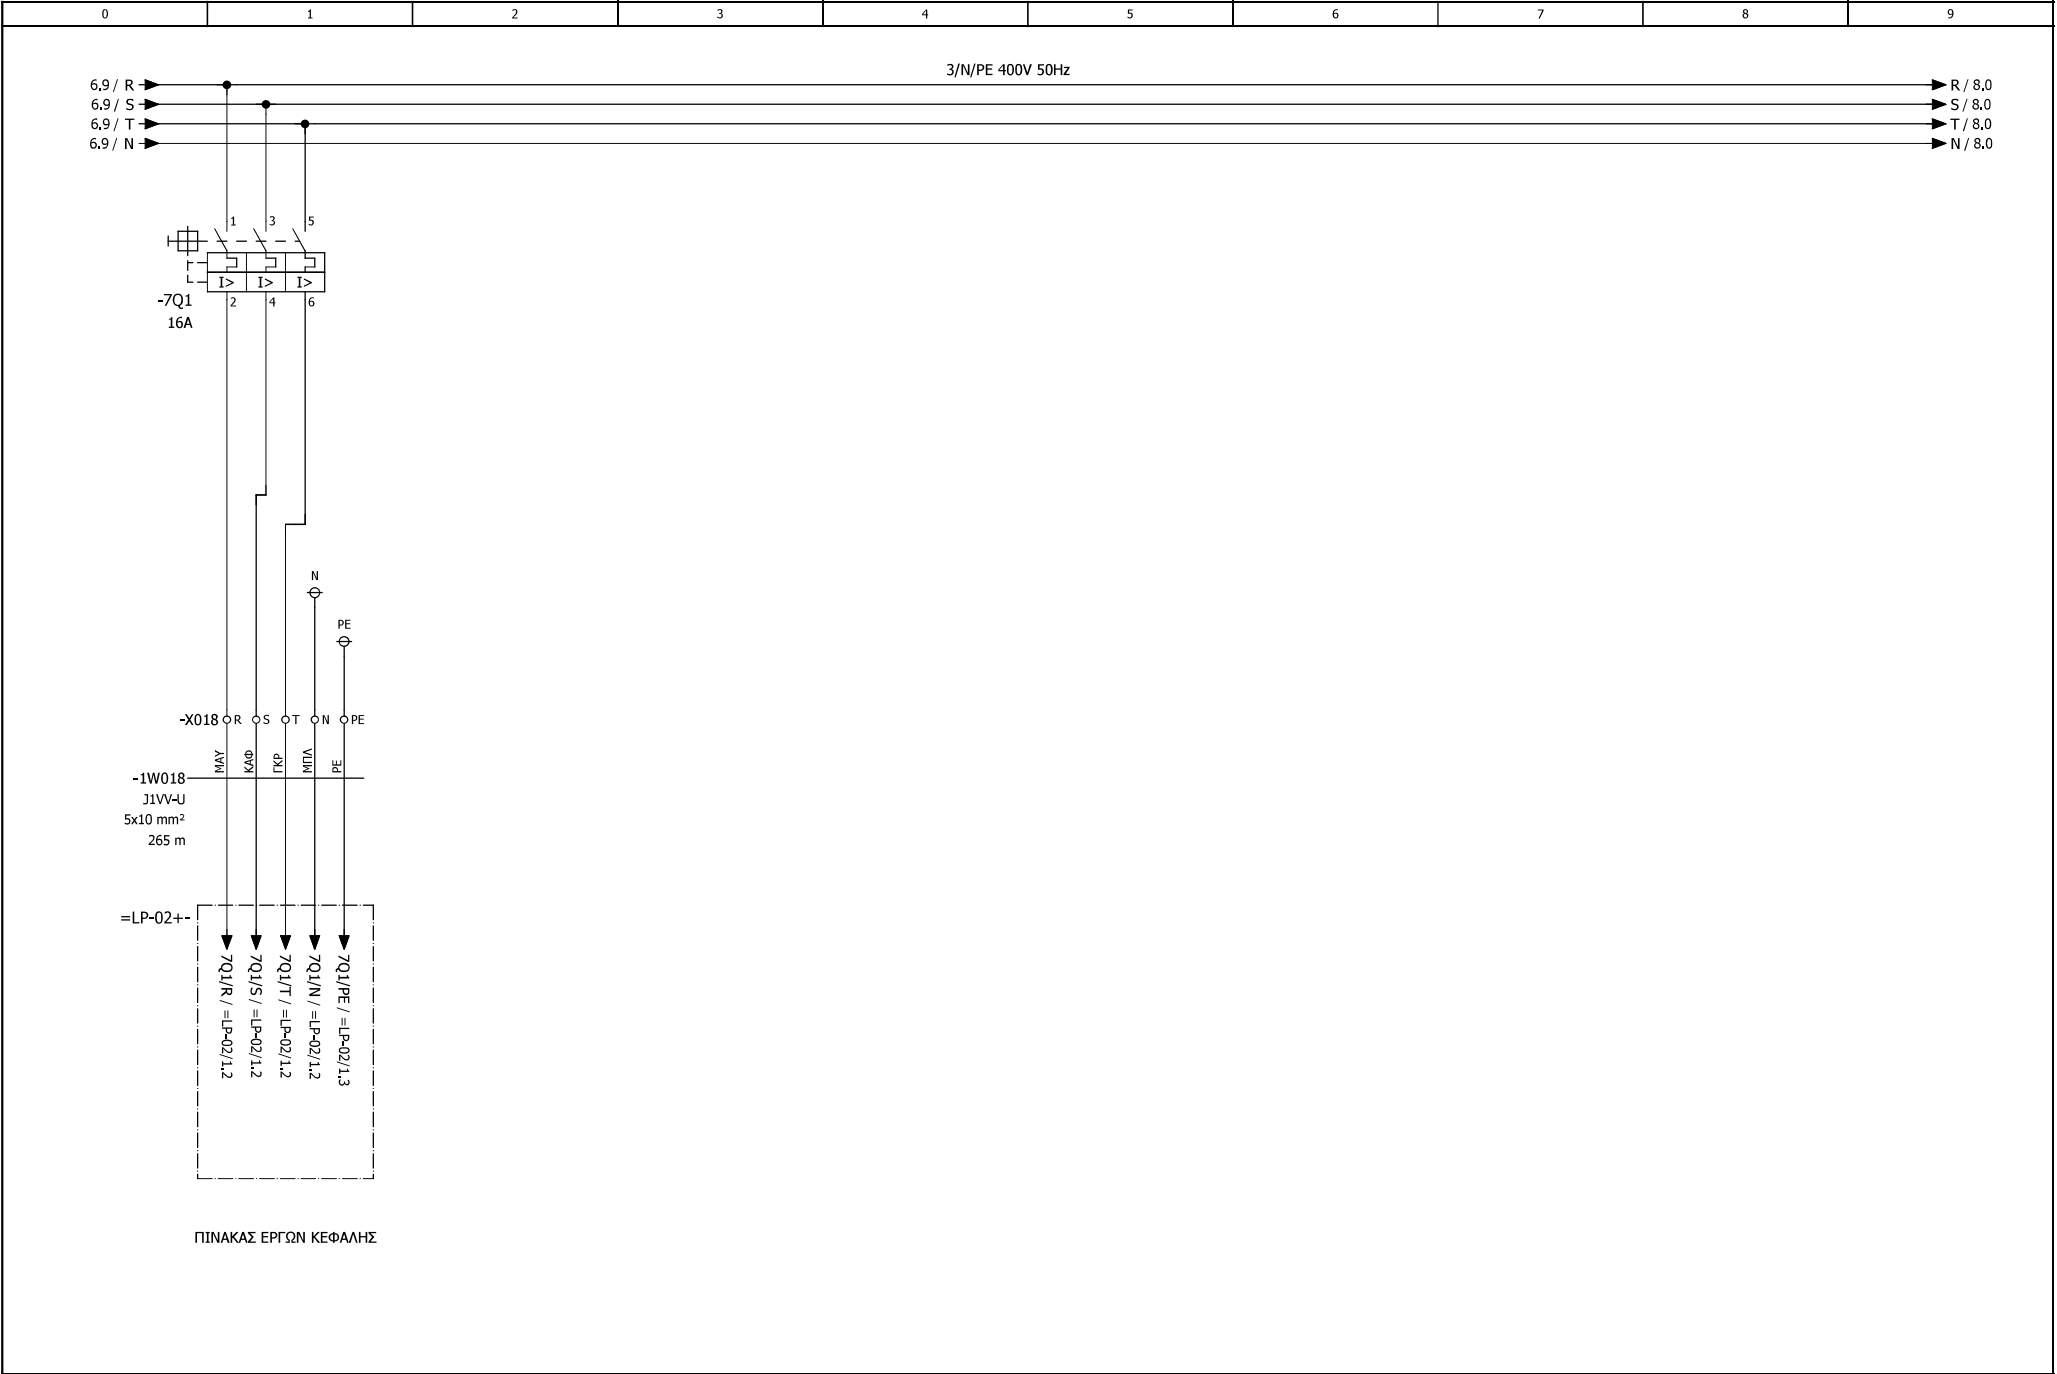



			ΗΜ/ΝΙΑ	19.09.2019	ΑΡ. ΣΧΕΔΙΟΥ : ΕΡΓΟ ΑΝΑΒΑΘΜΙΣΗΣ ΚΑΙ ΕΠΕΚΤΑΣΗΣ ΤΗΣ ΕΡΓΟ : ΕΓΚΑΤΑΣΤΑΣΗΣ ΕΠΕΞΕΡΓΑΣΙΑΣ ΛΥΜΑΤΩΝ (ΕΕΛ) ΠΕΛΑΤΗΣ : ΑΓΙΟΥ ΝΙΚΟΛΑΟΥ ΠΕΡΙΓΡΑΦΗ ΠΙΝΑΚΑ : ΠΙΝΑΚΑΣ ΕΡΓΩΝ ΕΙΣΟΔΟΥ	ΑΝΑΧΩΡΗΣΕΙΣ ΠΙΝΑΚΩΝ	=	MCC-01
			ΜΕΛΕΤΗ				+	ΜΑΙΝ
	09.04.2019		ΣΧΕΔΙΟ				ΦΥΛΛΟ:	7
ΑΛΛΑΓΗ	ΗΜ/ΝΙΑ	ΟΝΟΜΑ	ΘΕΩΡ.				ΤΕΛ. ΦΥΛΛΟ:	16

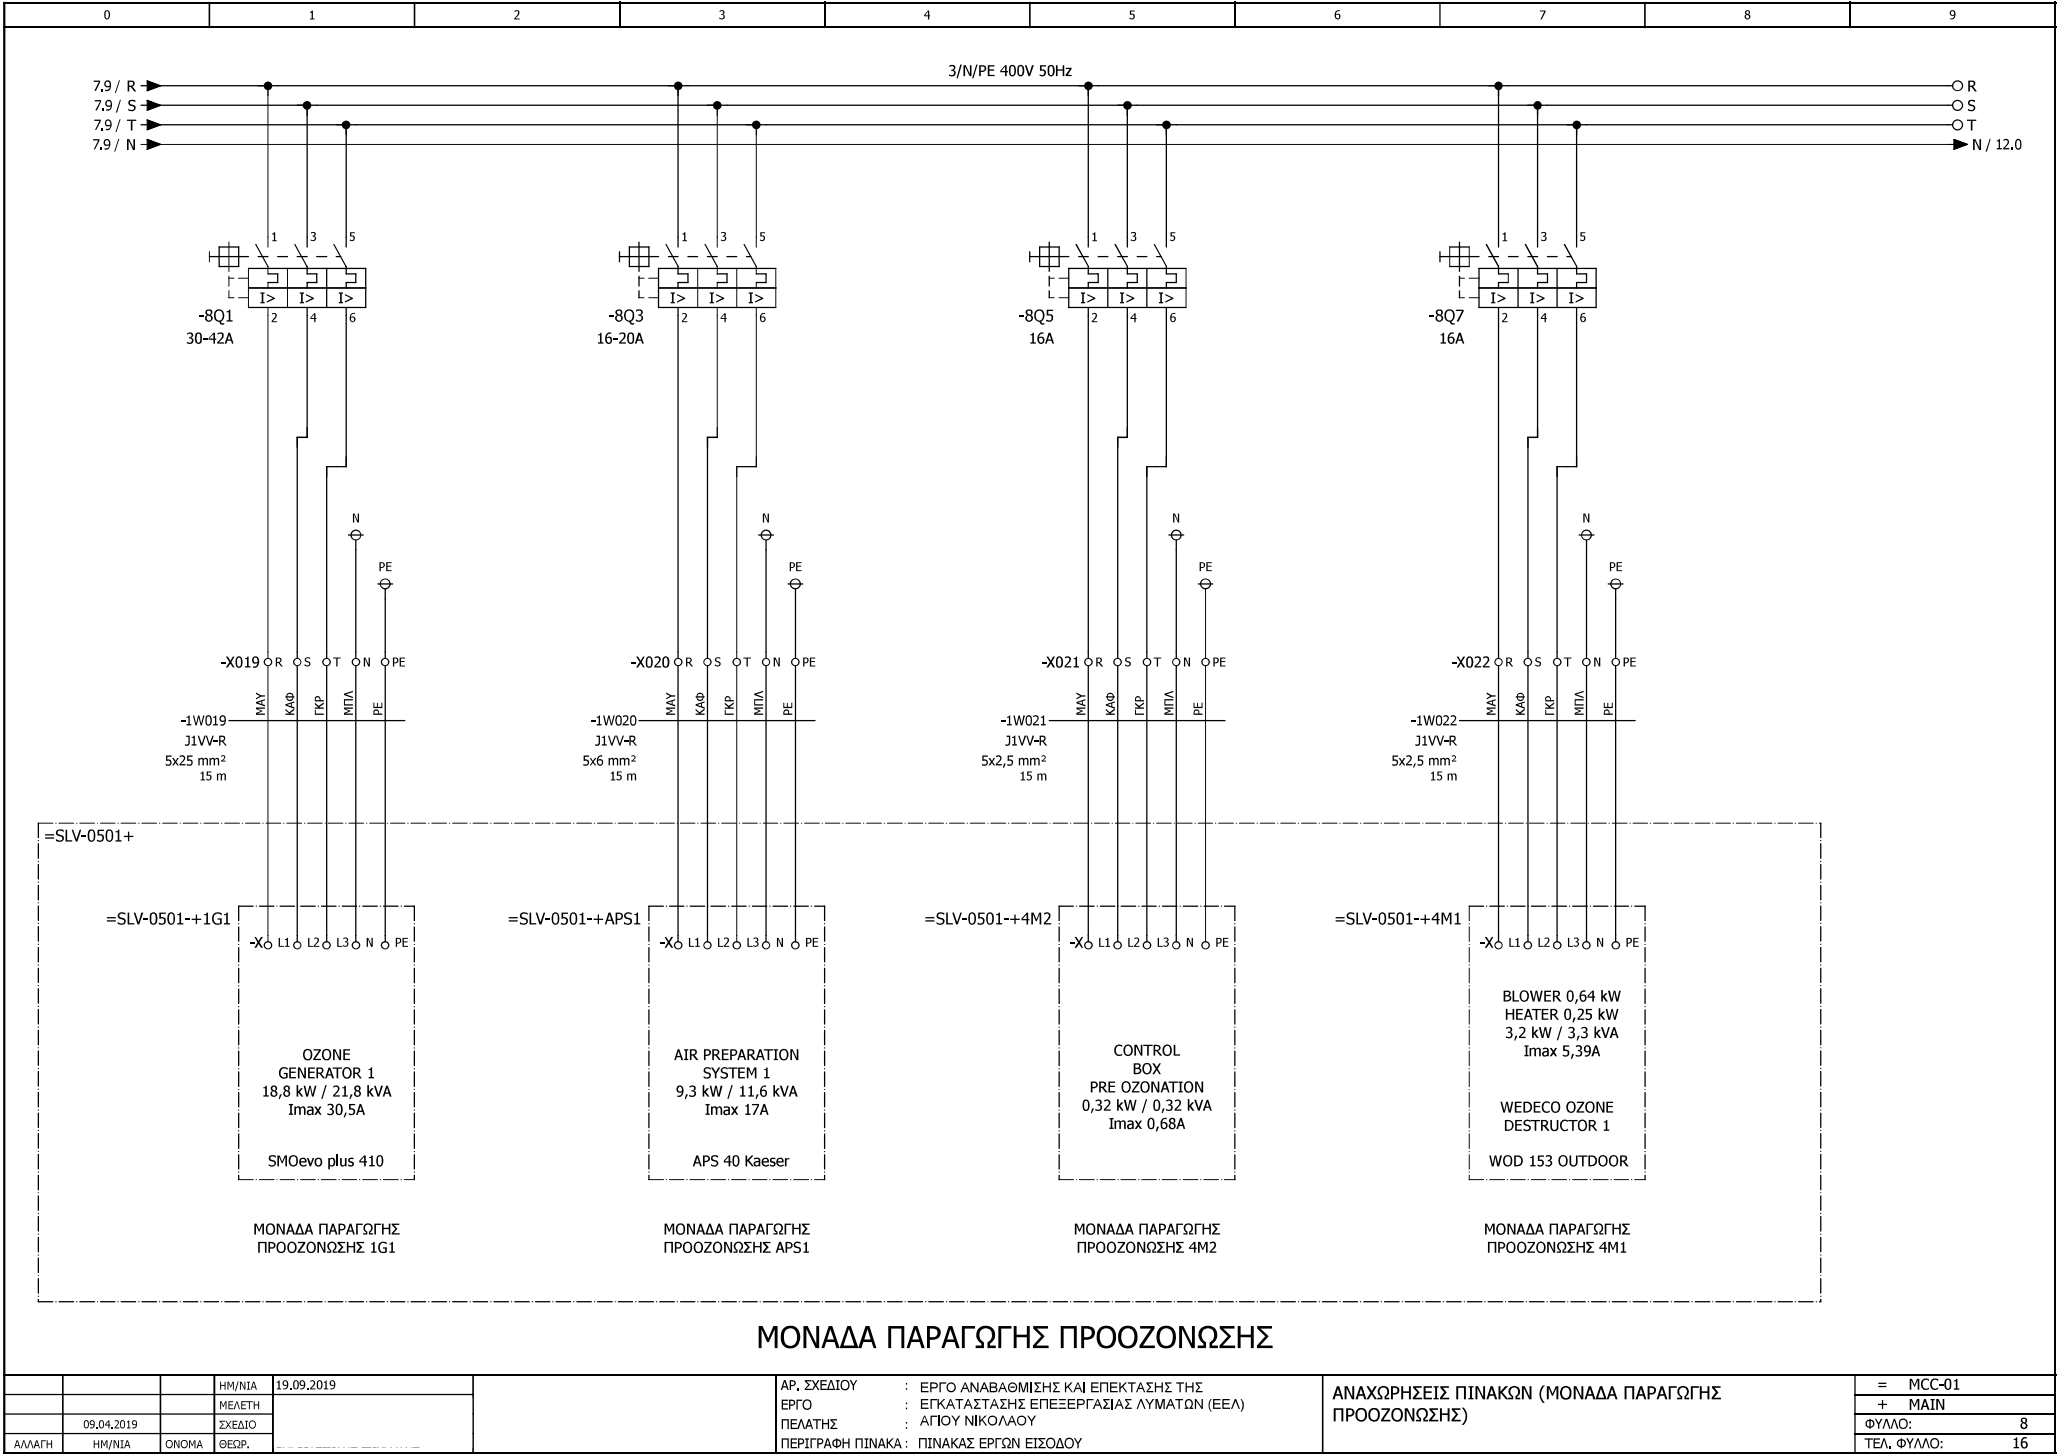

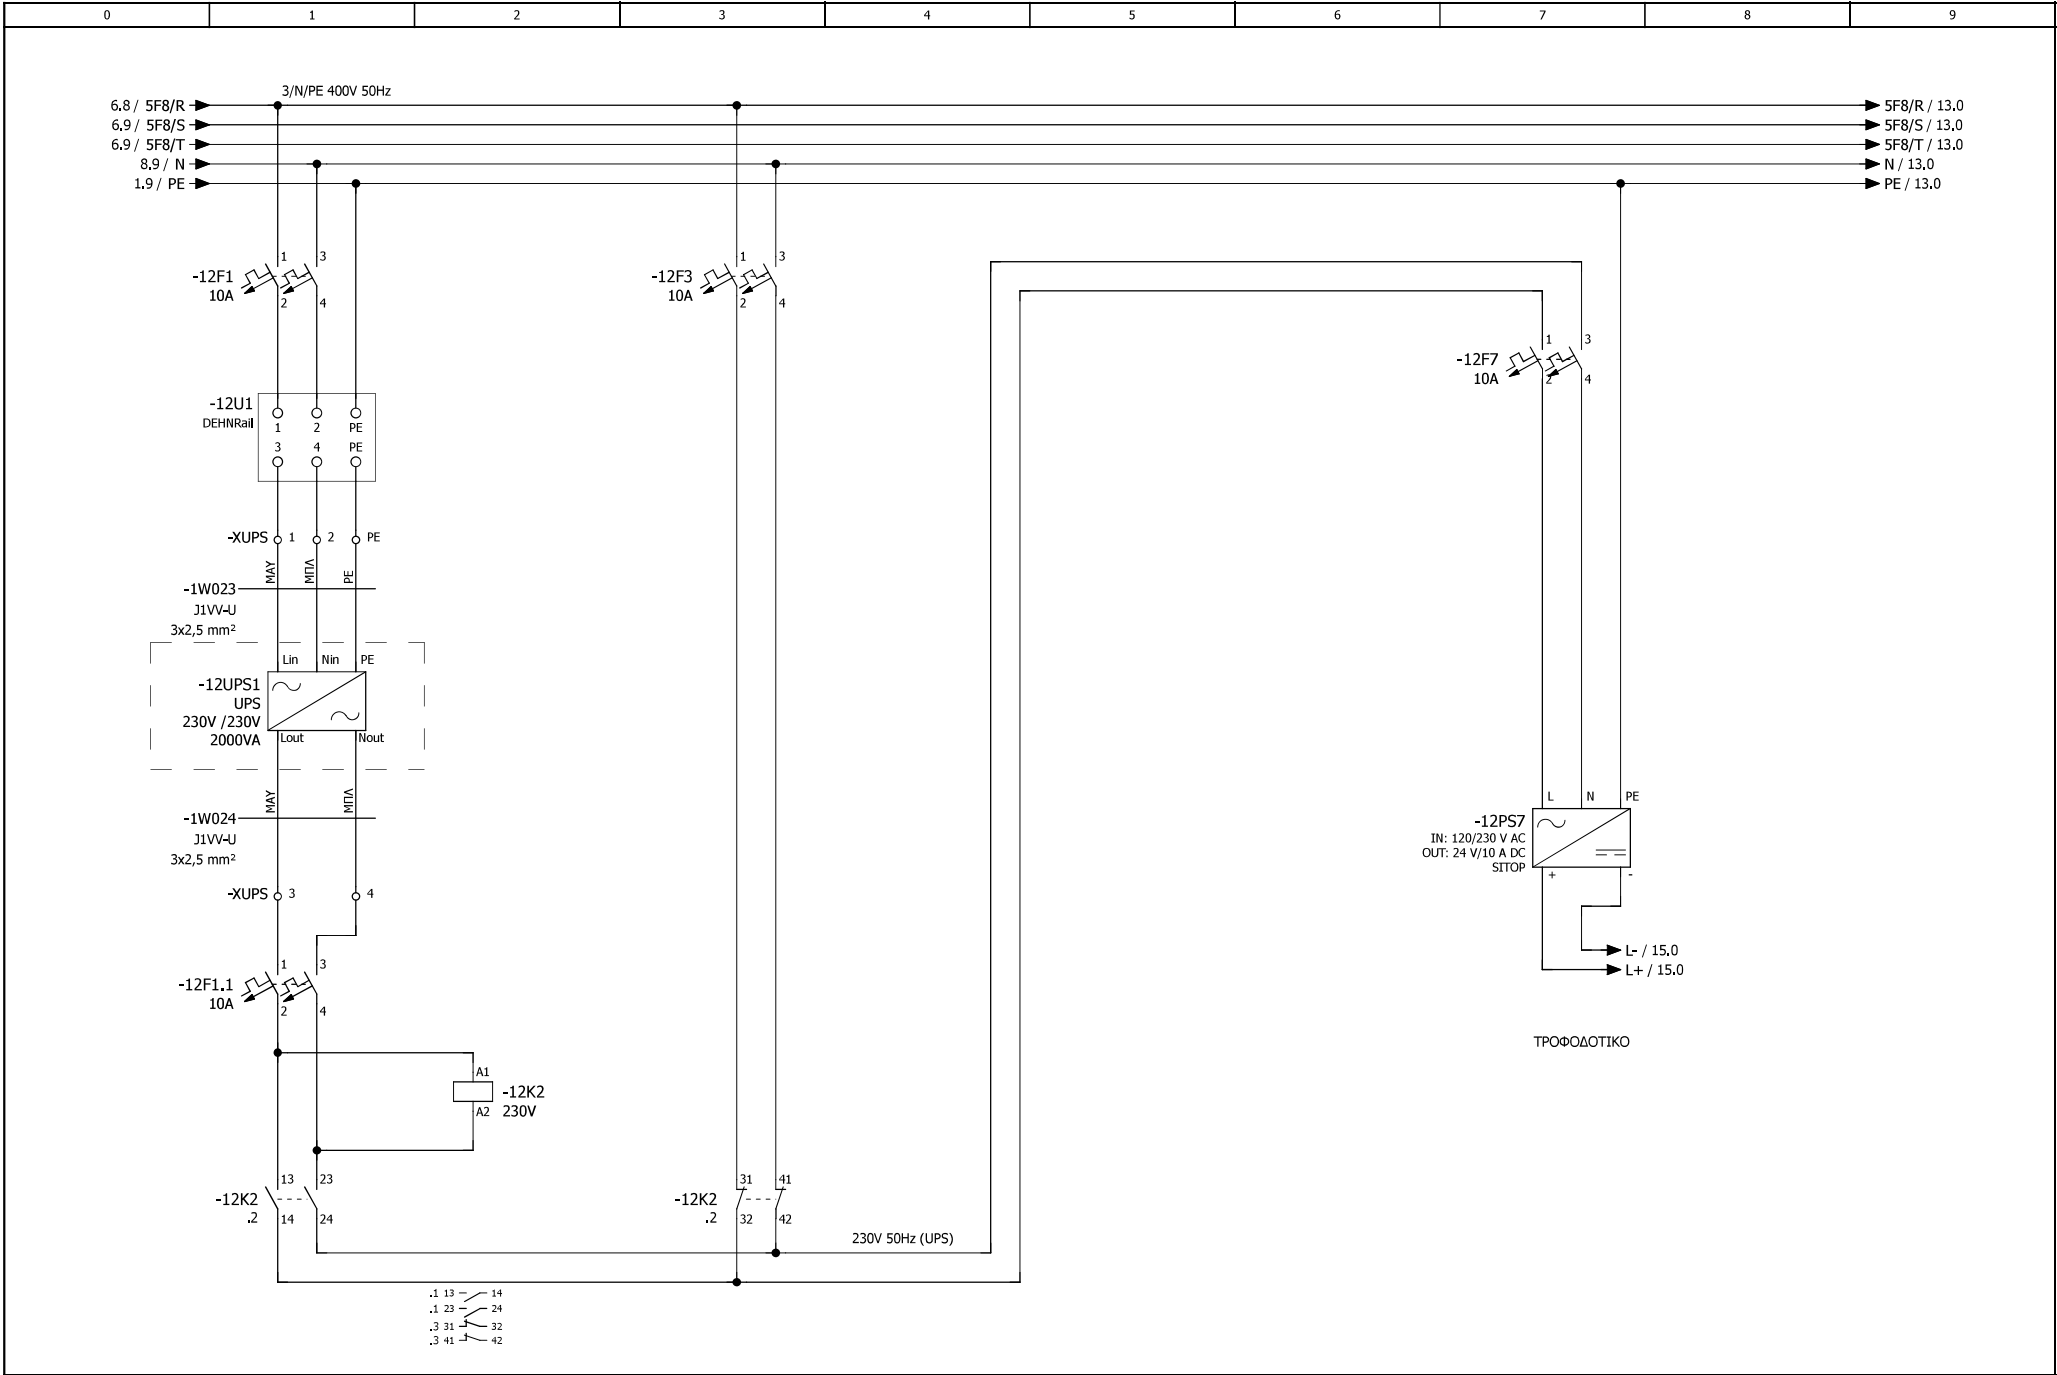


			ΗΜ/ΝΙΑ	19.09.2019	ΑΡ. ΣΧΕΔΙΟΥ	ΕΡΓΟ ΑΝΑΒΑΘΜΙΣΗΣ ΚΑΙ ΕΠΕΚΤΑΣΗΣ ΤΗΣ	UPS	=	MCC-01
			ΜΕΛΕΤΗ		ΕΡΓΟ	: ΕΓΚΑΤΑΣΤΑΣΗΣ ΕΠΕΞΕΡΓΑΣΙΑΣ ΛΥΜΑΤΩΝ (ΕΕΛ)		+	MAIN
09.04.2019			ΣΧΕΔΙΟ		ΠΕΛΑΤΗΣ	: ΑΓΙΟΥ ΝΙΚΟΛΑΟΥ		ΦΥΛΛΟ:	12
ΑΛΛΑΓΗ	ΗΜ/ΝΙΑ	ΟΝΟΜΑ	ΘΕΩΡ.		ΠΕΡΙΓΡΑΦΗ ΠΙΝΑΚΑ	: ΠΙΝΑΚΑΣ ΕΡΓΩΝ ΕΙΣΟΔΟΥ		ΤΕΛ. ΦΥΛΛΟ:	16

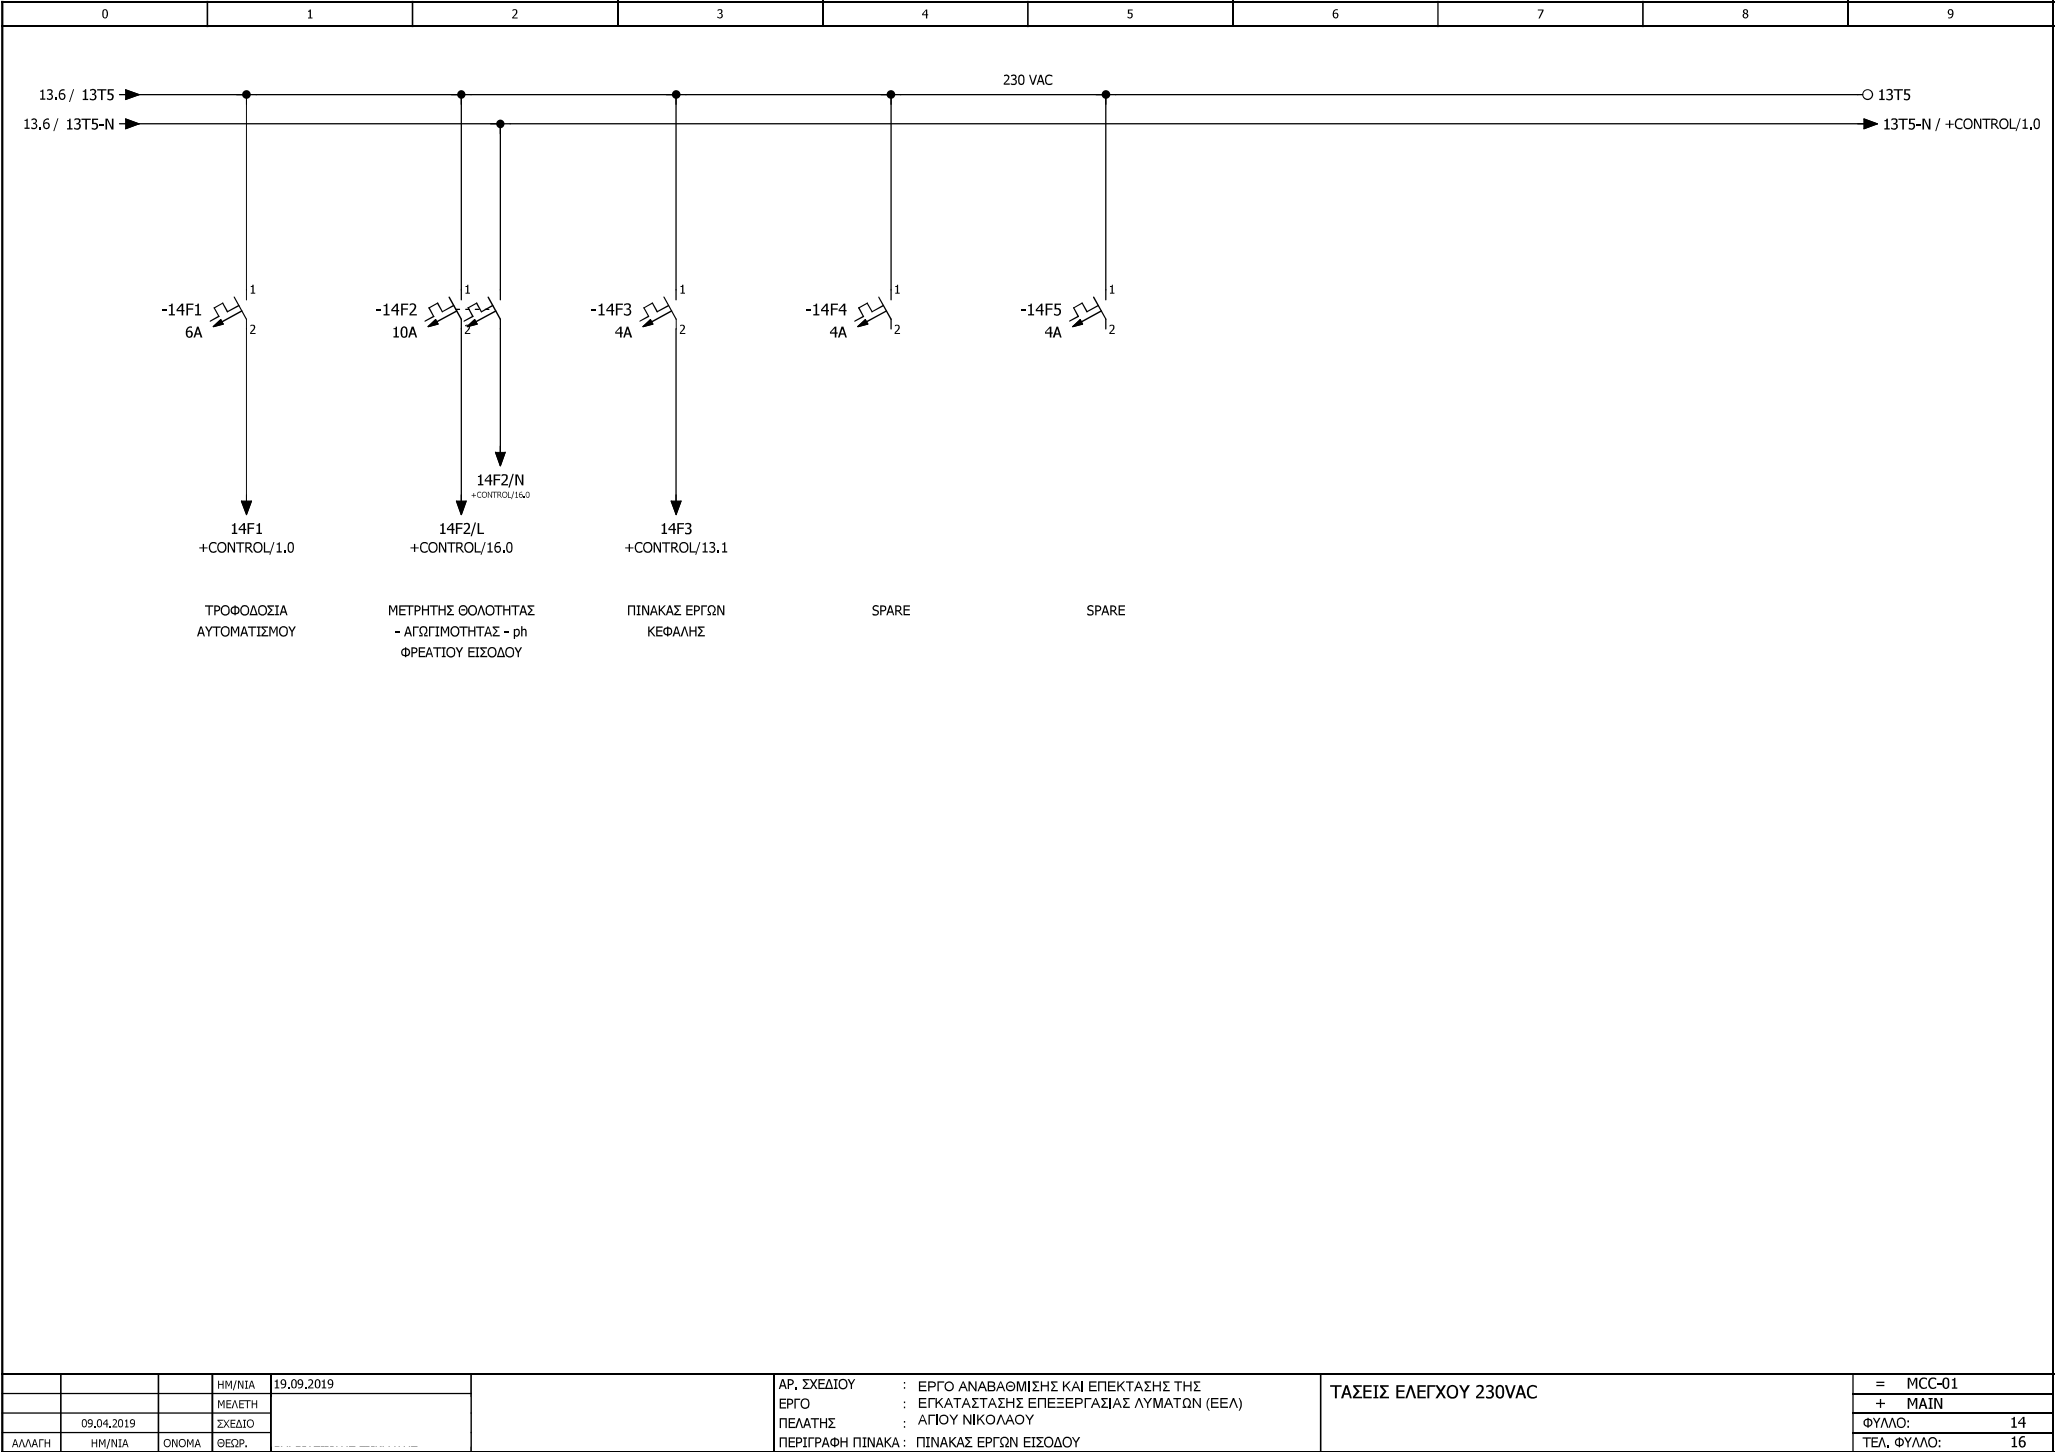


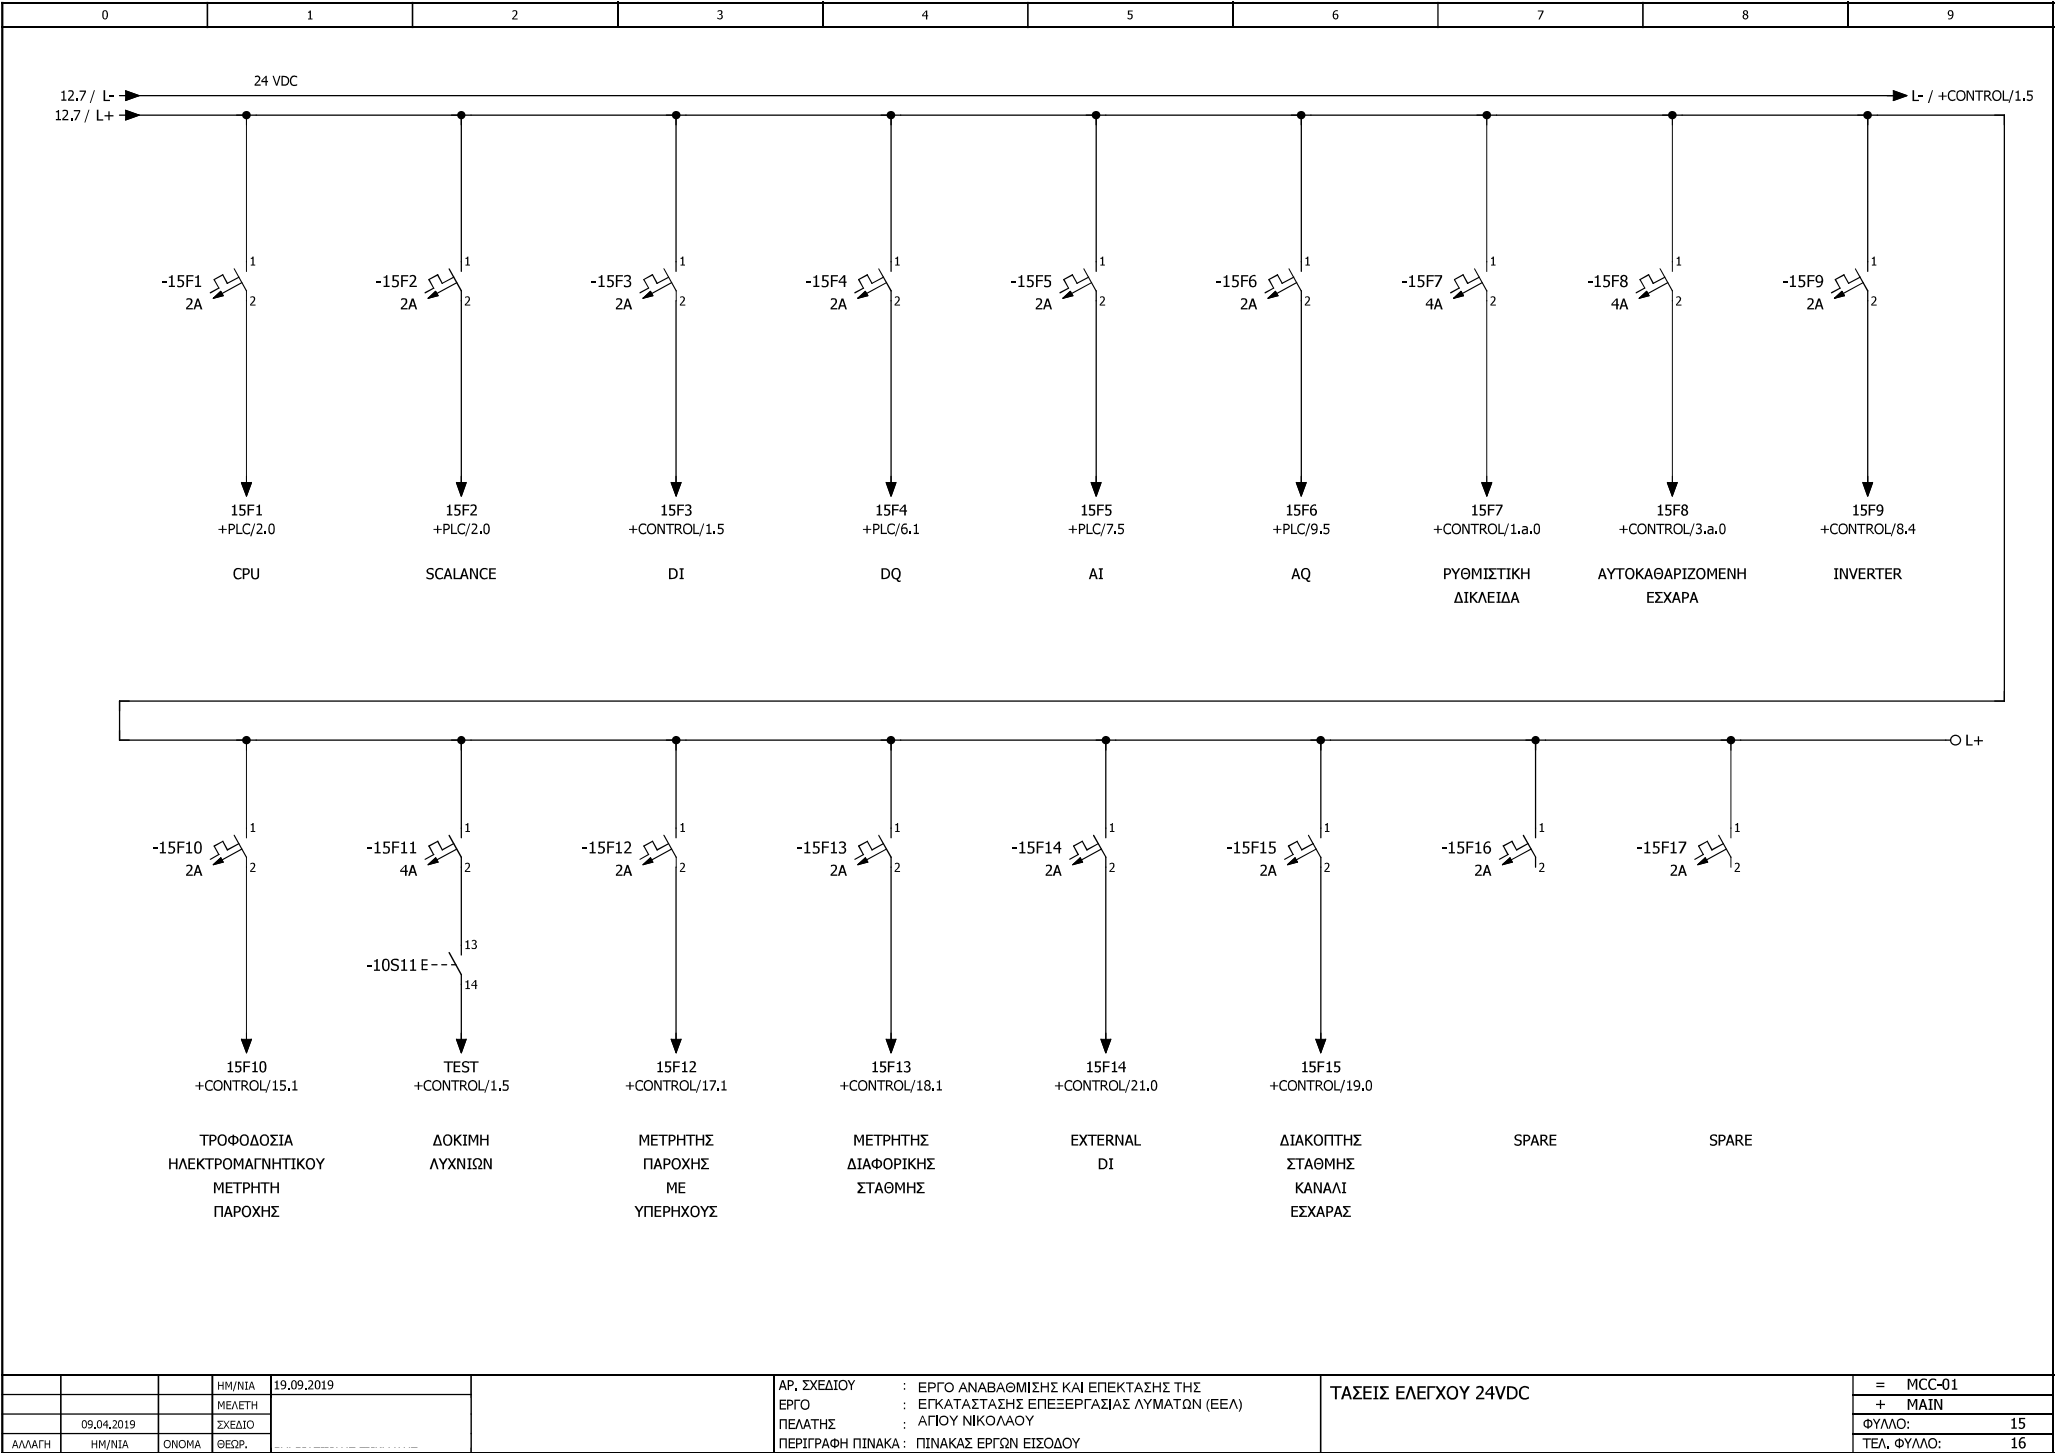


0	1	2	3	4	5	6	7	8	9
			ΗΜ/ΝΙΑ	19.09.2019		ΑΡ. ΣΧΕΔΙΟΥ : ΕΡΓΟ ΑΝΑΒΑΘΜΙΣΗΣ ΚΑΙ ΕΠΕΚΤΑΣΗΣ ΤΗΣ ΕΡΓΟ : ΕΓΚΑΤΑΣΤΑΣΗΣ ΕΠΕΞΕΡΓΑΣΙΑΣ ΛΥΜΑΤΩΝ (ΕΕΛ) ΠΕΛΑΤΗΣ : ΑΓΙΟΥ ΝΙΚΟΛΑΟΥ ΠΕΡΙΓΡΑΦΗ ΠΙΝΑΚΑ : ΠΙΝΑΚΑΣ ΕΡΓΩΝ ΕΙΣΟΔΟΥ	ΚΕΝΗ ΣΕΛΙΔΑ	= MCC-01	
			ΜΕΛΕΤΗ					+ ΜΑΙΝ	
	09.04.2019		ΣΧΕΔΙΟ					ΦΥΛΛΟ:	16
ΑΛΛΑΓΗ	ΗΜ/ΝΙΑ	ΟΝΟΜΑ	ΘΕΩΡ.					ΤΕΛ. ΦΥΛΛΟ:	16

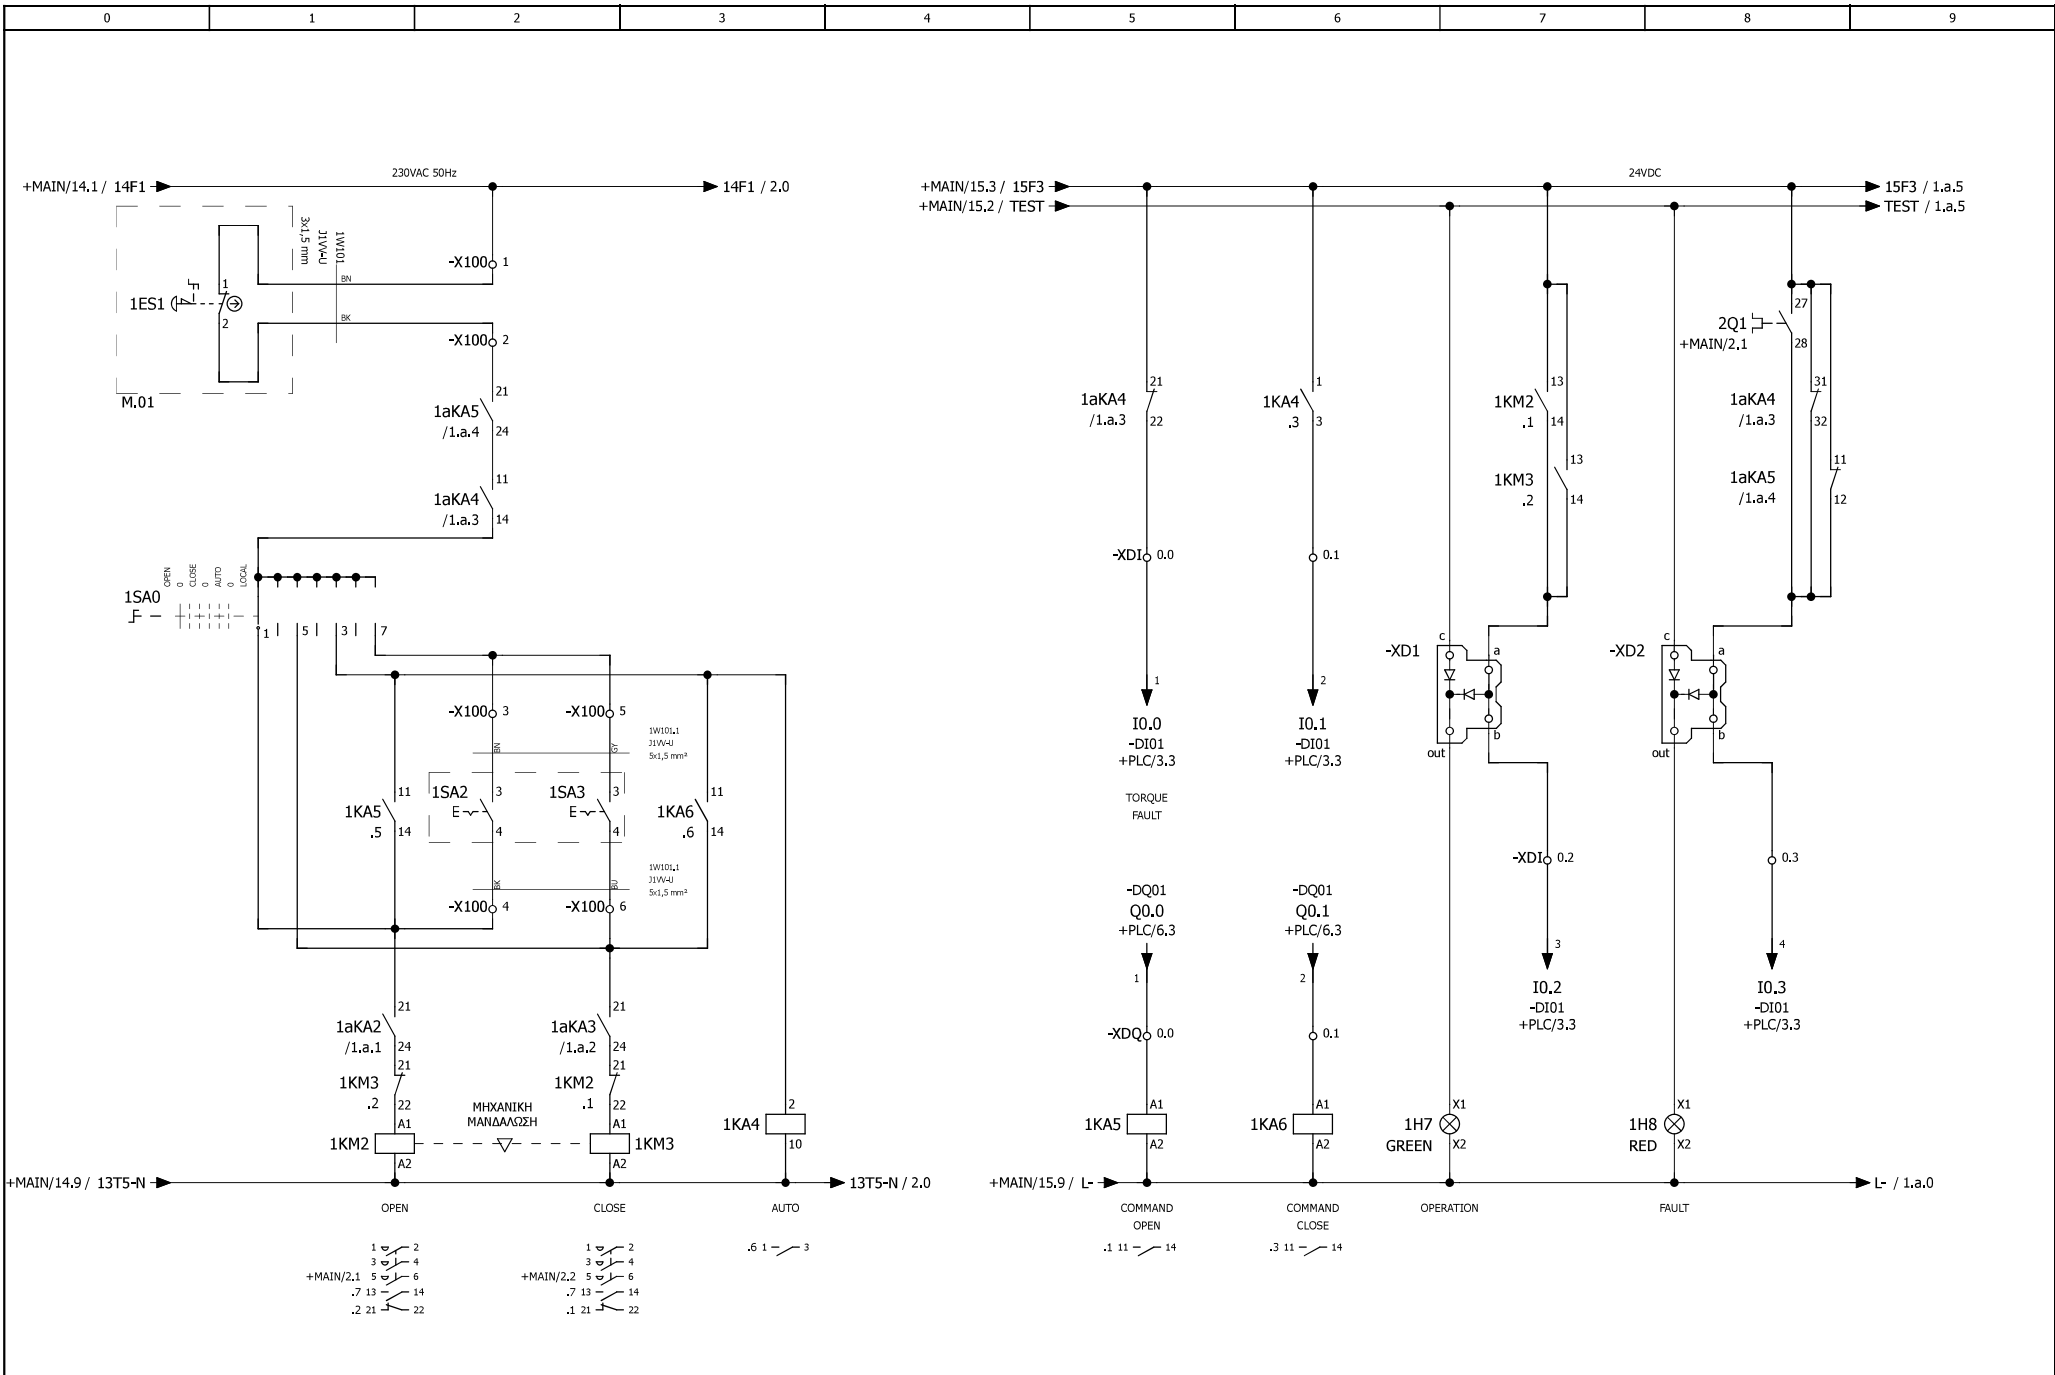


ΑΡ. ΣΧΕΔΙΟΥ	ΕΡΓΟ ΑΝΑΒΑΘΜΙΣΗΣ ΚΑΙ ΕΠΕΚΤΑΣΗΣ ΤΗΣ	ΡΥΘΜΙΣΤΙΚΗ ΔΙΚΛΕΙΔΑ ΚΥΡΙΟΥ ΑΓΩΓΟΥ ΕΙΣΟΔΟΥ Μ01-01-05	= MCC-01
ΕΡΓΟ	ΕΓΚΑΤΑΣΤΑΣΗΣ ΕΠΕΞΕΡΓΑΣΙΑΣ ΛΥΜΑΤΩΝ (ΕΕΛ)	+ CONTROL	
ΠΕΛΑΤΗΣ	ΑΓΙΟΥ ΝΙΚΟΛΑΟΥ	ΦΥΛΛΟ:	1
ΠΕΡΙΓΡΑΦΗ ΠΙΝΑΚΑ:	ΠΙΝΑΚΑΣ ΕΡΓΩΝ ΕΙΣΟΔΟΥ	ΤΕΛ. ΦΥΛΛΟ:	23

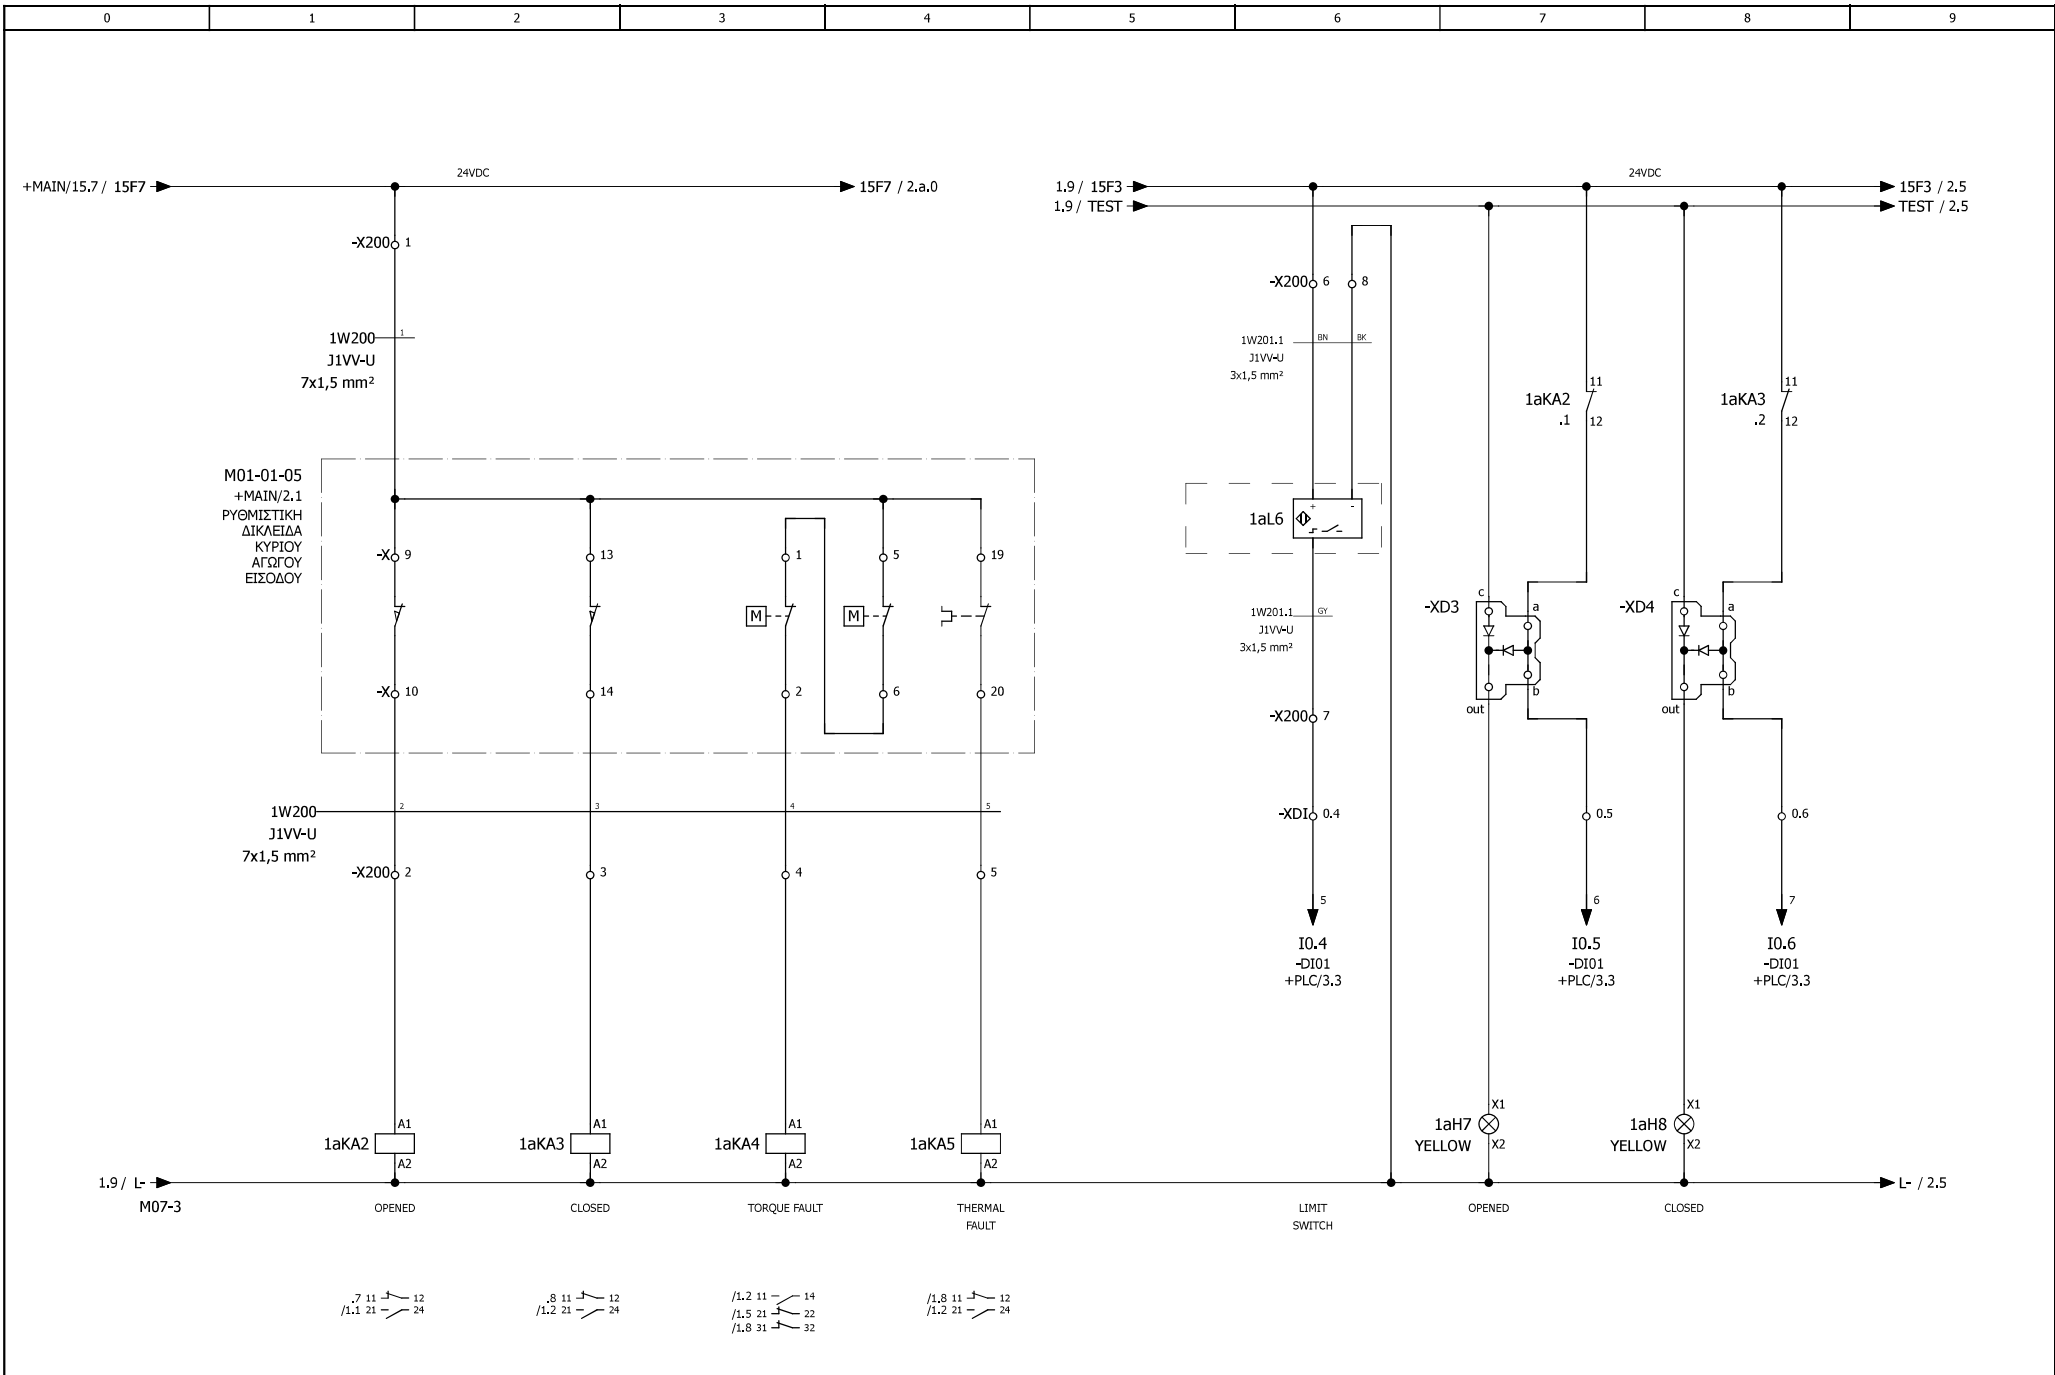


ΑΛΛΑΓΗ	ΗΜ/ΝΙΑ	ΟΝΟΜΑ	ΘΕΩΡ.	19.09.2019	ΑΡ. ΣΧΕΔΙΟΥ : ΕΡΓΟ ΑΝΑΒΑΘΜΙΣΗΣ ΚΑΙ ΕΠΕΚΤΑΣΗΣ ΤΗΣ ΕΡΓΟ : ΕΓΚΑΤΑΣΤΑΣΗΣ ΕΠΕΞΕΡΓΑΣΙΑΣ ΛΥΜΑΤΩΝ (ΕΕΛ) ΠΕΛΑΤΗΣ : ΑΓΙΟΥ ΝΙΚΟΛΑΟΥ ΠΕΡΙΓΡΑΦΗ ΠΙΝΑΚΑ : ΠΙΝΑΚΑΣ ΕΡΓΩΝ ΕΙΣΟΔΟΥ	ΡΥΘΜΙΣΤΙΚΗ ΔΙΚΛΕΙΔΑ ΚΥΡΙΟΥ ΑΓΩΓΟΥ ΕΙΣΟΔΟΥ Μ01-01-05	= MCC-01 + CONTROL ΦΥΛΛΟ: 1.a ΤΕΛ. ΦΥΛΛΟ: 23
				ΜΕΛΕΤΗ			
				ΣΧΕΔΙΟ			
				09.04.2019			

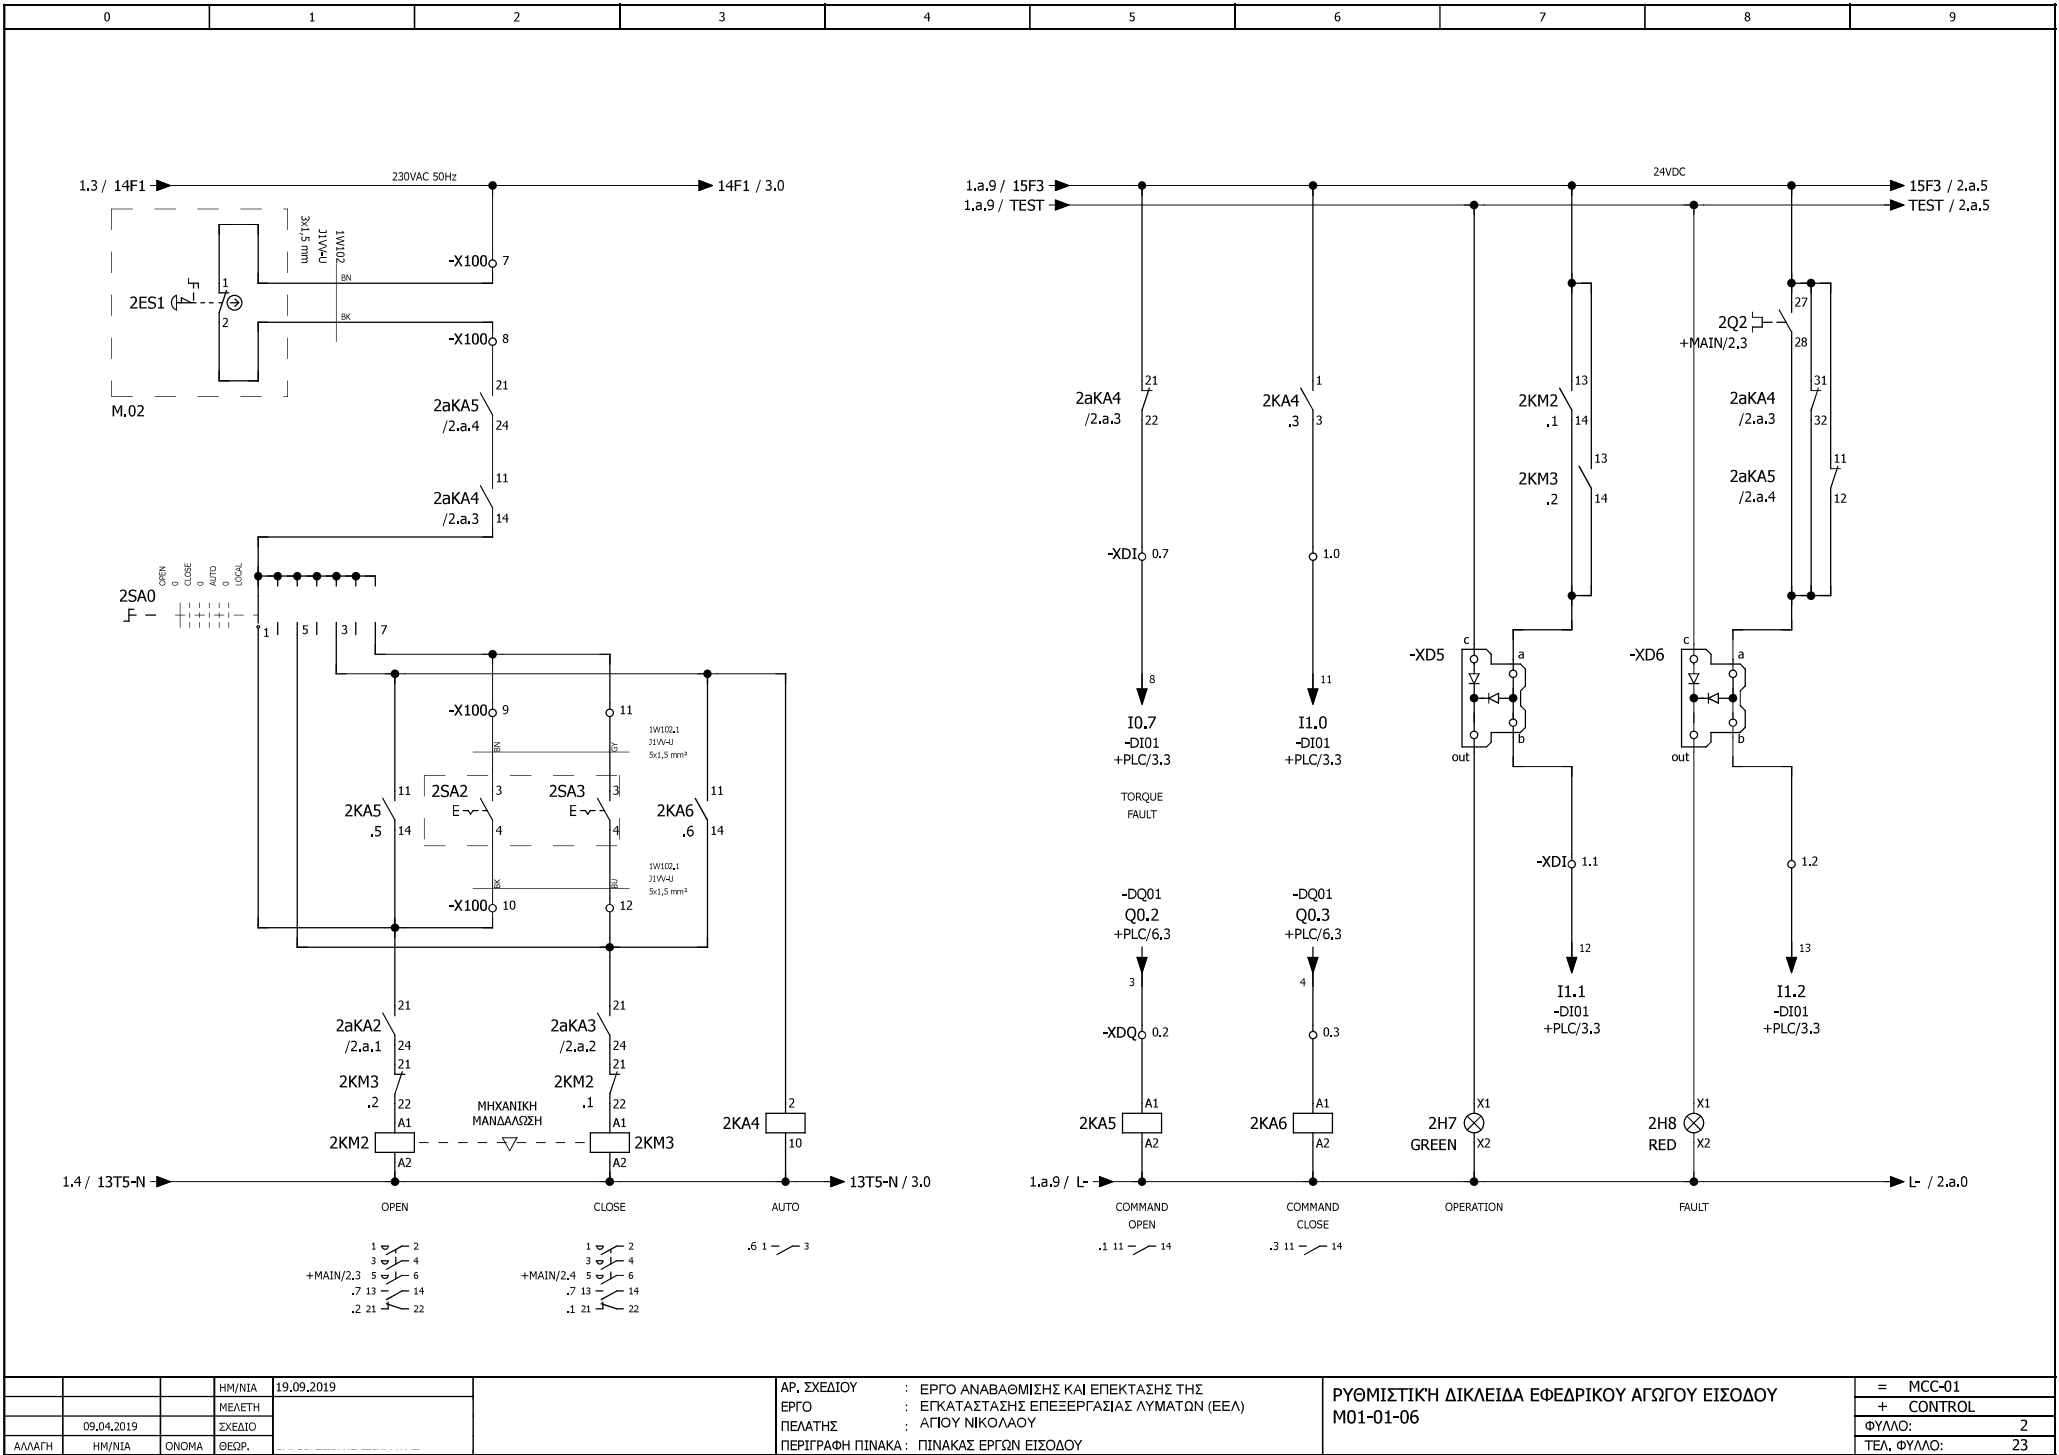


			HM/ΝΙΑ	19.09.2019	ΑΡ. ΣΧΕΔΙΟΥ	ΕΡΓΟ ΑΝΑΒΑΘΜΙΣΗΣ ΚΑΙ ΕΠΕΚΤΑΣΗΣ ΤΗΣ	ΡΥΘΜΙΣΤΙΚΗ ΔΙΚΛΕΙΔΑ ΕΦΕΔΡΙΚΟΥ ΑΓΩΓΟΥ ΕΙΣΟΔΟΥ	= MCC-01
			ΜΕΛΕΤΗ		ΕΡΓΟ	ΕΓΚΑΤΑΣΤΑΣΗΣ ΕΠΕΞΕΡΓΑΣΙΑΣ ΛΥΜΑΤΩΝ (ΕΕΛ)	M01-01-06	+ CONTROL
09.04.2019			ΣΧΕΔΙΟ		ΠΕΛΑΤΗΣ	ΑΓΙΟΥ ΝΙΚΟΛΑΟΥ		ΦΥΛΛΟ: 2
ΑΛΛΑΓΗ	HM/ΝΙΑ	ΟΝΟΜΑ	ΘΕΩΡ.		ΠΕΡΙΓΡΑΦΗ ΠΙΝΑΚΑ:	ΠΙΝΑΚΑΣ ΕΡΓΩΝ ΕΙΣΟΔΟΥ		ΤΕΛ. ΦΥΛΛΟ: 23

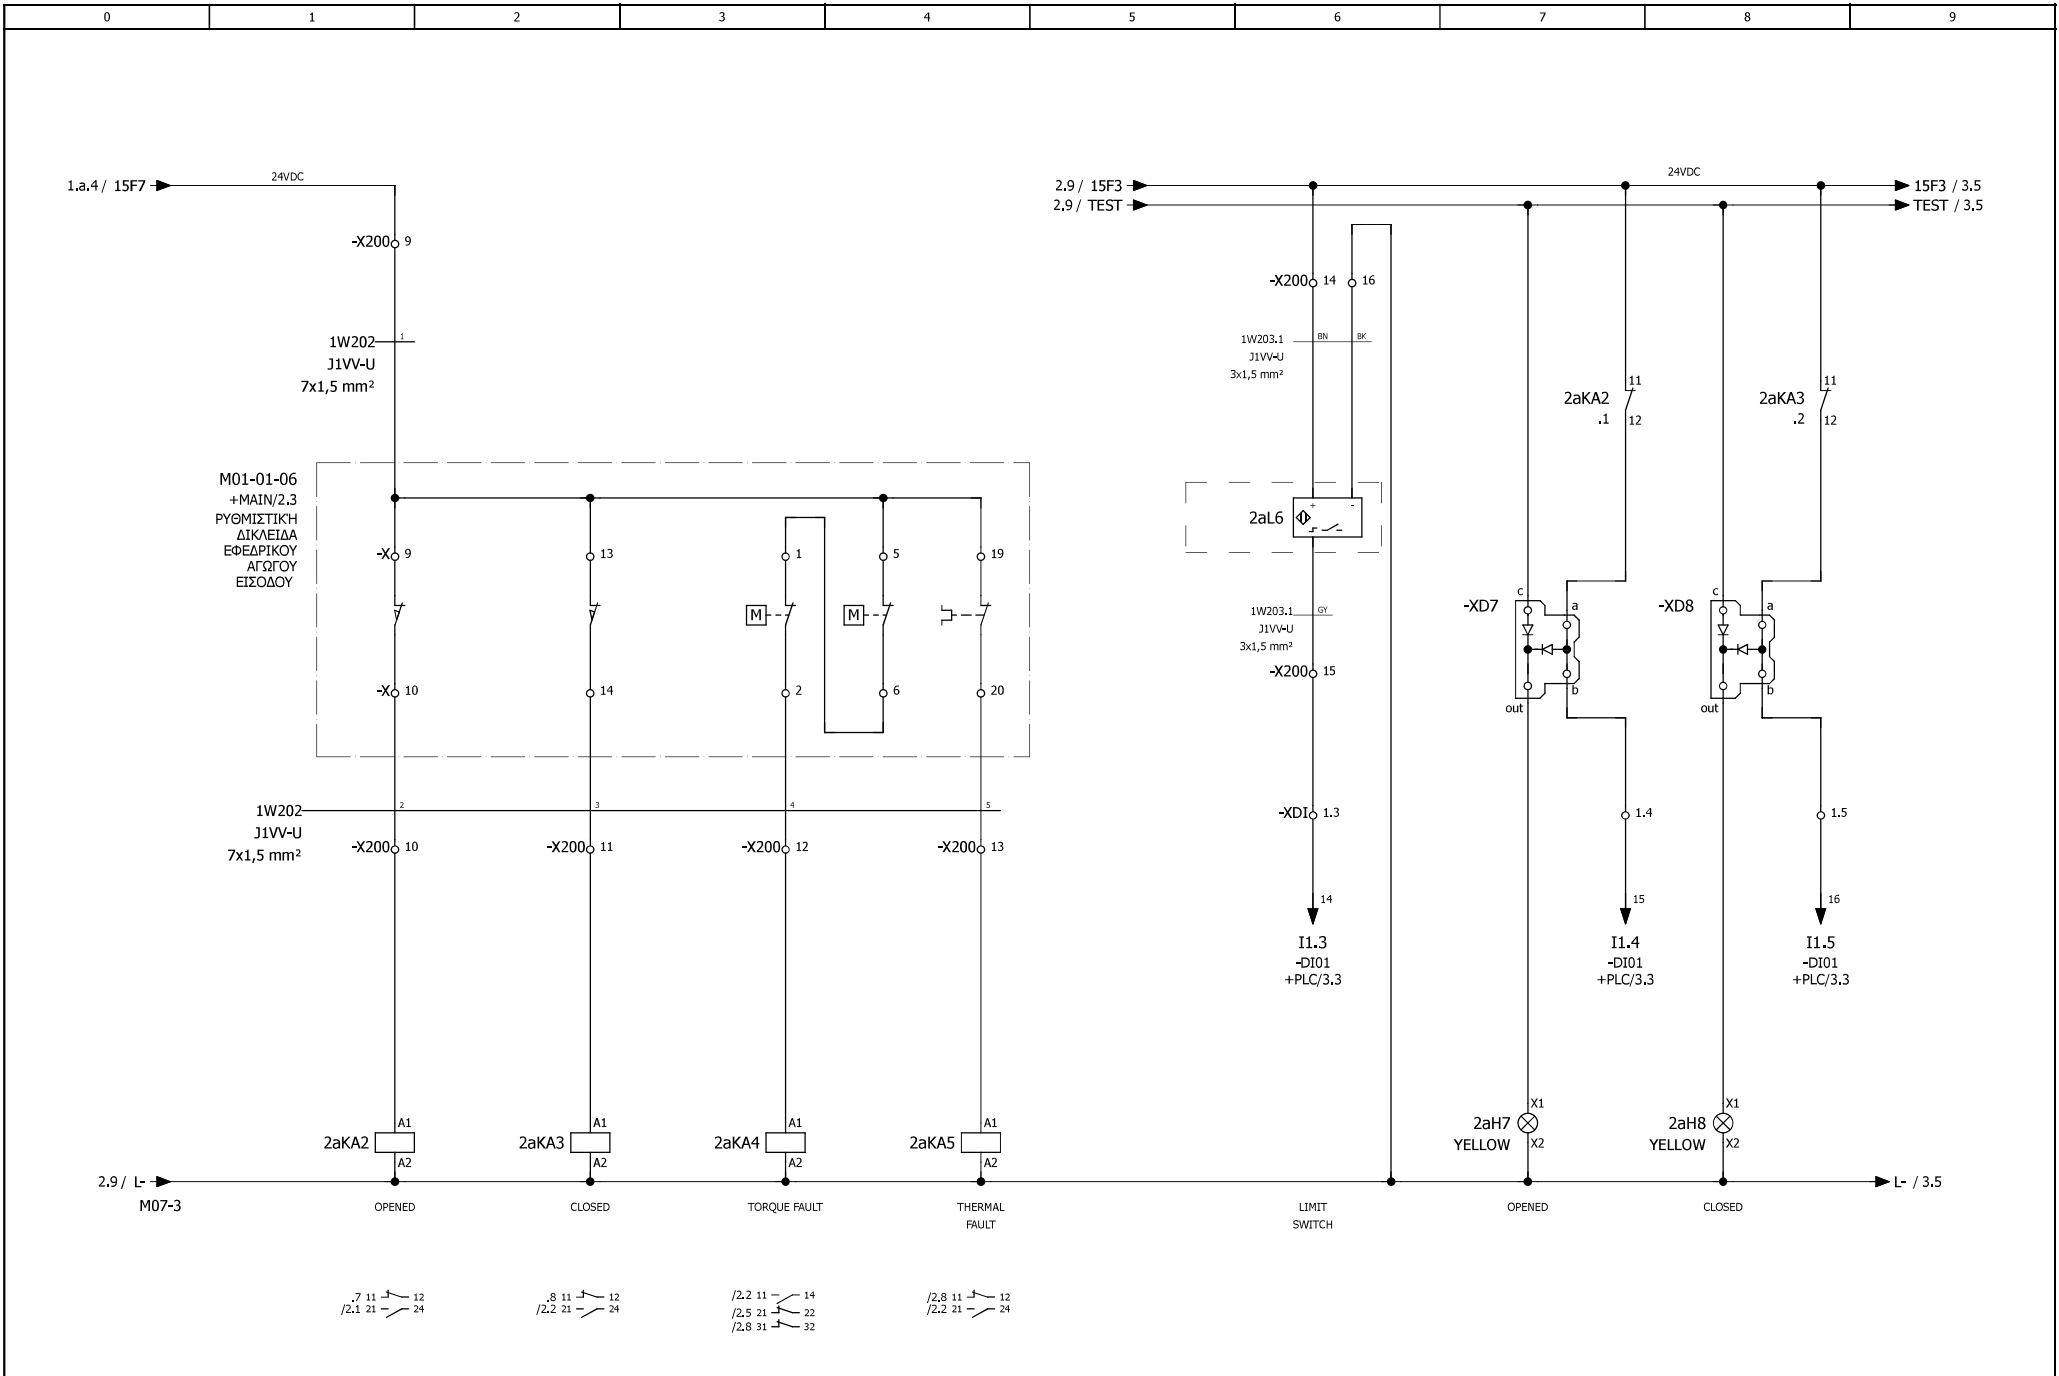


ΑΛΛΑΓΗ	ΗΜ/ΝΙΑ	ΟΝΟΜΑ	ΘΕΩΡ.	19.09.2019	ΑΡ. ΣΧΕΔΙΟΥ : ΕΡΓΟ ΑΝΑΒΑΘΜΙΣΗΣ ΚΑΙ ΕΠΕΚΤΑΣΗΣ ΤΗΣ ΕΡΓΟ : ΕΓΚΑΤΑΣΤΑΣΗΣ ΕΠΕΞΕΡΓΑΣΙΑΣ ΑΥΜΑΤΩΝ (ΕΕΛ) ΠΕΛΑΤΗΣ : ΑΓΙΟΥ ΝΙΚΟΛΑΟΥ ΠΕΡΙΓΡΑΦΗ ΠΙΝΑΚΑ : ΠΙΝΑΚΑΣ ΕΡΓΩΝ ΕΙΣΟΔΟΥ	ΡΥΘΜΙΣΤΙΚΗ ΔΙΚΛΕΙΔΑ ΕΦΕΔΡΙΚΟΥ ΑΓΩΓΟΥ ΕΙΣΟΔΟΥ M01-01-06	= MCC-01 + CONTROL ΦΥΛΛΟ: 2.a ΤΕΛ. ΦΥΛΛΟ: 23
				ΜΕΛΕΤΗ			
				ΣΧΕΔΙΟ			
				ΘΕΩΡ.			

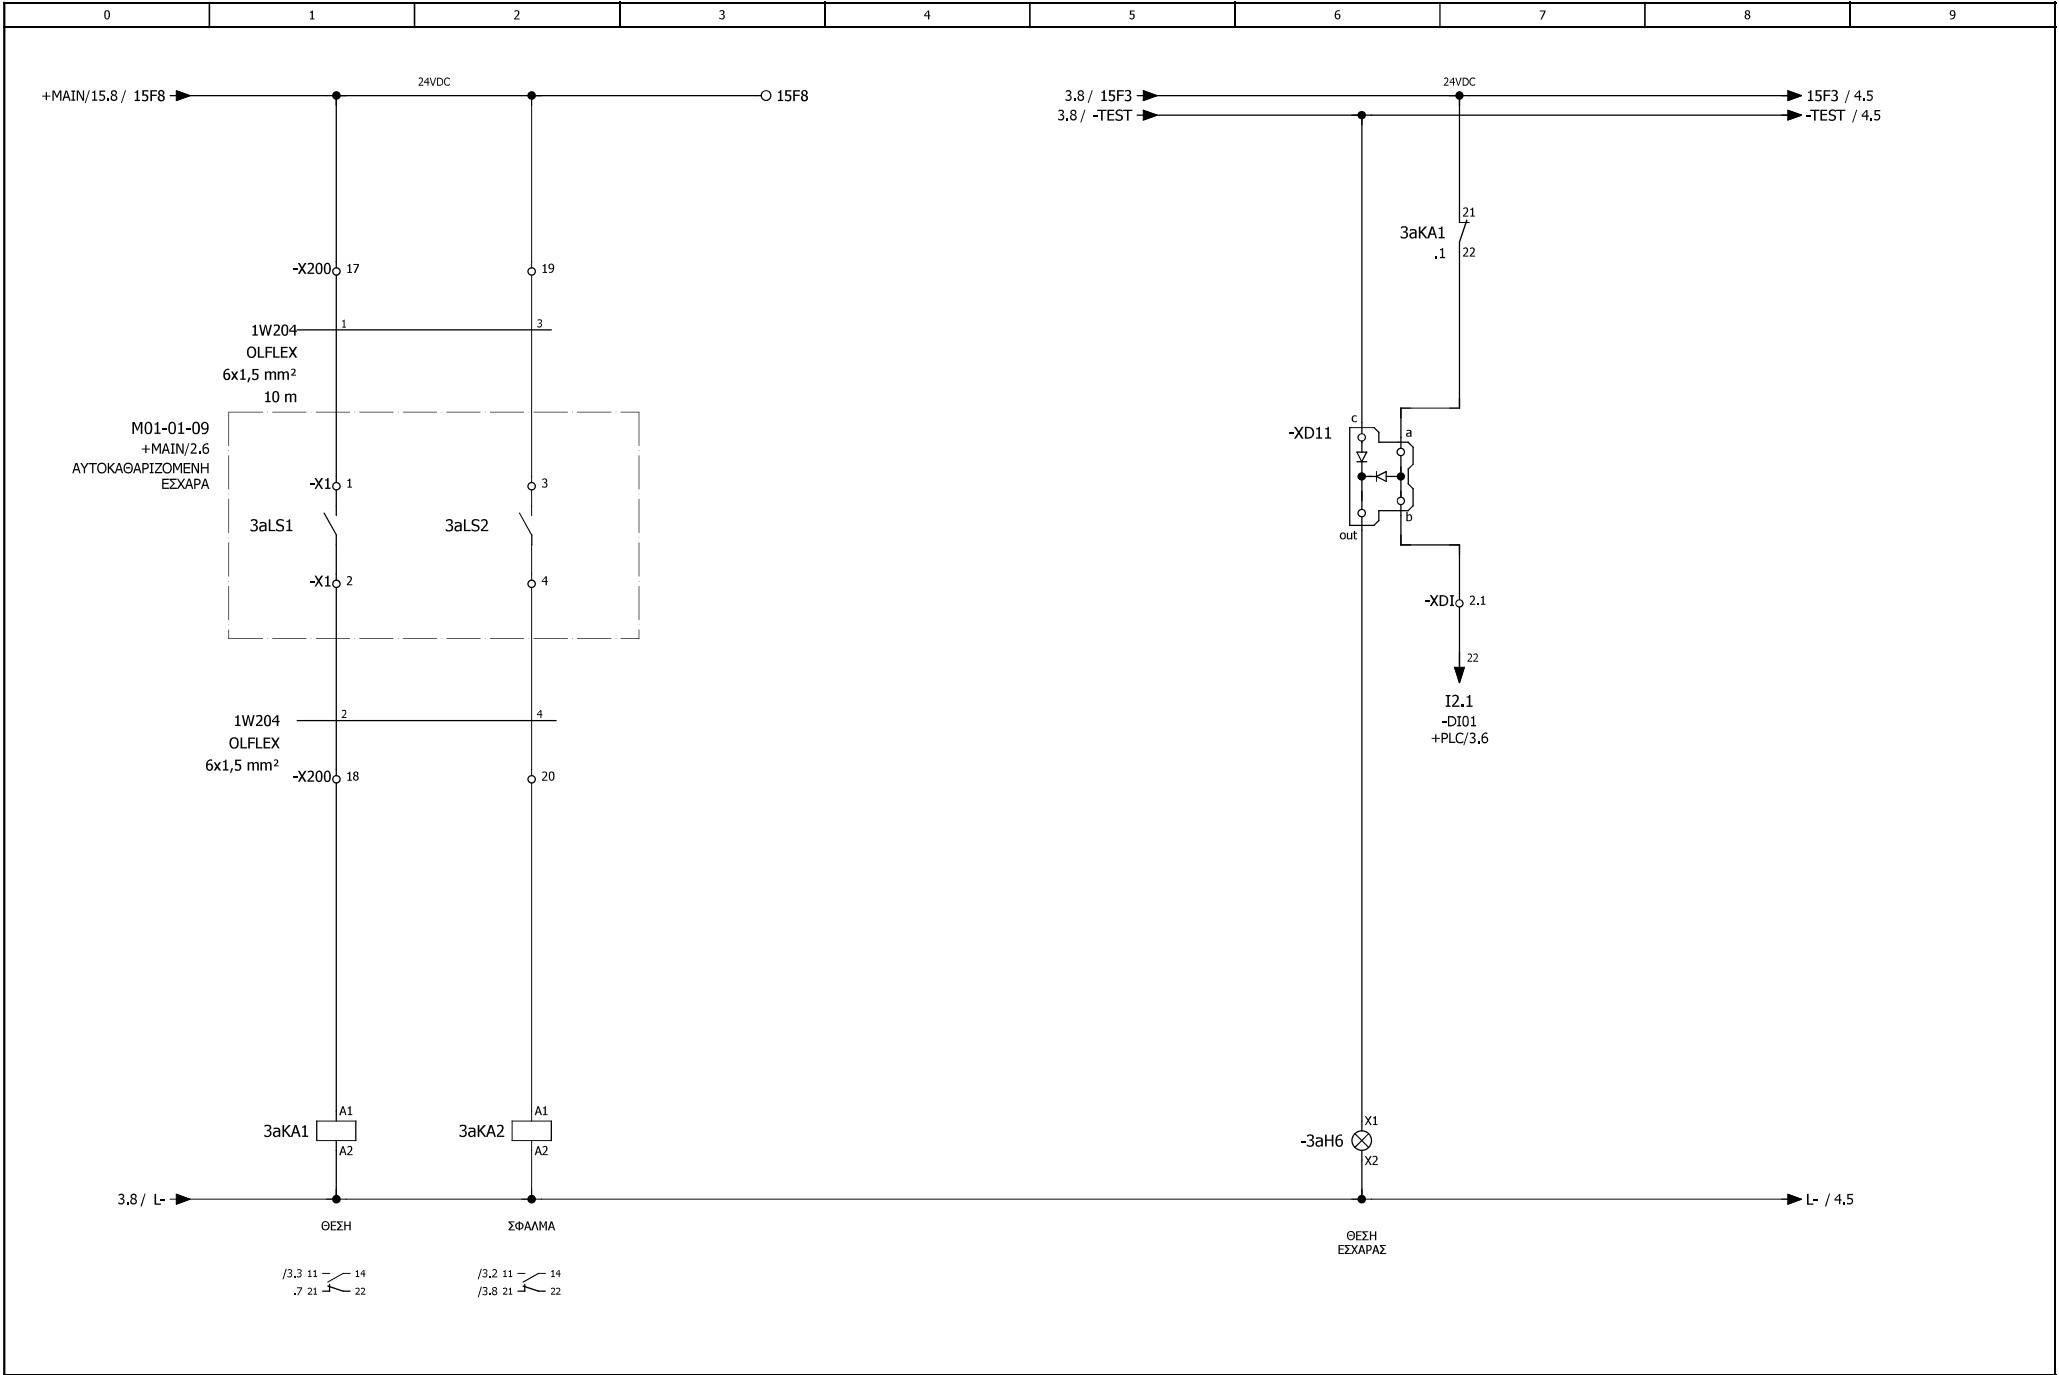


			ΗΜ/ΝΙΑ	19.09.2019	ΑΡ. ΣΧΕΔΙΟΥ	: ΕΡΓΟ ΑΝΑΒΑΘΜΙΣΗΣ ΚΑΙ ΕΠΕΚΤΑΣΗΣ ΤΗΣ	ΑΥΤΟΚΑΘΑΡΙΖΟΜΕΝΗ ΕΣΧΑΡΑ Μ01-01-09	=	MCC-01
			ΜΕΛΕΤΗ		ΕΡΓΟ	: ΕΓΚΑΤΑΣΤΑΣΗΣ ΕΠΕΞΕΡΓΑΣΙΑΣ ΛΥΜΑΤΩΝ (ΕΕΛ)		+	CONTROL
09.04.2019			ΣΧΕΔΙΟ		ΠΕΛΑΤΗΣ	: ΑΓΙΟΥ ΝΙΚΟΛΑΟΥ		ΦΥΛΛΟ:	3.a
ΑΛΛΑΓΗ	ΗΜ/ΝΙΑ	ΟΝΟΜΑ	ΘΕΩΡ.		ΠΕΡΙΓΡΑΦΗ ΠΙΝΑΚΑ	: ΠΙΝΑΚΑΣ ΕΡΓΩΝ ΕΙΣΟΔΟΥ		ΤΕΛ. ΦΥΛΛΟ:	23

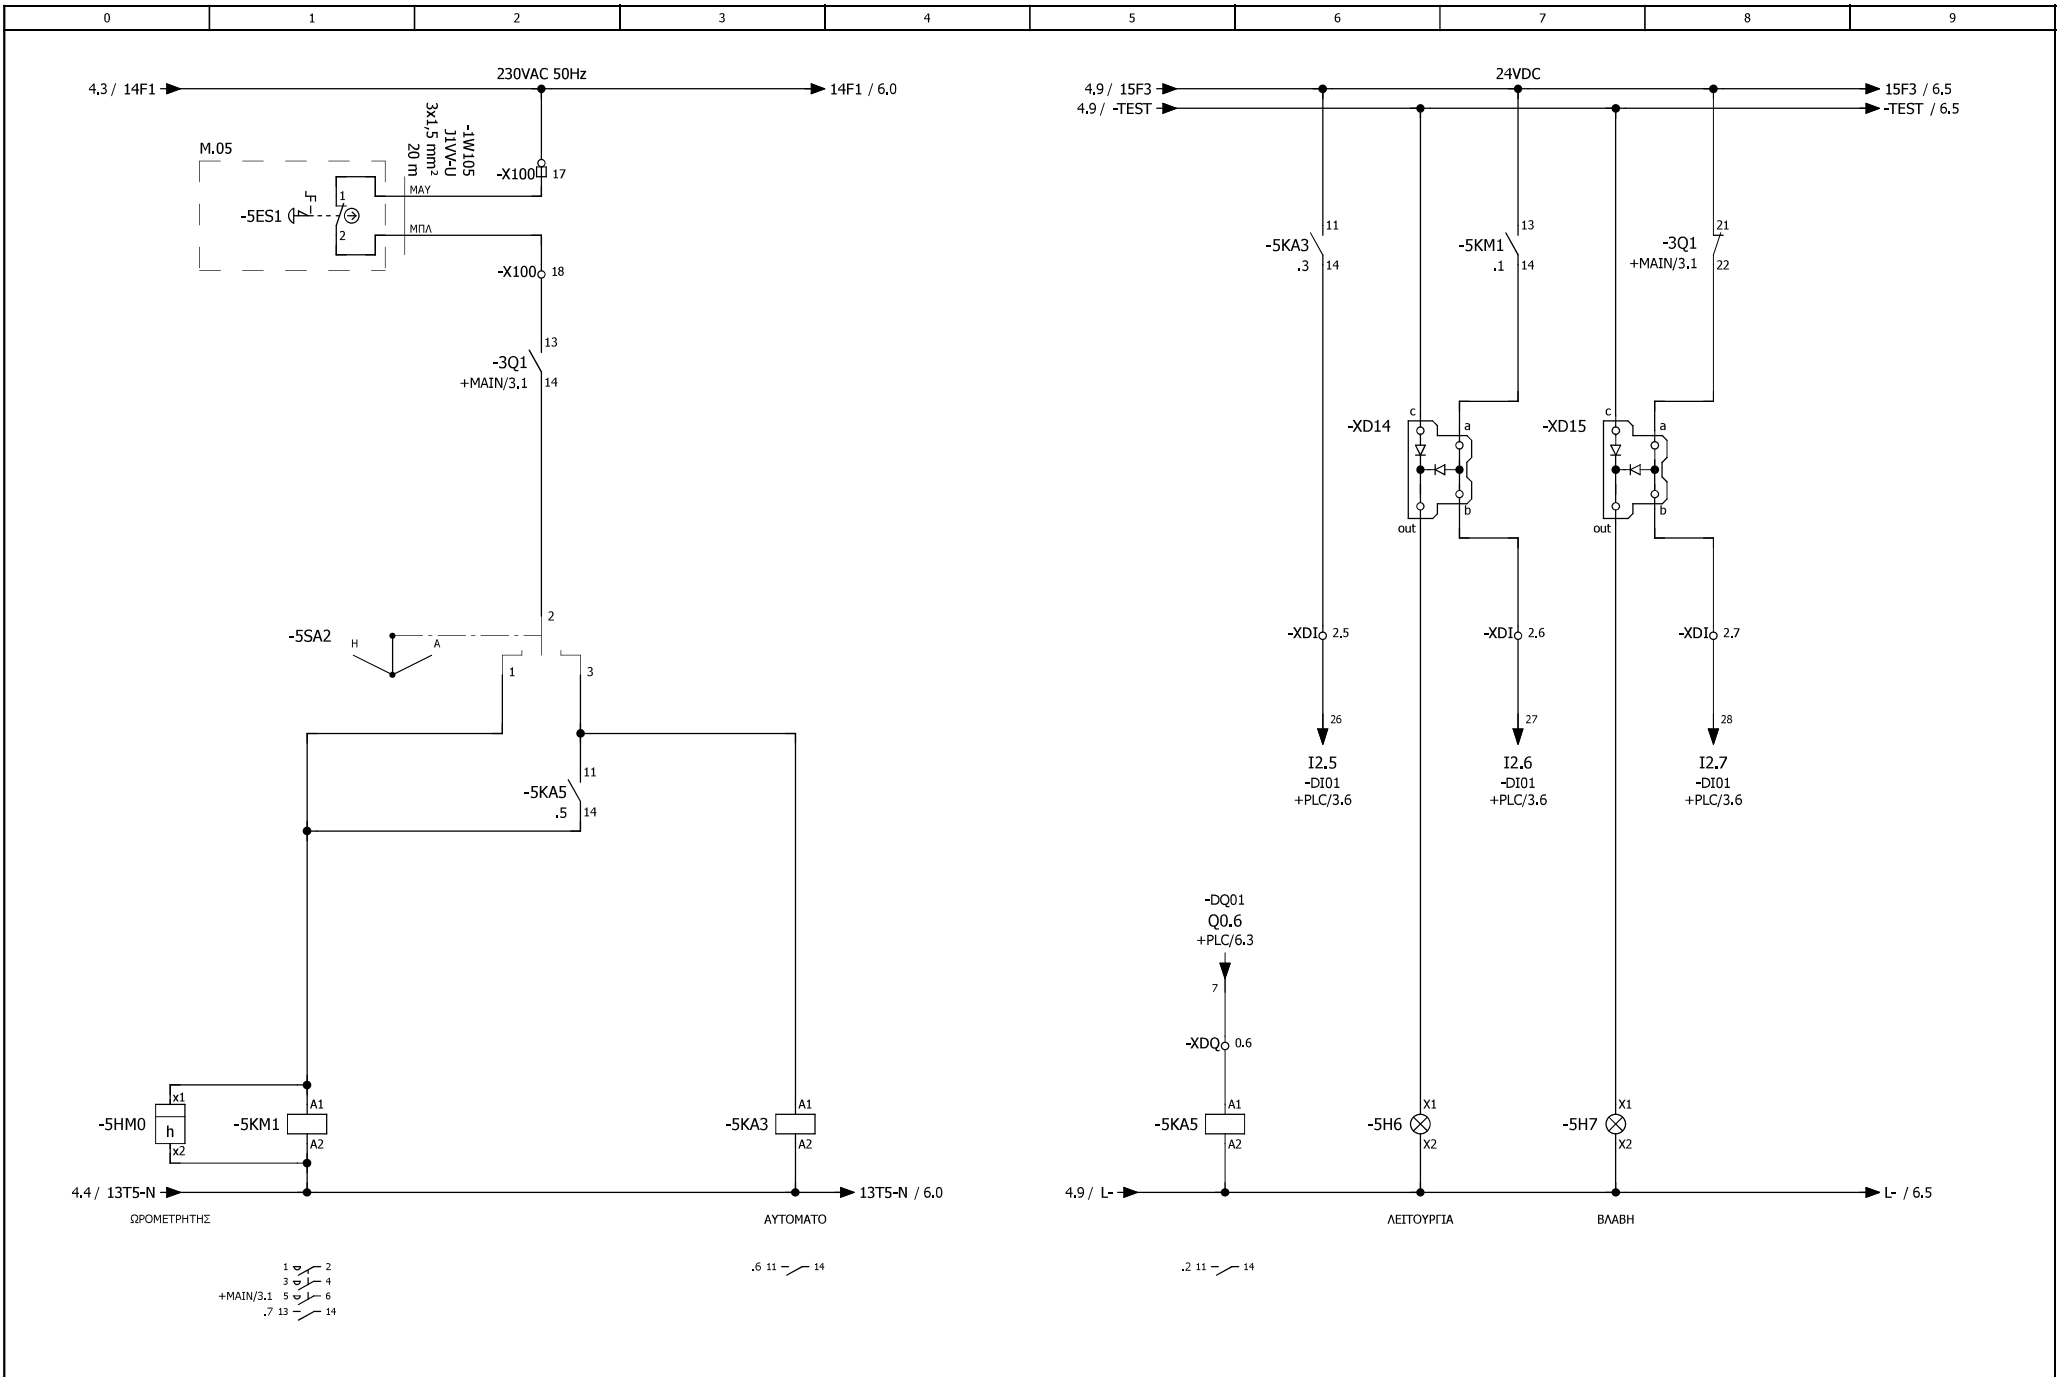


		ΗΜ/ΝΙΑ	19.09.2019		ΑΡ. ΣΧΕΔΙΟΥ : ΕΡΓΟ ΑΝΑΒΑΘΜΙΣΗΣ ΚΑΙ ΕΠΕΚΤΑΣΗΣ ΤΗΣ ΕΡΓΟ : ΕΓΚΑΤΑΣΤΑΣΗΣ ΕΠΕΞΕΡΓΑΣΙΑΣ ΑΥΜΑΤΩΝ (ΕΕΛ) ΠΕΛΑΤΗΣ : ΑΓΙΟΥ ΝΙΚΟΛΑΟΥ ΠΕΡΙΓΡΑΦΗ ΠΙΝΑΚΑ : ΠΙΝΑΚΑΣ ΕΡΓΩΝ ΕΙΣΟΔΟΥ	ΑΞΟΝΙΚΟΣ ΑΝΕΜΙΣΤΗΡΑΣ ΕΞΑΕΡΙΣΜΟΥ ΚΤΗΡΙΟΥ ΕΣΧΑΡΩΣΗΣ Μ01-01-16-1	= MCC-01 + CONTROL ΦΥΛΛΟ: 5 ΤΕΛ. ΦΥΛΛΟ: 23
ΑΛΛΑΓΗ	ΗΜ/ΝΙΑ	ΟΝΟΜΑ	ΘΕΩΡ.				

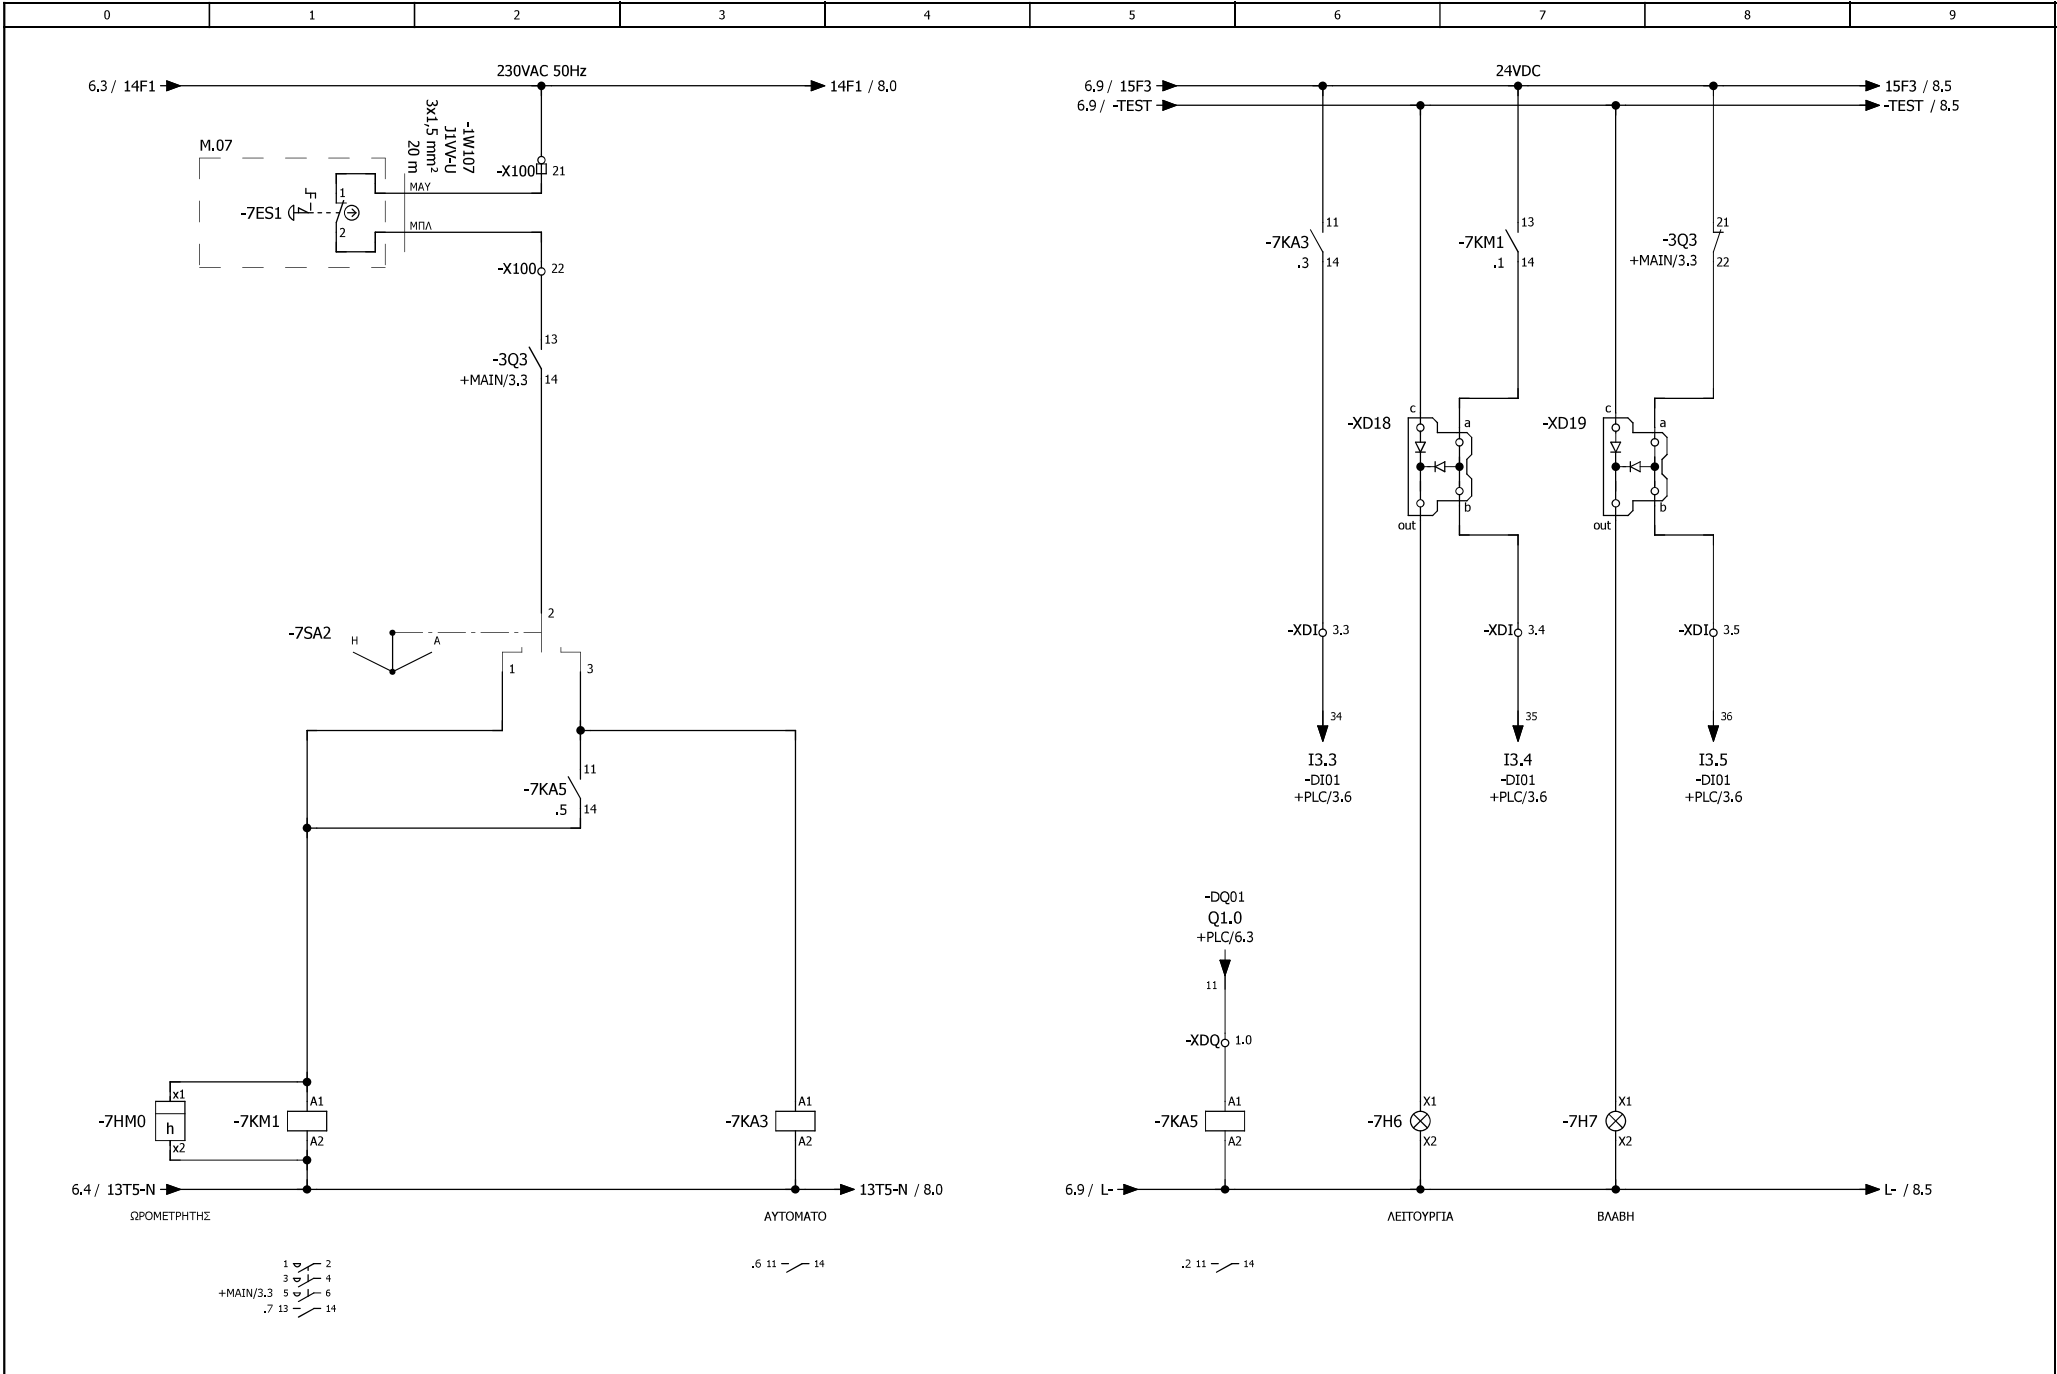


		ΗΜ/ΝΙΑ	19.09.2019	ΑΡ. ΣΧΕΔΙΟΥ : ΕΡΓΟ ΑΝΑΒΑΘΜΙΣΗΣ ΚΑΙ ΕΠΕΚΤΑΣΗΣ ΤΗΣ ΕΡΓΟ : ΕΓΚΑΤΑΣΤΑΣΗΣ ΕΠΕΞΕΡΓΑΣΙΑΣ ΑΥΜΑΤΩΝ (ΕΕΛ) ΠΕΛΑΤΗΣ : ΑΓΙΟΥ ΝΙΚΟΛΑΟΥ ΠΕΡΙΓΡΑΦΗ ΠΙΝΑΚΑ : ΠΙΝΑΚΑΣ ΕΡΓΩΝ ΕΙΣΟΔΟΥ	ΣΥΣΤΗΜΑ ΚΑΘ. ΑΕΡΑ ΠΙΝΑΚΑ MCC-01	= MCC-01	
		ΜΕΛΕΤΗ				+ CONTROL	
09.04.2019		ΣΧΕΔΙΟ				ΦΥΛΛΟ: 7	
ΑΛΛΑΓΗ	ΗΜ/ΝΙΑ	ΟΝΟΜΑ	ΘΕΩΡ.			ΤΕΛ. ΦΥΛΛΟ: 23	

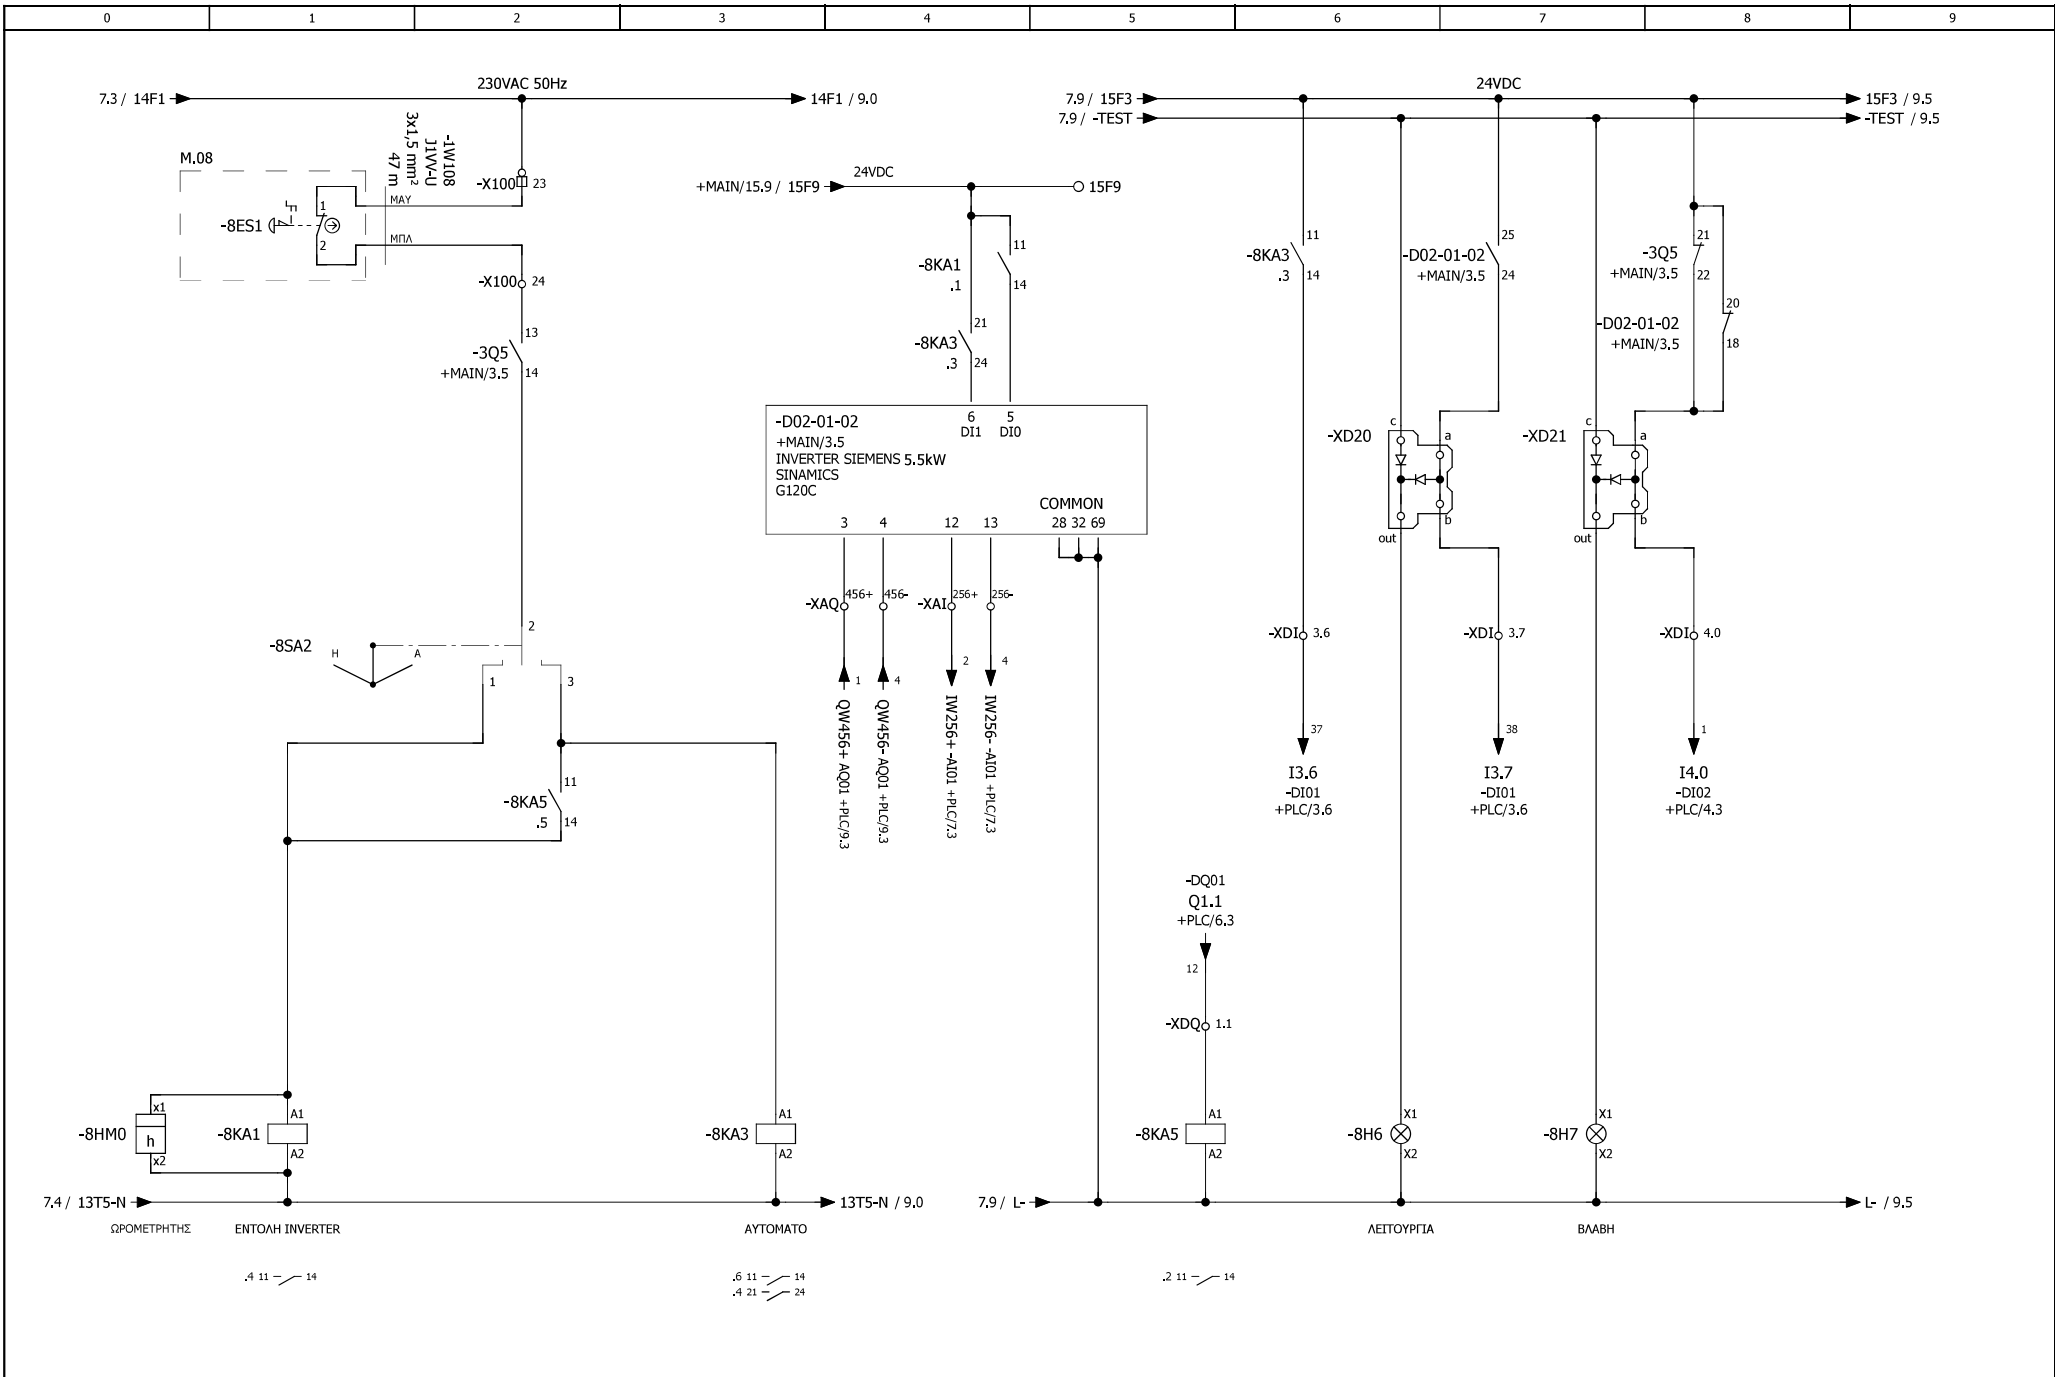


		ΗΜ/ΝΙΑ ΜΕΛΕΤΗ 09.04.2019 ΣΧΕΔΙΟ	19.09.2019		ΑΡ. ΣΧΕΔΙΟΥ : ΕΡΓΟ ΑΝΑΒΑΘΜΙΣΗΣ ΚΑΙ ΕΠΕΚΤΑΣΗΣ ΤΗΣ ΕΡΓΟ : ΕΓΚΑΤΑΣΤΑΣΗΣ ΕΠΕΞΕΡΓΑΣΙΑΣ ΛΥΜΑΤΩΝ (ΕΕΛ) ΠΕΛΑΤΗΣ : ΑΓΙΟΥ ΝΙΚΟΛΑΟΥ ΠΕΡΙΓΡΑΦΗ ΠΙΝΑΚΑ : ΠΙΝΑΚΑΣ ΕΡΓΩΝ ΕΙΣΟΔΟΥ	ΚΑΤΑΚΟΡΥΦΟΣ ΑΝΑΔΕΥΤΗΡΑΣ ΦΡΕΑΤΙΟΥ ΠΡΟΣΘΗΚΗΣ ΘΕΙΙΚΟΥ ΟΞΕΟΣ Μ02-01-01	= MCC-01 + CONTROL ΦΥΛΛΟ: 8 ΤΕΛ. ΦΥΛΛΟ: 23
ΑΛΛΑΓΗ	ΗΜ/ΝΙΑ	ΟΝΟΜΑ	ΘΕΩΡ.				

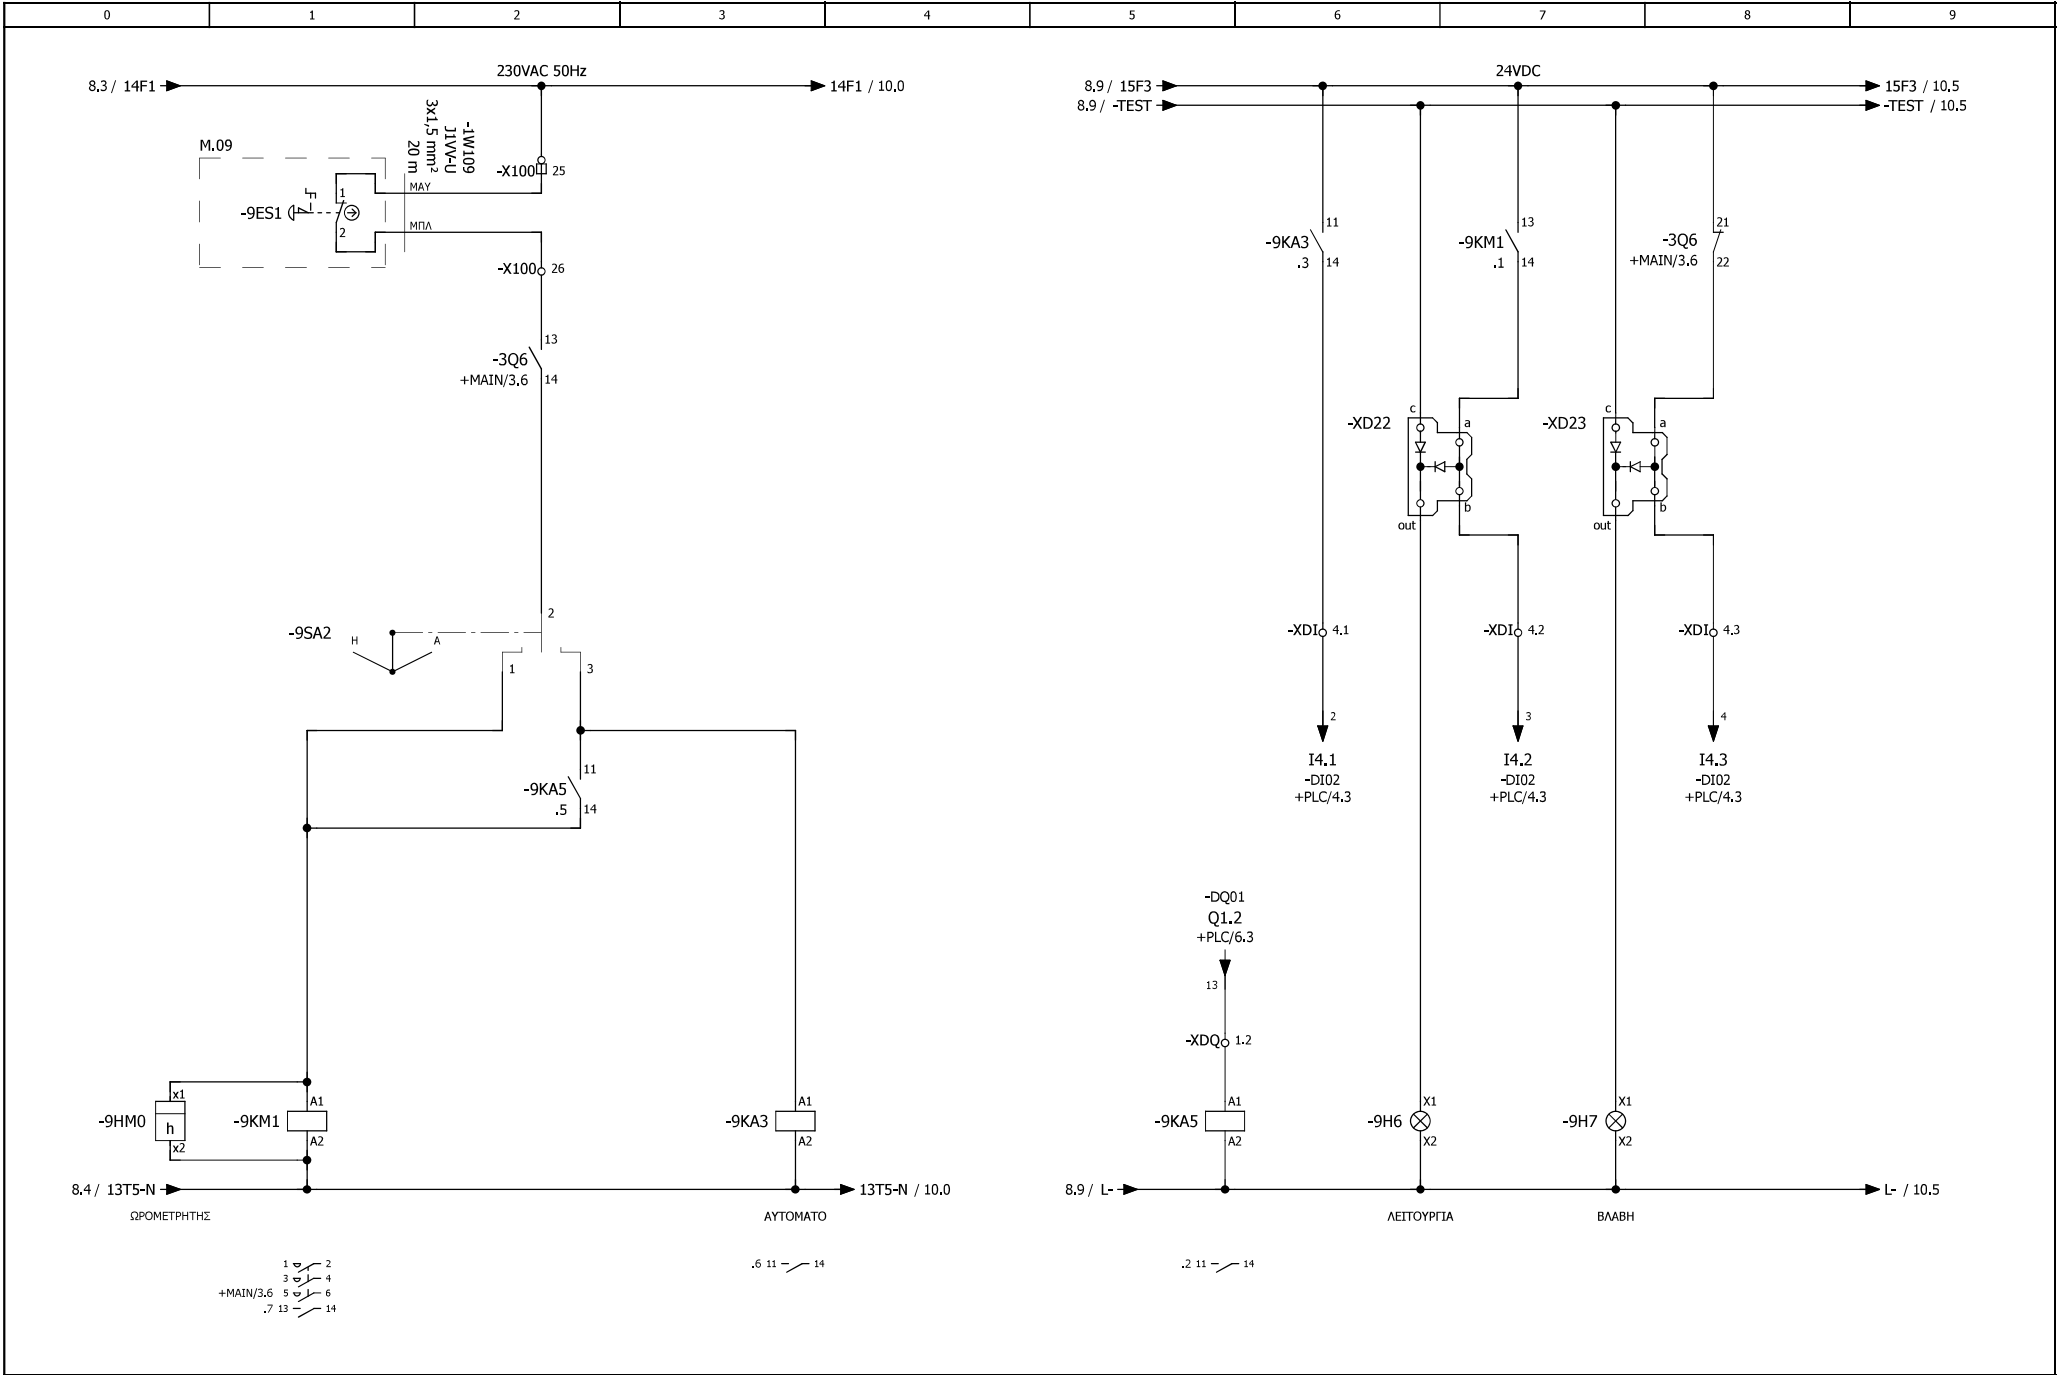


			ΗΜ/ΝΙΑ	19.09.2019	ΑΡ. ΣΧΕΔΙΟΥ	ΕΡΓΟ ΑΝΑΒΑΘΜΙΣΗΣ ΚΑΙ ΕΠΕΚΤΑΣΗΣ ΤΗΣ	ΑΝΕΜΙΣΤΗΡΑΣ ΧΩΡΟΥ ΠΑΡΑΓΩΓΗΣ ΠΡΟΟΖΟΝΩΣΗΣ Μ02-01-18	= MCC-01
			ΜΕΛΕΤΗ		ΕΡΓΟ	ΕΓΚΑΤΑΣΤΑΣΗΣ ΕΠΕΞΕΡΓΑΣΙΑΣ ΛΥΜΑΤΩΝ (ΕΕΛ)		+ CONTROL
09.04.2019			ΣΧΕΔΙΟ		ΠΕΛΑΤΗΣ	ΑΓΙΟΥ ΝΙΚΟΛΑΟΥ		ΦΥΛΛΟ: 9
ΑΛΛΑΓΗ	ΗΜ/ΝΙΑ	ΟΝΟΜΑ	ΘΕΩΡ.		ΠΕΡΙΓΡΑΦΗ ΠΙΝΑΚΑ	ΠΙΝΑΚΑΣ ΕΡΓΩΝ ΕΙΣΟΔΟΥ		ΤΕΛ. ΦΥΛΛΟ: 23

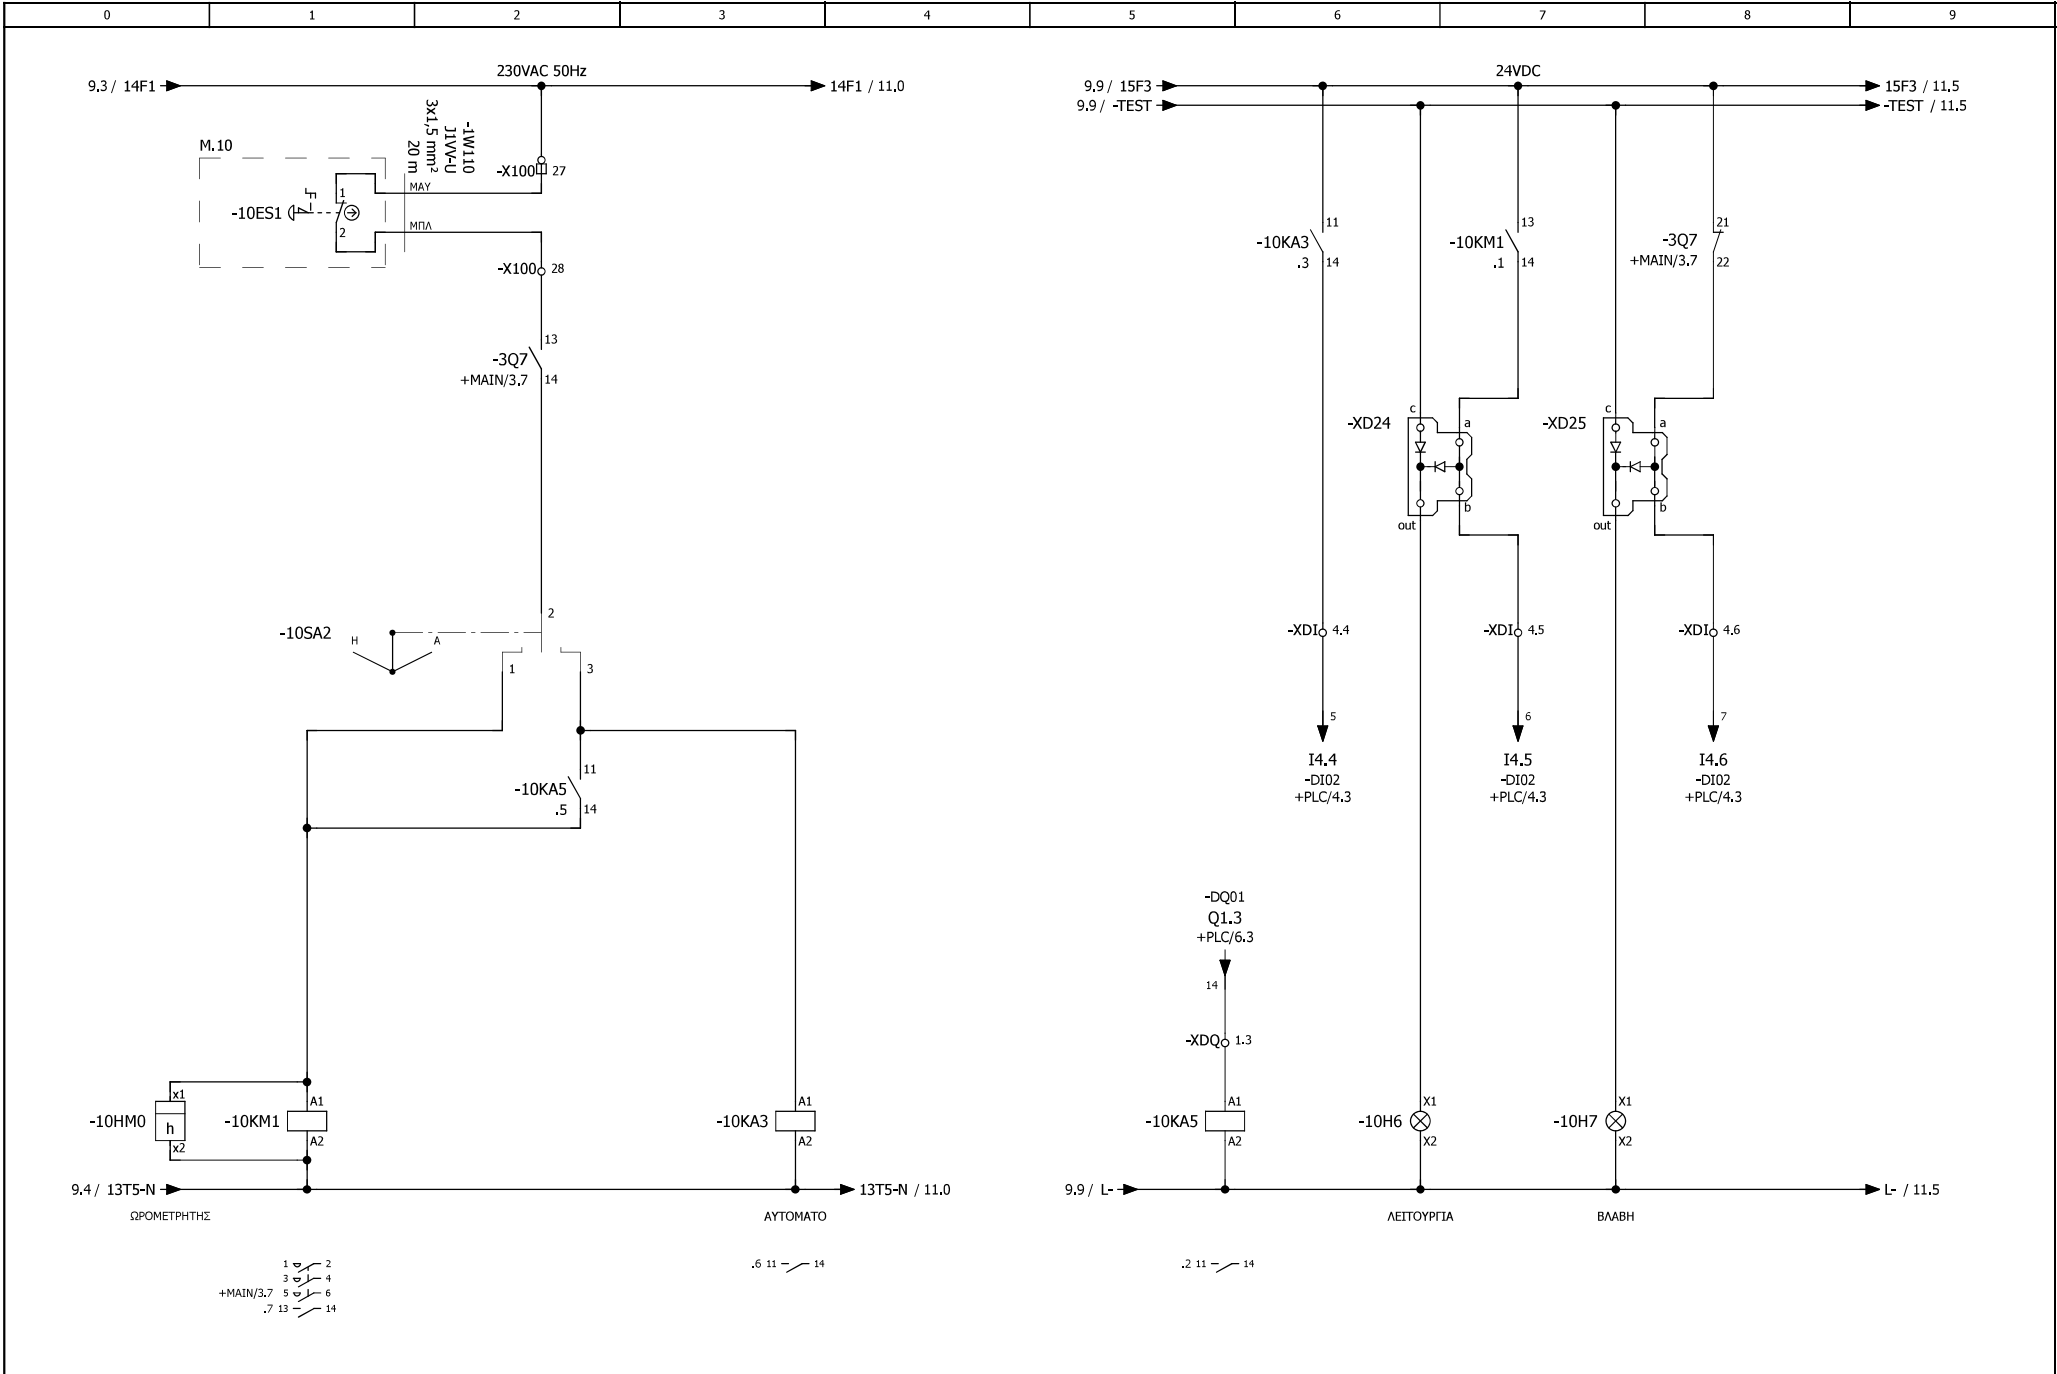


			ΗΜ/ΝΙΑ	19.09.2019	ΑΡ. ΣΧΕΔΙΟΥ	ΕΡΓΟ	ΕΡΓΟ ΑΝΑΒΑΘΜΙΣΗΣ ΚΑΙ ΕΠΕΚΤΑΣΗΣ ΤΗΣ	ΑΝΕΜΙΣΤΗΡΑΣ ΧΩΡΟΥ ΟΖΟΝΙΣΤΗΡΑ ΠΡΟΟΖΟΝΩΣΗΣ	= MCC-01
			ΜΕΛΕΤΗ		ΕΡΓΟ	ΕΓΚΑΤΑΣΤΑΣΗΣ ΕΠΕΞΕΡΓΑΣΙΑΣ ΛΥΜΑΤΩΝ (ΕΕΛ)		M02-01-19	+ CONTROL
	09.04.2019		ΣΧΕΔΙΟ		ΠΕΛΑΤΗΣ	ΑΓΙΟΥ ΝΙΚΟΛΑΟΥ			ΦΥΛΛΟ: 10
ΑΛΛΑΓΗ	ΗΜ/ΝΙΑ	ΟΝΟΜΑ	ΘΕΩΡ.		ΠΕΡΙΓΡΑΦΗ ΠΙΝΑΚΑ	ΠΙΝΑΚΑΣ ΕΡΓΩΝ ΕΙΣΟΔΟΥ			ΤΕΛ. ΦΥΛΛΟ: 23

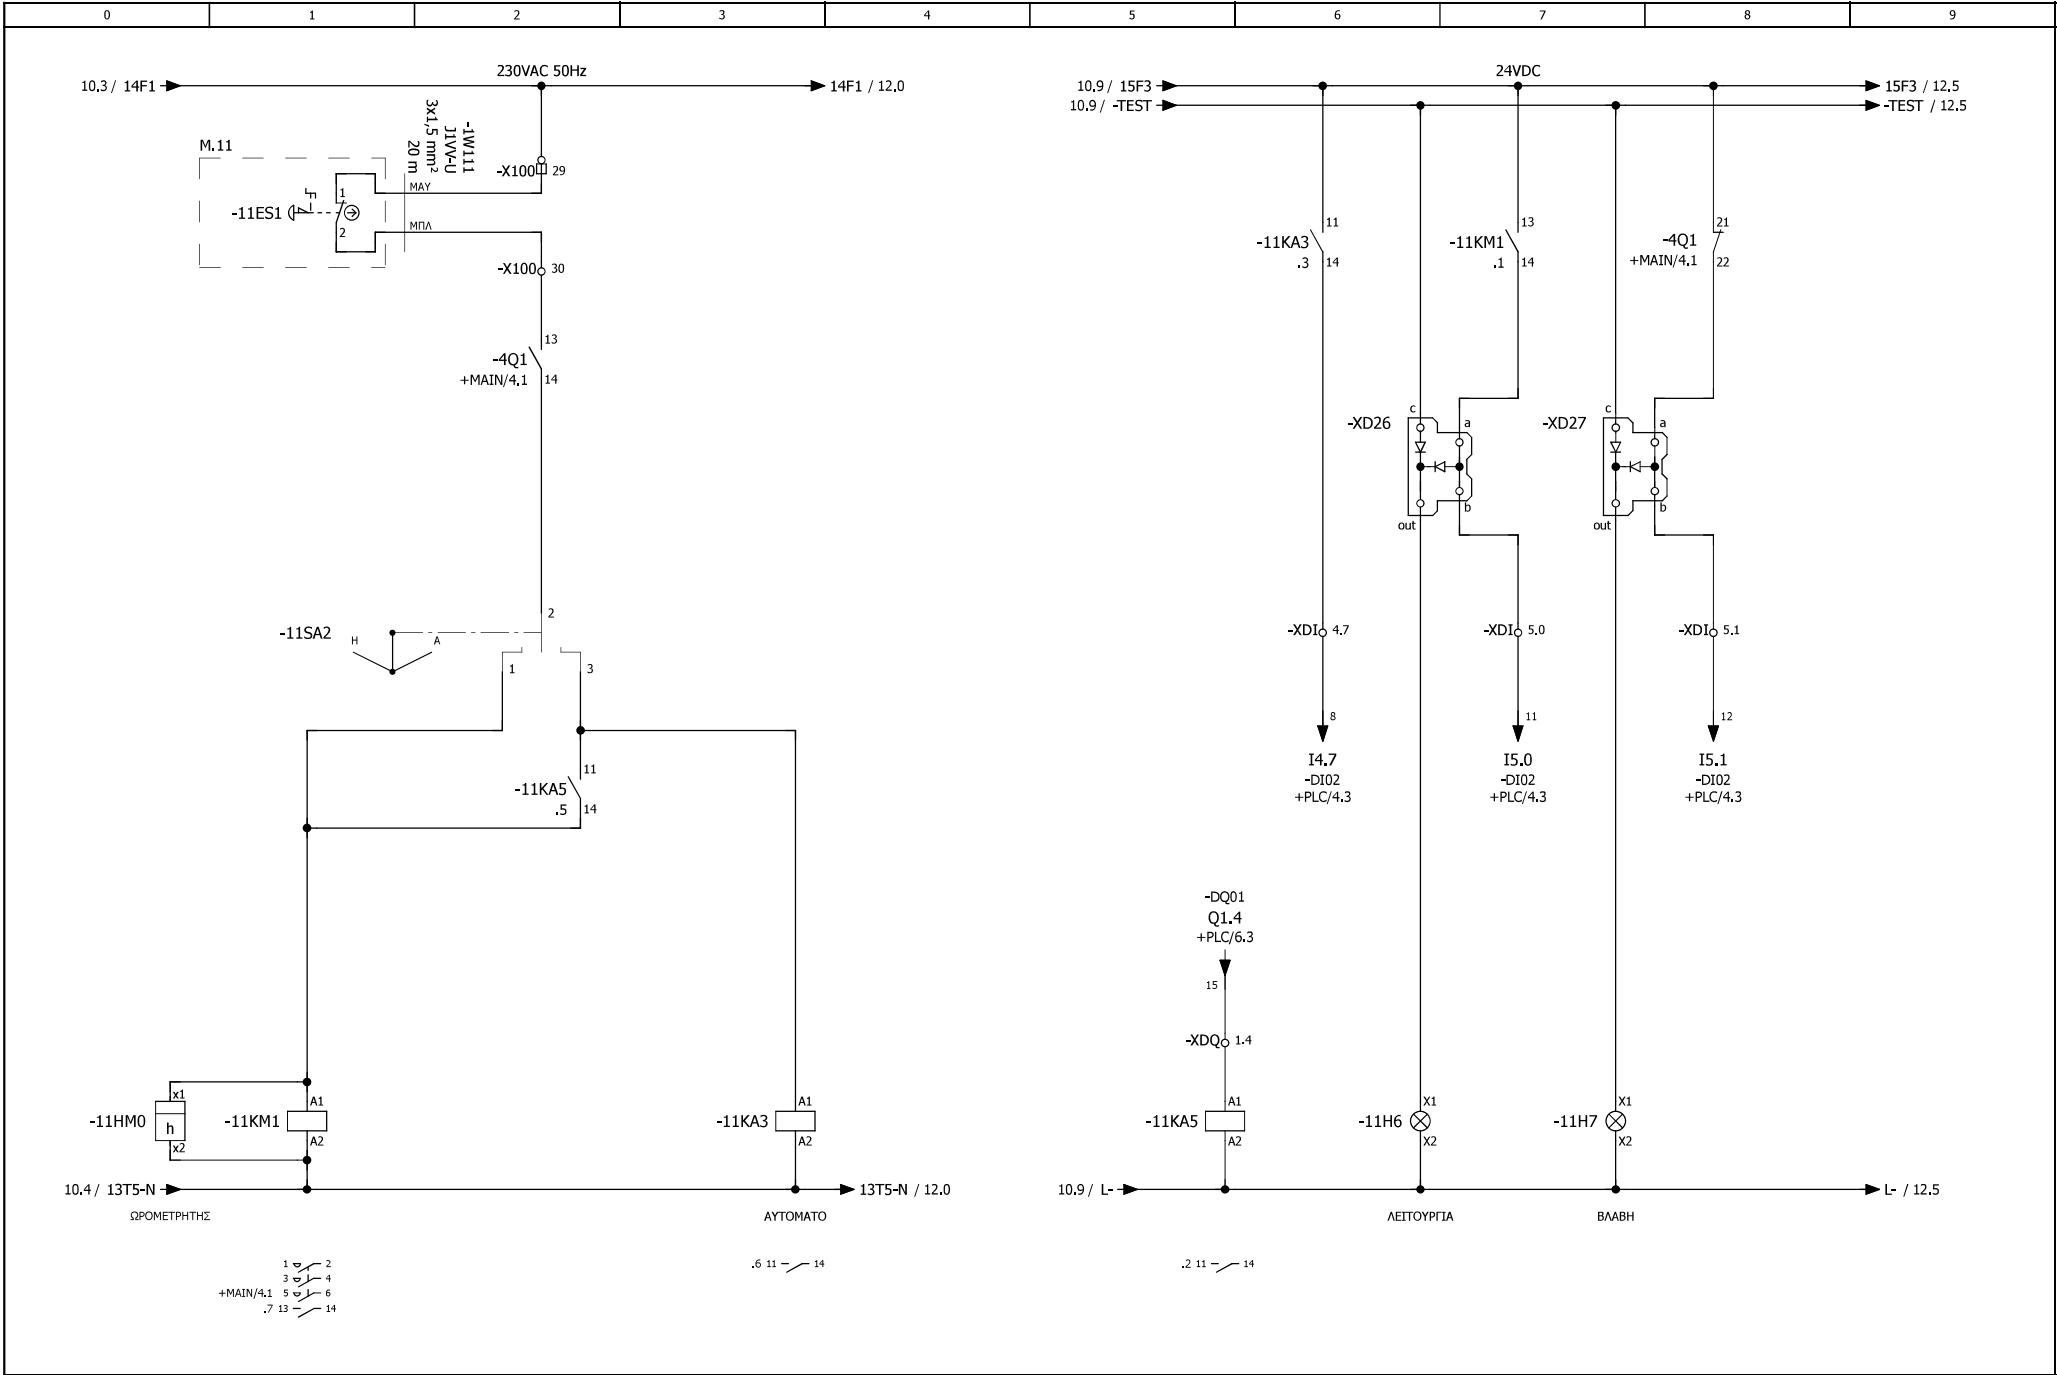


		ΗΜ/ΝΙΑ	19.09.2019	ΑΡ. ΣΧΕΔΙΟΥ : ΕΡΓΟ ΑΝΑΒΑΘΜΙΣΗΣ ΚΑΙ ΕΠΕΚΤΑΣΗΣ ΤΗΣ ΕΡΓΟ : ΕΓΚΑΤΑΣΤΑΣΗΣ ΕΠΕΞΕΡΓΑΣΙΑΣ ΛΥΜΑΤΩΝ (ΕΕΛ) ΠΕΛΑΤΗΣ : ΑΓΙΟΥ ΝΙΚΟΛΑΟΥ ΠΕΡΙΓΡΑΦΗ ΠΙΝΑΚΑ : ΠΙΝΑΚΑΣ ΕΡΓΩΝ ΕΙΣΟΔΟΥ	ΑΝΕΜΙΣΤΗΡΑΣ EMERGENSY ΠΡΟΟΖΟΝΩΣΗΣ M02-01-20	= MCC-01
		ΜΕΛΕΤΗ				+ CONTROL
09.04.2019		ΣΧΕΔΙΟ				ΦΥΛΛΟ: 11
ΑΛΛΑΓΗ	ΗΜ/ΝΙΑ	ΟΝΟΜΑ	ΘΕΩΡ.			ΤΕΛ. ΦΥΛΛΟ: 23

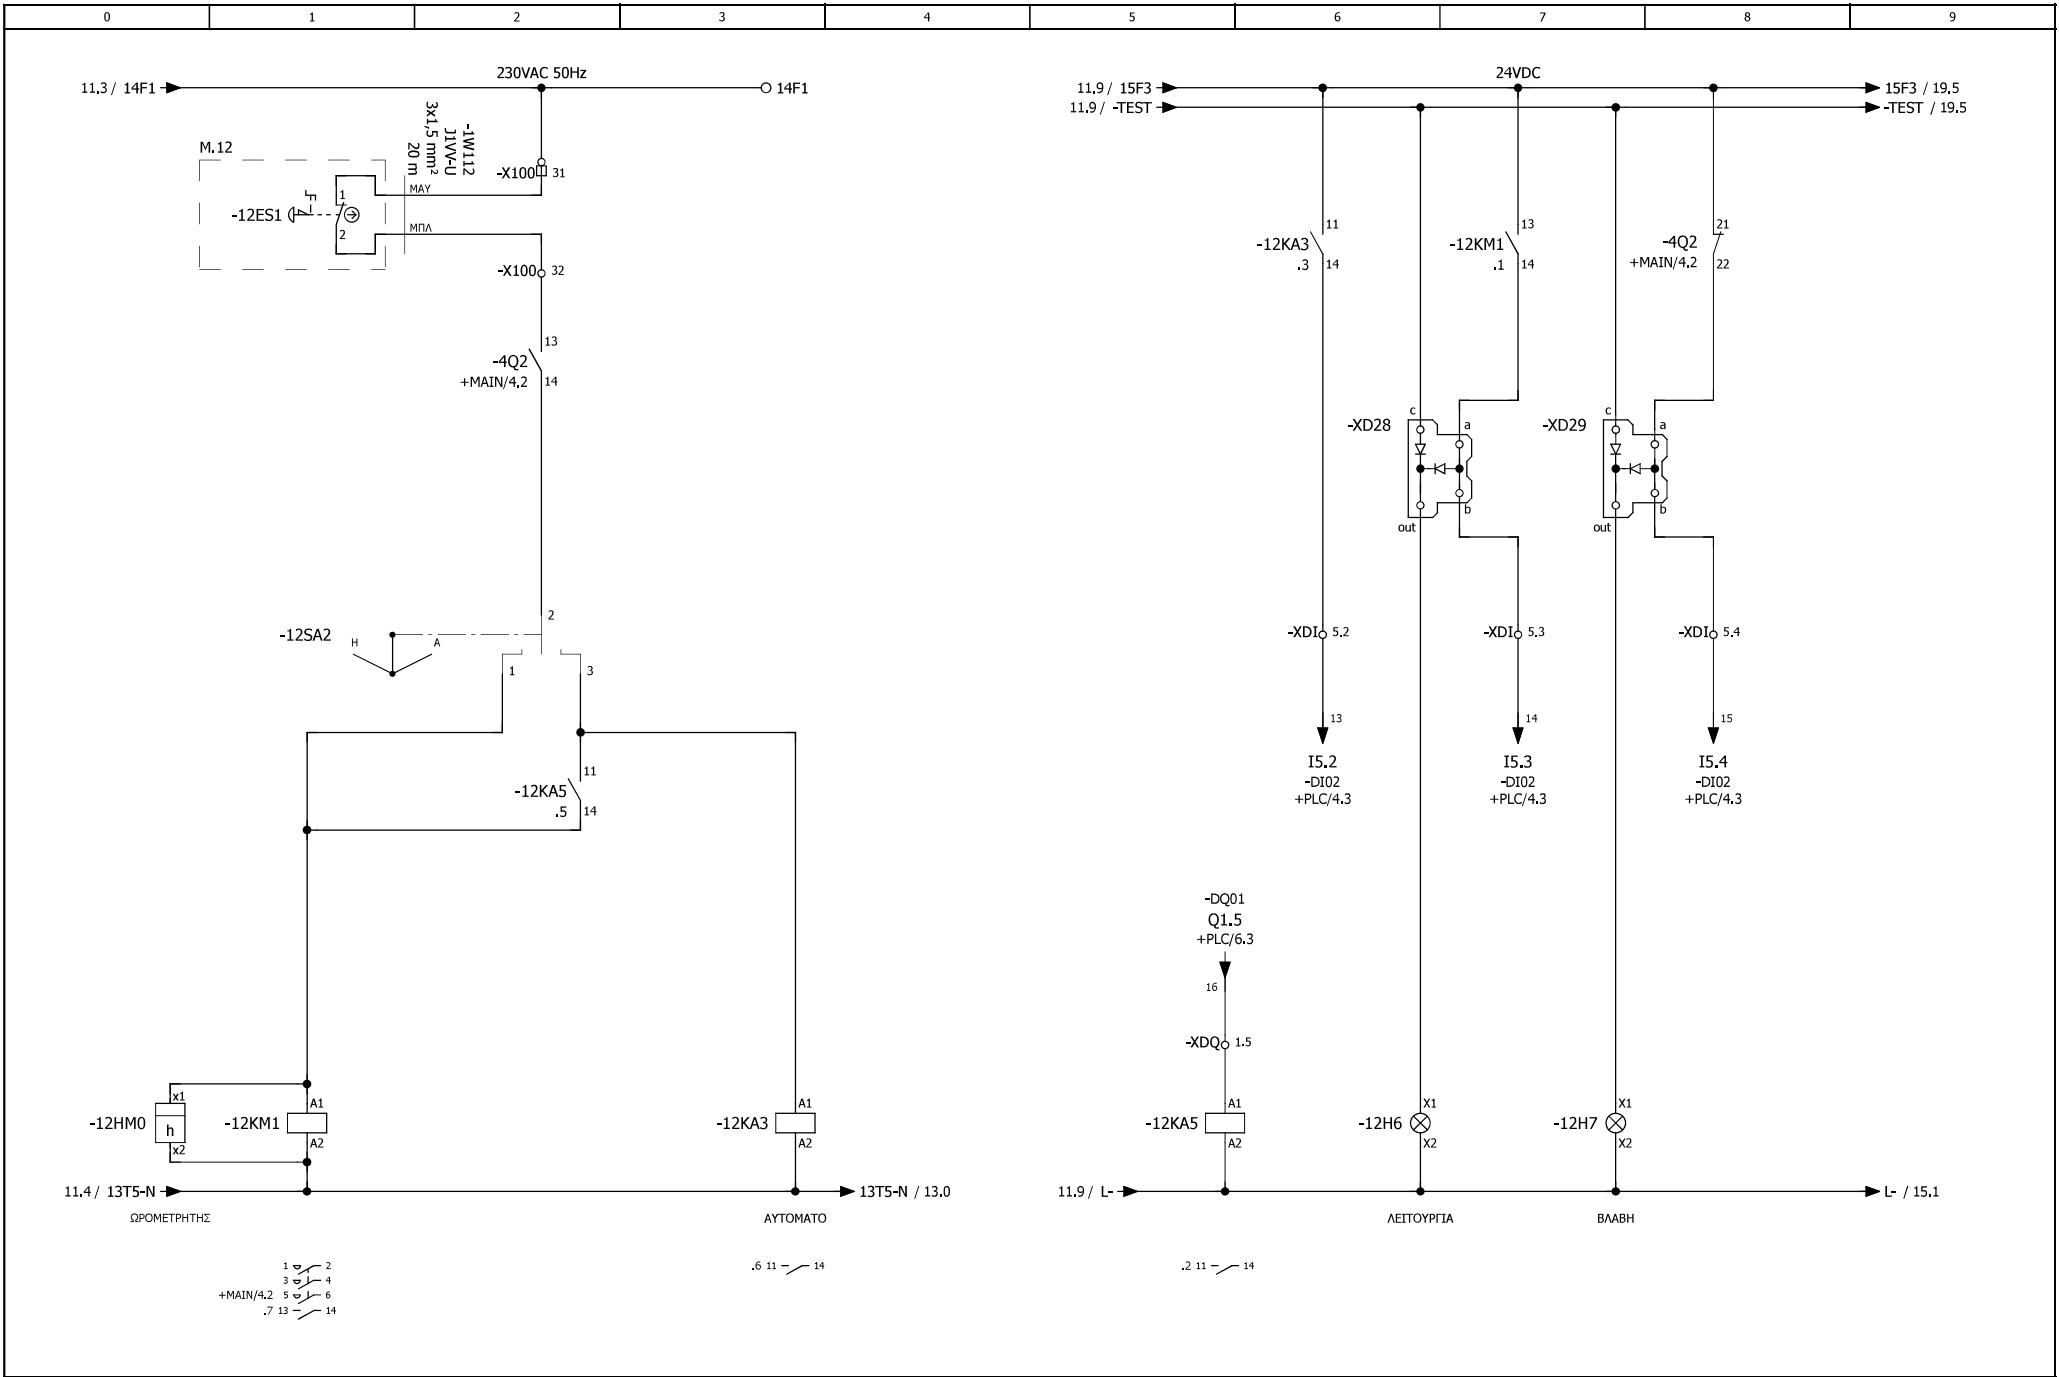


		ΗΜ/ΝΙΑ	19.09.2019	ΑΡ. ΣΧΕΔΙΟΥ	ΕΡΓΟ ΑΝΑΒΑΘΜΙΣΗΣ ΚΑΙ ΕΠΕΚΤΑΣΗΣ ΤΗΣ	ΑΝΤΛΙΑ ΤΡΟΦΟΔΟΣΙΑΣ ΟΡΓΑΝΟΥ ΜΕΤΡΗΣΗΣ ΔΙΑΛΥΜΕΝΟΥ	= MCC-01
		ΜΕΛΕΤΗ		ΕΡΓΟ	ΕΓΚΑΤΑΣΤΑΣΗΣ ΕΠΕΞΕΡΓΑΣΙΑΣ ΛΥΜΑΤΩΝ (ΕΕΛ)	ΟΖΟΝΤΟΣ ΣΤΟ ΝΕΡΟ Μ02-01-28	+ CONTROL
09.04.2019		ΣΧΕΔΙΟ		ΠΕΛΑΤΗΣ	ΑΓΙΟΥ ΝΙΚΟΛΑΟΥ		ΦΥΛΛΟ: 12
ΑΛΛΑΓΗ	ΗΜ/ΝΙΑ	ΟΝΟΜΑ	ΘΕΩΡ.	ΠΕΡΙΓΡΑΦΗ ΠΙΝΑΚΑ	ΠΙΝΑΚΑΣ ΕΡΓΩΝ ΕΙΣΟΔΟΥ		ΤΕΛ. ΦΥΛΛΟ: 23

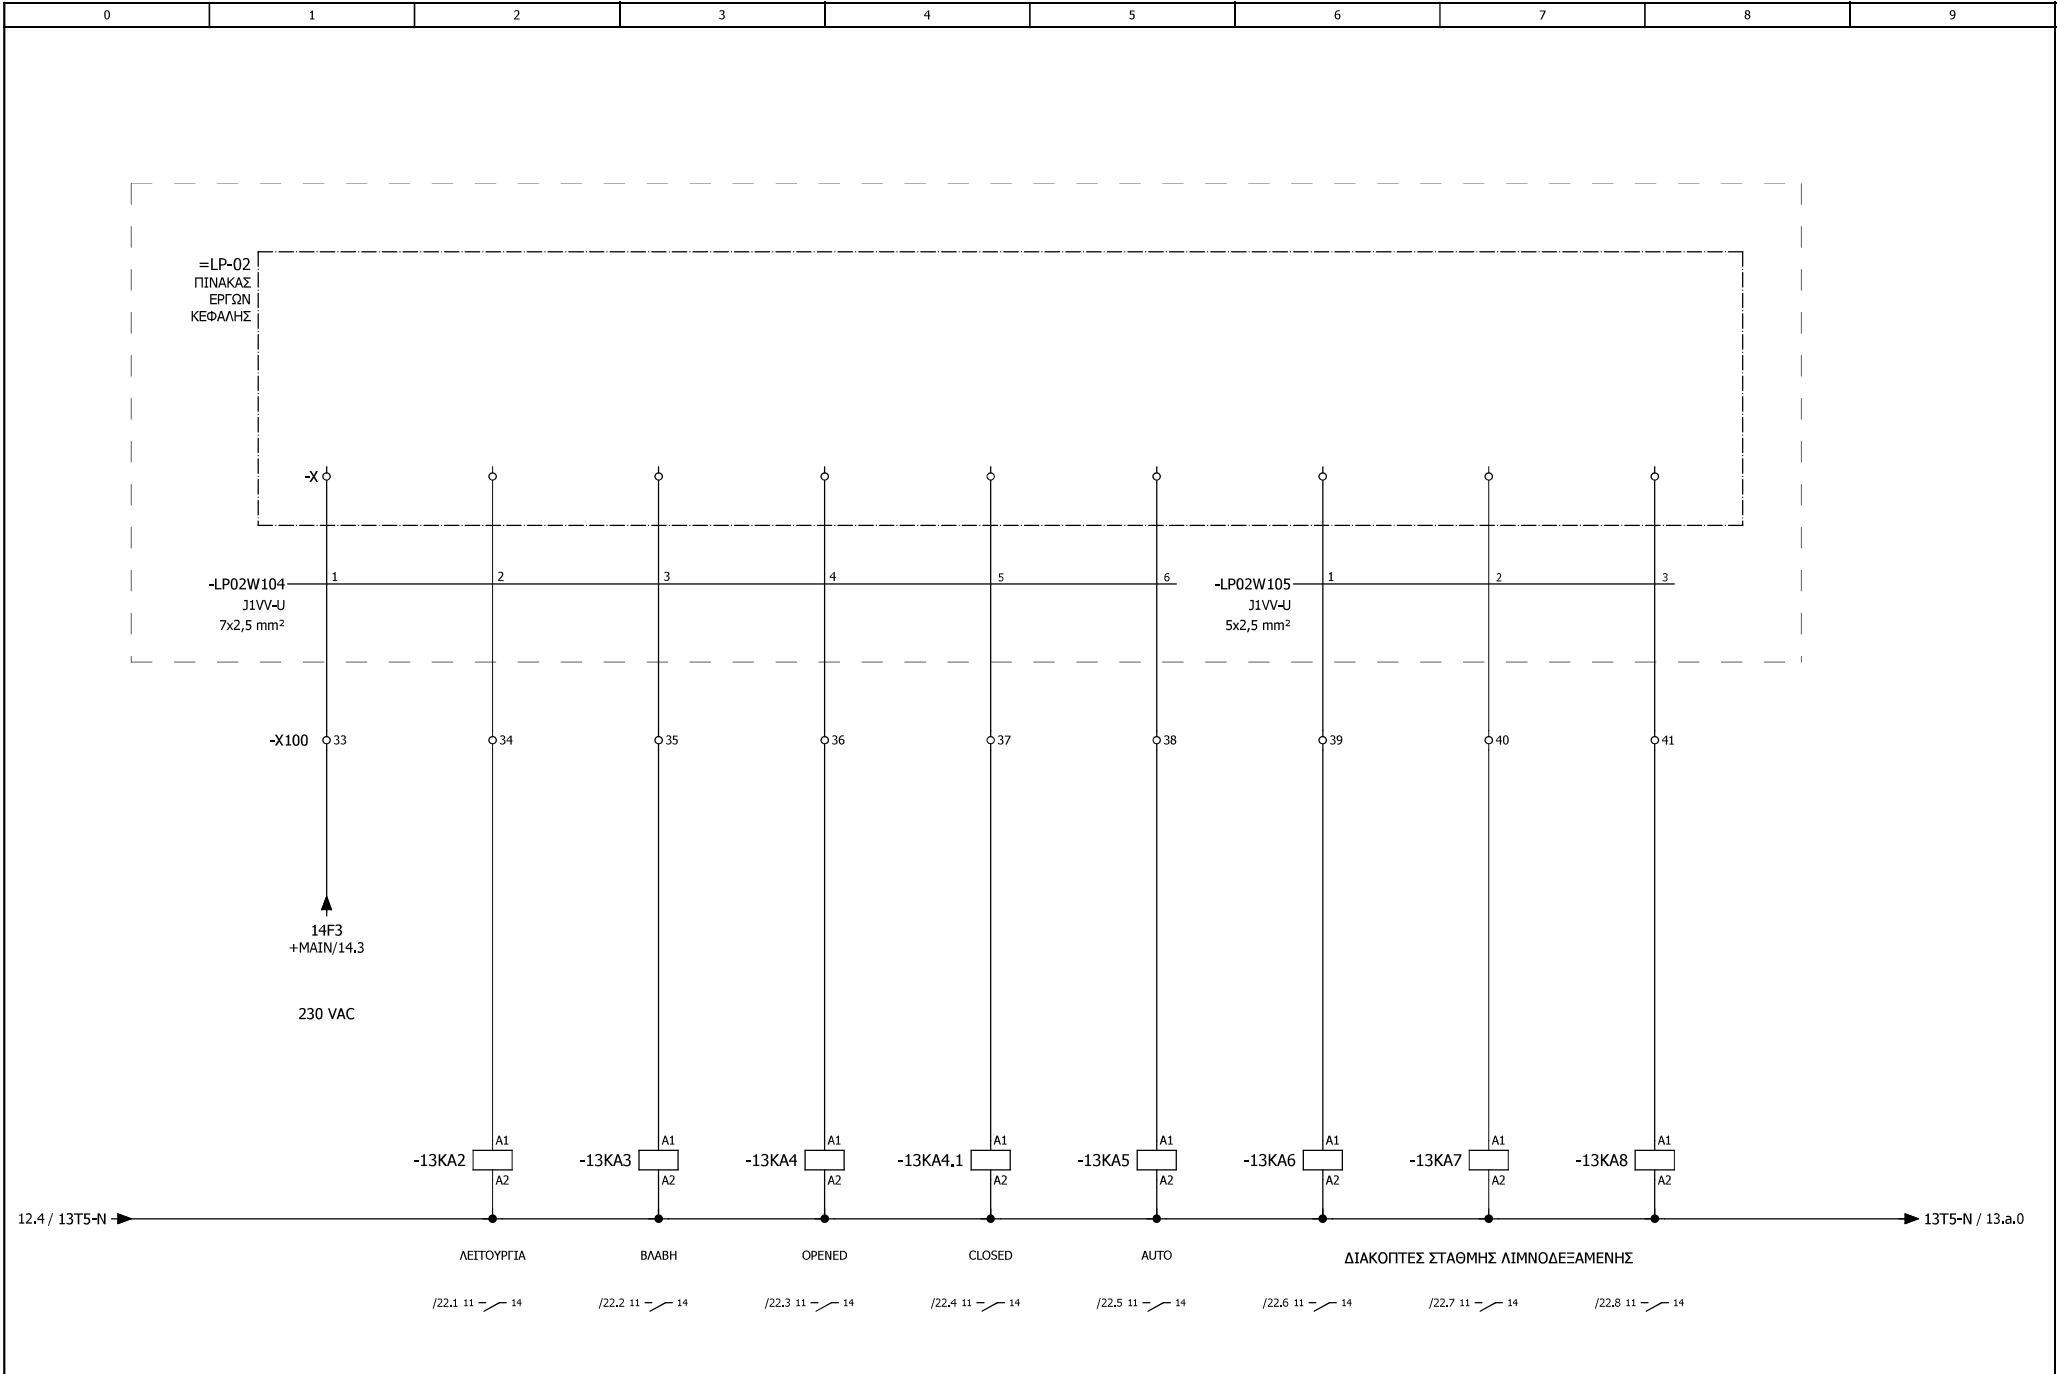

			ΗΜ/ΝΙΑ	19.09.2019	ΑΡ. ΣΧΕΔΙΟΥ : ΕΡΓΟ ΑΝΑΒΑΘΜΙΣΗΣ ΚΑΙ ΕΠΕΚΤΑΣΗΣ ΤΗΣ ΕΡΓΟ : ΕΓΚΑΤΑΣΤΑΣΗΣ ΕΠΕΞΕΡΓΑΣΙΑΣ ΛΥΜΑΤΩΝ (ΕΕΛ) ΠΕΛΑΤΗΣ : ΑΓΙΟΥ ΝΙΚΟΛΑΟΥ ΠΕΡΙΓΡΑΦΗ ΠΙΝΑΚΑ : ΠΙΝΑΚΑΣ ΕΡΓΩΝ ΕΙΣΟΔΟΥ	ΣΗΜΑΤΑ ΑΠΟ ΠΙΝΑΚΑ ΕΡΓΩΝ ΚΕΦΑΛΗΣ LP-02	= MCC-01 + CONTROL ΦΥΛΛΟ: 13 ΤΕΛ. ΦΥΛΛΟ: 23
			ΜΕΛΕΤΗ				
	09.04.2019		ΣΧΕΔΙΟ				
ΑΛΛΑΓΗ	ΗΜ/ΝΙΑ	ΟΝΟΜΑ	ΘΕΩΡ.				

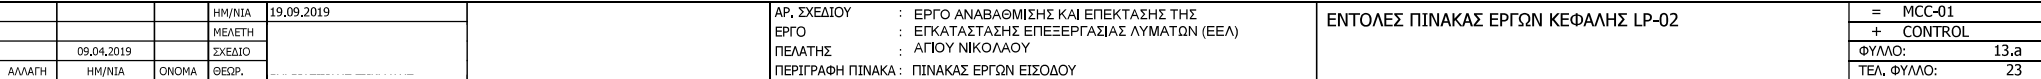


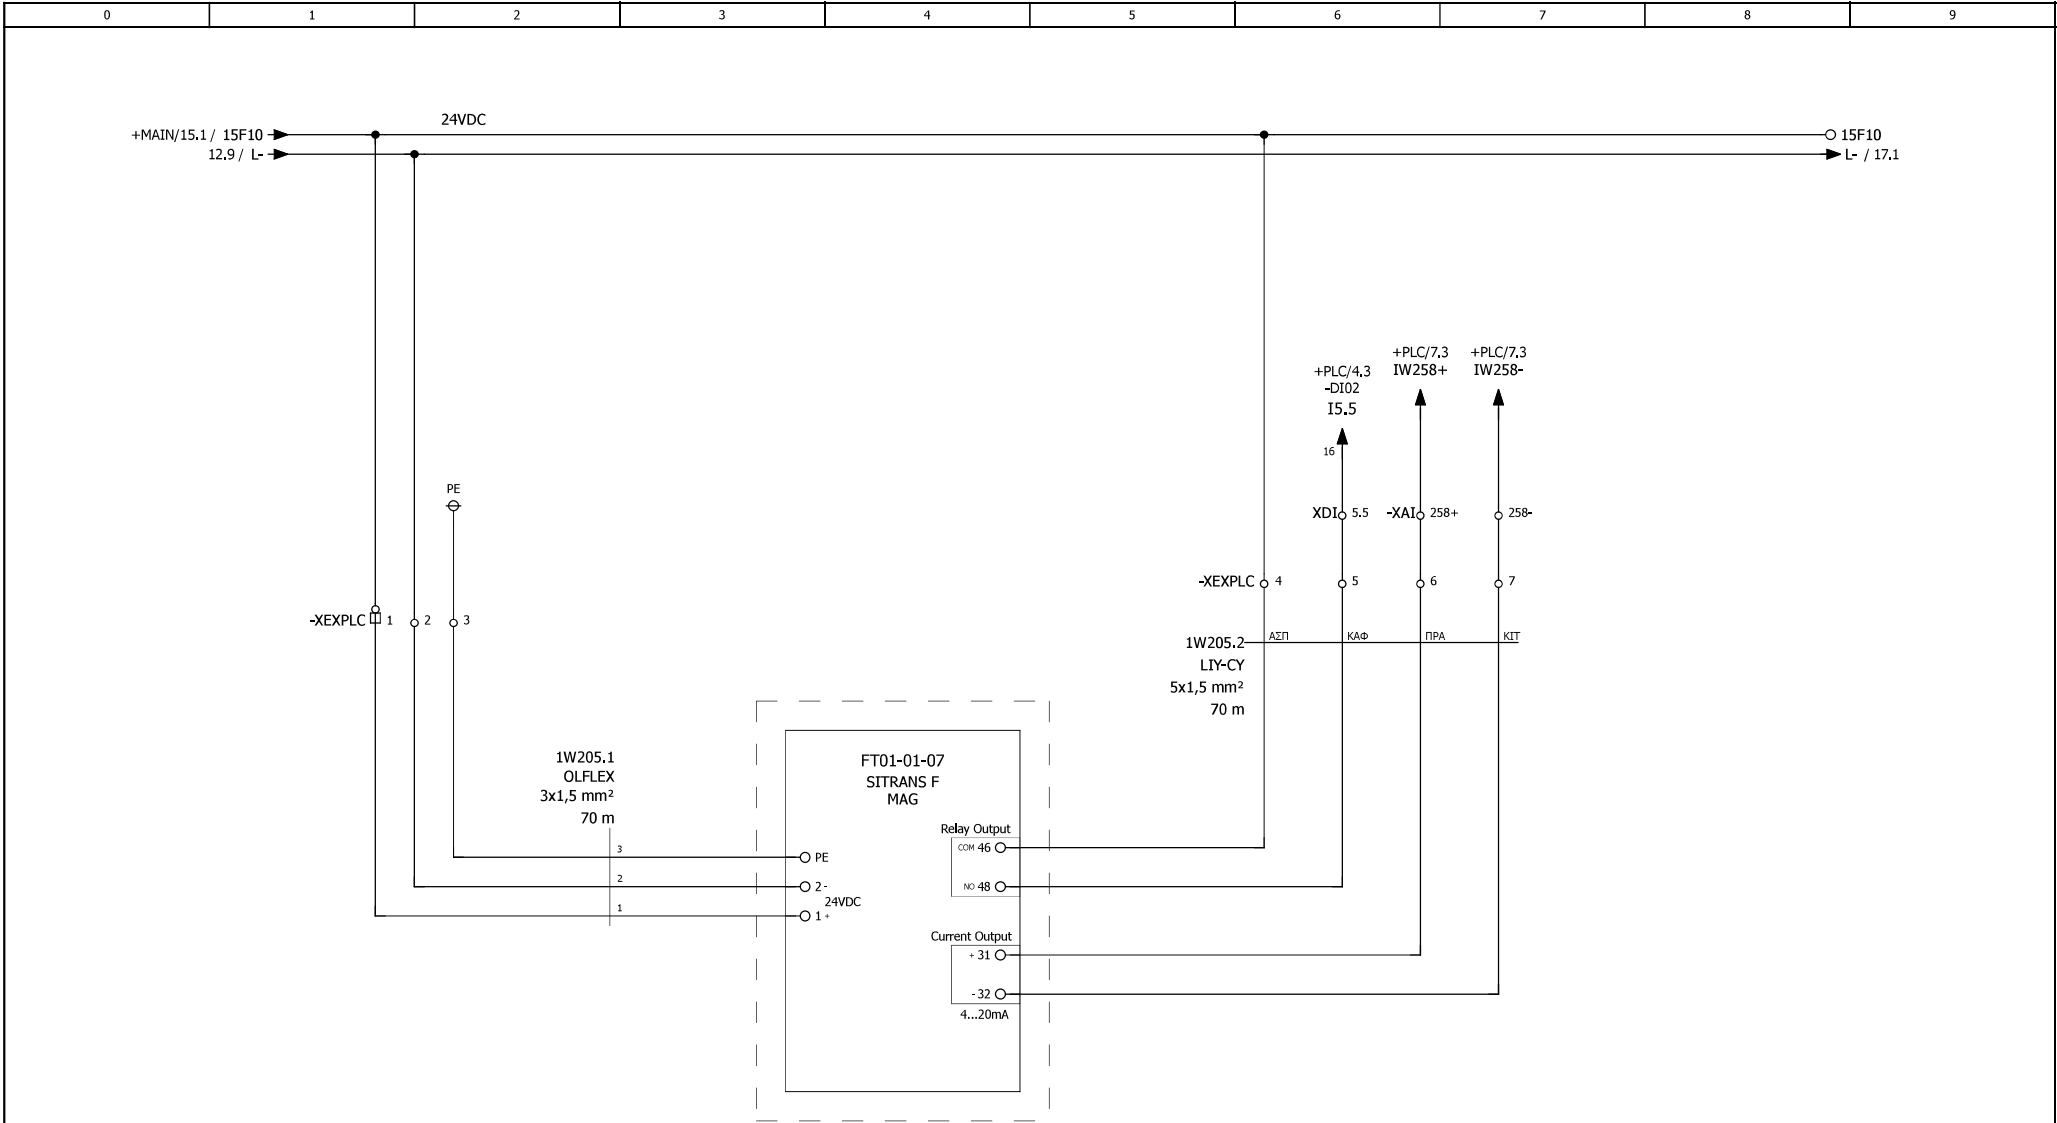


ΗΛΕΚΤΡΟΜΑΓΝΗΤΙΚΟΣ ΜΕΤΡΗΤΗΣ ΠΑΡΟΧΗΣ ΕΙΣΟΔΟΥ


			ΗΜ/ΝΙΑ	19.09.2019		ΑΡ. ΣΧΕΔΙΟΥ	: ΕΡΓΟ ΑΝΑΒΑΘΜΙΣΗΣ ΚΑΙ ΕΠΕΚΤΑΣΗΣ ΤΗΣ	ΗΛΕΚΤΡΟΜΑΓΝΗΤΙΚΟΣ ΜΕΤΡΗΣΗΣ ΠΑΡΟΧΗΣ ΕΙΣΟΔΟΥ	= MCC-01
			ΜΕΛΕΤΗ			ΕΡΓΟ	: ΕΓΚΑΤΑΣΤΑΣΗΣ ΕΠΕΞΕΡΓΑΣΙΑΣ ΛΥΜΑΤΩΝ (ΕΕΛ)	FT01-01-07	+ CONTROL
	09.04.2019		ΣΧΕΔΙΟ			ΠΕΛΑΤΗΣ	: ΑΓΙΟΥ ΝΙΚΟΛΑΟΥ		ΦΥΛΛΟ: 15
ΑΛΛΑΓΗ	ΗΜ/ΝΙΑ	ΟΝΟΜΑ	ΘΕΩΡ.			ΠΕΡΙΓΡΑΦΗ ΠΙΝΑΚΑ	: ΠΙΝΑΚΑΣ ΕΡΓΩΝ ΕΙΣΟΔΟΥ		ΤΕΛ. ΦΥΛΛΟ: 23

0	1	2	3	4	5	6	7	8	9
---	---	---	---	---	---	---	---	---	---

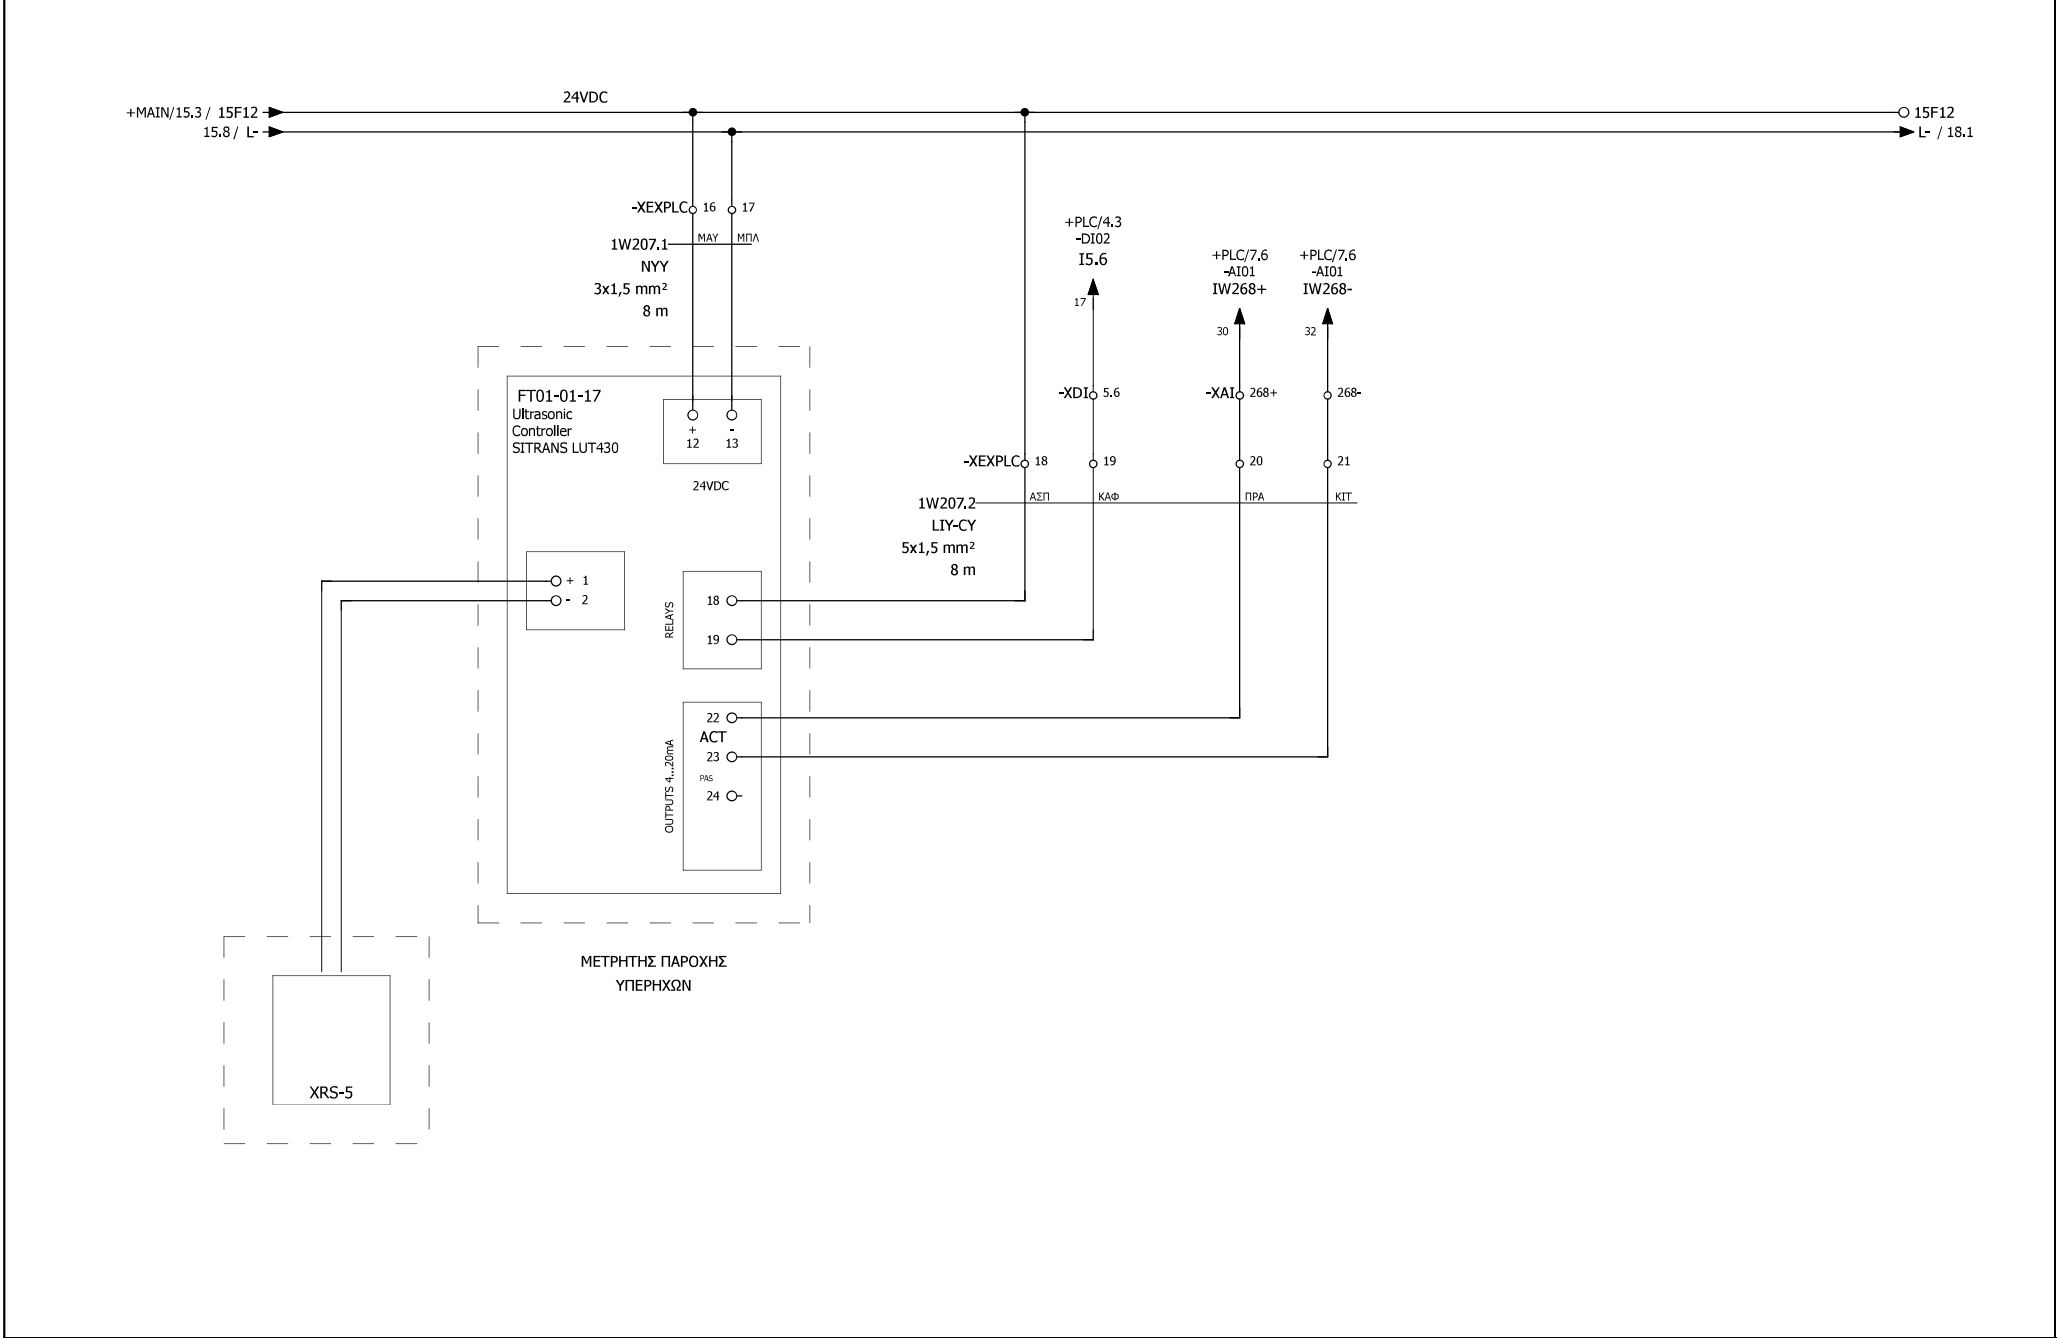



			ΗΜ/ΝΙΑ	19.09.2019	ΑΡ. ΣΧΕΔΙΟΥ : ΕΡΓΟ ΑΝΑΒΑΘΜΙΣΗΣ ΚΑΙ ΕΠΕΚΤΑΣΗΣ ΤΗΣ ΕΡΓΟ : ΕΓΚΑΤΑΣΤΑΣΗΣ ΕΠΕΞΕΡΓΑΣΙΑΣ ΛΥΜΑΤΩΝ (ΕΕΛ) ΠΕΛΑΤΗΣ : ΑΓΙΟΥ ΝΙΚΟΛΑΟΥ ΠΕΡΙΓΡΑΦΗ ΠΙΝΑΚΑ : ΠΙΝΑΚΑΣ ΕΡΓΩΝ ΕΙΣΟΔΟΥ	ΜΕΤΡΗΤΗΣ ΠΑΡΟΧΗΣ ΜΕ ΥΠΕΡΗΧΟΥΣ ΣΕ ΚΑΝΑΛΙ PARSHALL FT01-01-17	=	MCC-01
			ΜΕΛΕΤΗ				+	CONTROL
	09.04.2019		ΣΧΕΔΙΟ				ΦΥΛΛΟ:	17
ΑΛΛΑΓΗ	ΗΜ/ΝΙΑ	ΟΝΟΜΑ	ΘΕΩΡ.				ΤΕΛ. ΦΥΛΛΟ:	23

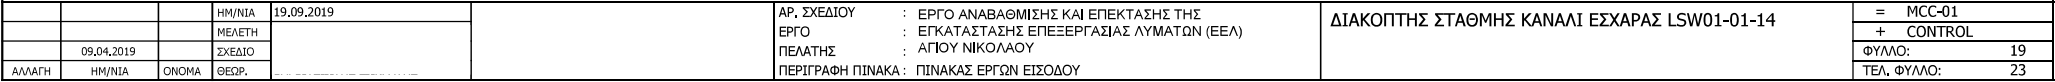

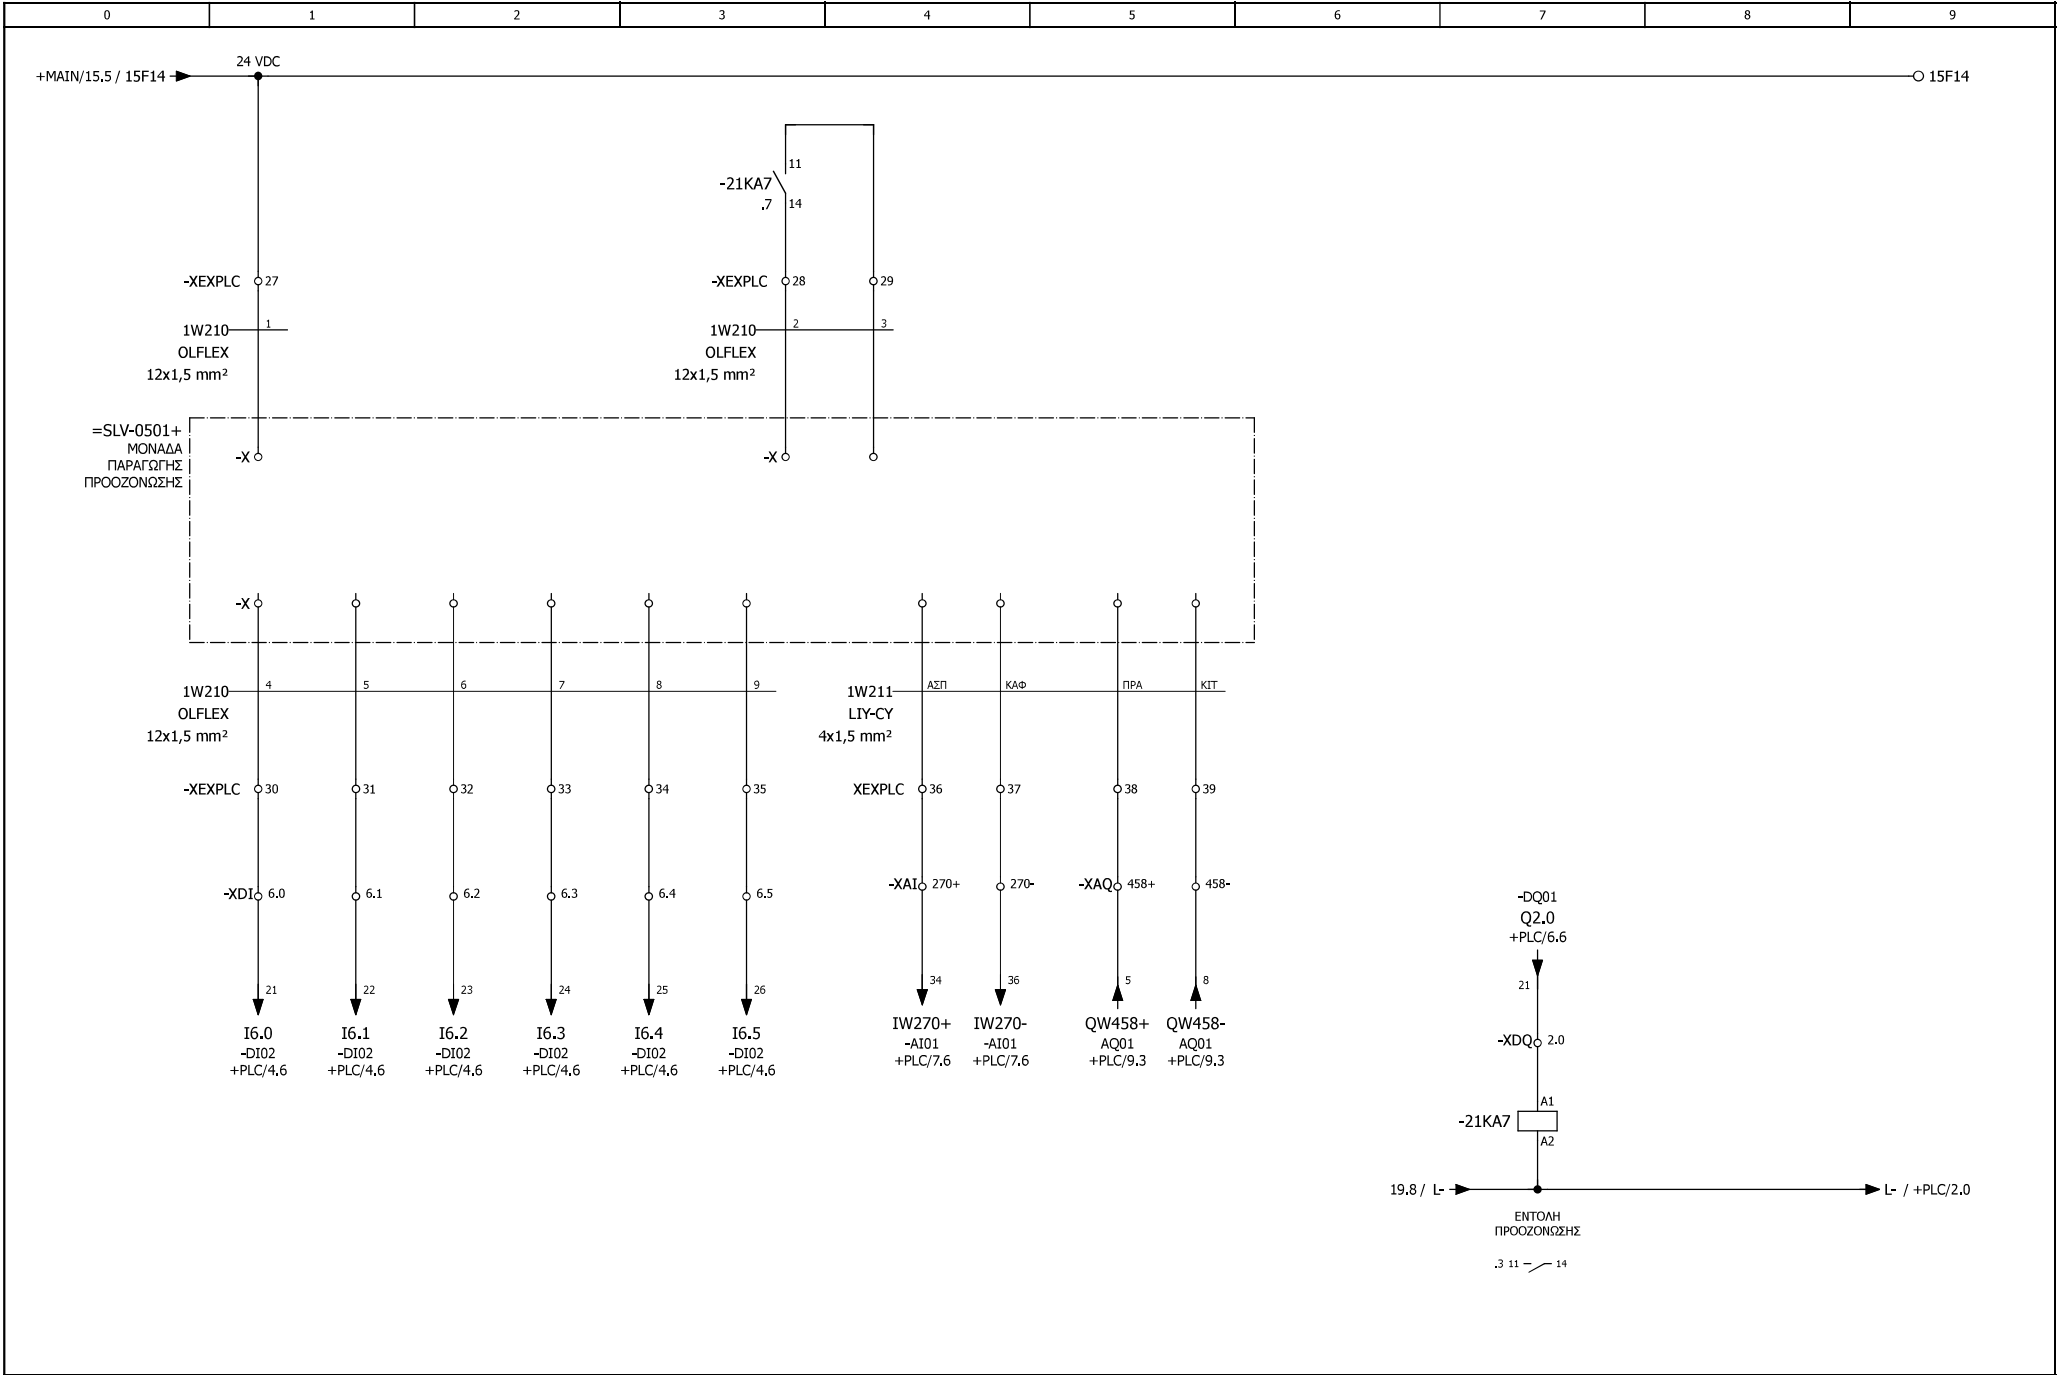



			ΗΜ/ΝΙΑ	19.09.2019	ΑΡ. ΣΧΕΔΙΟΥ : ΕΡΓΟ ΑΝΑΒΑΘΜΙΣΗΣ ΚΑΙ ΕΠΕΚΤΑΣΗΣ ΤΗΣ ΕΡΓΟ : ΕΓΚΑΤΑΣΤΑΣΗΣ ΕΠΕΞΕΡΓΑΣΙΑΣ ΛΥΜΑΤΩΝ (ΕΕΛ) ΠΕΛΑΤΗΣ : ΑΓΙΟΥ ΝΙΚΟΛΑΟΥ ΠΕΡΙΓΡΑΦΗ ΠΙΝΑΚΑ : ΠΙΝΑΚΑΣ ΕΡΓΩΝ ΕΙΣΟΔΟΥ	ΣΗΜΑΤΑ ΠΡΟΟΖΩΣΗΣ	= MCC-01 + CONTROL ΦΥΛΛΟ: 21 ΤΕΛ. ΦΥΛΛΟ: 23
			ΜΕΛΕΤΗ				
	09.04.2019		ΣΧΕΔΙΟ				
ΑΛΛΑΓΗ	ΗΜ/ΝΙΑ	ΟΝΟΜΑ	ΘΕΩΡ.				

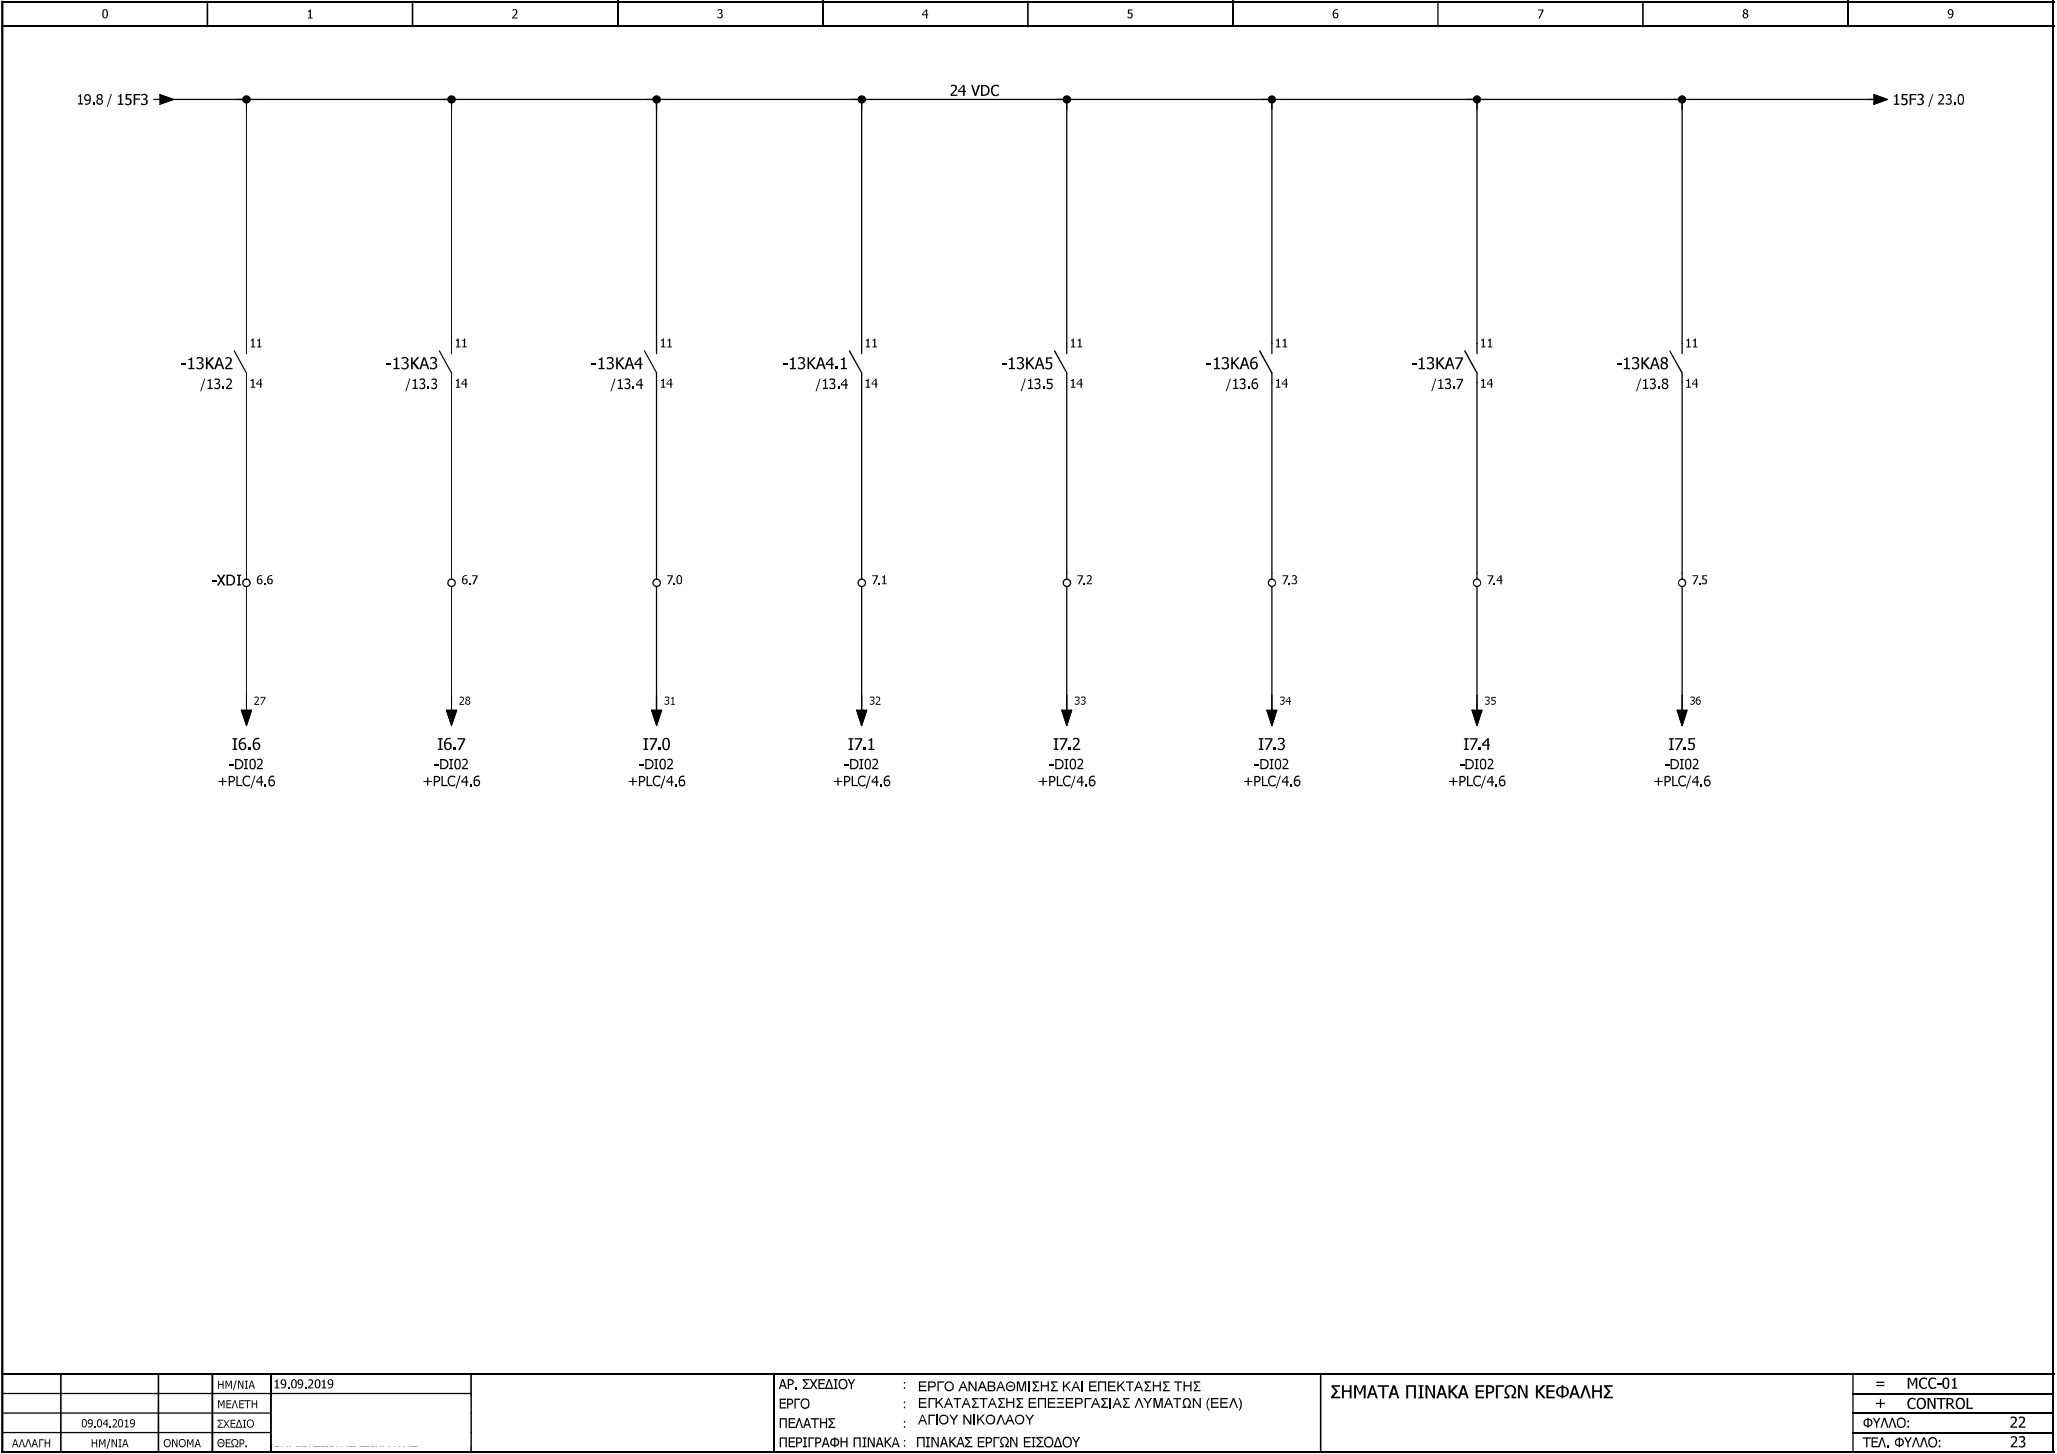

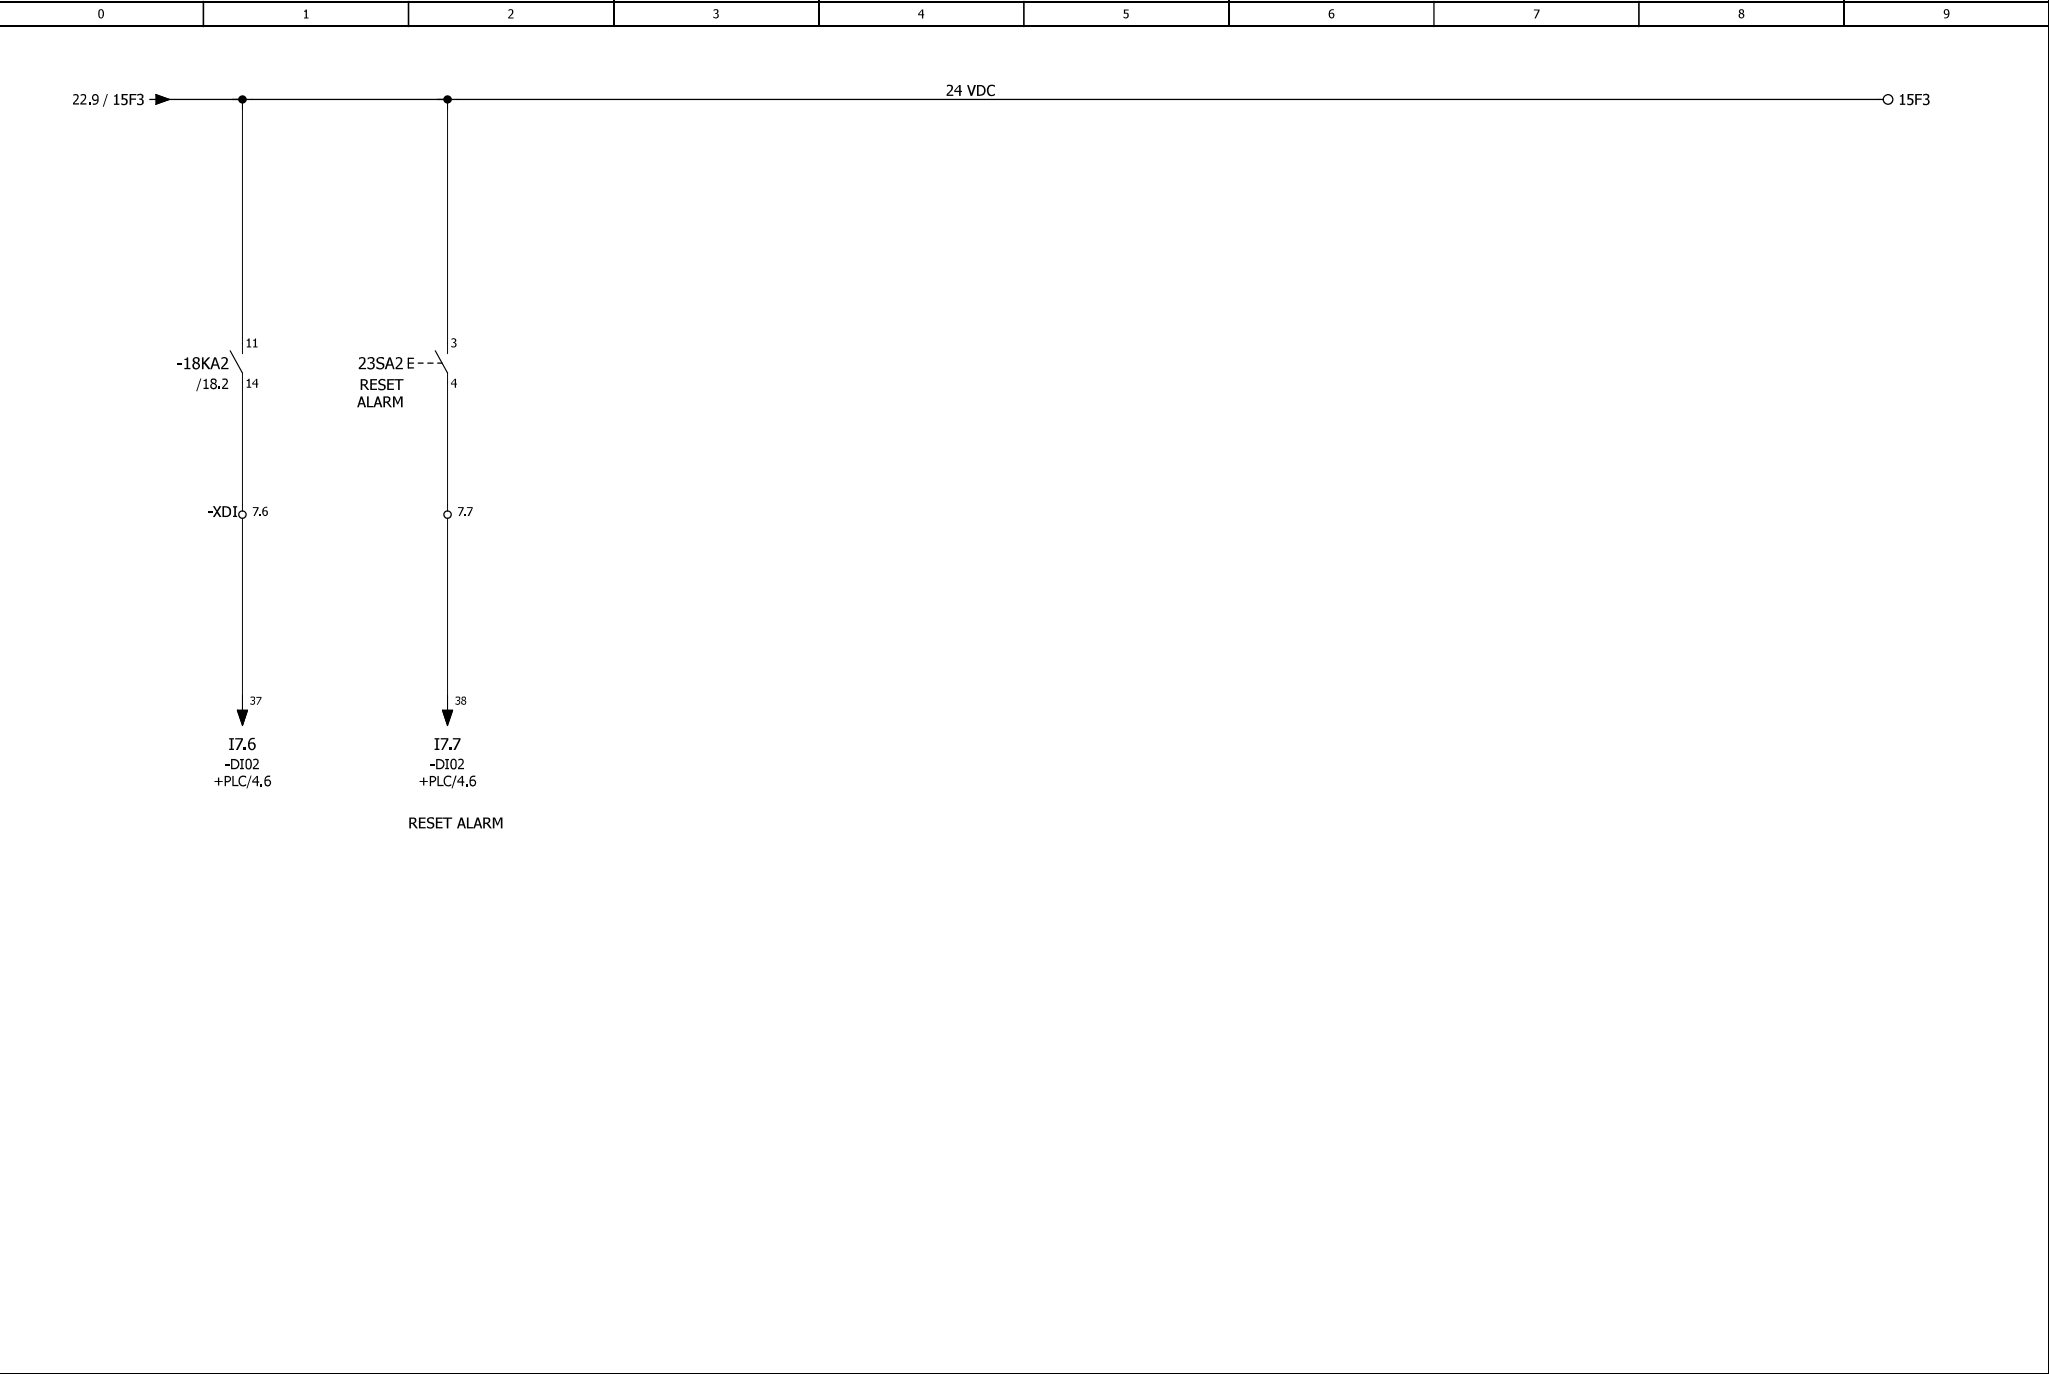

			ΗΜ/ΝΙΑ	19.09.2019		ΑΡ. ΣΧΕΔΙΟΥ : ΕΡΓΟ ΑΝΑΒΑΘΜΙΣΗΣ ΚΑΙ ΕΠΕΚΤΑΣΗΣ ΤΗΣ ΕΡΓΟ : ΕΓΚΑΤΑΣΤΑΣΗΣ ΕΠΕΞΕΡΓΑΣΙΑΣ ΛΥΜΑΤΩΝ (ΕΕΛ) ΠΕΛΑΤΗΣ : ΑΓΙΟΥ ΝΙΚΟΛΑΟΥ ΠΕΡΙΓΡΑΦΗ ΠΙΝΑΚΑ : ΠΙΝΑΚΑΣ ΕΡΓΩΝ ΕΙΣΟΔΟΥ	ΣΗΜΑΤΑ ΠΡΟΣ PLC	=	MCC-01
			ΜΕΛΕΤΗ					+	CONTROL
	09.04.2019		ΣΧΕΔΙΟ					ΦΥΛΛΟ:	23
ΑΛΛΑΓΗ	ΗΜ/ΝΙΑ	ΟΝΟΜΑ	ΘΕΩΡ.					ΤΕΛ. ΦΥΛΛΟ:	23

0	1	2	3	4	5	6	7	8	9
---	---	---	---	---	---	---	---	---	---

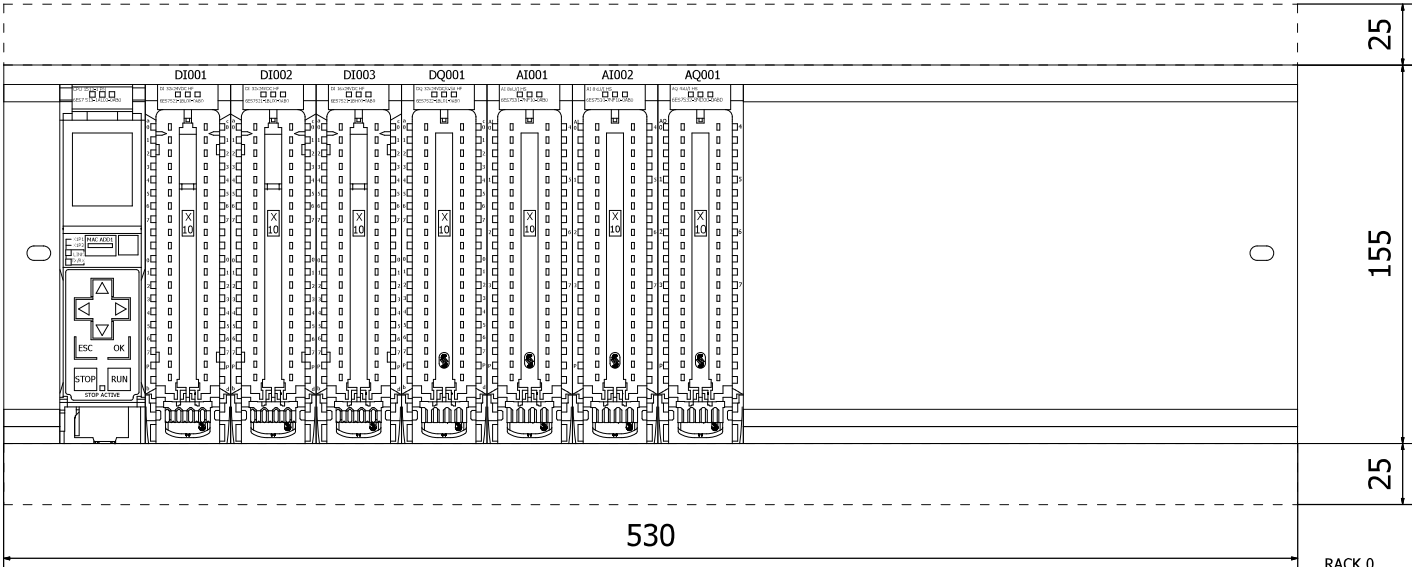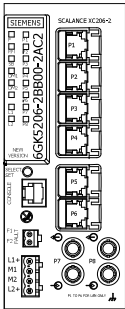


*Minimum clearances


*Minimum clearances

RACK 0
6ES7590-1AF30-0AA0
SIMATIC S7-1500, mounting rail 530 mm


			ΗΜ/ΝΙΑ	19.09.2019		ΑΡ. ΣΧΕΔΙΟΥ	: ΕΡΓΟ ΑΝΑΒΑΘΜΙΣΗΣ ΚΑΙ ΕΠΕΚΤΑΣΗΣ ΤΗΣ	ΓΕΝΙΚΗ ΔΙΑΤΑΞΗ PLC & SCALANCE	=	MCC-01
			ΜΕΛΕΤΗ			ΕΡΓΟ	: ΕΓΚΑΤΑΣΤΑΣΗΣ ΕΠΕΞΕΡΓΑΣΙΑΣ ΛΥΜΑΤΩΝ (ΕΕΛ)		+	PLC
	09.04.2019		ΣΧΕΔΙΟ			ΠΕΛΑΤΗΣ	: ΑΓΙΟΥ ΝΙΚΟΛΑΟΥ		ΦΥΛΛΟ:	1
ΑΛΛΑΓΗ	ΗΜ/ΝΙΑ	ΟΝΟΜΑ	ΘΕΩΡ.			ΠΕΡΙΓΡΑΦΗ ΠΙΝΑΚΑ	: ΠΙΝΑΚΑΣ ΕΡΓΩΝ ΕΙΣΟΔΟΥ		ΤΕΛ. ΦΥΛΛΟ:	9

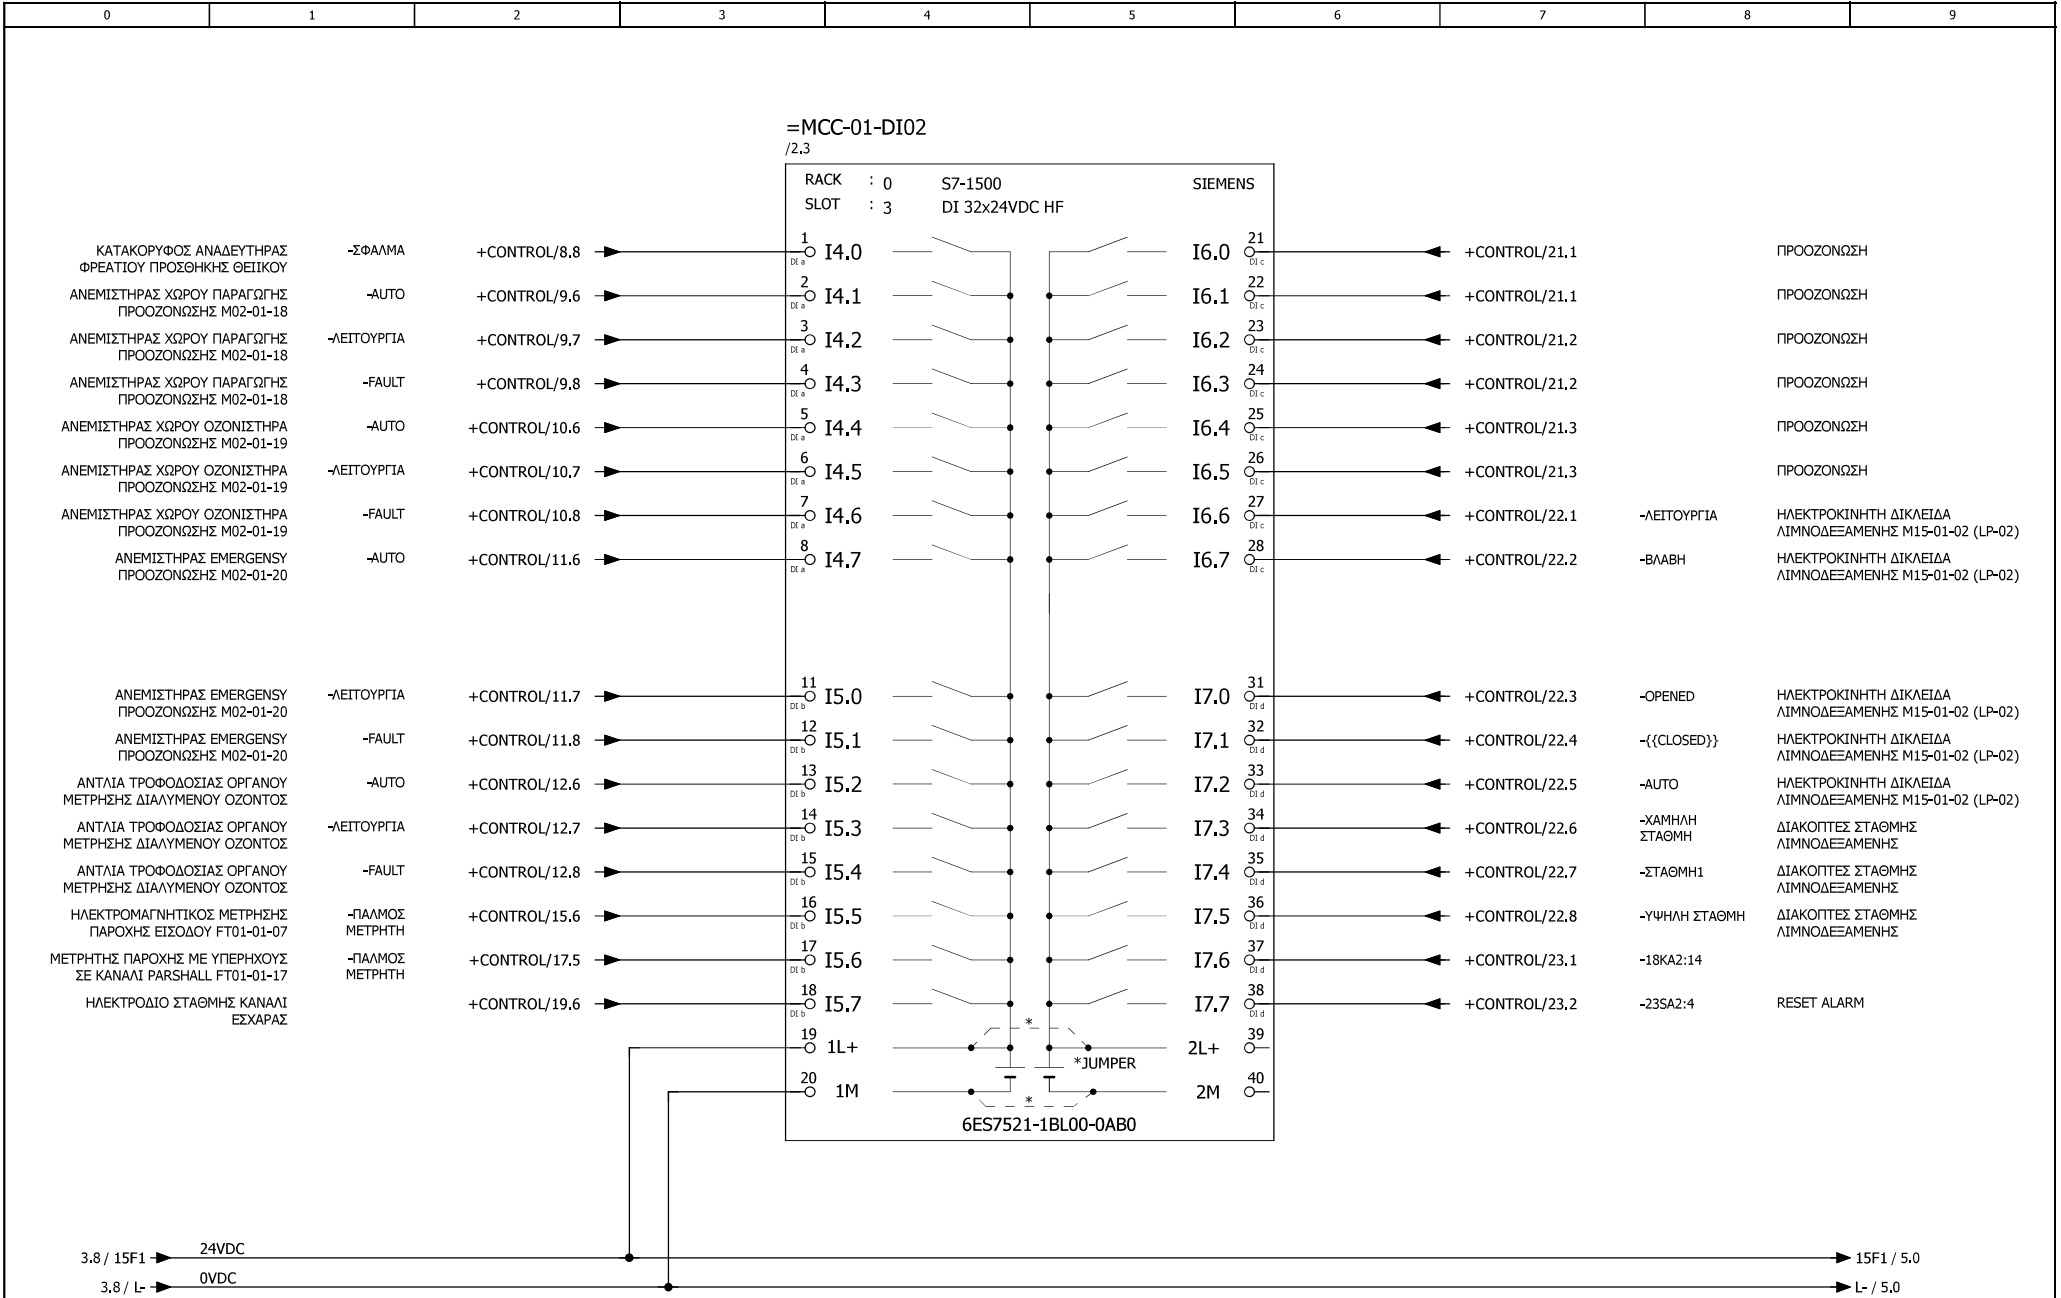


		ΗΜ/ΝΙΑ	19.09.2019	ΑΡ. ΣΧΕΔΙΟΥ : ΕΡΓΟ ΑΝΑΒΑΘΜΙΣΗΣ ΚΑΙ ΕΠΕΚΤΑΣΗΣ ΤΗΣ	ΦΥΛΙΑΚΗ ΚΑΡΤΑ ΕΙΣΟΔΩΝ ΠΛΑΙΣΙΟ 0, ΘΕΣΗ 3	= MCC-01
		ΜΕΛΕΤΗ		ΕΡΓΟ : ΕΓΚΑΤΑΣΤΑΣΗΣ ΕΠΕΞΕΡΓΑΣΙΑΣ ΛΥΜΑΤΩΝ (ΕΕΛ)		+ PLC
	09.04.2019	ΣΧΕΔΙΟ		ΠΕΛΑΤΗΣ : ΑΓΙΟΥ ΝΙΚΟΛΑΟΥ		ΦΥΛΛΟ: 4
ΑΛΛΑΓΗ	ΗΜ/ΝΙΑ	ΟΝΟΜΑ	ΘΕΩΡ.	ΠΕΡΙΓΡΑΦΗ ΠΙΝΑΚΑ : ΠΙΝΑΚΑΣ ΕΡΓΩΝ ΕΙΣΟΔΟΥ		ΤΕΛ. ΦΥΛΛΟ: 9

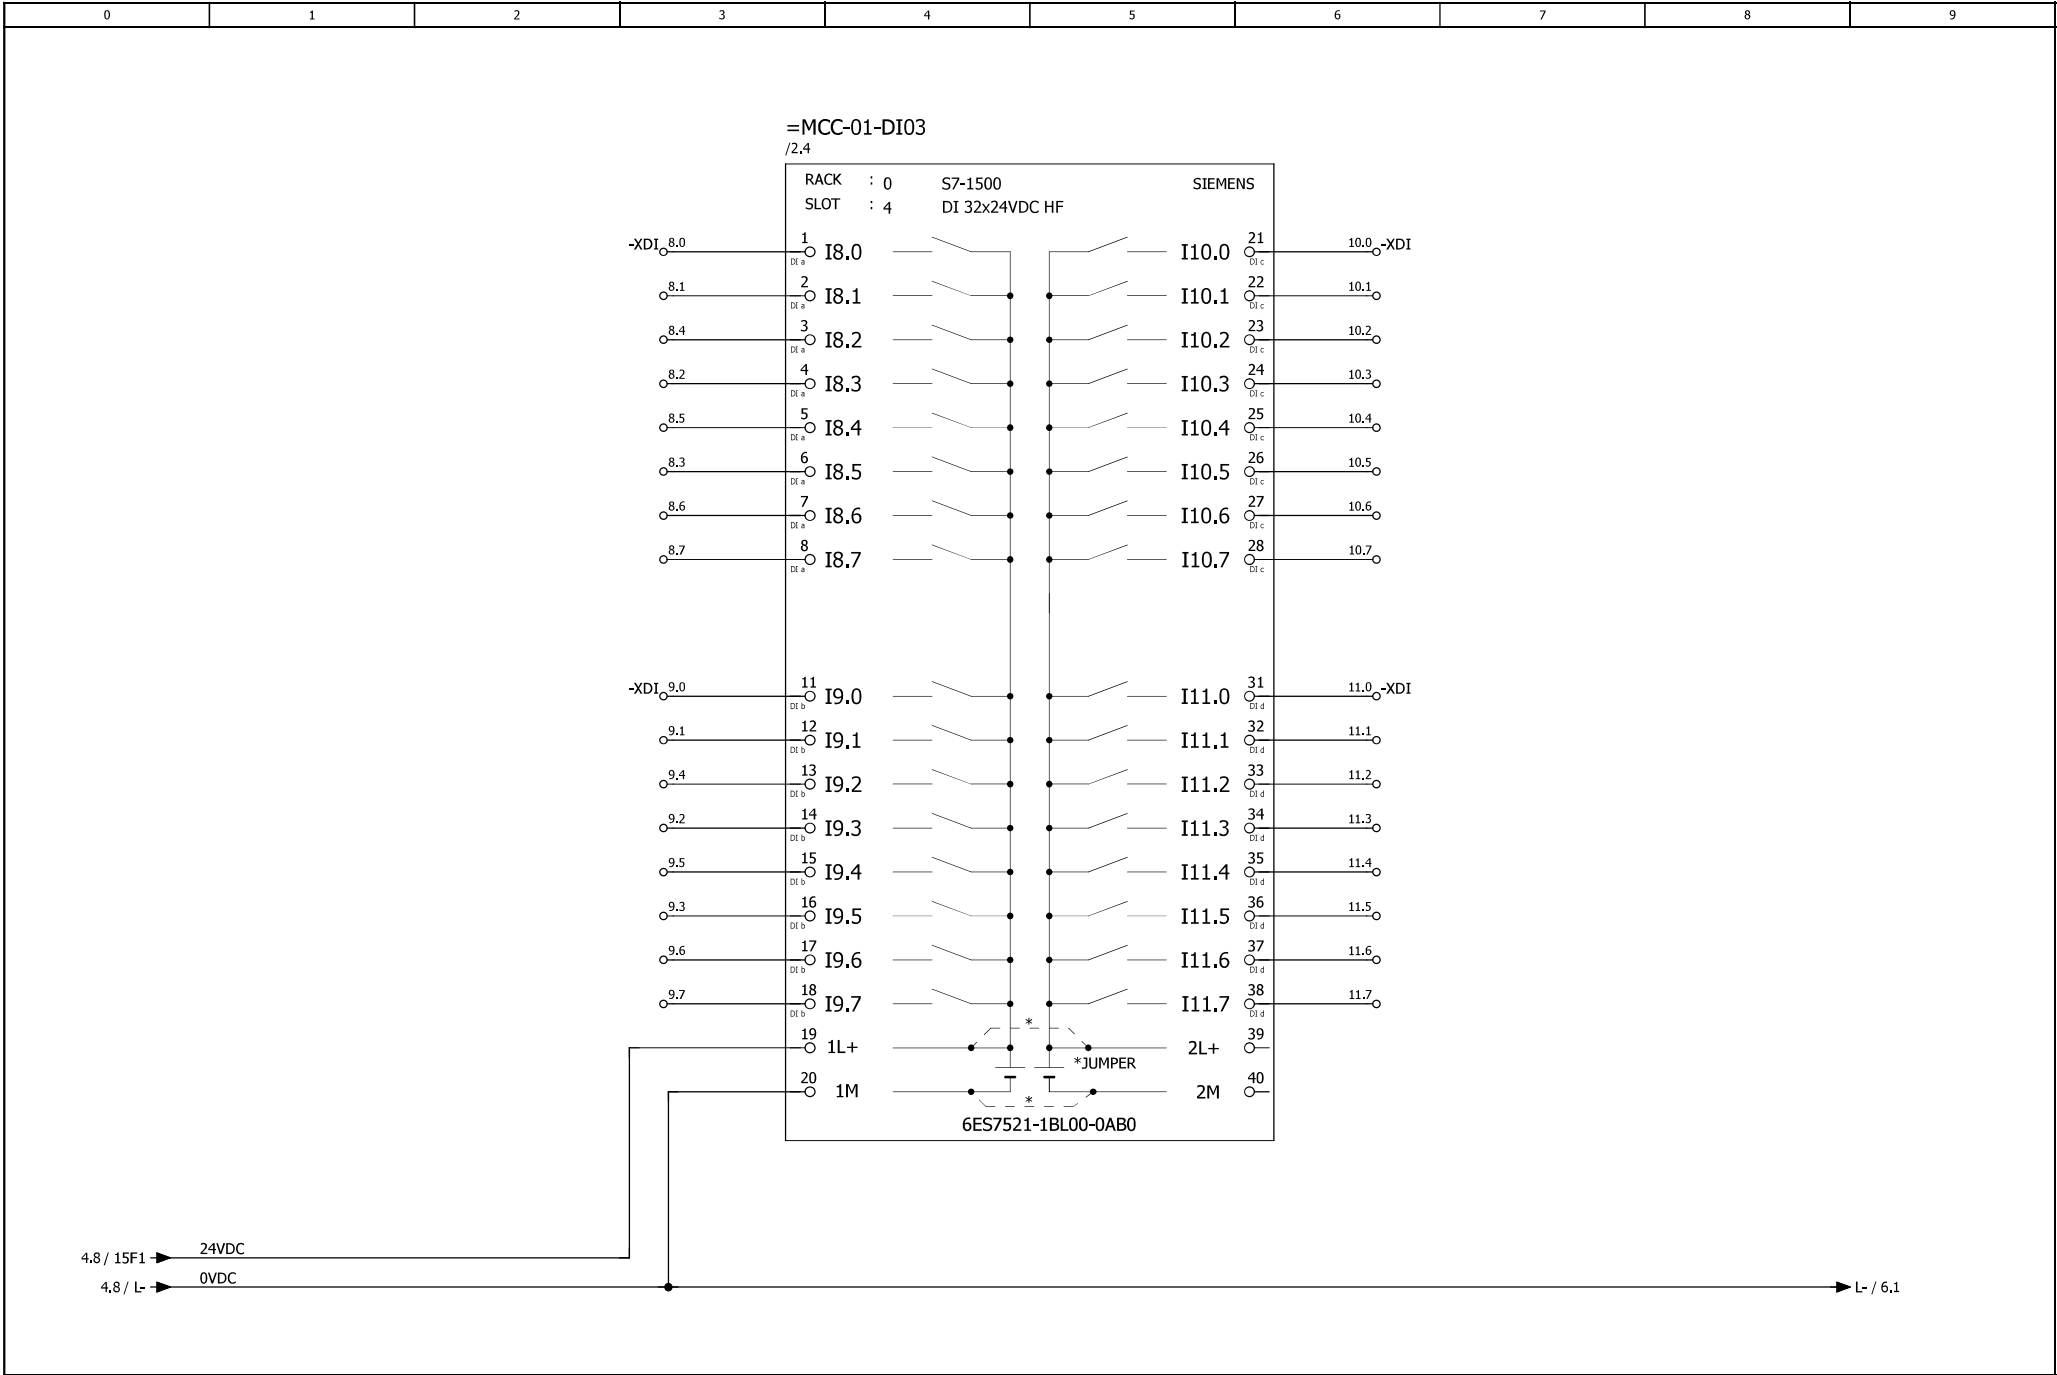

			ΗΜ/ΝΙΑ	19.09.2019	ΑΡ. ΣΧΕΔΙΟΥ	: ΕΡΓΟ ΑΝΑΒΑΘΜΙΣΗΣ ΚΑΙ ΕΠΕΚΤΑΣΗΣ ΤΗΣ	ΨΗΦΙΑΚΗ ΚΑΡΤΑ ΕΙΣΟΔΩΝ ΠΛΑΙΣΙΟ 0, ΘΕΣΗ 4	=	MCC-01
			ΜΕΛΕΤΗ		ΕΡΓΟ	: ΕΓΚΑΤΑΣΤΑΣΗΣ ΕΠΕΞΕΡΓΑΣΙΑΣ ΛΥΜΑΤΩΝ (ΕΕΛ)		+	PLC
	09.04.2019		ΣΧΕΔΙΟ		ΠΕΛΑΤΗΣ	: ΑΓΙΟΥ ΝΙΚΟΛΑΟΥ		ΦΥΛΛΟ:	5
ΑΛΛΑΓΗ	ΗΜ/ΝΙΑ	ΟΝΟΜΑ	ΘΕΩΡ.		ΠΕΡΙΓΡΑΦΗ ΠΙΝΑΚΑ	: ΠΙΝΑΚΑΣ ΕΡΓΩΝ ΕΙΣΟΔΟΥ		ΤΕΛ. ΦΥΛΛΟ:	9

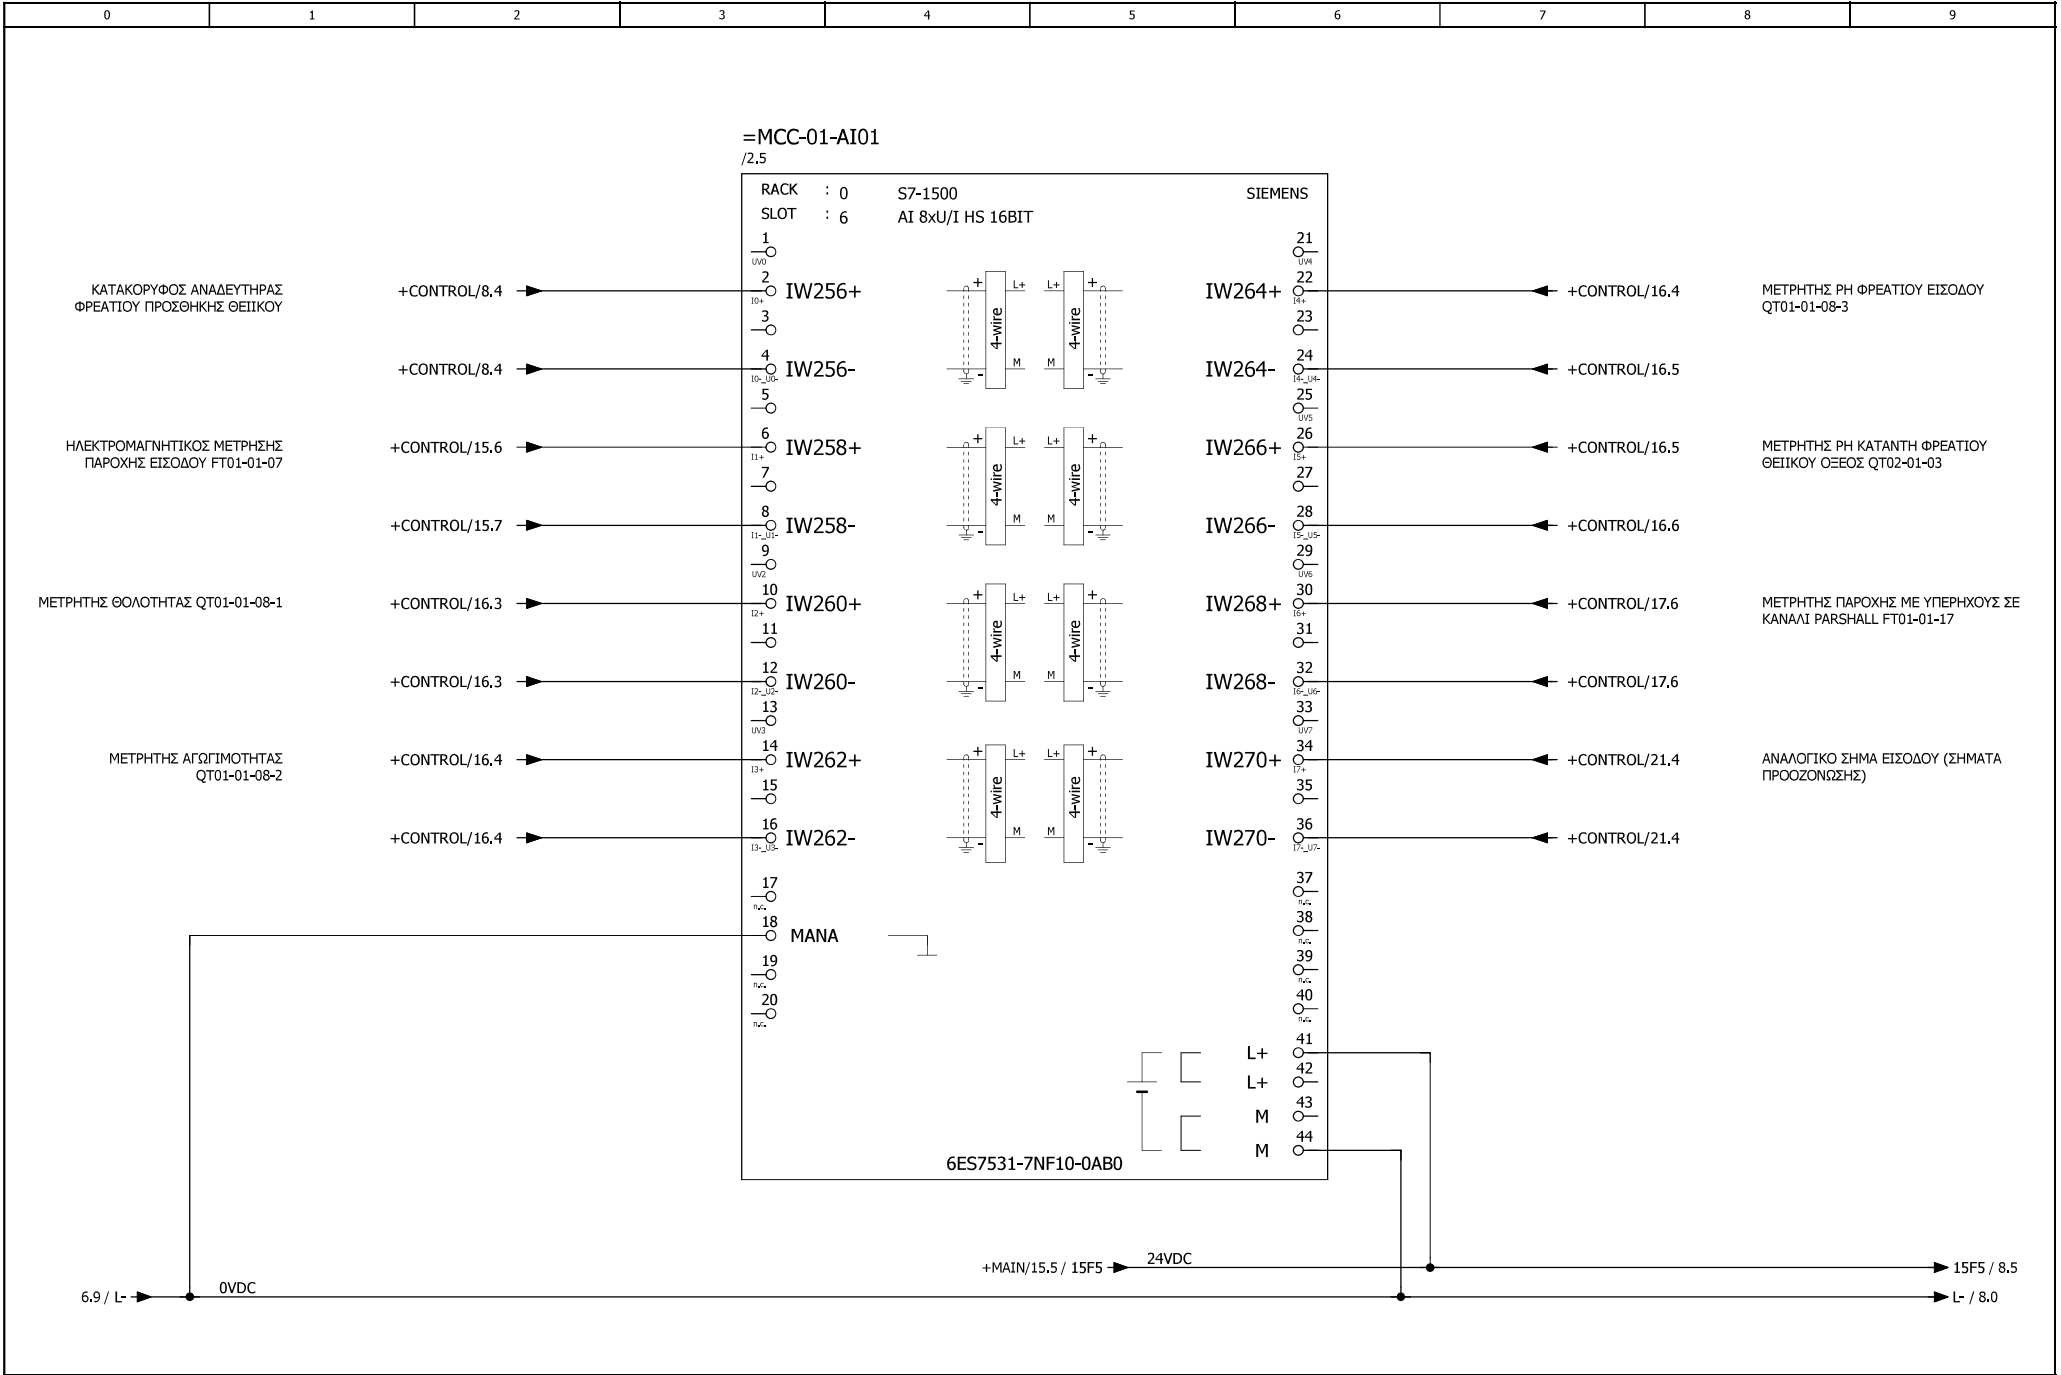

			ΗΜ/ΝΙΑ	19.09.2019	ΑΡ. ΣΧΕΔΙΟΥ	ΕΡΓΟ ΑΝΑΒΑΘΜΙΣΗΣ ΚΑΙ ΕΠΕΚΤΑΣΗΣ ΤΗΣ	ΑΝΑΛΟΓΙΚΗ ΚΑΡΤΑ ΕΙΣΟΔΩΝ, ΘΕΣΗ 6	=	MCC-01
			ΜΕΛΕΤΗ		ΕΡΓΟ	ΕΓΚΑΤΑΣΤΑΣΗΣ ΕΠΕΞΕΡΓΑΣΙΑΣ ΛΥΜΑΤΩΝ (ΕΕΛ)		+	PLC
	09.04.2019		ΣΧΕΔΙΟ		ΠΕΛΑΤΗΣ	ΑΓΙΟΥ ΝΙΚΟΛΑΟΥ		ΦΥΛΛΟ:	7
ΑΛΛΑΓΗ	ΗΜ/ΝΙΑ	ΟΝΟΜΑ	ΘΕΩΡ.		ΠΕΡΙΓΡΑΦΗ ΠΙΝΑΚΑ	ΠΙΝΑΚΑΣ ΕΡΓΩΝ ΕΙΣΟΔΟΥ		ΤΕΛ. ΦΥΛΛΟ:	9

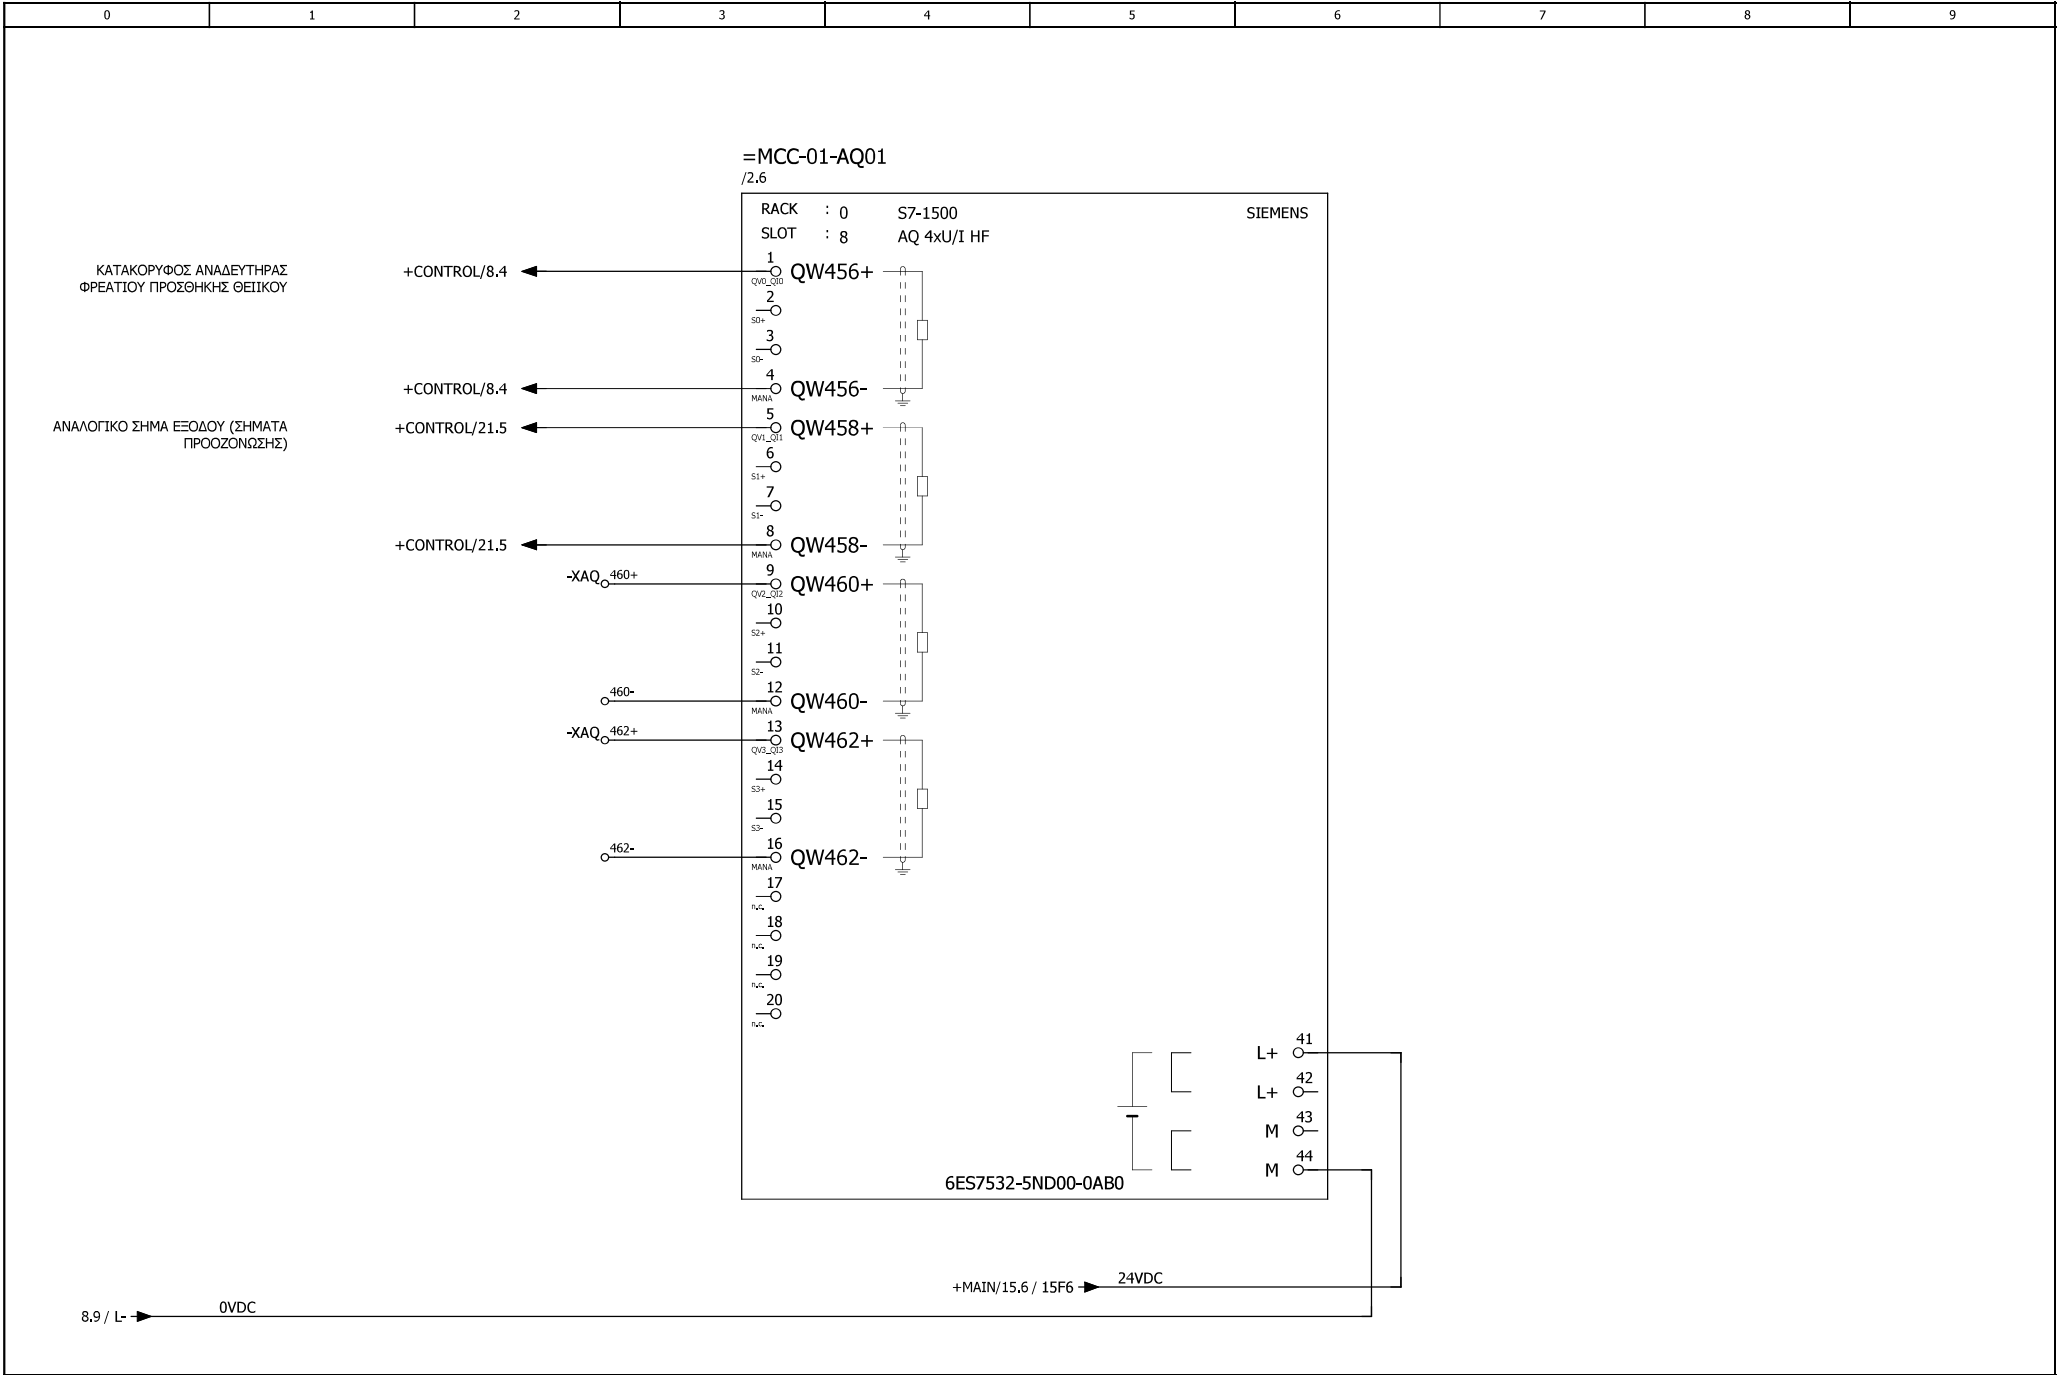


			ΗΜ/ΝΙΑ	19.09.2019	ΑΡ. ΣΧΕΔΙΟΥ	: ΕΡΓΟ ΑΝΑΒΑΘΜΙΣΗΣ ΚΑΙ ΕΠΕΚΤΑΣΗΣ ΤΗΣ	ΑΝΑΛΟΓΙΚΗ ΚΑΡΤΑ ΕΞΟΔΩΝ, ΘΕΣΗ 8	=	MCC-01
			ΜΕΛΕΤΗ		ΕΡΓΟ	: ΕΓΚΑΤΑΣΤΑΣΗΣ ΕΠΕΞΕΡΓΑΣΙΑΣ ΛΥΜΑΤΩΝ (ΕΕΛ)		+	PLC
	09.04.2019		ΣΧΕΔΙΟ		ΠΕΛΑΤΗΣ	: ΑΓΙΟΥ ΝΙΚΟΛΑΟΥ		ΦΥΛΛΟ:	9
ΑΛΛΑΓΗ	ΗΜ/ΝΙΑ	ΟΝΟΜΑ	ΘΕΩΡ.		ΠΕΡΙΓΡΑΦΗ ΠΙΝΑΚΑ	: ΠΙΝΑΚΑΣ ΕΡΓΩΝ ΕΙΣΟΔΟΥ		ΤΕΛ. ΦΥΛΛΟ:	9




ΠΕΛΑΤΗΣ	:	ΕΡΓΟ ΑΝΑΒΑΘΜΙΣΗΣ ΚΑΙ ΕΠΕΚΤΑΣΗΣ ΤΗΣ ΕΓΚΑΤΑΣΤΑΣΗΣ
ΕΡΓΟ	:	ΕΠΕΞΕΡΓΑΣΙΑΣ ΛΥΜΑΤΩΝ (ΕΕΛ) ΑΓΙΟΥ ΝΙΚΟΛΑΟΥ
ΑΡΙΘΜΟΣ ΣΧΕΔΙΟΥ	:	190409
ΠΕΡΙΓΡΑΦΗ ΠΙΝΑΚΑ	:	ΠΙΝΑΚΑΣ ΕΡΓΩΝ ΕΙΣΟΔΟΥ
ΚΩΔΙΚΟΣ ΠΙΝΑΚΑ	:	MCC-01
ΚΑΤΑΣΚΕΥΑΣΤΗΣ	:	
ΥΠΕΥΘΥΝΟΣ ΕΡΓΟΥ	:	
ΣΧΕΔΙΑΣΤΗΣ	:	
ΤΥΠΟΣ	:	
ΤΟΠΟΘΕΤΗΣΗ	:	
ΟΝΟΜΑ ΑΡΧΕΙΟΥ (EPLAN Electric P8 2.4)	:	
ΗΜ/ΝΙΑ ΔΗΜΙΟΥΡΓΙΑΣ	:	09.04.2019
ΕΠΕΞΕΡΓΑΣΘΗΚΕ	:	19.09.2019
ΑΡΙΘΜΟΣ ΣΕΛΙΔΩΝ: 1070		



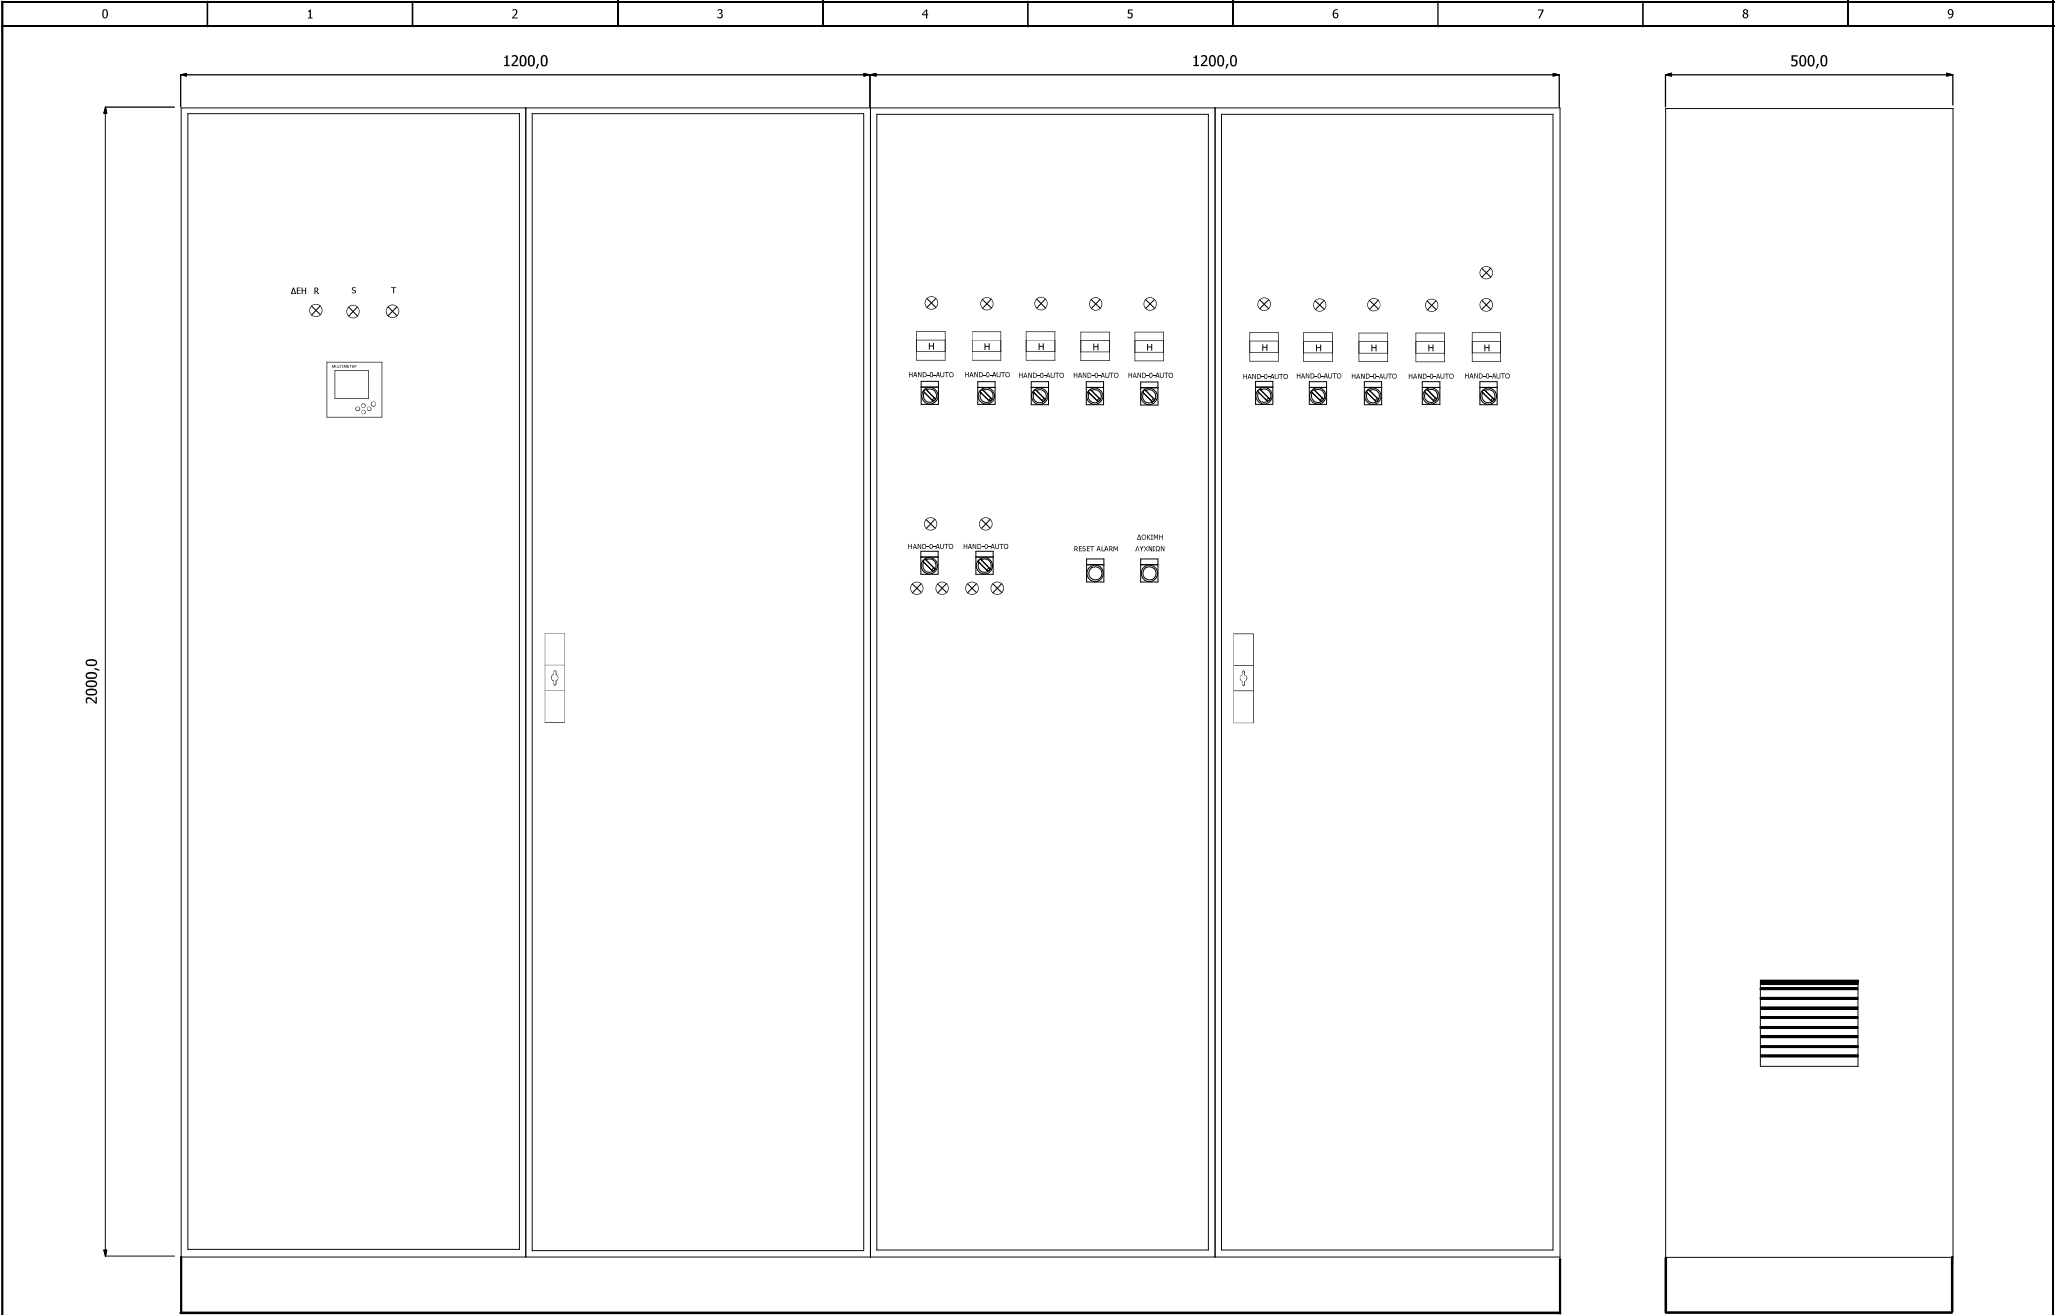

ΠΡΟΣΟΨΗ & ΠΛΑΪΝΗ ΟΨΗ ΗΛΕΚΤΡΙΚΟΥ ΠΙΝΑΚΑ MCC1 (HxWxD) (2000mm x 2400mm x 500mm)

			ΗΜ/ΝΙΑ	19.09.2019	ΑΡ. ΣΧΕΔΙΟΥ : ΕΡΓΟ ΑΝΑΒΑΘΜΙΣΗΣ ΚΑΙ ΕΠΕΚΤΑΣΗΣ ΤΗΣ ΕΡΓΟ : ΕΓΚΑΤΑΣΤΑΣΗΣ ΕΠΕΞΕΡΓΑΣΙΑΣ ΛΥΜΑΤΩΝ (ΕΕΛ) ΠΕΛΑΤΗΣ : ΑΓΙΟΥ ΝΙΚΟΛΑΟΥ ΠΕΡΙΓΡΑΦΗ ΠΙΝΑΚΑ : ΠΙΝΑΚΑΣ ΕΡΓΩΝ ΕΙΣΟΔΟΥ	ΠΡΟΣΟΨΗ & ΠΛΑΪΝΗ ΟΨΗ MCC-01	= MCC-01 + PANEL ΦΥΛΛΟ: 2 ΤΕΛ. ΦΥΛΛΟ: 3
			ΜΕΛΕΤΗ				
	09.04.2019		ΣΧΕΔΙΟ				
ΑΛΛΑΓΗ	ΗΜ/ΝΙΑ	ΟΝΟΜΑ	ΘΕΩΡ.				

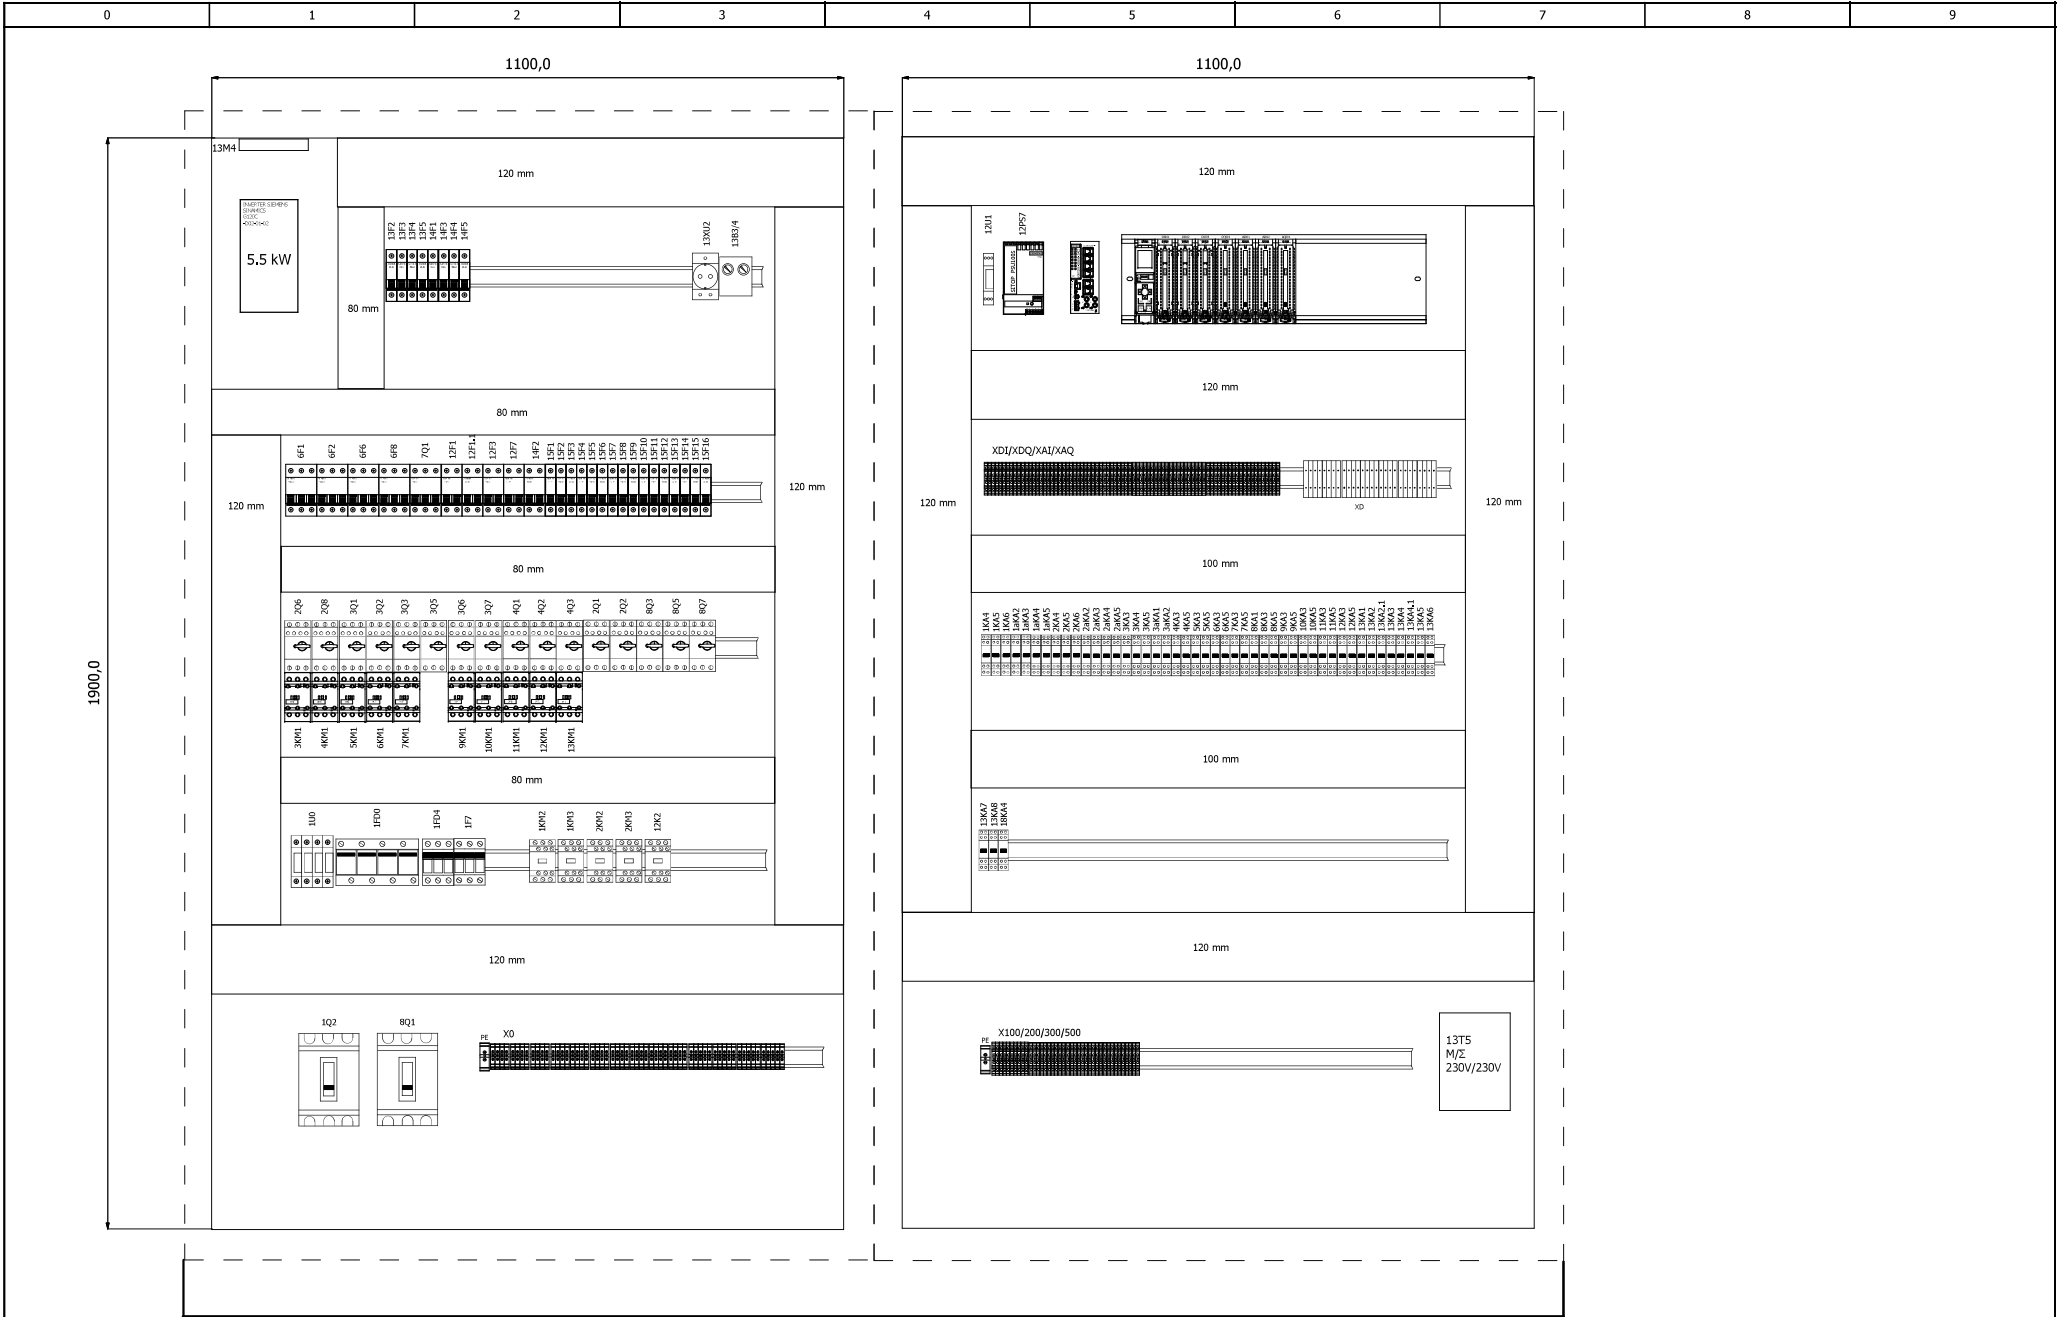

ΕΞΩΤΕΡΙΚΟ ΗΛΕΚΤΡΙΚΟΥ ΠΙΝΑΚΑ MCC1 (HxWxD) (2000mm x 2400mm x 500mm)

			ΗΜ/ΝΙΑ	19.09.2019	ΑΡ. ΣΧΕΔΙΟΥ	: ΕΡΓΟ ΑΝΑΒΑΘΜΙΣΗΣ ΚΑΙ ΕΠΕΚΤΑΣΗΣ ΤΗΣ	ΤΟΠΟΘΕΤΙΚΟ MCC-01	=	MCC-01
			ΜΕΛΕΤΗ		ΕΡΓΟ	: ΕΓΚΑΤΑΣΤΑΣΗΣ ΕΠΕΞΕΡΓΑΣΙΑΣ ΛΥΜΑΤΩΝ (ΕΕΛ)		+	PANEL
09.04.2019			ΣΧΕΔΙΟ		ΠΕΛΑΤΗΣ	: ΑΓΙΟΥ ΝΙΚΟΛΑΟΥ		ΦΥΛΛΟ:	3
ΑΛΛΑΓΗ	ΗΜ/ΝΙΑ	ΟΝΟΜΑ	ΘΕΩΡ.		ΠΕΡΙΓΡΑΦΗ ΠΙΝΑΚΑ	: ΠΙΝΑΚΑΣ ΕΡΓΩΝ ΕΙΣΟΔΟΥ		ΤΕΛ. ΦΥΛΛΟ:	3